


VOX

VOX

**TURQUOISE LUXURY REDEFINED,
MUMBAI - (R0)**

Date: AUG 21 .2026

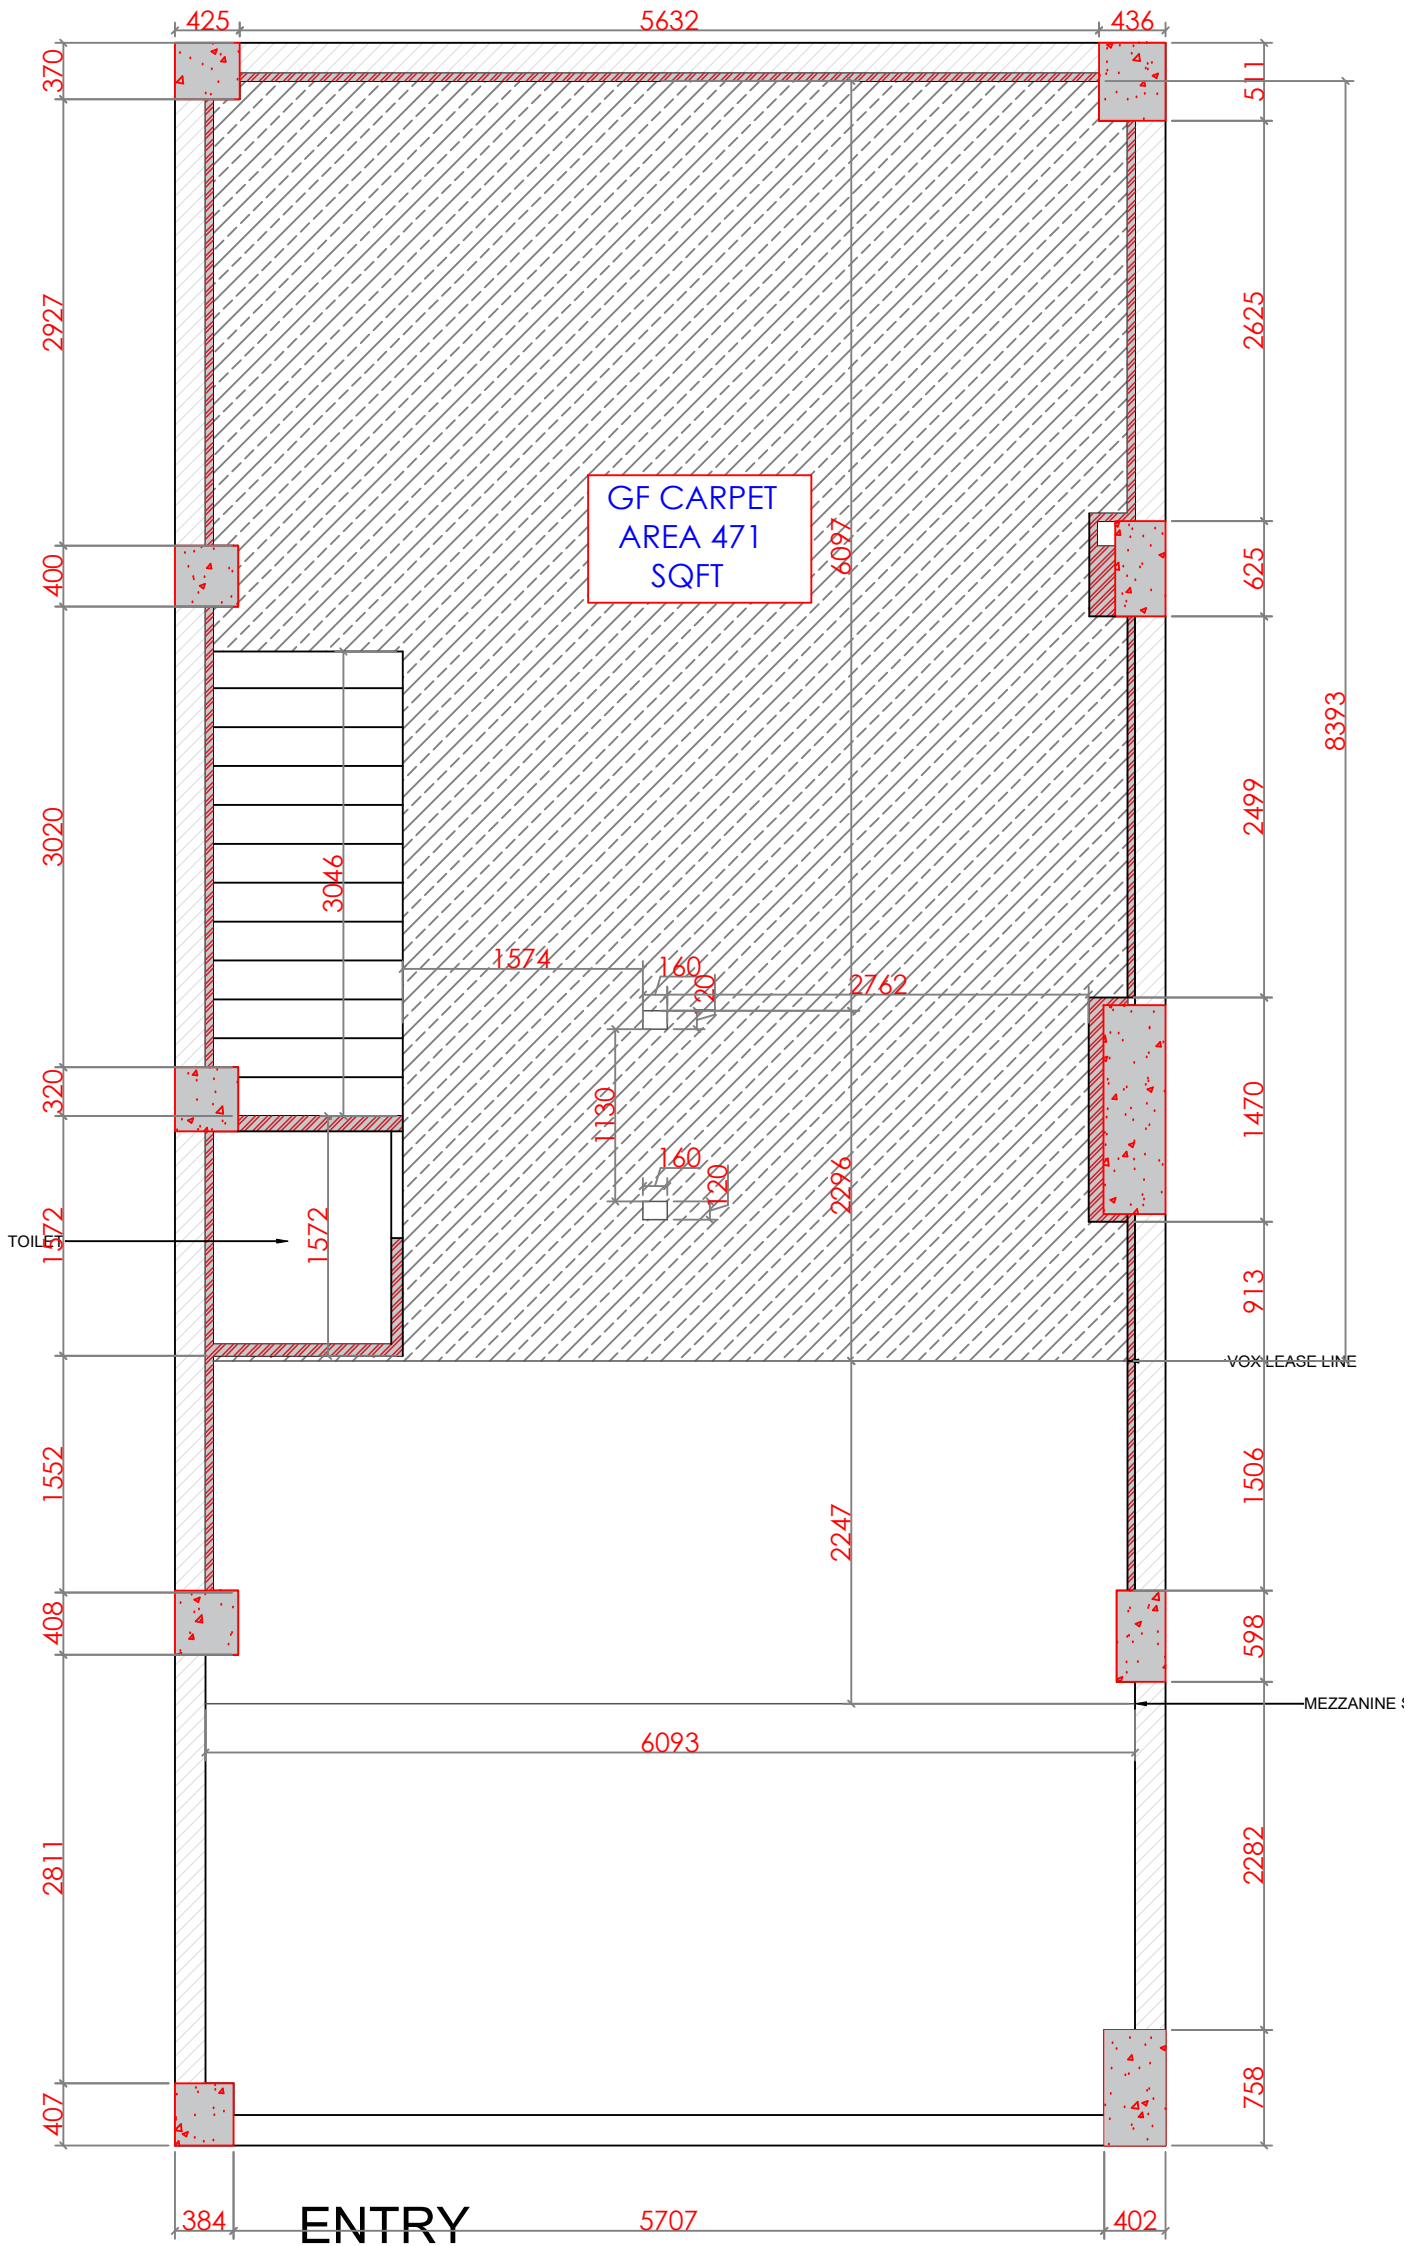

LEGEND :

KEY PLAN :

REVISIONS

R01	01
R02	
R03	



NO. 681, SUKHADA, 2ND FLOOR, 2ND PHASE,
2ND BLOCK, RAILWAY PARALLEL ROAD,
NEAR MALL OF ASIA, BANGALORE,
KARNATAKA, 560097
domoredesign.co.in

GENERAL NOTES:

THIS DRAWING IS COPYRIGHT & PROPERTY OF
DOMORE DESIGN PVT.LTD. AND IS NOT TO BE
REPRODUCED, COPIED OR USED FOR ANY OTHER PURPOSE.
WRITTEN DIMENSIONS TO BE FOLLOWED.
DIMENSIONS TO BE CROSS CHECKED PRIOR TO THE
COMMENCEMENT OF WORK.
ALL DRAWINGS TO BE READ IN CONJUNCTION TO THE
CONSULTANTS AND VENDORS DRAWINGS/DETAILS.
FOR ALL LEGENDS, SYMBOLS, ABBREVIATIONS AND
ANNOTATIONS RELATED QUERIES,
REFER TO REFERENCE SHEET.
ANY DISCREPANCY OR DOUBT IN DRAWING TO BE
BROUGHT
TO THE NOTICE OF DOMORE DESIGN PVT.LTD
SCALE : AS MENTIONED

PROJECT NAME :

**VOX
TURQUOISE LUXURY
DEFINED - MUMBAI**

COMPASS



STORE INFO:

STATE	MAHARASHTRA
CITY	MUMBAI
HIGHSTREET/MALL	AAA
AREA	400 SFT
SLAB BOTTOM:	2500 MM
BEAM BOTTOM:	2346 MM, SPANDREL BEAM - 2173MM


DRAWING NAME:

AREA STATEMENT LAYOUT

DESIGNED BY:	CHECKED BY:	
RISHAD	-	
DATE:	REVISION NO:	DWG NO:
04-08-2026	00	00

CARPET AREA -471 SFT

NOTE :- 1) SLAB / B.O.B HEIGHTS ARE BASED ON EXISTING SITE CONDITIONS.
2) LAYOUT IS ACCORDING TO THE SITE PLAN.
3) MEASUREMENTS TO BE CROSS CHECKED BEFORE SITE EXECUTION.

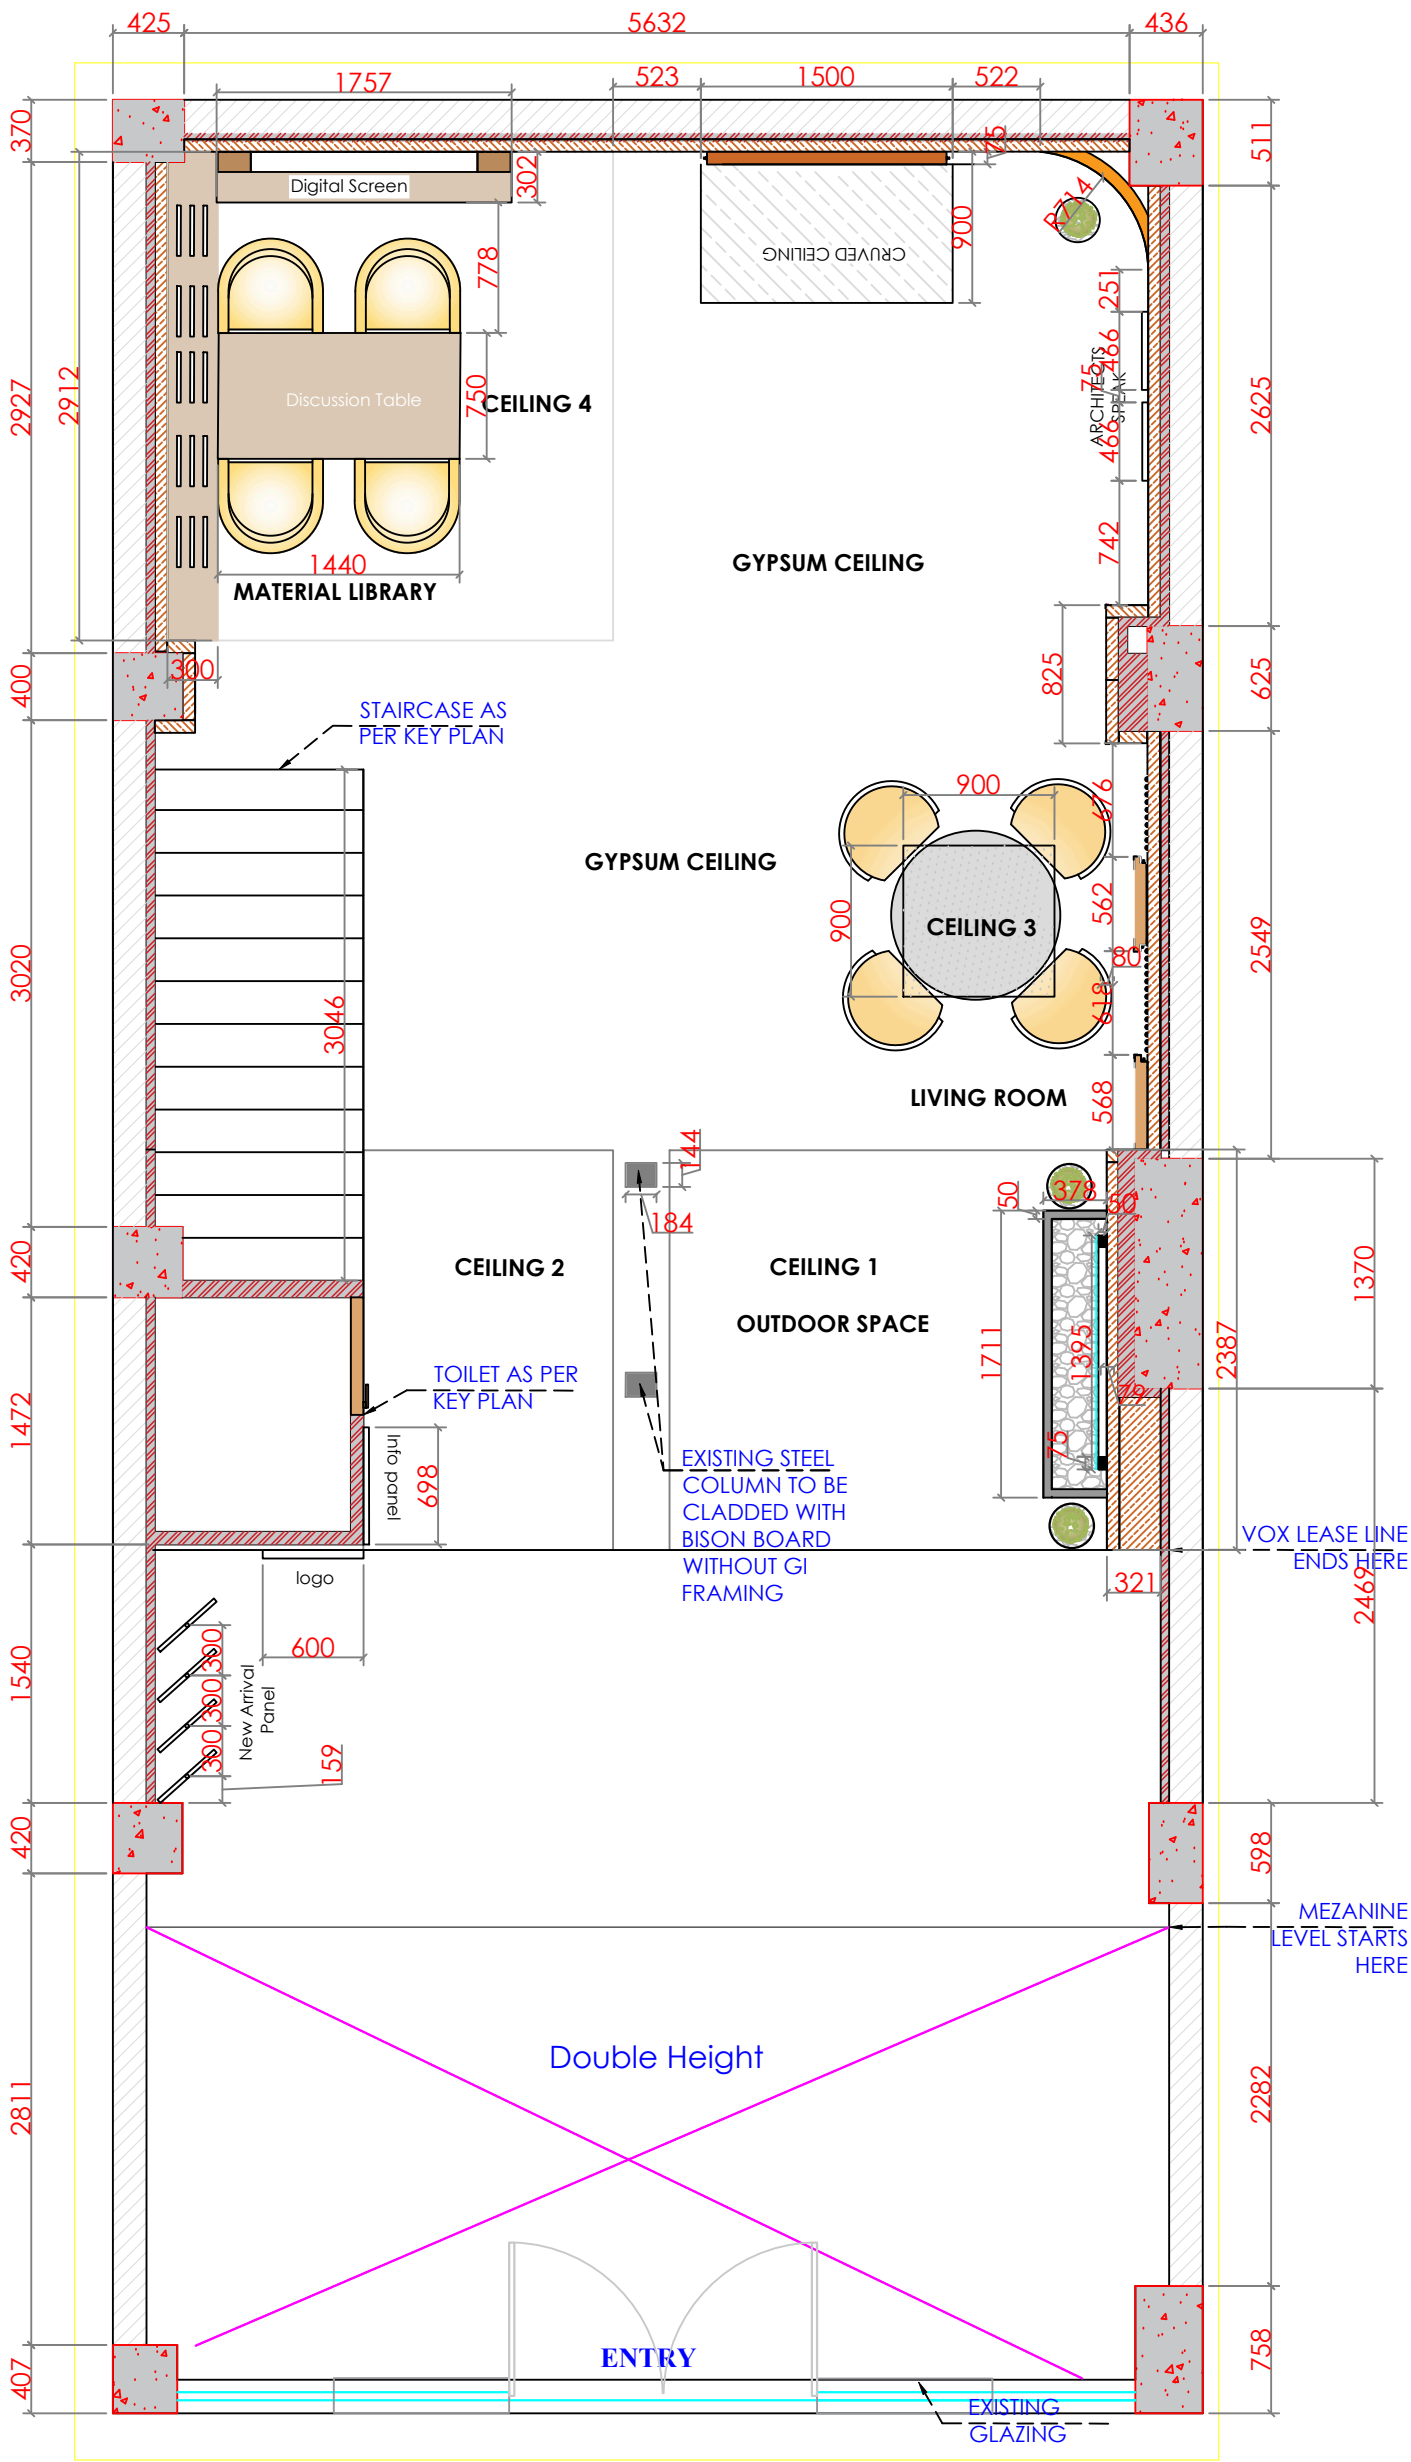

NOTE :- THE LAYOUT IS PROPOSED ON THE GROUND FLOOR.

LEGEND :



CURVED CEILING

KEY PLAN :

REVISIONS

R01	01
R02	
R03	



NO.681, SUKHADA, 2ND FLOOR, 2ND PHASE,
2ND BLOCK, RAILWAY PARALLEL ROAD,
NEAR MALL OF ASIA, BANGALORE,
KARNATAKA, 560097
domoredesign.co.in

GENERAL NOTES:

THIS DRAWING IS COPYRIGHT & PROPERTY OF
DOMORE DESIGN PVT.LTD. AND IS NOT TO BE
REPRODUCED, COPIED OR USED FOR ANY OTHER PURPOSE.
WRITTEN DIMENSIONS TO BE FOLLOWED.
DIMENSIONS TO BE CROSS CHECKED PRIOR TO THE
COMMENCEMENT OF WORK.
ALL DRAWINGS TO BE READ IN CONJUNCTION TO THE
CONSULTANTS AND VENDORS DRAWINGS/DETAILS.
FOR ALL LEGENDS, SYMBOLS, ABBREVIATIONS AND
ANNOTATIONS RELATED QUERIES,
REFER TO REFERENCE SHEET.
ANY DISCREPANCY OR DOUBT IN DRAWING TO BE
BROUGHT
TO THE NOTICE OF DOMORE DESIGN PVT.LTD
SCALE : AS MENTIONED

PROJECT NAME :

VOX
TURQUOISE LUXURY
DEFINED - MUMBAI

COMPASS



STORE INFO:

STATE	MAHARASHTRA
CITY	MUMBAI
HIGHSTREET/MALL	AAA
AREA	471 SFT
SLAB BOTTOM:	2500 MM
BEAM BOTTOM:	2346 MM, SPANDREL BEAM - 2173MM

DRAWING NAME:

FIXTURE LAYOUT

DESIGNED BY:	CHECKED BY:	
RISHAD	-	
DATE:	REVISION NO:	DWG NO:
04-08-2026	00	00

LEGEND :

POWER SOCKET LEGEND		
SL. NO.	SYMBOL	DESCRIPTION
1		DISTRIBUTION BOARD
2		6/16A SOCKET WITH SWITCH RAW POWER
3		6/16A SOCKET WITH SWITCH UPS POWER
4		6A SOCKET CONNECTED TO UPS POWER
5		6A SOCKET CONNECTED TO RAW POWER
6		LIGHTING POINT for chandelier in false ceiling
7		DATA POINT
8		TELEPHONE POINT
9		ROLLING SHUTTER POWER POINT
10		SIGNAGE POINT CONNECTED TO AUTO SHUT-OFF TIMER
11		WIFI OUTLET
12		SENSORMATIC MACHINE
13		POPUP SOCKET @ FLOOR LEVEL
14		RAW POWER CABLE
15		WIFI OUTLET
15		COVE LIGHT POINT AT FLOOR

KEY PLAN :


REVISIONS

R01	01
R02	
R03	

DRAWING NAME:

POWER LAYOUT

DESIGNED BY:	CHECKED BY:	
RISHAD	-	
DATE:	REVISION NO:	DWG NO:
04-08-2026	00	00

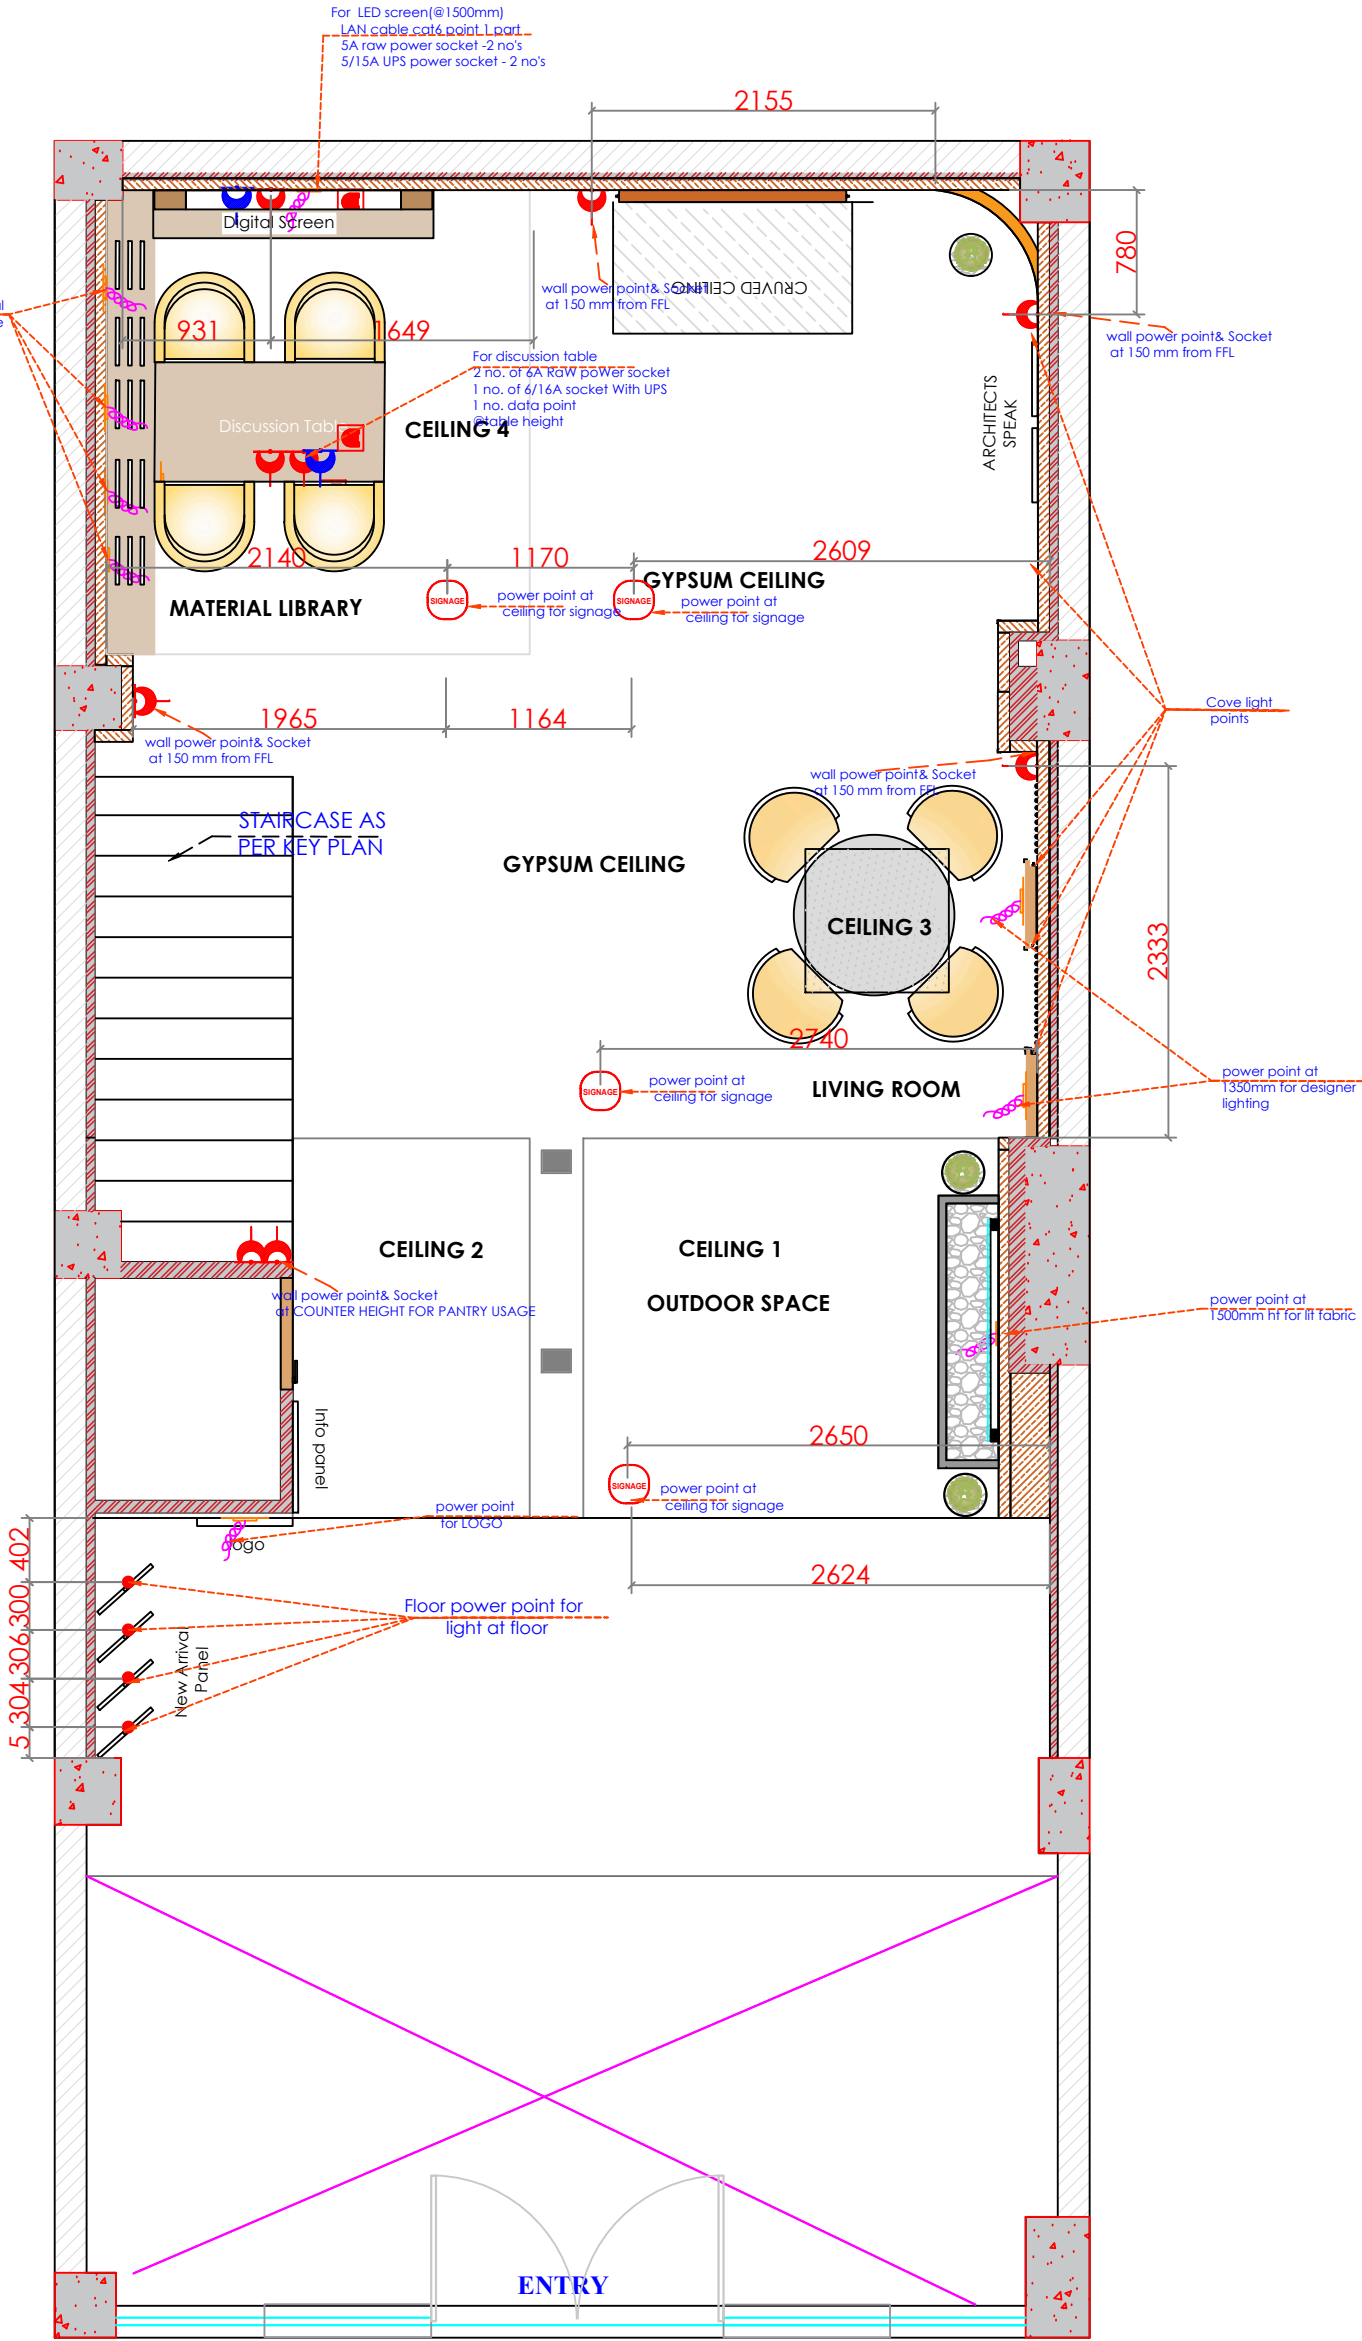

NOTE :- THE LAYOUT IS PROPOSED ON THE GROUND FLOOR.



NO. 681, SUKHADA, 2ND FLOOR, 2ND PHASE,
2ND BLOCK, RAILWAY PARALLEL ROAD,
NEAR MALL OF ASIA, BANGALORE,
KARNATAKA, 560097
domoredesign.co.in

GENERAL NOTES:

THIS DRAWING IS COPYRIGHT & PROPERTY OF
DOMORE DESIGN PVT.LTD. AND IS NOT TO BE
REPRODUCED, COPIED OR USED FOR ANY OTHER PURPOSE.
WRITTEN DIMENSIONS TO BE FOLLOWED.
DIMENSIONS TO BE CROSS CHECKED PRIOR TO THE
COMMENCEMENT OF WORK.
ALL DRAWINGS TO BE READ IN CONJUNCTION TO THE
CONSULTANTS AND VENDORS DRAWINGS/DETAILS.
FOR ALL LEGENDS, SYMBOLS, ABBREVIATIONS AND
ANNOTATIONS RELATED QUERIES,
REFER TO REFERENCE SHEET.
ANY DISCREPANCY OR DOUBT IN DRAWING TO BE
BROUGHT
TO THE NOTICE OF DOMORE DESIGN PVT.LTD.
SCALE : AS MENTIONED

PROJECT NAME :


VOX
TURQUOISE LUXURY
DEFINED - MUMBAI

COMPASS



STORE INFO:

STATE	MAHARASHTRA
CITY	MUMBAI
HIGHSTREET/MALL	AAA
AREA	400 SFT
SLAB BOTTOM:	2500 MM
BEAM BOTTOM:	2346 MM, SPANDREL BEAM - 2173MM

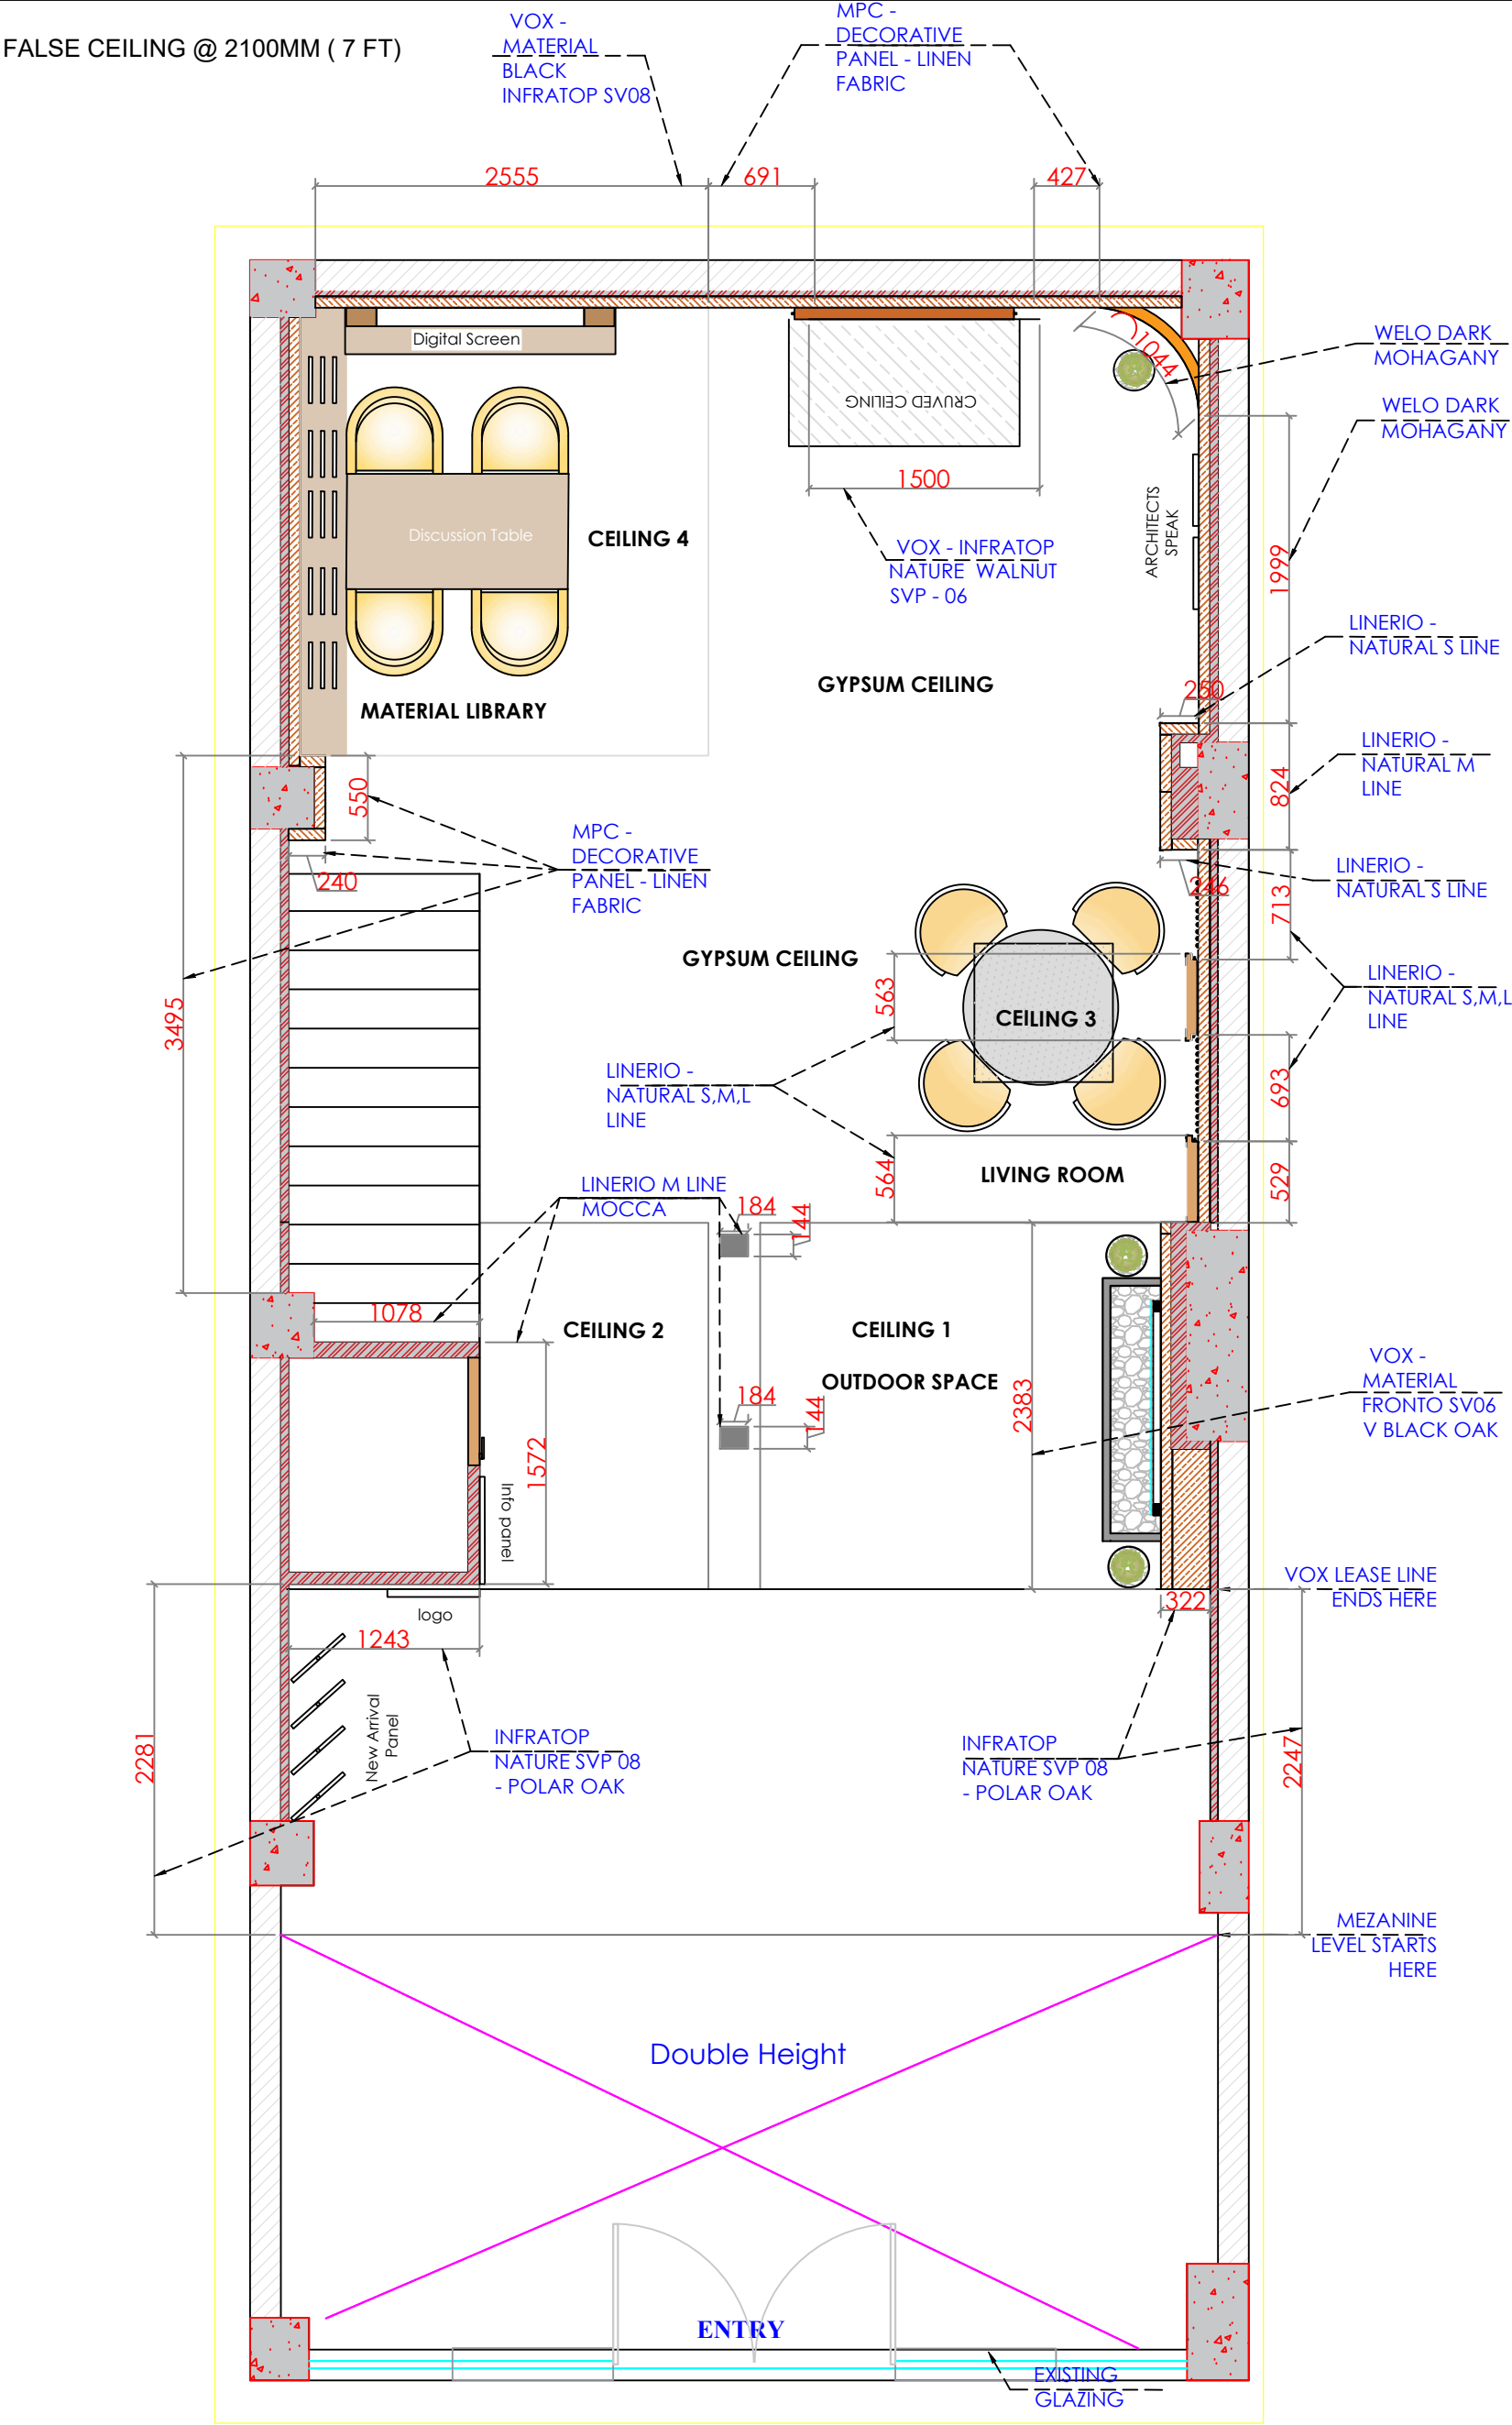

NOTE :- THE LAYOUT IS PROPOSED ON THE GROUND FLOOR.

LEGEND :


KEY PLAN :

REVISIONS			
R01	01		
R02			
R03			

DRAWING NAME:			
WALL DECOR LAYOUT			
DESIGNED BY:		CHECKED BY:	
RISHAD		-	
DATE:		REVISION NO:	DWG NO:
04-08-2026		00	00



STORE INFO:	
STATE	MAHARASHTRA
CITY	MUMBAI
HIGHSTREET/MALL	AAA
AREA	471 SFT
SLAB BOTTOM:	2500 MM
BEAM BOTTOM:	2346 MM, SPANDREL BEAM - 2173MM

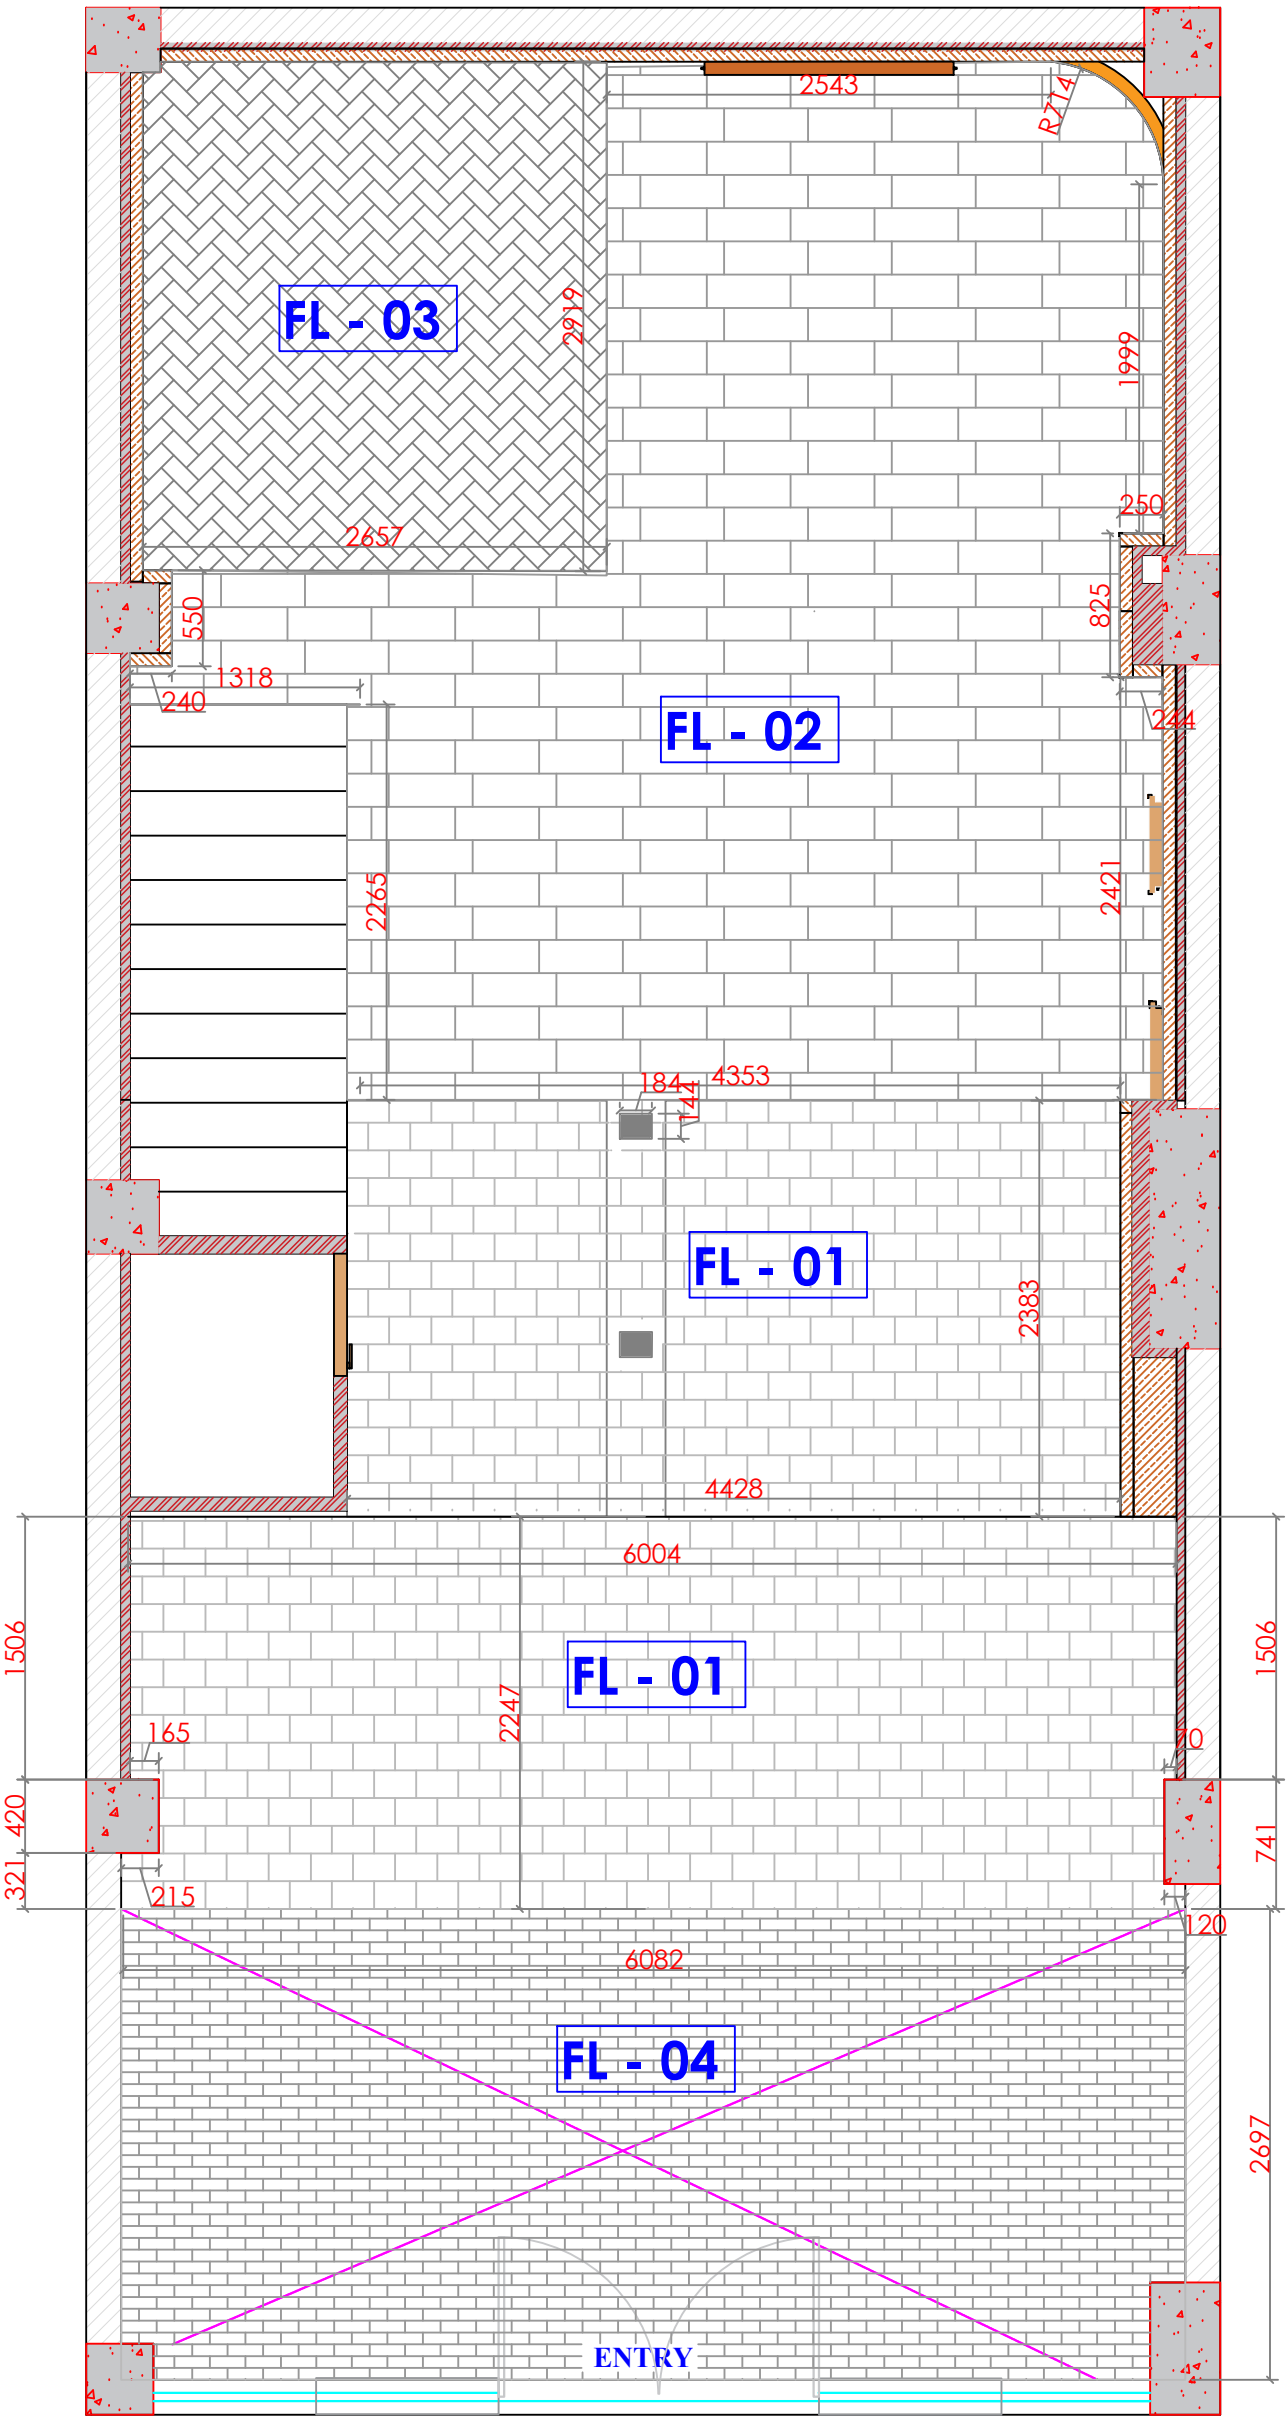

LEGEND :

LEGEND	SYMBOL	DESCRIPTION
	FL - 01	VOX flooring to be done on existing floor (SPC OAK MIST)
	FL - 02	VOX flooring to be done on existing floor (NATURE OAK)
	FL - 03	VOX flooring to be done on existing floor (GOLDEN OAK HERRINGBONE)
	FL - 04	VOX flooring to be done on existing floor (CHERRY OAK)

KEY PLAN :

REVISIONS

R01	
R02	
R03	

DRAWING NAME:

FLOORING LAYOUT

DESIGNED BY:	CHECKED BY:	
RISHAD	-	
DATE:	REVISION NO:	DWG NO:
04-08-2026	00	00



DOMORE DESIGN PVT. LTD.
NO.681, SUKHADA, 2ND FLOOR, 2ND PHASE,
2ND BLOCK, RAILWAY PARALLEL ROAD,
NEAR MALL OF ASIA, BANGALORE,
KARNATAKA, 560097

GENERAL NOTES:

THIS DRAWING IS COPYRIGHT & PROPERTY OF
DOMORE DESIGN PVT.LTD. AND IS NOT TO BE
REPRODUCED, COPIED OR USED FOR ANY OTHER PURPOSE.
WRITTEN DIMENSIONS TO BE FOLLOWED.
DIMENSIONS TO BE CROSS CHECKED PRIOR TO THE
COMMENCEMENT OF WORK.
ALL DRAWINGS TO BE READ IN CONJUNCTION TO THE
CONSULTANTS AND VENDORS DRAWINGS/DETAILS.
FOR ALL LEGENDS, SYMBOLS, ABBREVIATIONS AND
ANNOTATIONS RELATED QUERIES,
REFER TO REFERENCE SHEET.
ANY DISCREPANCY OR DOUBT IN DRAWING TO BE
BROUGHT
TO THE NOTICE OF DOMORE DESIGN PVT.LTD

SCALE : AS MENTIONED

PROJECT NAME :

VOX
TURQUOISE LUXURY
DEFINED - MUMBAI

COMPASS



STORE INFO:

STATE	MAHARASHTRA
CITY	MUMBAI
HIGHSTREET/MALL	AAA
AREA	400 SFT
SLAB BOTTOM:	2500 MM
BEAM BOTTOM:	2346 MM, SPANDREL BEAM - 2173MM

LEGEND :

LEGEND SYMBOL	HT.MM	DESCRIPTION
	FC - 01 2100	FLEXI PLY CEILING @ TO BE FINISHED WITH FRONTO SV06 V BLACK OAK
	FC - 02 2200	GYPSUM FALSE CEILING COVE @ TO BE FINISHED WITH MORNING GLORY_0765 FROM ASIAN PAINTS.
	FC - 03 2100	GYPSUM FALSE CEILING @ TO BE FINISHED WITH MORNING GLORY_0765 FROM ASIAN PAINTS.
	FC - 04 2100	FLEXI PLY CEILING @ TO BE FINISHED WITH INFRATOP SV08 BLACK
	FC - 05 2200	FLEXI PLY CEILING @ TO BE FINISHED WITH FRONTO SV06 GOLDEN OAK
	FC - 06 2100	FLEXI PLY CEILING @ TO BE FINISHED WITH SVOP 08 GOLDEN OAK
	FC - 07 2100	GYPSUM FALSE CEILING COVE @ TO BE FINISHED WITH SVP - 08 POLAR OAK

KEY PLAN :


REVISIONS

R01	
R02	
R03	

DRAWING NAME:

FC LAYOUT

DESIGNED BY:	CHECKED BY:	
RISHAD	-	
DATE:	REVISION NO:	DWG NO:
04-08-2026	00	00

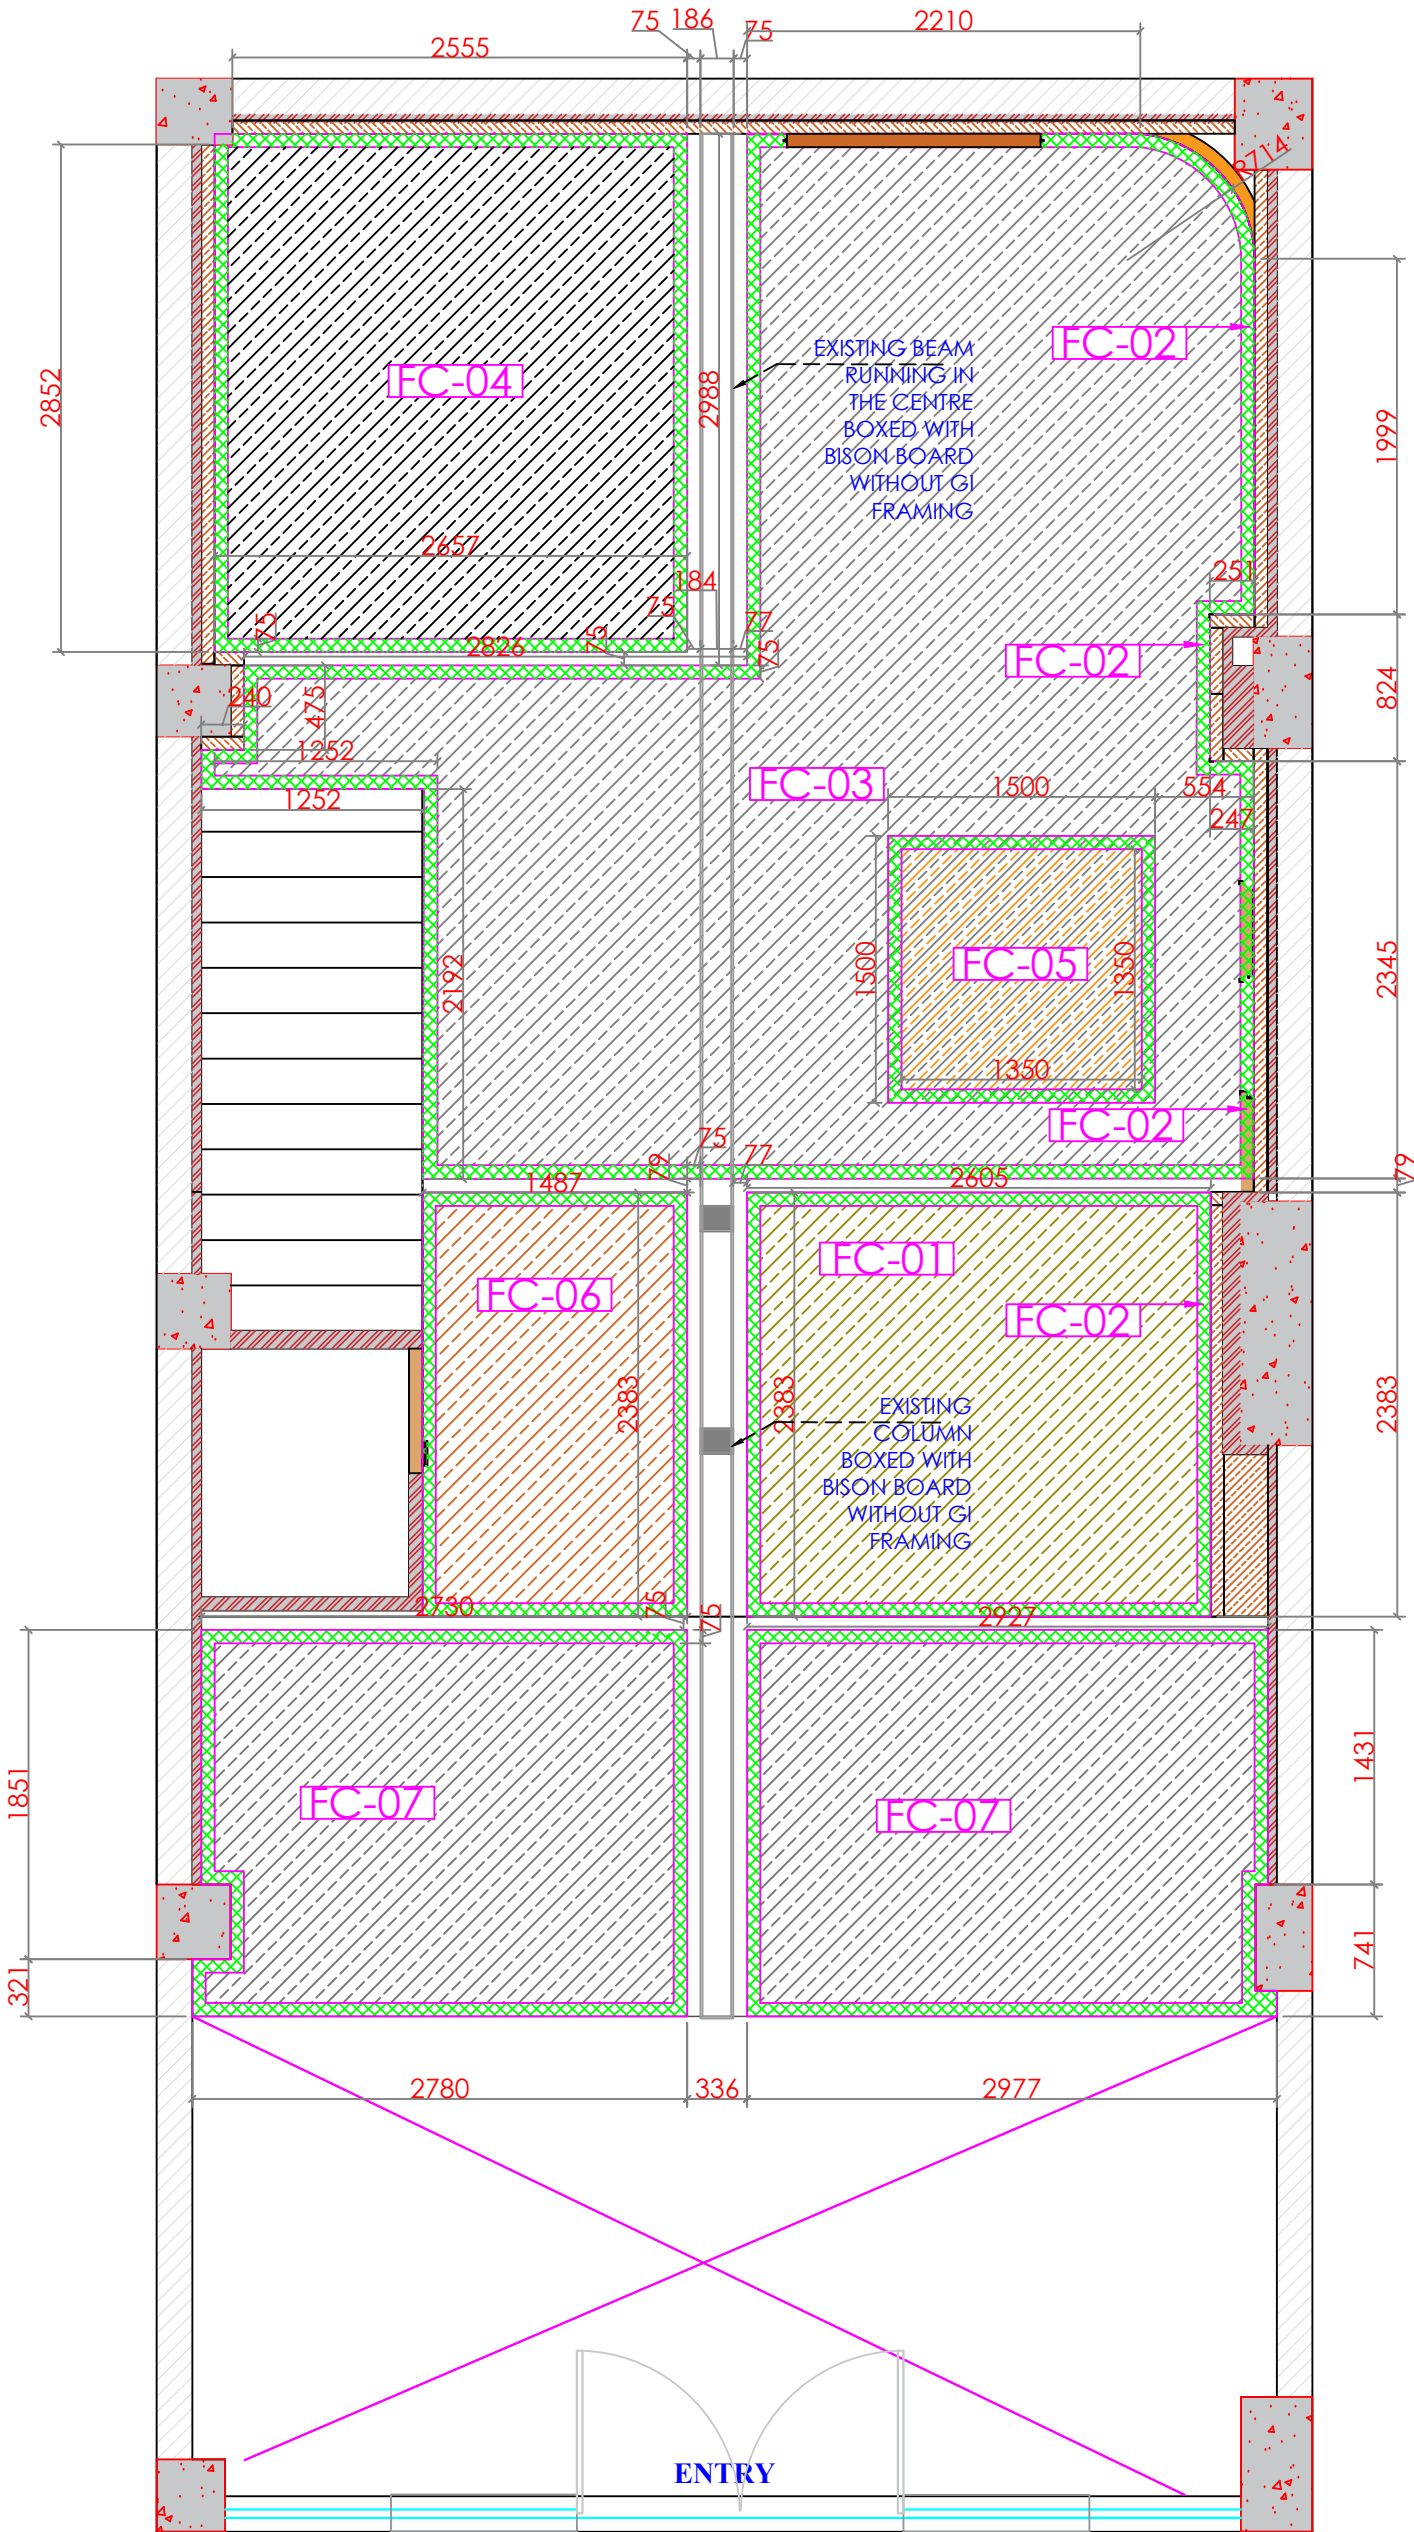

DOMORE DESIGN PVT. LTD.
NO.681, SUKHADA, 2ND FLOOR, 2ND PHASE,
2ND BLOCK, RAILWAY PARALLEL ROAD,
NEAR MALL OF ASIA, BANGALORE,
KARNATAKA, 560097
domoredesign.co.in


GENERAL NOTES:

THIS DRAWING IS COPYRIGHT & PROPERTY OF
DOMORE DESIGN PVT.LTD. AND IS NOT TO BE
REPRODUCED, COPIED OR USED FOR ANY OTHER PURPOSE.
WRITTEN DIMENSIONS TO BE FOLLOWED.
DIMENSIONS TO BE CROSS CHECKED PRIOR TO THE
COMMENCEMENT OF WORK.
ALL DRAWINGS TO BE READ IN CONJUNCTION TO THE
CONSULTANTS AND VENDORS DRAWINGS/DETAILS.
FOR ALL LEGENDS, SYMBOLS, ABBREVIATIONS AND
ANNOTATIONS RELATED QUERIES,
REFER TO REFERENCE SHEET.
ANY DISCREPANCY OR DOUBT IN DRAWING TO BE
BROUGHT
TO THE NOTICE OF DOMORE DESIGN PVT.LTD
SCALE: AS MENTIONED

PROJECT NAME :


VOX
TURQUOISE LUXURY
DEFINED - MUMBAI

COMPASS

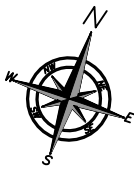

STORE INFO:

STATE	MAHARASHTRA
CITY	MUMBAI
HIGHSTREET/MALL	AAA
AREA	400 SFT
SLAB BOTTOM:	2500 MM
BEAM BOTTOM:	2346 MM, SPANDREL BEAM - 2173MM

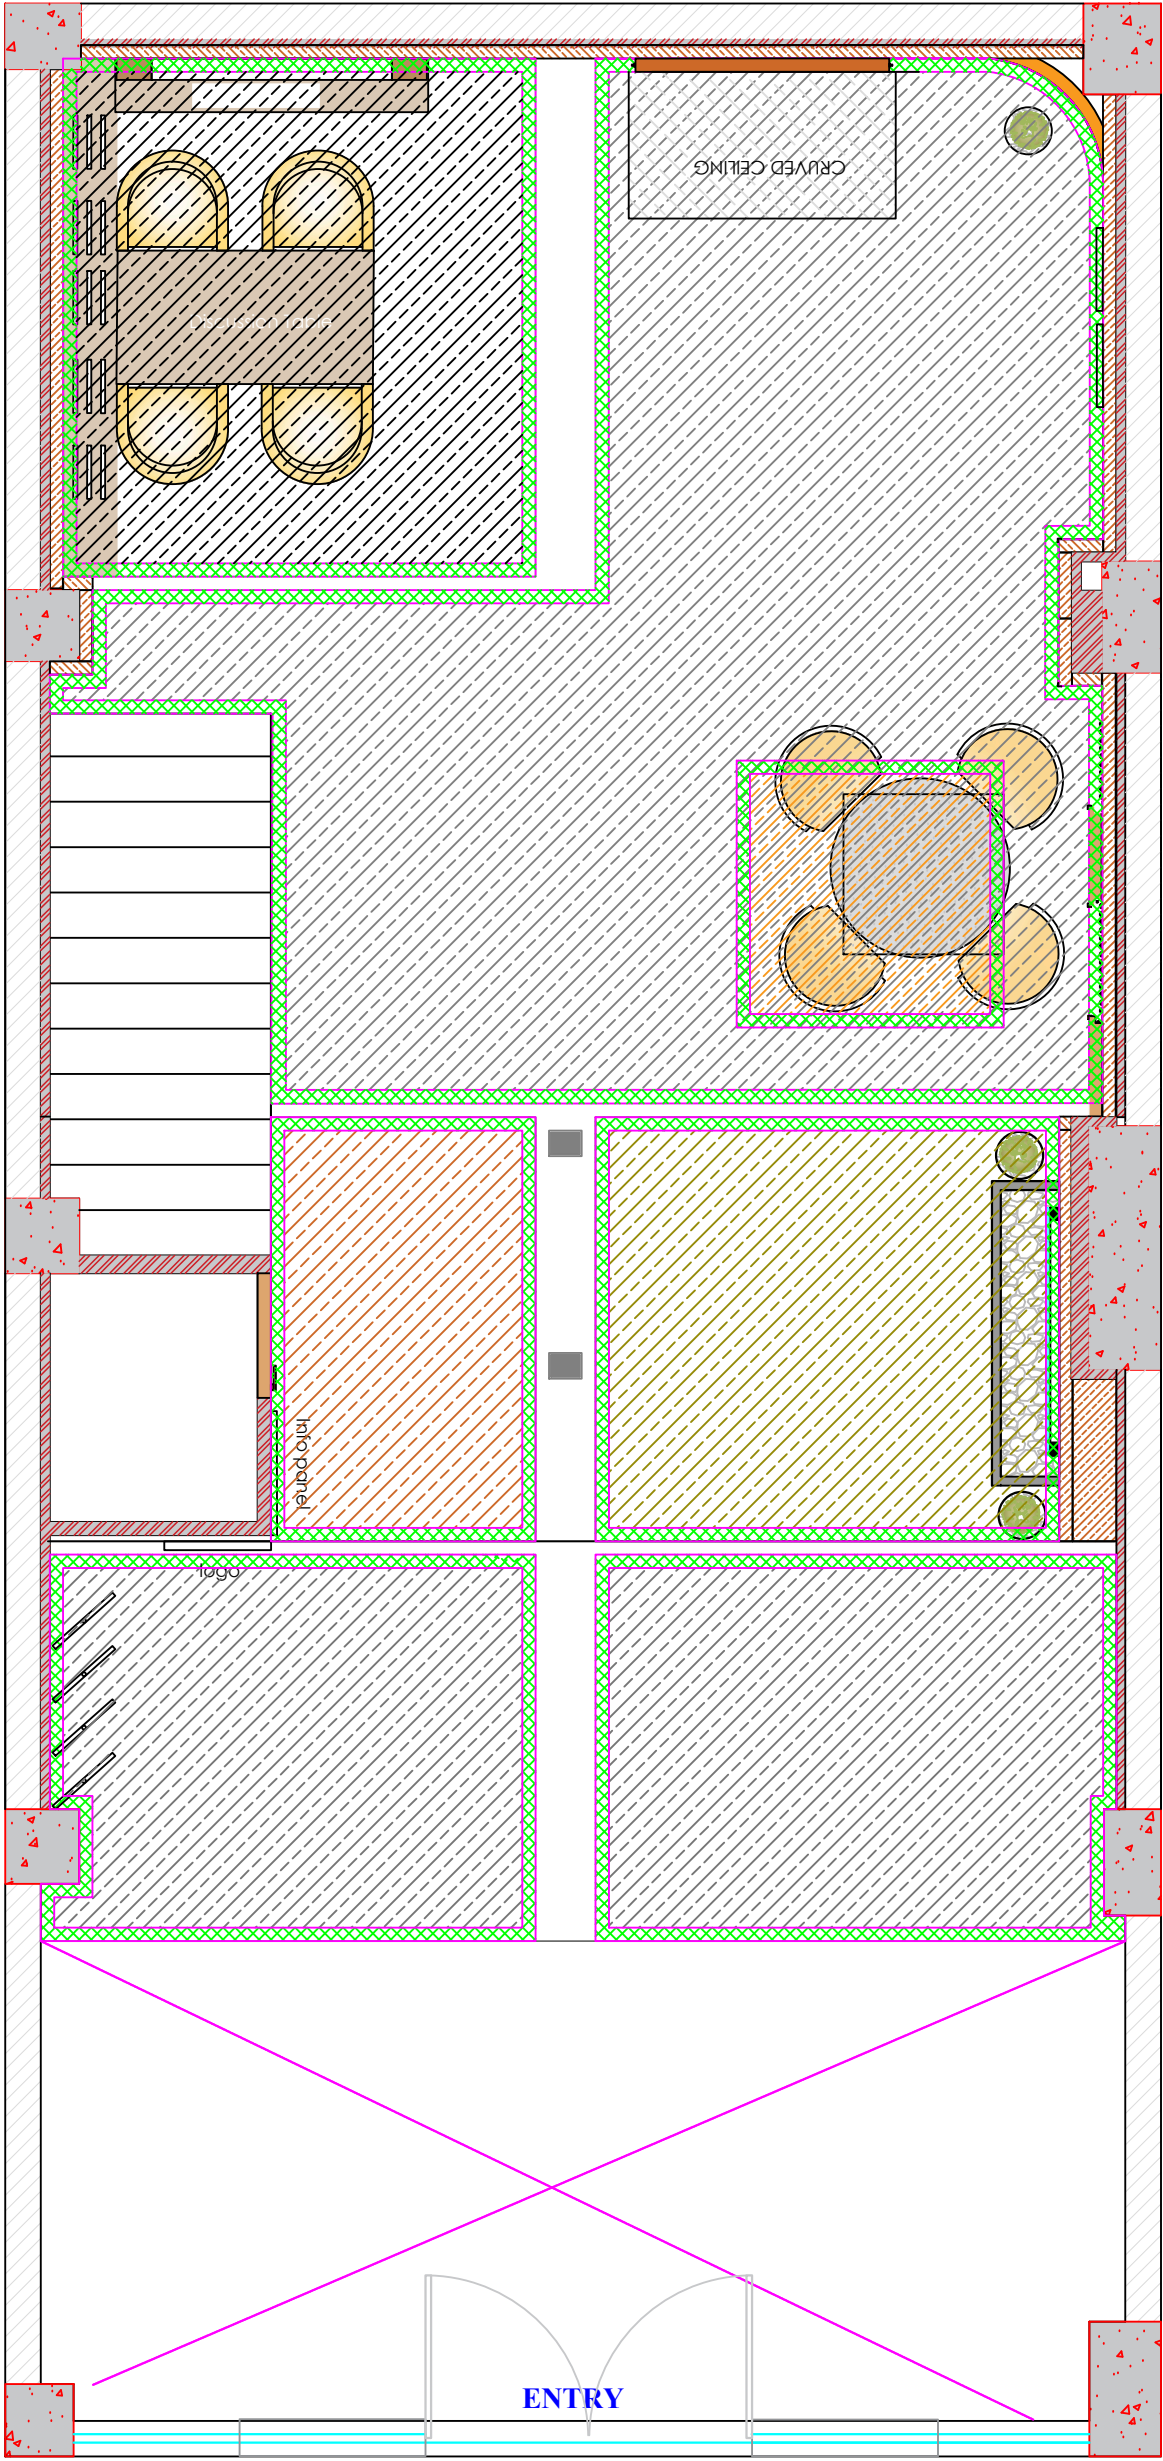

LEGEND :

LEGEND	SYMBOL	HT.MM	DESCRIPTION
		FC - 01	2100 FLEXI PLY CEILING @ TO BE FINISHED WITH FRONTO SV06 V BLACK OAK
		FC - 02	2200 GYPSUM FALSE CEILING COVE @ TO BE FINISHED WITH MORNING GLORY_0765 FROM ASIAN PAINTS.
		FC - 03	2100 GYPSUM FALSE CEILING @ TO BE FINISHED WITH MORNING GLORY_0765 FROM ASIAN PAINTS.
		FC - 04	2100 FLEXI PLY CEILING @ TO BE FINISHED WITH INFRATOP SV08 BLACK
		FC - 05	2200 FLEXI PLY CEILING @ TO BE FINISHED WITH FRONTO SV06 GOLDEN OAK
		FC - 06	2100 FLEXI PLY CEILING @ TO BE FINISHED WITH SVOP 08 GOLDEN OAK
		FC - 07	2100 GYPSUM FALSE CEILING COVE @ TO BE FINISHED WITH SVP - 08 POLAR OAK

KEY PLAN :

REVISIONS

R01	
R02	
R03	

DRAWING NAME:

FC W FURNITURE LAYOUT

DESIGNED BY:	CHECKED BY:	
RISHAD	-	
DATE:	REVISION NO:	DWG NO:
04-08-2026	00	00



DOMORE DESIGN PVT. LTD.
NO.681, SUKHADA, 2ND FLOOR, 2ND PHASE,
2ND BLOCK, RAILWAY PARALLEL ROAD,
NEAR MALL OF ASIA, BANGALORE,
KARNATAKA, 560097
domoredesign.co.in


GENERAL NOTES:

THIS DRAWING IS COPYRIGHT & PROPERTY OF
DOMORE DESIGN PVT.LTD. AND IS NOT TO BE
REPRODUCED, COPIED OR USED FOR ANY OTHER PURPOSE.
WRITTEN DIMENSIONS TO BE FOLLOWED.
DIMENSIONS TO BE CROSS CHECKED PRIOR TO THE
COMMENCEMENT OF WORK.
ALL DRAWINGS TO BE READ IN CONJUNCTION TO THE
CONSULTANTS AND VENDORS DRAWINGS/DETAILS.
FOR ALL LEGENDS, SYMBOLS, ABBREVIATIONS AND
ANNOTATIONS RELATED QUERIES,
REFER TO REFERENCE SHEET.
ANY DISCREPANCY OR DOUBT IN DRAWING TO BE
BROUGHT
TO THE NOTICE OF DOMORE DESIGN PVT.LTD
SCALE : AS MENTIONED

PROJECT NAME :


VOX
TURQUOISE LUXURY
DEFINED - MUMBAI

COMPASS

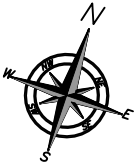


STORE INFO:


STATE	MAHARASHTRA
CITY	MUMBAI
HIGHSTREET/MALL	AAA
AREA	400 SFT
SLAB BOTTOM:	2500 MM
BEAM BOTTOM:	2346 MM, SPANDREL BEAM - 2173MM

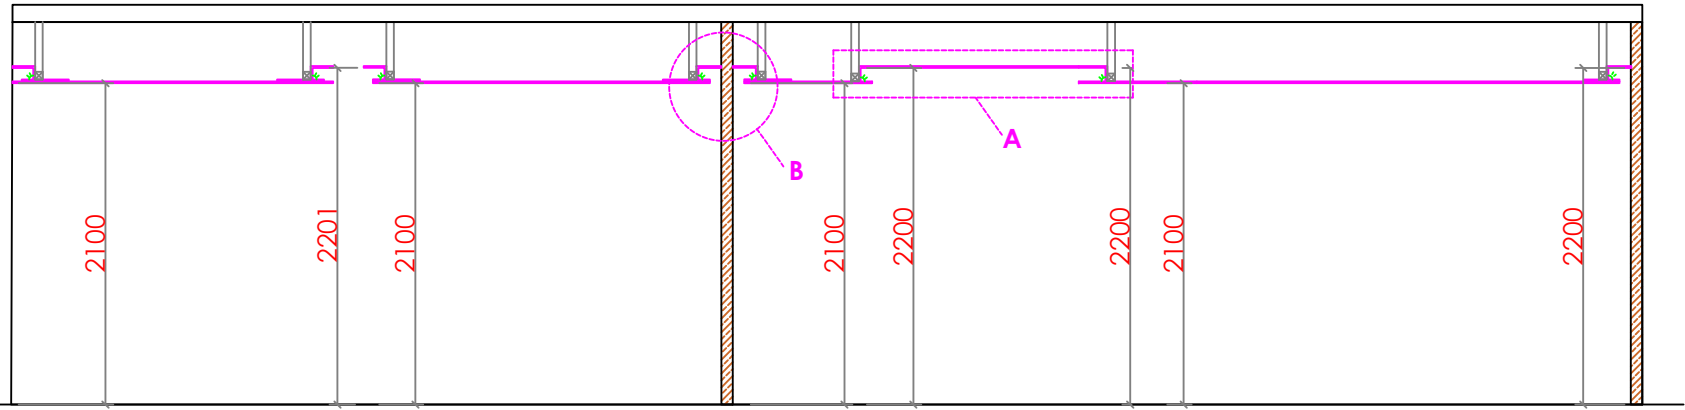


1 SECTION - S1
Scale: NTS

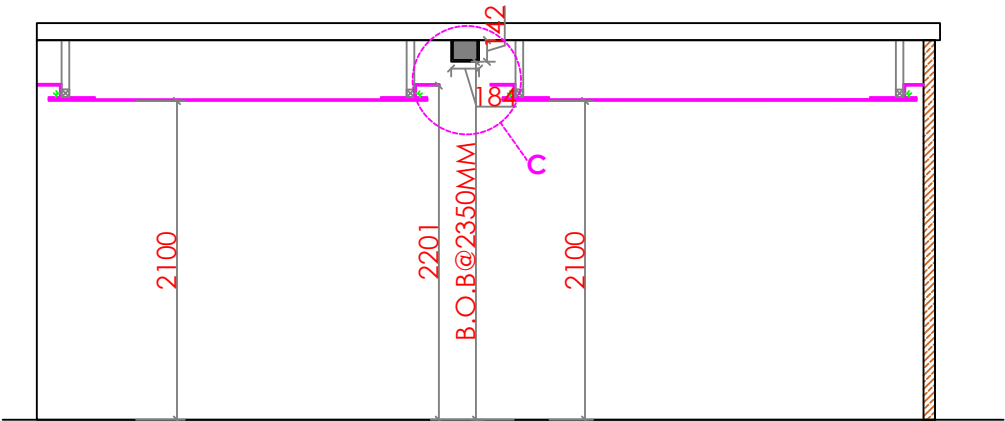


2 SECTION - S2
Scale: NTS

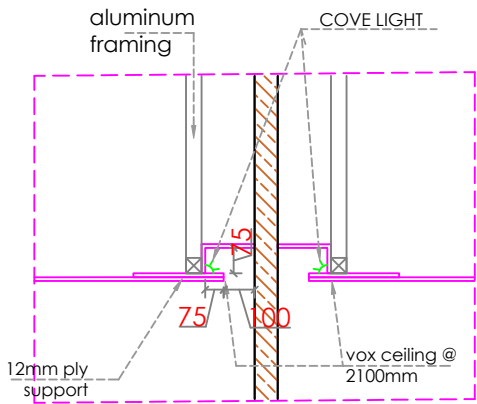

B DETAIL- B

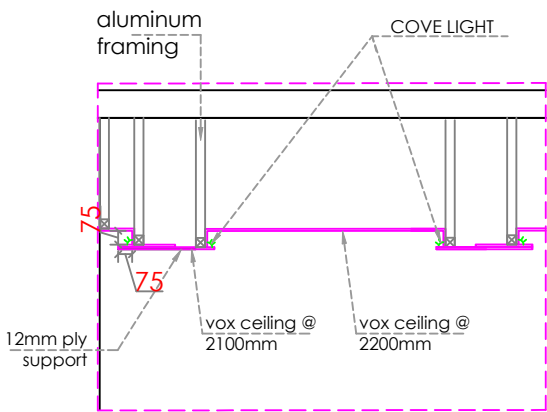


A DETAIL- A

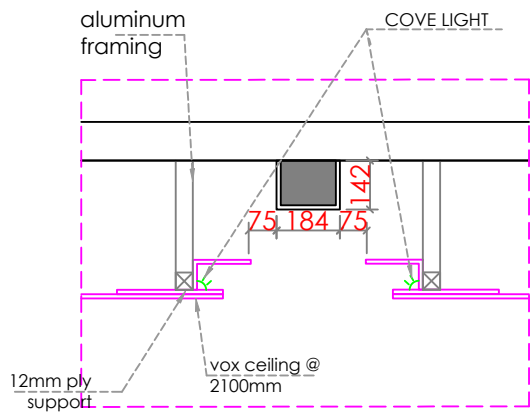

C DETAIL- C

LEGEND :

KEY PLAN :

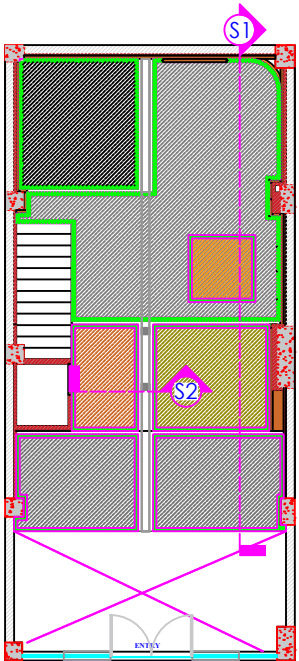

DOMORE DESIGN PVT. LTD.
NO.681, SUKHADA, 2ND FLOOR, 2ND PHASE, 2ND BLOCK,
RAILWAY PARALLEL ROAD,
NEAR MALL OF ASIA, BANGALORE, KARNATAKA, 560097
domoredesign.co.in

GENERAL NOTES

THIS DRAWING IS COPYRIGHT & PROPERTY OF DOMORE
DESIGN PVT.LTD, AND IS NOT TO BE REPRODUCED, COPIED
OR USED FOR ANY OTHER PURPOSE.
WRITTEN DIMENSIONS TO BE FOLLOWED.
DIMENSIONS TO BE CROSS CHECKED PRIOR TO THE
COMMENCEMENT OF WORK.
ALL DRAWINGS TO BE READ IN CONJUNCTION TO THE
CONSULTANTS AND VENDORS DRAWINGS/DETAILS.
FOR ALL LEGENDS, SYMBOLS, ABBREVIATIONS AND
ANNOTATIONS RELATED QUERIES, REFER TO REFERENCE SHEET.
ANY DISCREPANCY OR DOUBT IN DRAWING TO BE BROUGHT
TO THE NOTICE OF DOMORE DESIGN PVT.LTD

SCALE : AS MENTIONED


REVISIONS

R01
R02
R03

PROJECT NAME :

**TURQUOISE
LUXURYREDEFINED,
MUMBAI**

COMPASS:

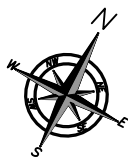



STORE INFO:

STATE	MAHARASHTRA
CITY	MUMBAI
HIGHSTREET/MALL	TURQUOISE MUMBAI HIGHSTREET
AREA	471 SFT
SLAB BOTTOM: 2500 MM	BEAM BOTTOM: 2350 MM


DRAWING NAME:

FC SECTION


DESIGNED BY:	CHECKED BY:	
AA	AAA	
DATE:	REVISION NO:	DWG NO:
24-8-2026	R0	00

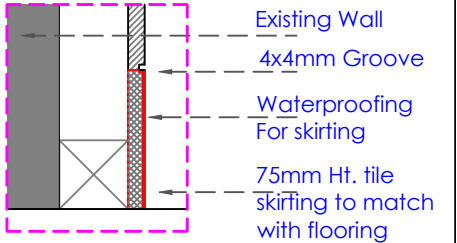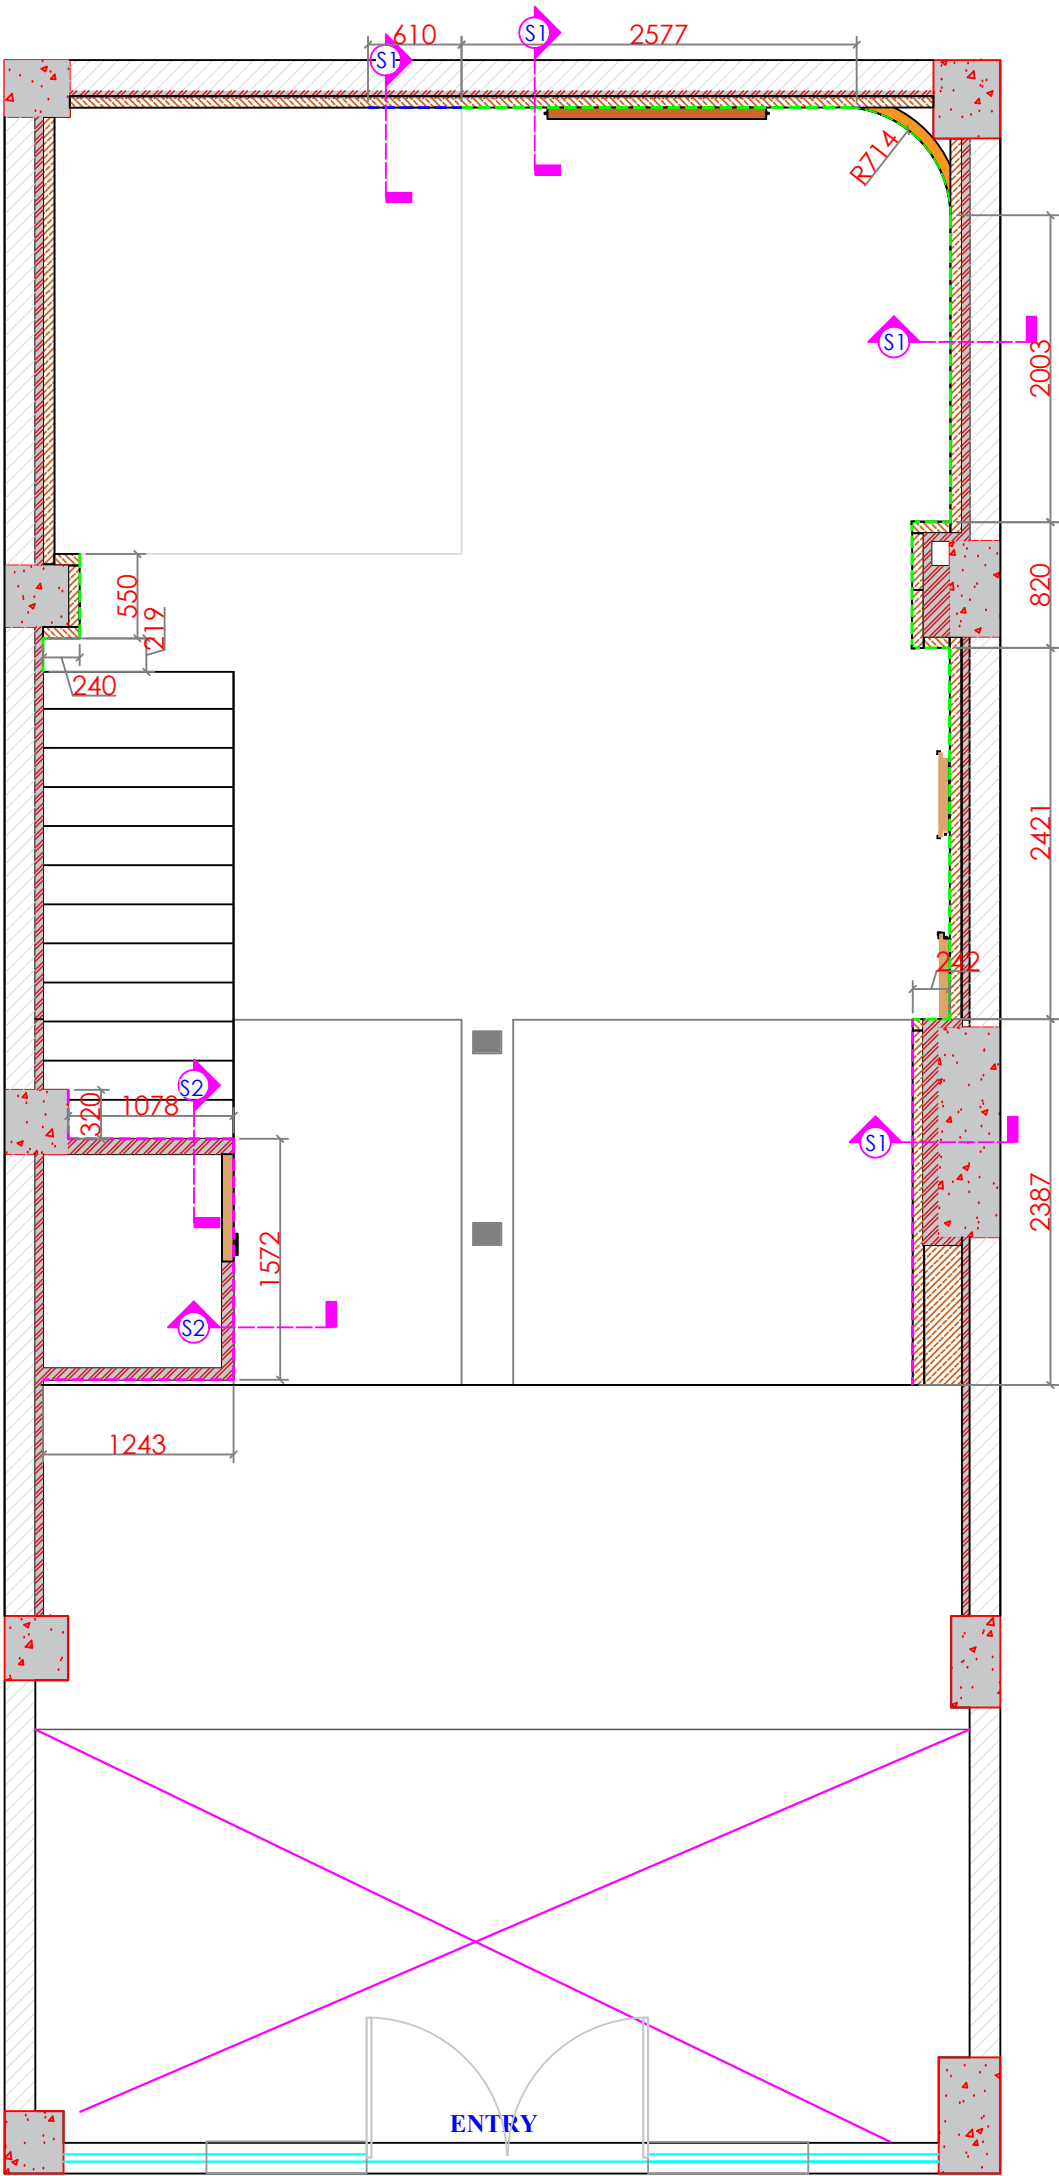

1 SECTION - S1
Scale: 1:4

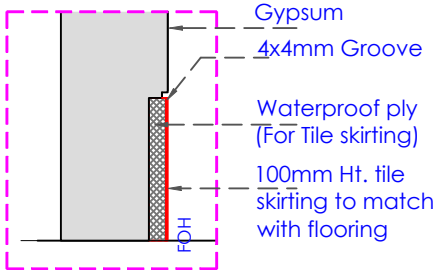

2 SECTION - S2
Scale: 1:4

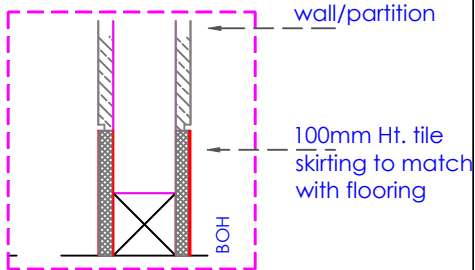

3 SECTION - S3
Scale: 1:4

LEGEND :

LEGEND: SKIRTING		
SINO	SYMBOL	DESCRIPTION
S1		75 MM HT SKIRTING TO MATCH WITH VOX FLOORING
S2		75 MM HT SKIRTING TO MATCH WITH VOX FLOORING
S3		75MM HT. SKIRTING MATCHING TO VPX FLOORING

KEY PLAN :

REVISIONS


R01	
R02	
R03	

DRAWING NAME:

SKIRTING LAYOUT

DESIGNED BY:	CHECKED BY:	
RISHAD	-	
DATE:	REVISION NO:	DWG NO:
04-08-2026	00	00



COMPASS

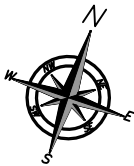


STORE INFO:

STATE	MAHARASHTRA
CITY	MUMBAI
HIGHSTREET/MALL	AAA
AREA	400 SFT
SLAB BOTTOM:	2500 MM
BEAM BOTTOM:	2346 MM, SPANDREL BEAM - 2173MM


NOTE -
1. all partition to be done with 12mm thick ply/MDF Or Directly clad vox material on the GI Frame

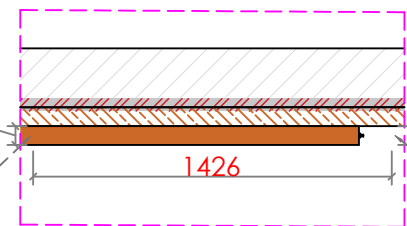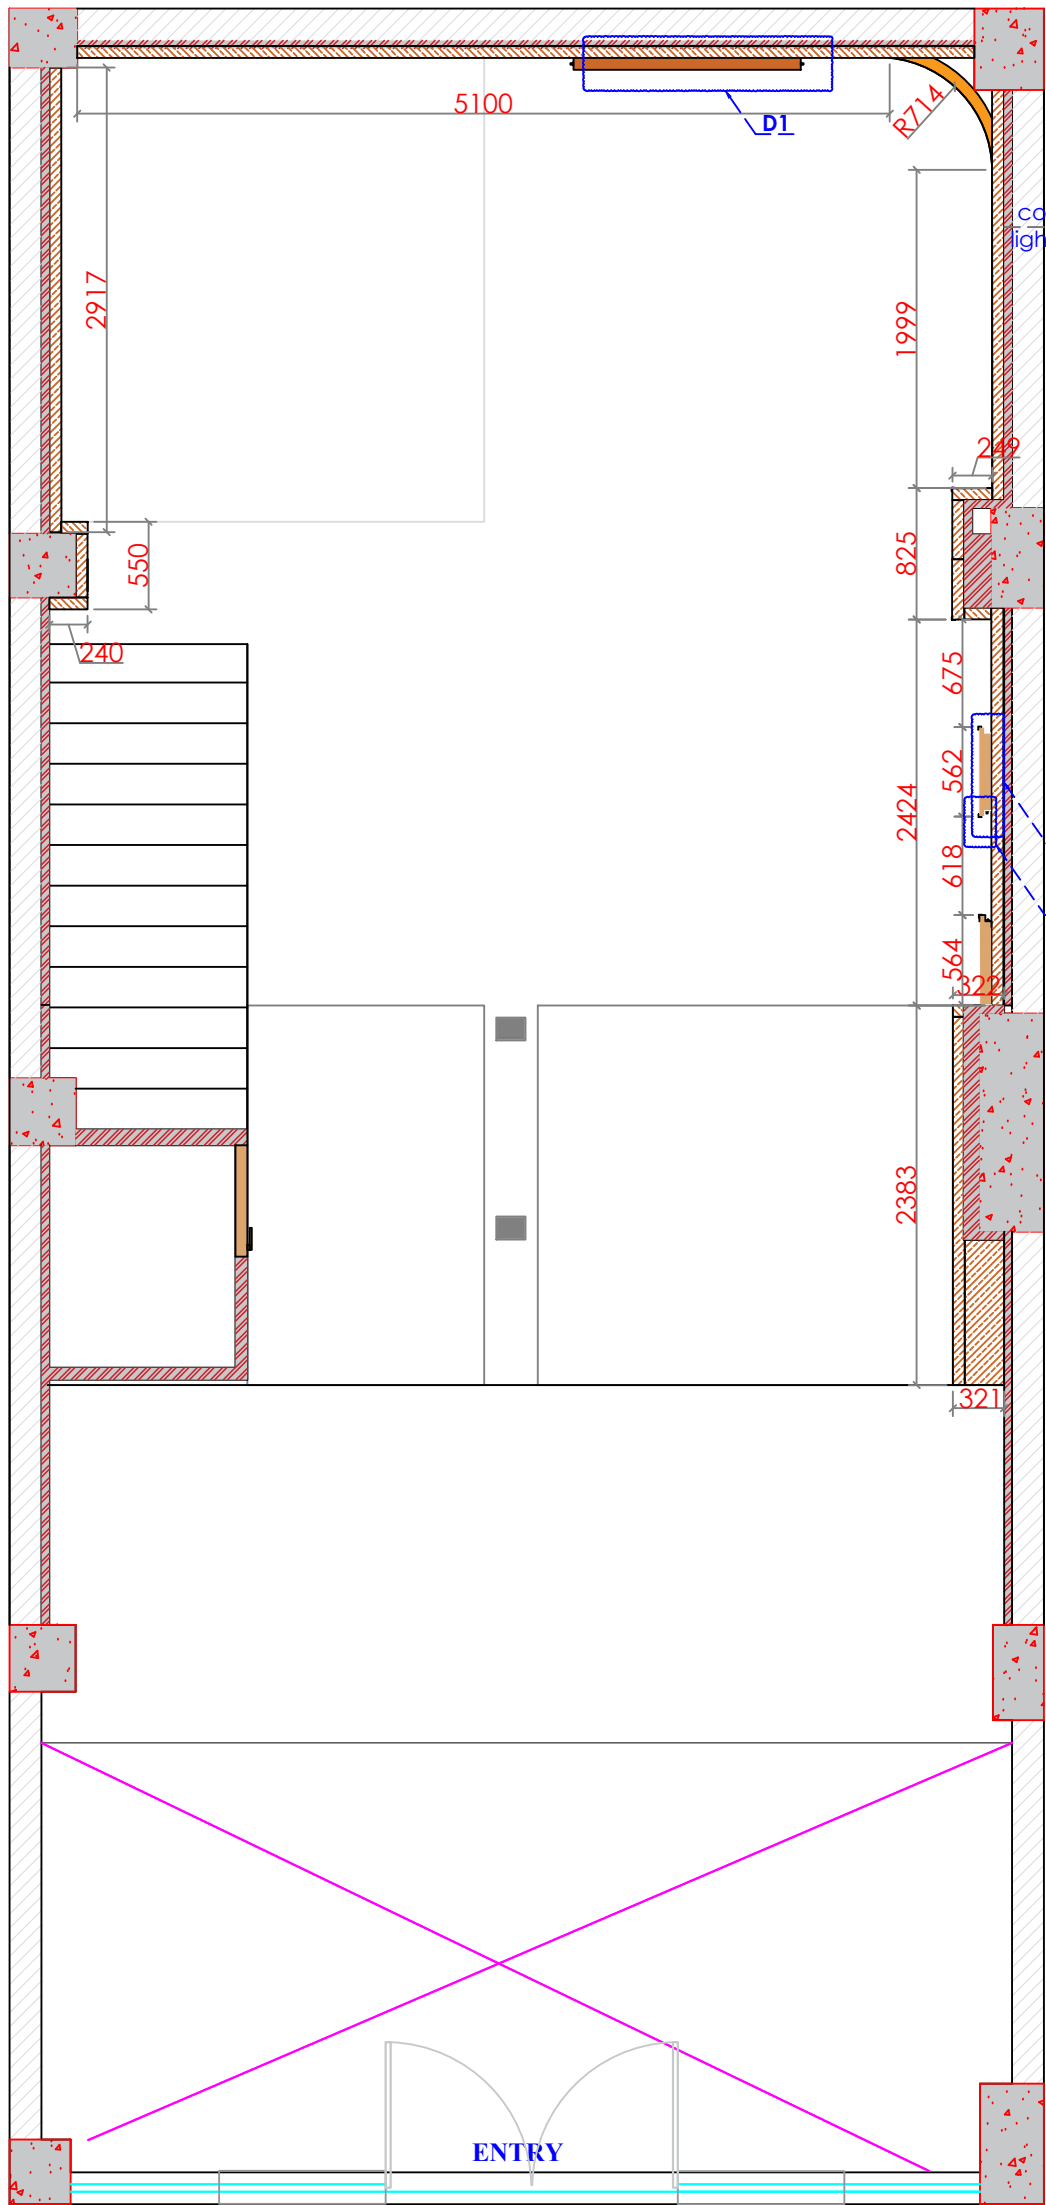

1 DETAIL- 1

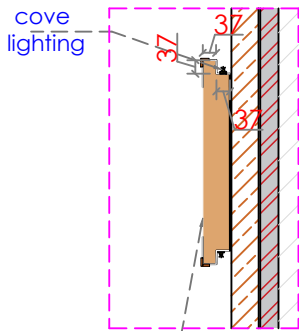

2 DETAIL- 2

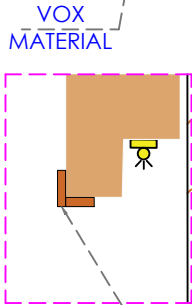

3 DETAIL- 3

LEGEND :

KEY PLAN :

REVISIONS

R01

R02

R03

DRAWING NAME:

PARTITION LAYOUT

DESIGNED BY:

CHECKED BY:

RISHAD

-

DATE:

REVISION NO:

DWG NO:

04-08-2026

00

00



NO.681, SUKHADA, 2ND FLOOR, 2ND PHASE,
2ND BLOCK, RAILWAY PARALLEL ROAD,
NEAR MALL OF ASIA, BANGALORE,
KARNATAKA, 560097
domoredesign.co.in

GENERAL NOTES:

THIS DRAWING IS COPYRIGHT & PROPERTY OF
DOMORE DESIGN PVT.LTD. AND IS NOT TO BE
REPRODUCED, COPIED OR USED FOR ANY OTHER PURPOSE.
WRITTEN DIMENSIONS TO BE FOLLOWED.
DIMENSIONS TO BE CROSS CHECKED PRIOR TO THE
COMMENCEMENT OF WORK.
ALL DRAWINGS TO BE READ IN CONJUNCTION TO THE
CONSULTANTS AND VENDORS DRAWINGS/DETAILS.
FOR ALL LEGENDS, SYMBOLS, ABBREVIATIONS AND
ANNOTATIONS RELATED QUERIES,
REFER TO REFERENCE SHEET.
ANY DISCREPANCY OR DOUBT IN DRAWING TO BE
BROUGHT
TO THE NOTICE OF DOMORE DESIGN PVT.LTD
SCALE : AS MENTIONED

PROJECT NAME :


VOX
TURQUOISE LUXURY
DEFINED - MUMBAI

COMPASS



STORE INFO:

STATE	MAHARASHTRA
CITY	MUMBAI
HIGHSTREET/MALL	AAA
AREA	400 SFT
SLAB BOTTOM:	2500 MM
BEAM BOTTOM:	2346 MM, SPANDREL BEAM - 2173MM

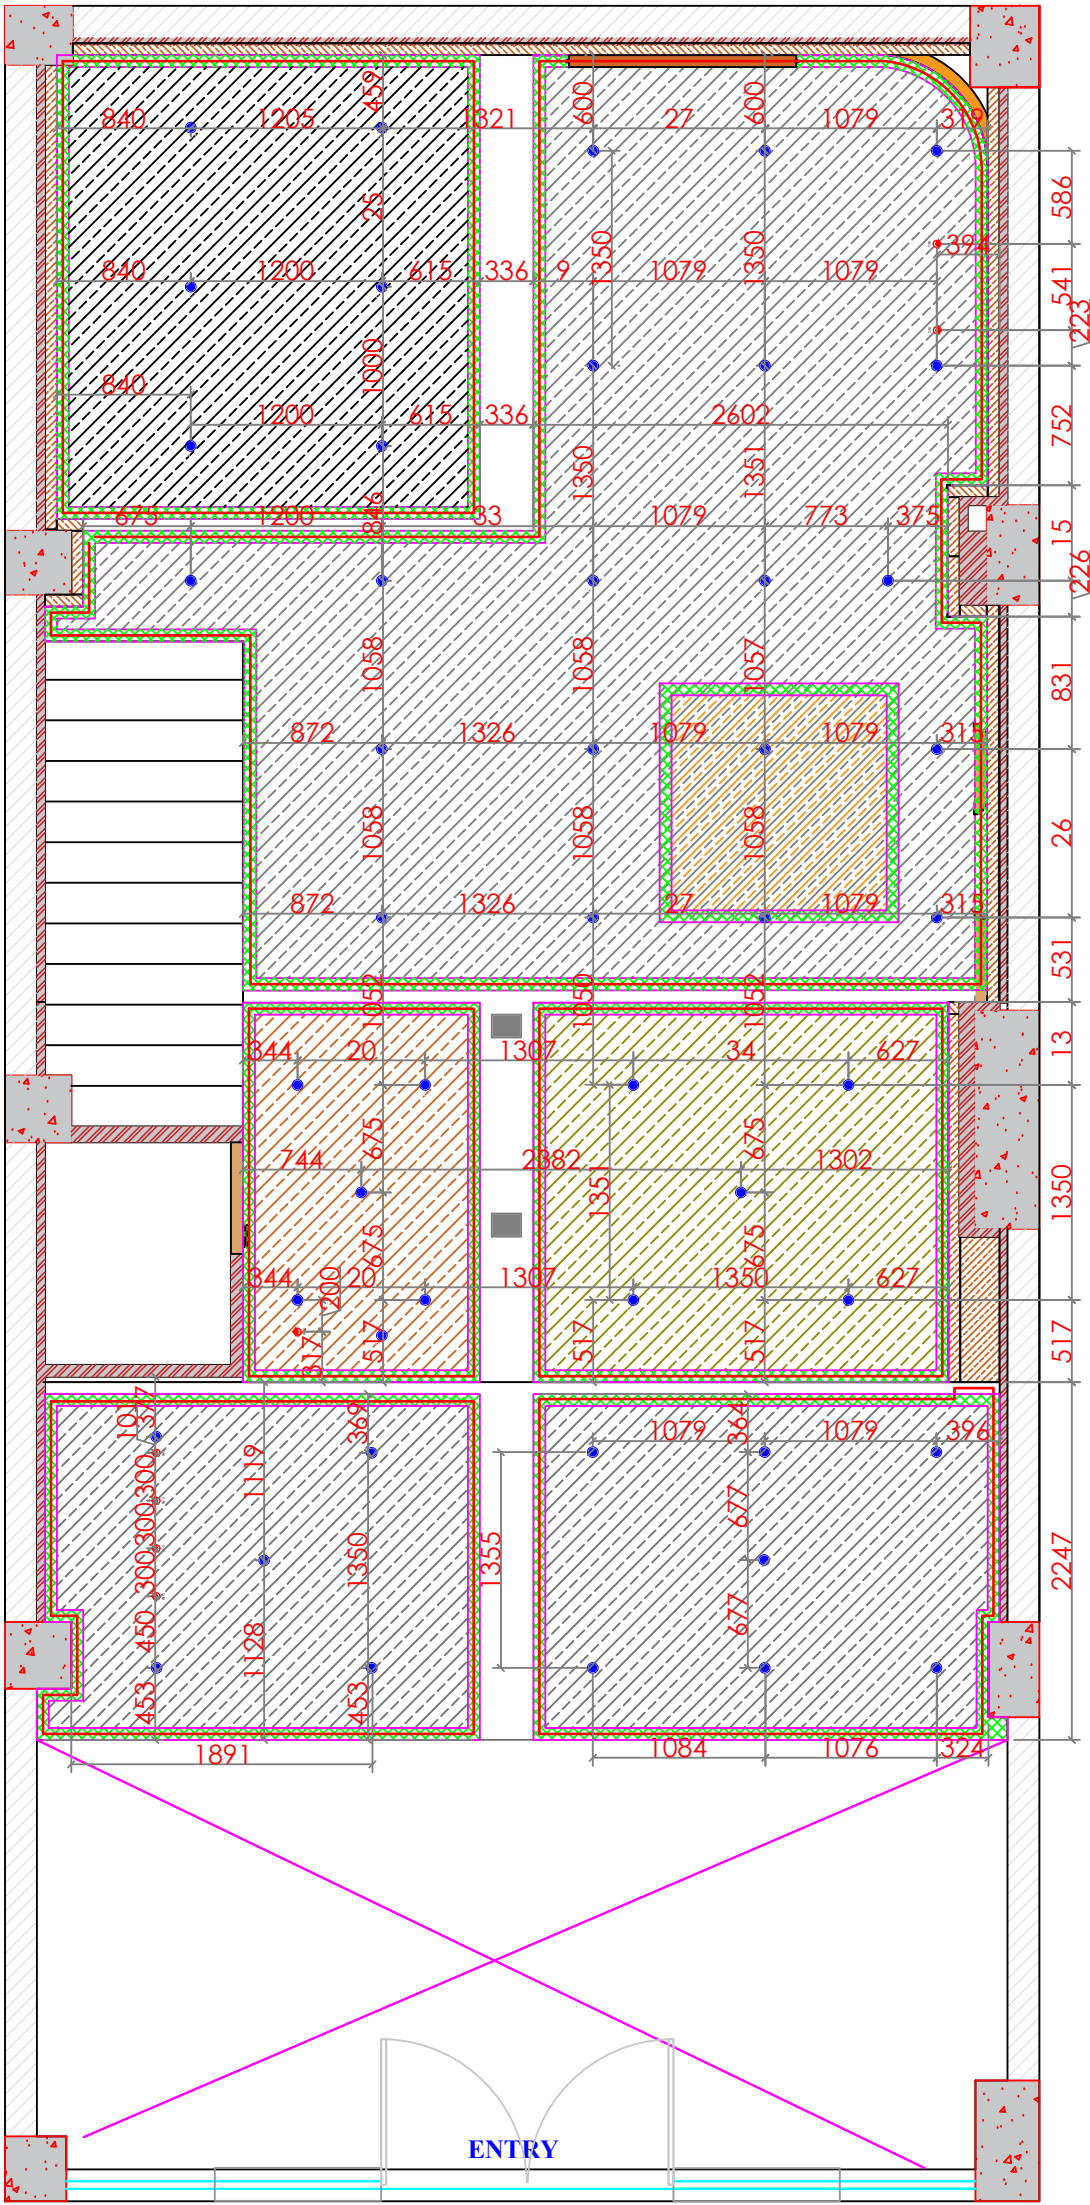

LEGEND :

LIGHTING LEGEND				
SL.NO	SYMBOLS	PRODUCT DESCRIPTION	CCT	QNTY
1	•	EOS 12W ASY RECESSED MOUNTED LED DL+WW	4000K	7
2	•	EOS 12W 53° RECESSED MOUNTED LED DL	4000K	47
3		SERIES LED COVE LIGHT 10834+23408+9675+7440MM		77MT

KEY PLAN :

REVISIONS

R01	
R02	
R03	

DRAWING NAME:

LIGHTING LAYOUT

DESIGNED BY:	CHECKED BY:	
RISHAD	-	
DATE:	REVISION NO:	DWG NO:
04-08-2026	00	00



DOMORE DESIGN PVT. LTD.
NO.681, SUKHADA, 2ND FLOOR, 2ND PHASE,
2ND BLOCK, RAILWAY PARALLEL ROAD,
NEAR MALL OF ASIA, BANGALORE,
KARNATAKA, 560097
domoredesign.co.in

GENERAL NOTES:

THIS DRAWING IS COPYRIGHT & PROPERTY OF DOMORE DESIGN PVT.LTD. AND IS NOT TO BE REPRODUCED, COPIED OR USED FOR ANY OTHER PURPOSE. WRITTEN DIMENSIONS TO BE FOLLOWED. DIMENSIONS TO BE CROSS CHECKED PRIOR TO THE COMMENCEMENT OF WORK. ALL DRAWINGS TO BE READ IN CONJUNCTION TO THE CONSULTANTS AND VENDORS DRAWINGS/DETAILS. FOR ALL LEGENDS, SYMBOLS, ABBREVIATIONS AND ANNOTATIONS RELATED QUERIES, REFER TO REFERENCE SHEET. ANY DISCREPANCY OR DOUBT IN DRAWING TO BE BROUGHT TO THE NOTICE OF DOMORE DESIGN PVT.LTD. SCALE : AS MENTIONED

PROJECT NAME :


VOX
TURQUOISE LUXURY
DEFINED - MUMBAI

COMPASS



STORE INFO:

STATE	MAHARASHTRA
CITY	MUMBAI
HIGHSTREET/MALL	AAA
AREA	400 SFT
SLAB BOTTOM:	2500 MM
BEAM BOTTOM:	2346 MM, SPANDREL BEAM - 2173MM

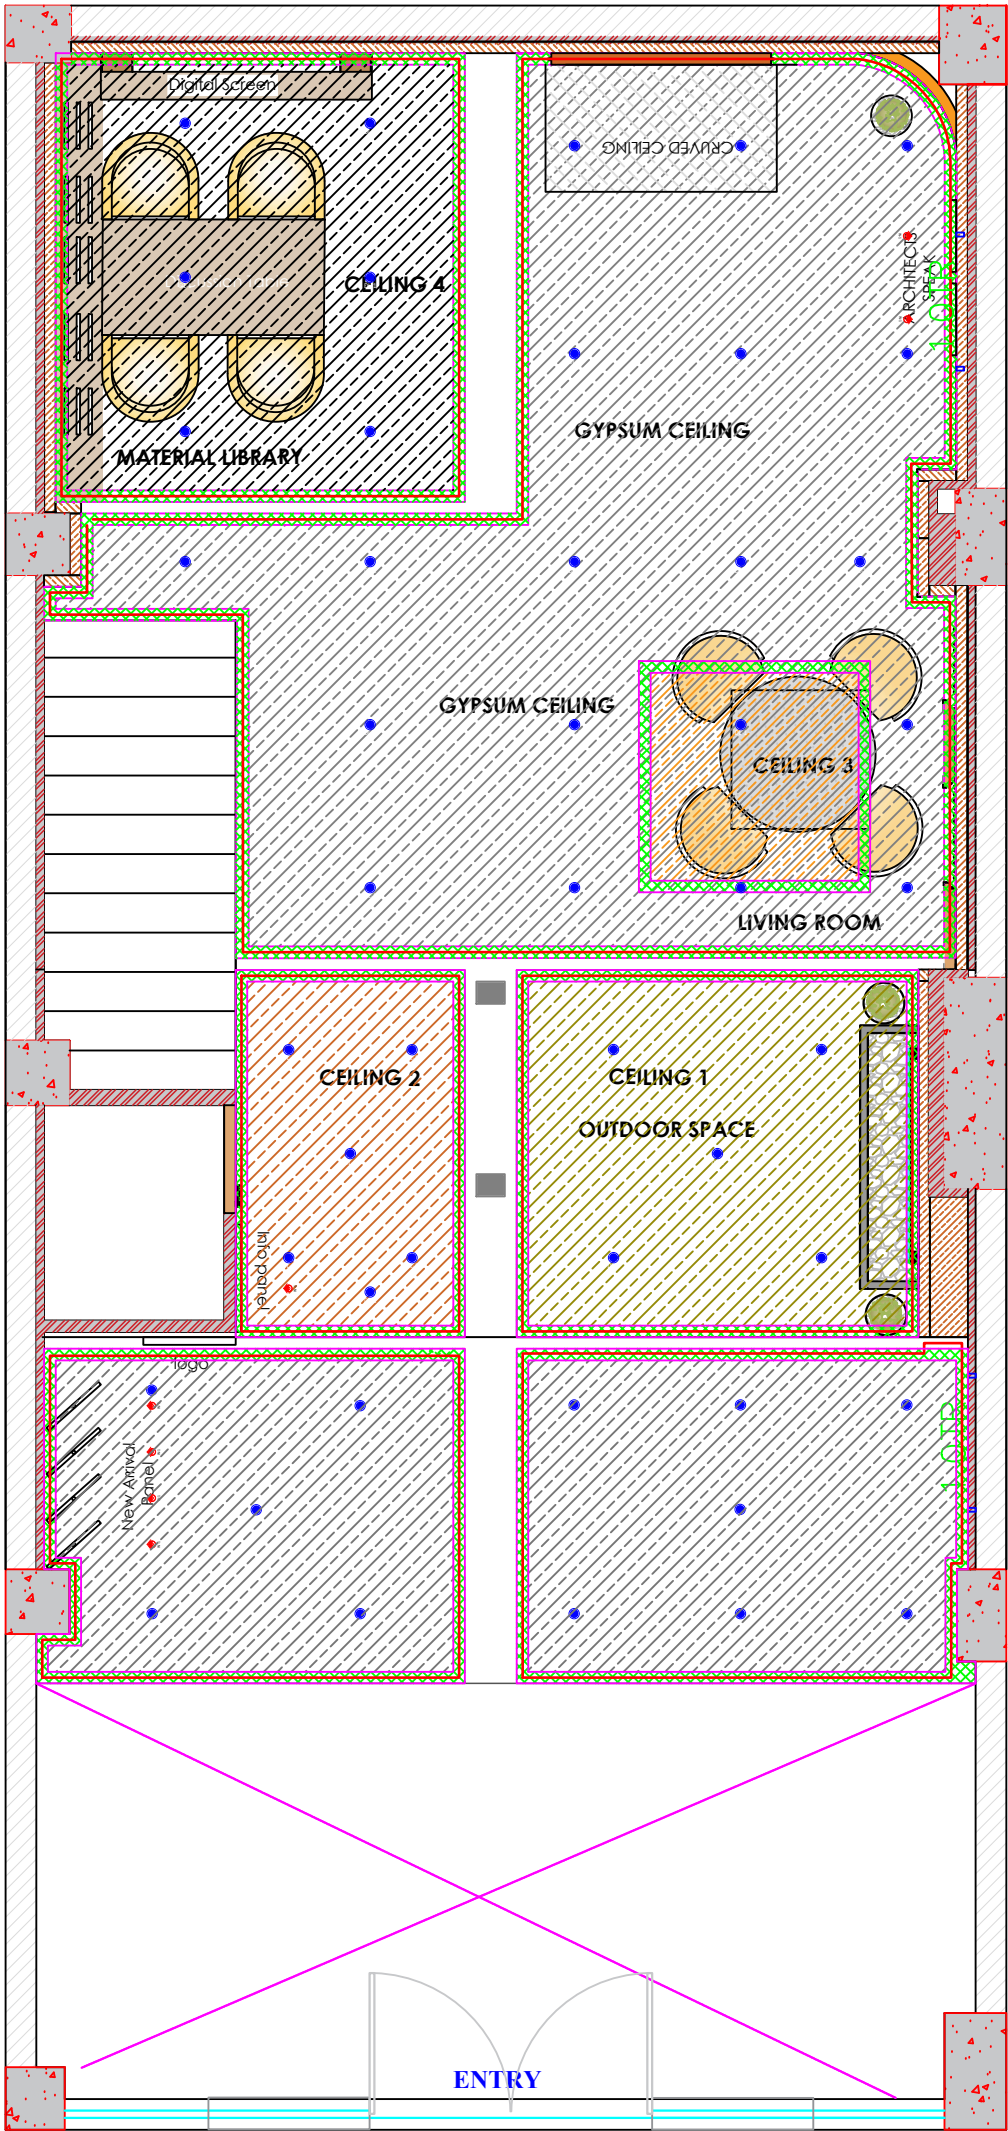

ENTRY

LEGEND :

LIGHTING LEGEND				
SL.NO	SYMBOLS	PRODUCT DESCRIPTION	CCT	QNTY
1		EOS 12W ASY RECESSED MOUNTED LED DL+WW	4000K	7
2		EOS 12W 53° RECESSED MOUNTED LED DL	4000K	47
3		SERIES LED COVE LIGHT 10834+23408+9675+7440MM		77MT

KEY PLAN :

REVISIONS

R01

R02

R03



DOMORE DESIGN PVT. LTD.
NO.681, SUKHADA, 2ND FLOOR, 2ND PHASE,
2ND BLOCK, RAILWAY PARALLEL ROAD,
NEAR MALL OF ASIA, BANGALORE,
KARNATAKA, 560097
domoredesign.co.in


GENERAL NOTES:

THIS DRAWING IS COPYRIGHT & PROPERTY OF DOMORE DESIGN PVT.LTD. AND IS NOT TO BE REPRODUCED, COPIED OR USED FOR ANY OTHER PURPOSE. WRITTEN DIMENSIONS TO BE FOLLOWED. DIMENSIONS TO BE CROSS CHECKED PRIOR TO THE COMMENCEMENT OF WORK. ALL DRAWINGS TO BE READ IN CONJUNCTION TO THE CONSULTANTS AND VENDORS DRAWINGS/DETAILS. FOR ALL LEGENDS, SYMBOLS, ABBREVIATIONS AND ANNOTATIONS RELATED QUERIES, REFER TO REFERENCE SHEET. ANY DISCREPANCY OR DOUBT IN DRAWING TO BE BROUGHT TO THE NOTICE OF DOMORE DESIGN PVT.LTD
SCALE : AS MENTIONED

PROJECT NAME :

VOX
TURQUOISE LUXURY
DEFINED - MUMBAI

COMPASS

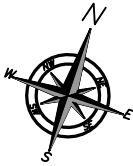


STORE INFO:

STATE	MAHARASHTRA
CITY	MUMBAI
HIGHSTREET/MALL	AAA
AREA	400 SFT
SLAB BOTTOM:	2500 MM
BEAM BOTTOM:	2346 MM, SPANDREL BEAM - 2173MM

DRAWING NAME:

LIGHTING LAYOUT W
FURNITURE LAYOUT

DESIGNED BY:	CHECKED BY:	
RISHAD	-	
DATE:	REVISION NO:	DWG NO:
04-08-2026	00	00

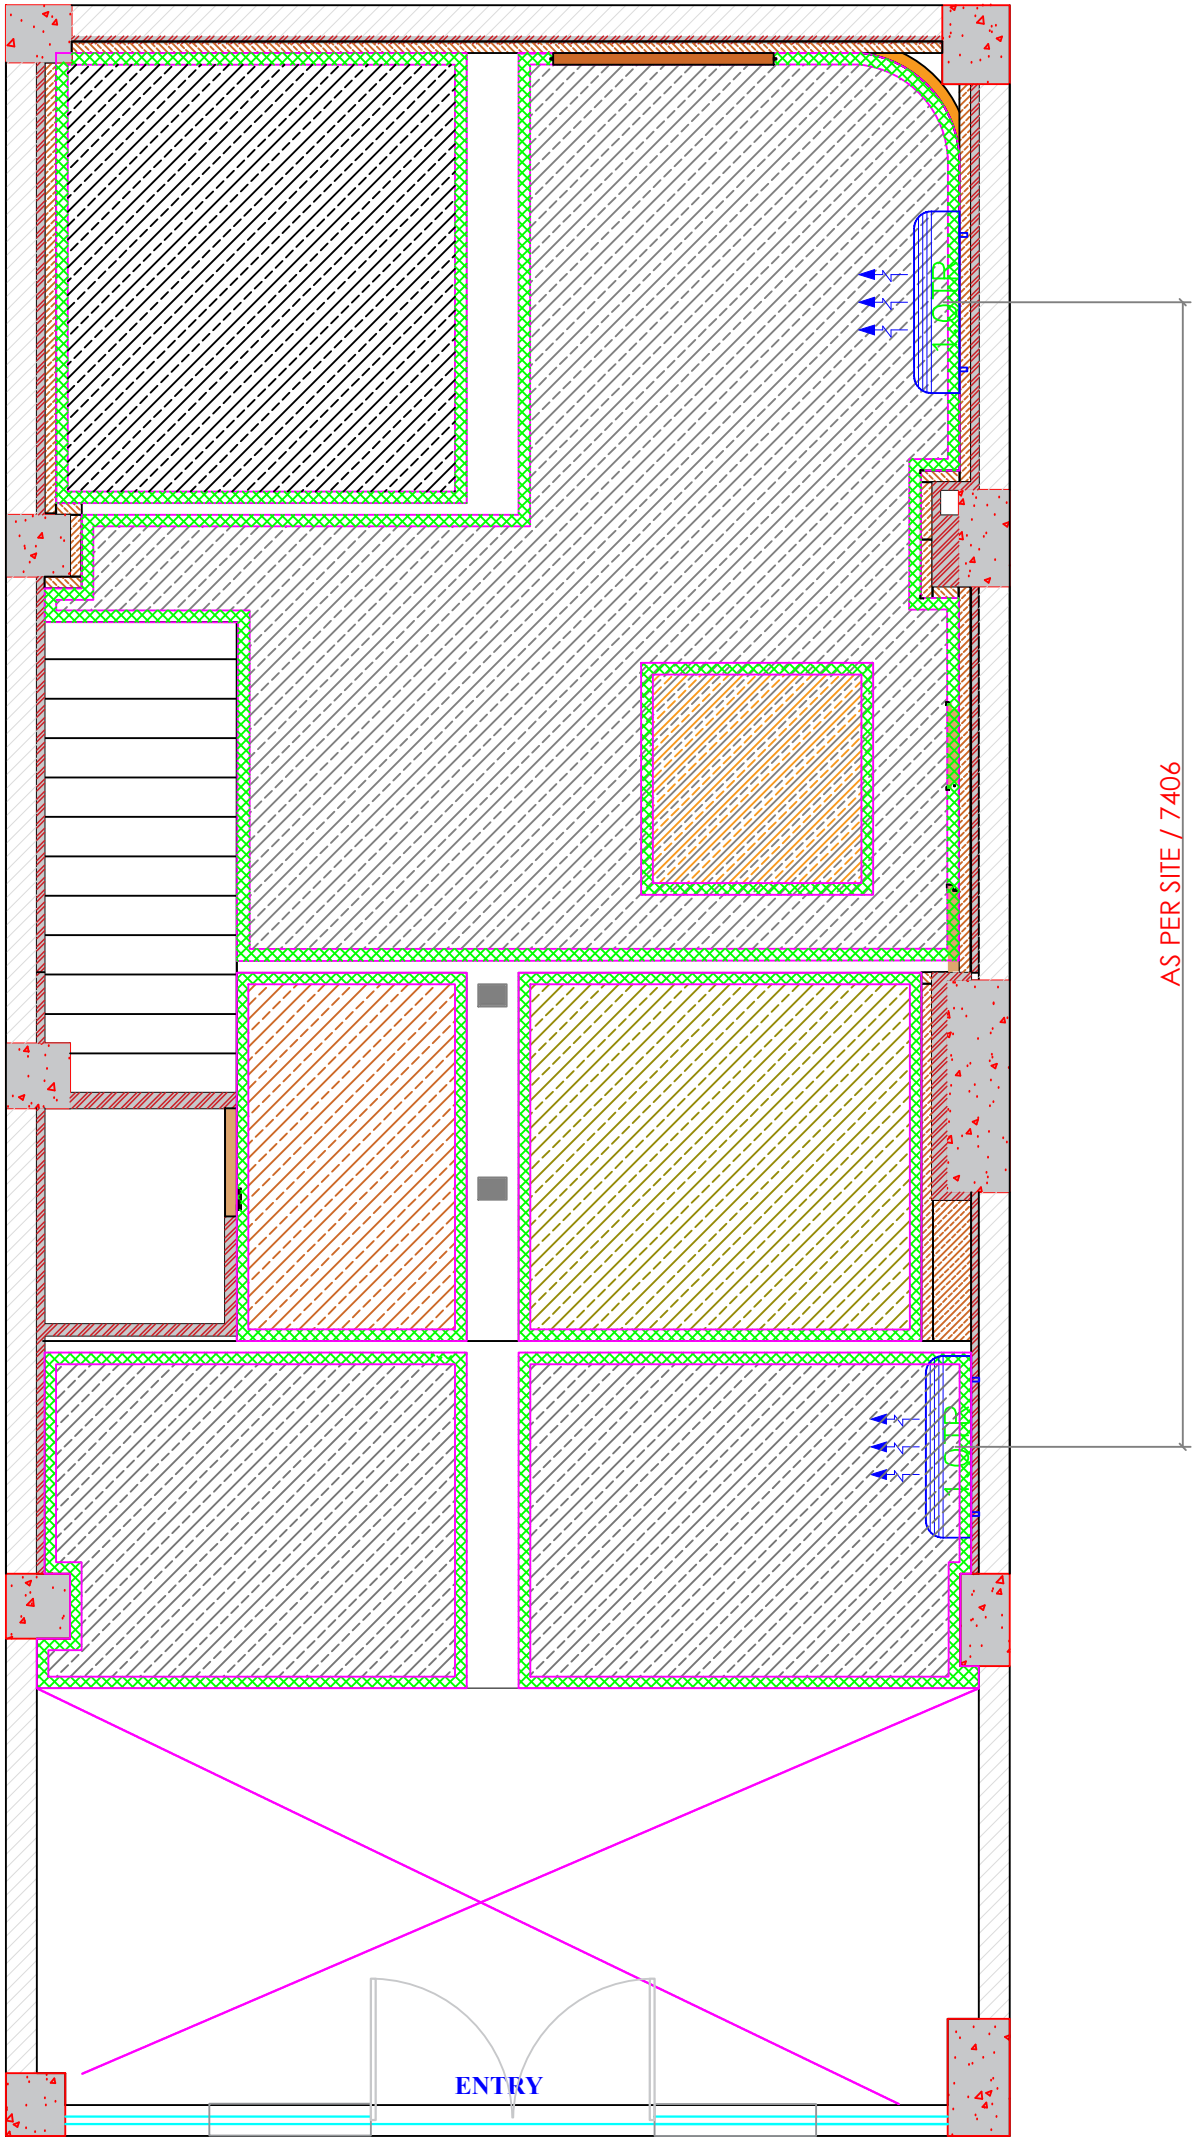

LEGEND :

KEY PLAN :

REVISIONS

R01

R02

R03



DOMORE DESIGN PVT. LTD.
NO.681, SUKHADA, 2ND FLOOR, 2ND PHASE,
2ND BLOCK, RAILWAY PARALLEL ROAD,
NEAR MALL OF ASIA, BANGALORE,
KARNATAKA, 560097

domoredesign.co.in

GENERAL NOTES:

THIS DRAWING IS COPYRIGHT & PROPERTY OF
DOMORE DESIGN PVT.LTD. AND IS NOT TO BE
REPRODUCED, COPIED OR USED FOR ANY OTHER PURPOSE.
WRITTEN DIMENSIONS TO BE FOLLOWED.
DIMENSIONS TO BE CROSS CHECKED PRIOR TO THE
COMMENCEMENT OF WORK.
ALL DRAWINGS TO BE READ IN CONJUNCTION TO THE
CONSULTANTS AND VENDORS DRAWINGS/DETAILS.
FOR ALL LEGENDS, SYMBOLS, ABBREVIATIONS AND
ANNOTATIONS RELATED QUERIES.
REFER TO REFERENCE SHEET.
ANY DISCREPANCY OR DOUBT IN DRAWING TO BE
BROUGHT
TO THE NOTICE OF DOMORE DESIGN PVT.LTD

SCALE : AS MENTIONED

PROJECT NAME :

**VOX
TURQUOISE LUXURY
DEFINED - MUMBAI**

COMPASS




STORE INFO:

STATE	MAHARASHTRA
CITY	MUMBAI
HIGHSTREET/MALL	AAA
AREA	400 SFT
SLAB BOTTOM:	2500 MM
BEAM BOTTOM:	2346 MM, SPANDREL BEAM - 2173MM

DRAWING NAME:

EXISITNG AC LAYOUT

DESIGNED BY:	CHECKED BY:	
RISHAD	-	
DATE:	REVISION NO:	DWG NO:
04-08-2026	00	00

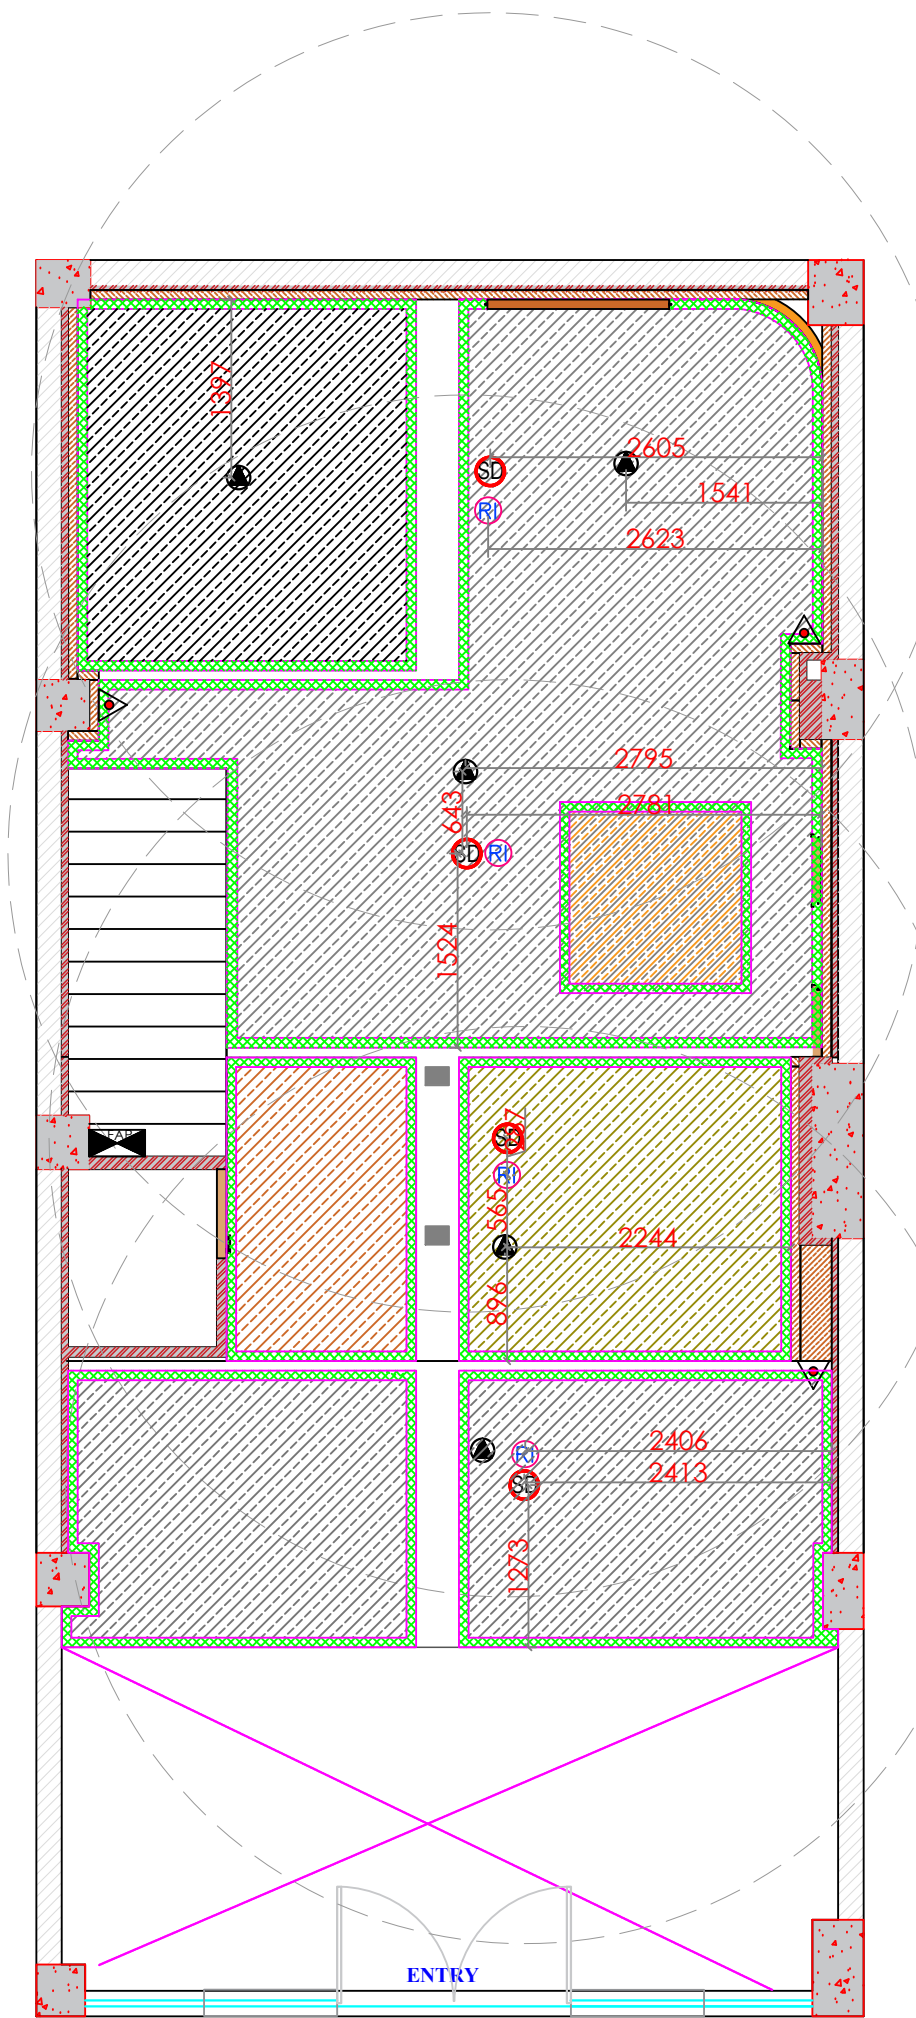

LEGEND :

LEGEND : FAS

SINO	SYMBOL	DESCRIPTION	QTY.
1		PROPOSED SMOKE DETECTOR BELOW FALSE CEILING	04
2		PROPOSED ABOVE FALSE CEILING SMOKE DETECTOR	04
3		RESPONSE INDICATOR	04
4		AUTOMATIC EXTINGUISHER CEILING MOUNTED	00
5		FIRE EXTINGUISHER CO2 5KG WITH AUTOGLOW SIGNAGE	00
6		MANUAL CALL POINT @ 1350MM FROM FFL(Break Glass Type)	01
7		HOOTER @ FALSE CEILING LEVEL	01
8		FIRE ALARM CONTROL PANEL-	01
9		FIRE EXTINGUISHER ABC 2.5KG WITH AUTOGLOW SIGNAGE	03
9		FIRE EXTINGUISHER DRY WITH AUTOGLOW SIGNAGE	00

KEY PLAN :

REVISIONS

R01
R02
R03


STORE INFO:

STATE	MAHARASHTRA
CITY	MUMBAI
HIGHSTREET/MALL	AAA
AREA	400 SFT
SLAB BOTTOM:	2500 MM
BEAM BOTTOM:	2346 MM, SPANDREL BEAM - 2173MM

DRAWING NAME:

FAS LAYOUT

DESIGNED BY:	CHECKED BY:	
RISHAD	-	
DATE:	REVISION NO:	DWG NO:
04-08-2026	00	00

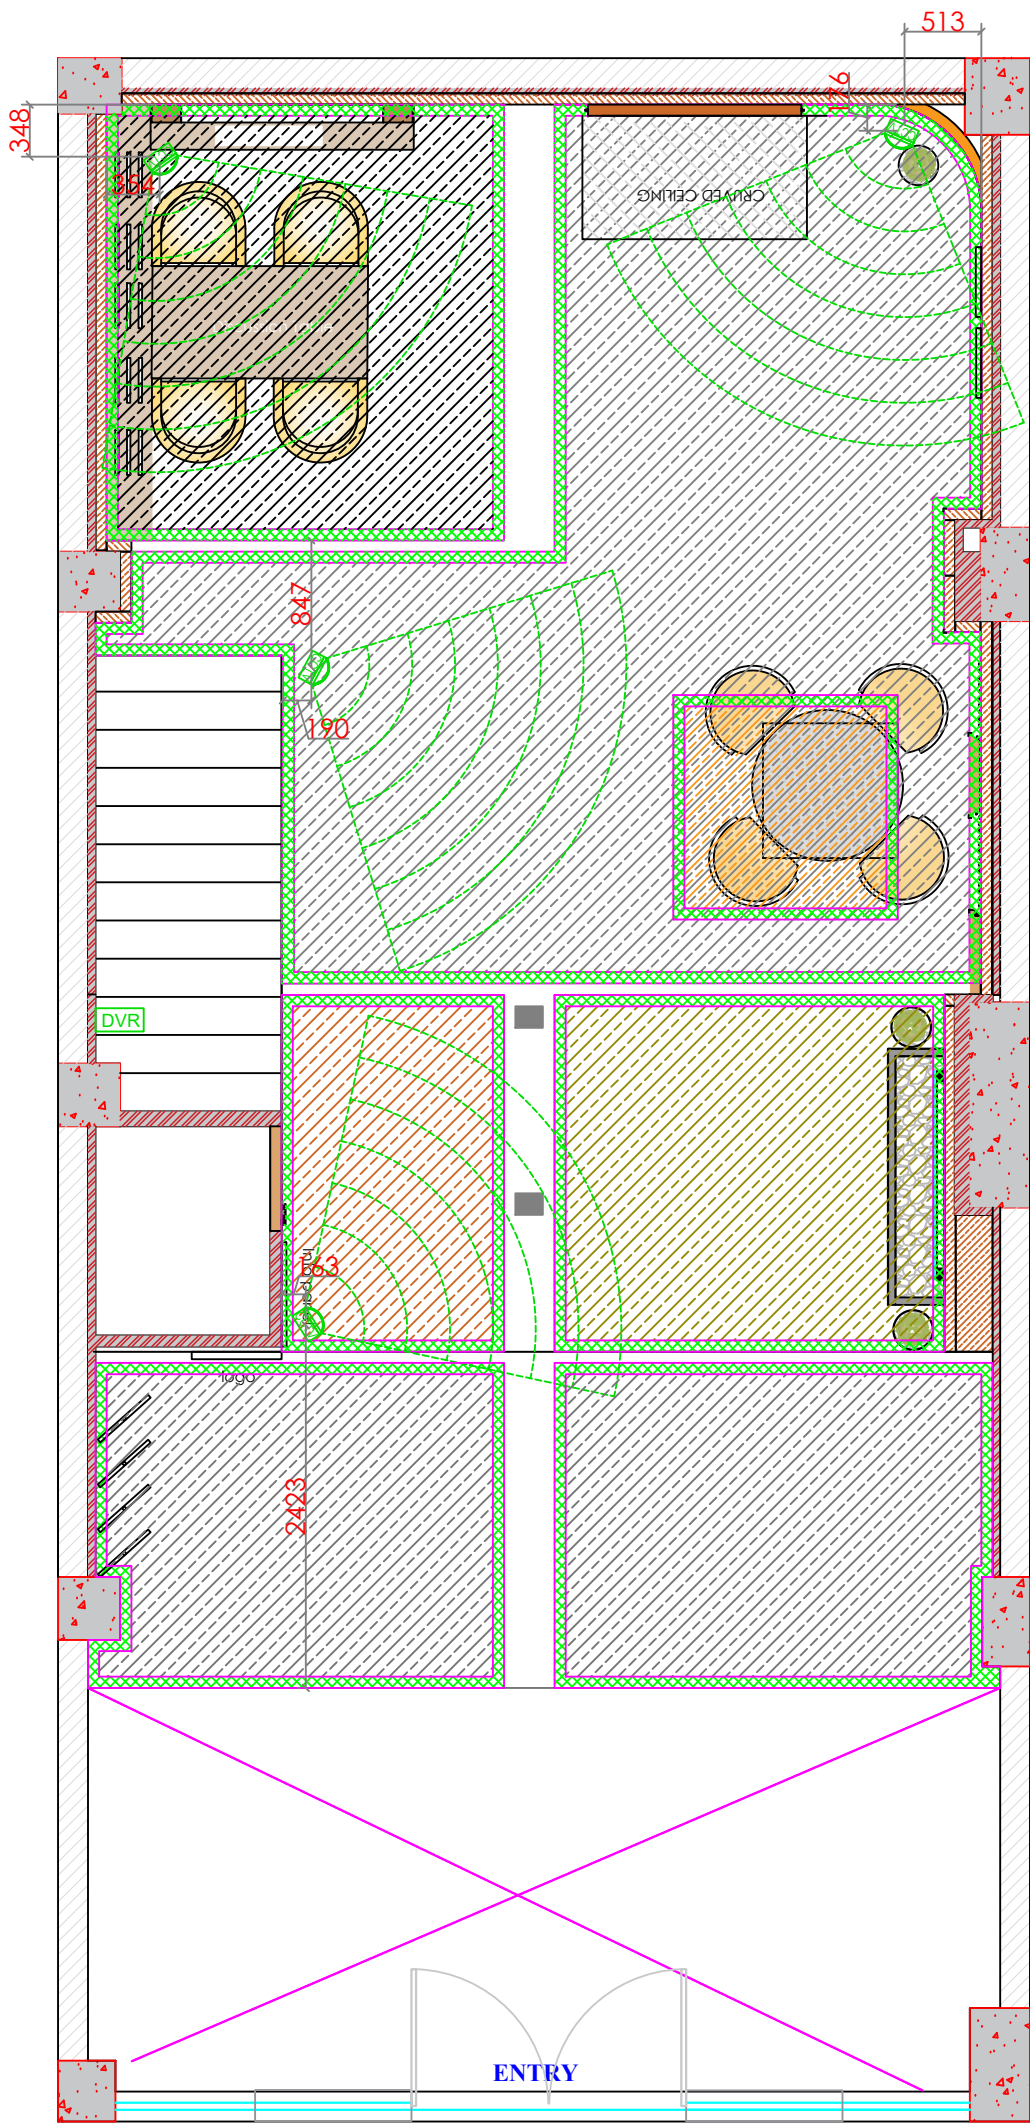

LEGEND :

LEGEND : CCTV

SINO	SYMBOL	DESCRIPTION	QTY.
1		HIK VISION MAKE ,INFRA RED ENABLED ONE HIGH RESOLUTION , FIXED 6.0MM LENS DOME CAMERA	04
2		FISH EYE CAMERA	00
3		BULLET-PROOF CAMERA FOR OUTSIDE	00
4		DVR UNIT	01

KEY PLAN :

REVISIONS

R01
R02
R03



DOMORE DESIGN PVT. LTD.
NO.681, SUKHADA, 2ND FLOOR, 2ND PHASE,
2ND BLOCK, RAILWAY PARALLEL ROAD,
NEAR MALL OF ASIA, BANGALORE,
KARNATAKA, 560097
domoredesign.co.in


GENERAL NOTES:

THIS DRAWING IS COPYRIGHT & PROPERTY OF
DOMORE DESIGN PVT.LTD. AND IS NOT TO BE
REPRODUCED, COPIED OR USED FOR ANY OTHER PURPOSE.
WRITTEN DIMENSIONS TO BE FOLLOWED.
DIMENSIONS TO BE CROSS CHECKED PRIOR TO THE
COMMENCEMENT OF WORK.
ALL DRAWINGS TO BE READ IN CONJUNCTION TO THE
CONSULTANTS AND VENDORS DRAWINGS/DETAILS.
FOR ALL LEGENDS, SYMBOLS, ABBREVIATIONS AND
ANNOTATIONS RELATED QUERIES,
REFER TO REFERENCE SHEET.
ANY DISCREPANCY OR DOUBT IN DRAWING TO BE
BROUGHT
TO THE NOTICE OF DOMORE DESIGN PVT.LTD
SCALE : AS MENTIONED

PROJECT NAME :

VOX
TURQUOISE LUXURY
DEFINED - MUMBAI

COMPASS

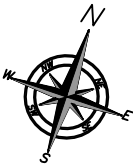


STORE INFO:

STATE	MAHARASHTRA
CITY	MUMBAI
HIGHSTREET/MALL	AAA
AREA	400 SFT
SLAB BOTTOM:	2500 MM
BEAM BOTTOM:	2346 MM, SPANDREL BEAM - 2173MM

DRAWING NAME:

CCTV LAYOUT

DESIGNED BY:	CHECKED BY:	
RISHAD	-	
DATE:	REVISION NO:	DWG NO:
04-08-2026	00	00

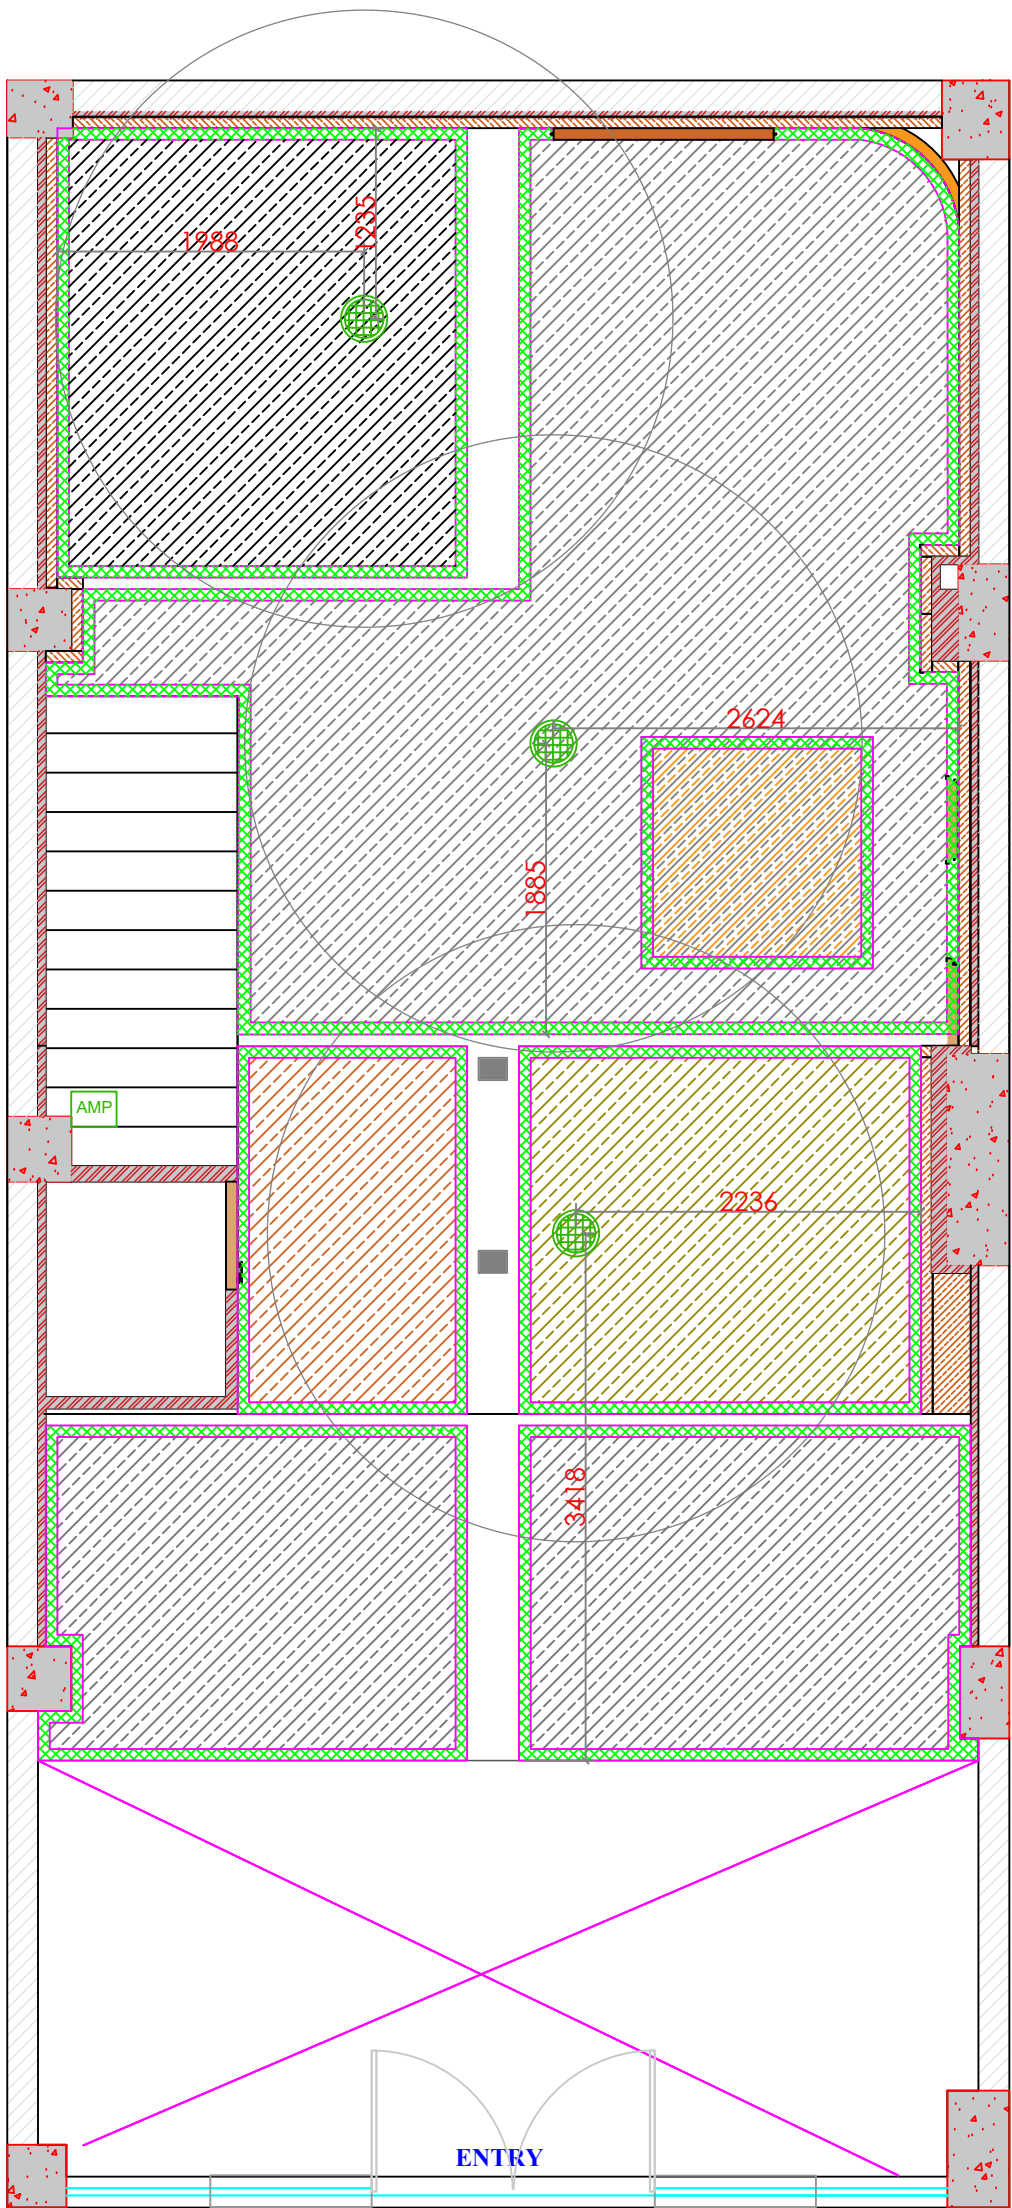

LEGEND :

LEGEND : AUDIO

SINO	SYMBOL	DESCRIPTION	QTY.
1		CEILING MOUNTED SPEAKERS	03
2		SURFACE MOUNTED SPEAKERS	00
3		AMPLIFIER	01

KEY PLAN :

REVISIONS

R01	
R02	
R03	



DOMORE DESIGN PVT. LTD.
NO.681, SUKHADA, 2ND FLOOR, 2ND PHASE,
2ND BLOCK, RAILWAY PARALLEL ROAD,
NEAR MALL OF ASIA, BANGALORE,
KARNATAKA, 560097

domoredesign.co.in

GENERAL NOTES:


THIS DRAWING IS COPYRIGHT & PROPERTY OF
DOMORE DESIGN PVT.LTD. AND IS NOT TO BE
REPRODUCED, COPIED OR USED FOR ANY OTHER PURPOSE.
WRITTEN DIMENSIONS TO BE FOLLOWED.
DIMENSIONS TO BE CROSS CHECKED PRIOR TO THE
COMMENCEMENT OF WORK.
ALL DRAWINGS TO BE READ IN CONJUNCTION TO THE
CONSULTANTS AND VENDORS DRAWINGS/DETAILS.
FOR ALL LEGENDS, SYMBOLS, ABBREVIATIONS AND
ANNOTATIONS RELATED QUERIES,
REFER TO REFERENCE SHEET.
ANY DISCREPANCY OR DOUBT IN DRAWING TO BE
BROUGHT
TO THE NOTICE OF DOMORE DESIGN PVT.LTD

SCALE : AS MENTIONED

PROJECT NAME :

**VOX
TURQUOISE LUXURY
DEFINED - MUMBAI**

COMPASS

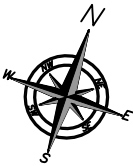


STORE INFO:

STATE	MAHARASHTRA
CITY	MUMBAI
HIGHSTREET/MALL	AAA
AREA	400 SFT
SLAB BOTTOM:	2500 MM
BEAM BOTTOM:	2346 MM, SPANDREL BEAM - 2173MM

DRAWING NAME:

AUDIO LAYOUT

DESIGNED BY:	CHECKED BY:	
RISHAD	-	
DATE:	REVISION NO:	DWG NO:
04-08-2026	00	00

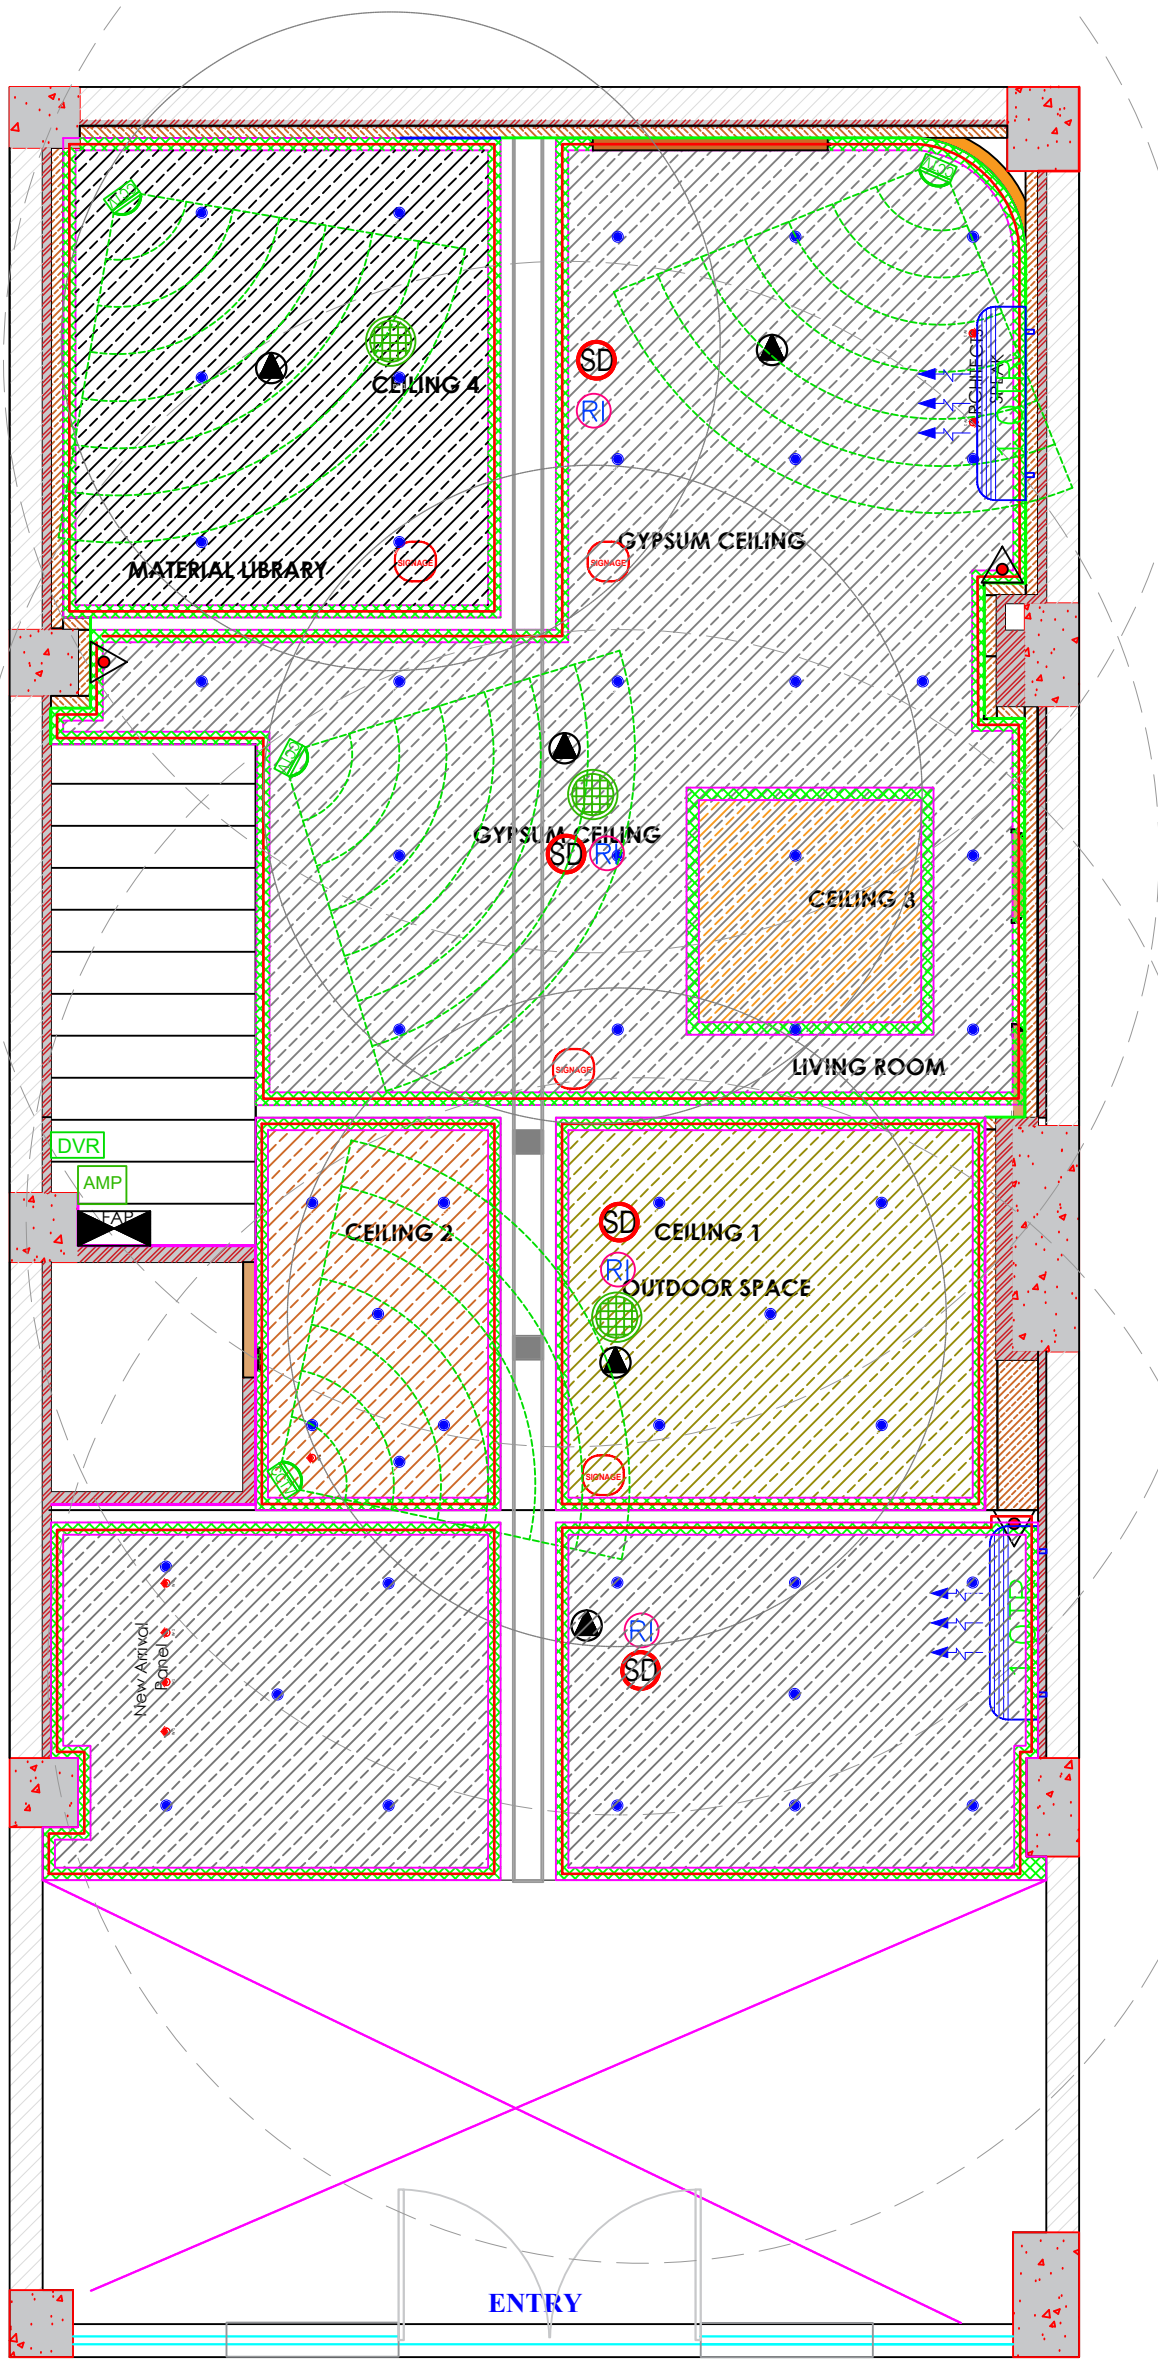

ENTRY

LEGEND :

KEY PLAN :

REVISIONS

R01	
R02	
R03	



DOMORE DESIGN PVT. LTD.
NO.681, SUKHADA, 2ND FLOOR, 2ND PHASE,
2ND BLOCK, RAILWAY PARALLEL ROAD,
NEAR MALL OF ASIA, BANGALORE,
KARNATAKA, 560097
domoredesign.co.in


GENERAL NOTES:

THIS DRAWING IS COPYRIGHT & PROPERTY OF
DOMORE DESIGN PVT.LTD. AND IS NOT TO BE
REPRODUCED, COPIED OR USED FOR ANY OTHER PURPOSE.
WRITTEN DIMENSIONS TO BE FOLLOWED.
DIMENSIONS TO BE CROSS CHECKED PRIOR TO THE
COMMENCEMENT OF WORK.
ALL DRAWINGS TO BE READ IN CONJUNCTION TO THE
CONSULTANTS AND VENDORS DRAWINGS/DETAILS.
FOR ALL LEGENDS, SYMBOLS, ABBREVIATIONS AND
ANNOTATIONS RELATED QUERIES,
REFER TO REFERENCE SHEET.
ANY DISCREPANCY OR DOUBT IN DRAWING TO BE
BROUGHT
TO THE NOTICE OF DOMORE DESIGN PVT.LTD
SCALE : AS MENTIONED

PROJECT NAME :

VOX
TURQUOISE LUXURY
DEFINED - MUMBAI

COMPASS

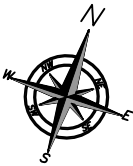


STORE INFO:

STATE	MAHARASHTRA
CITY	MUMBAI
HIGHSTREET/MALL	AAA
AREA	400 SFT
SLAB BOTTOM:	2500 MM
BEAM BOTTOM:	2346 MM, SPANDREL BEAM - 2173MM

DRAWING NAME:

RCP LAYOUT

DESIGNED BY:	CHECKED BY:	
RISHAD	-	
DATE:	REVISION NO:	DWG NO:
04-08-2026	00	00

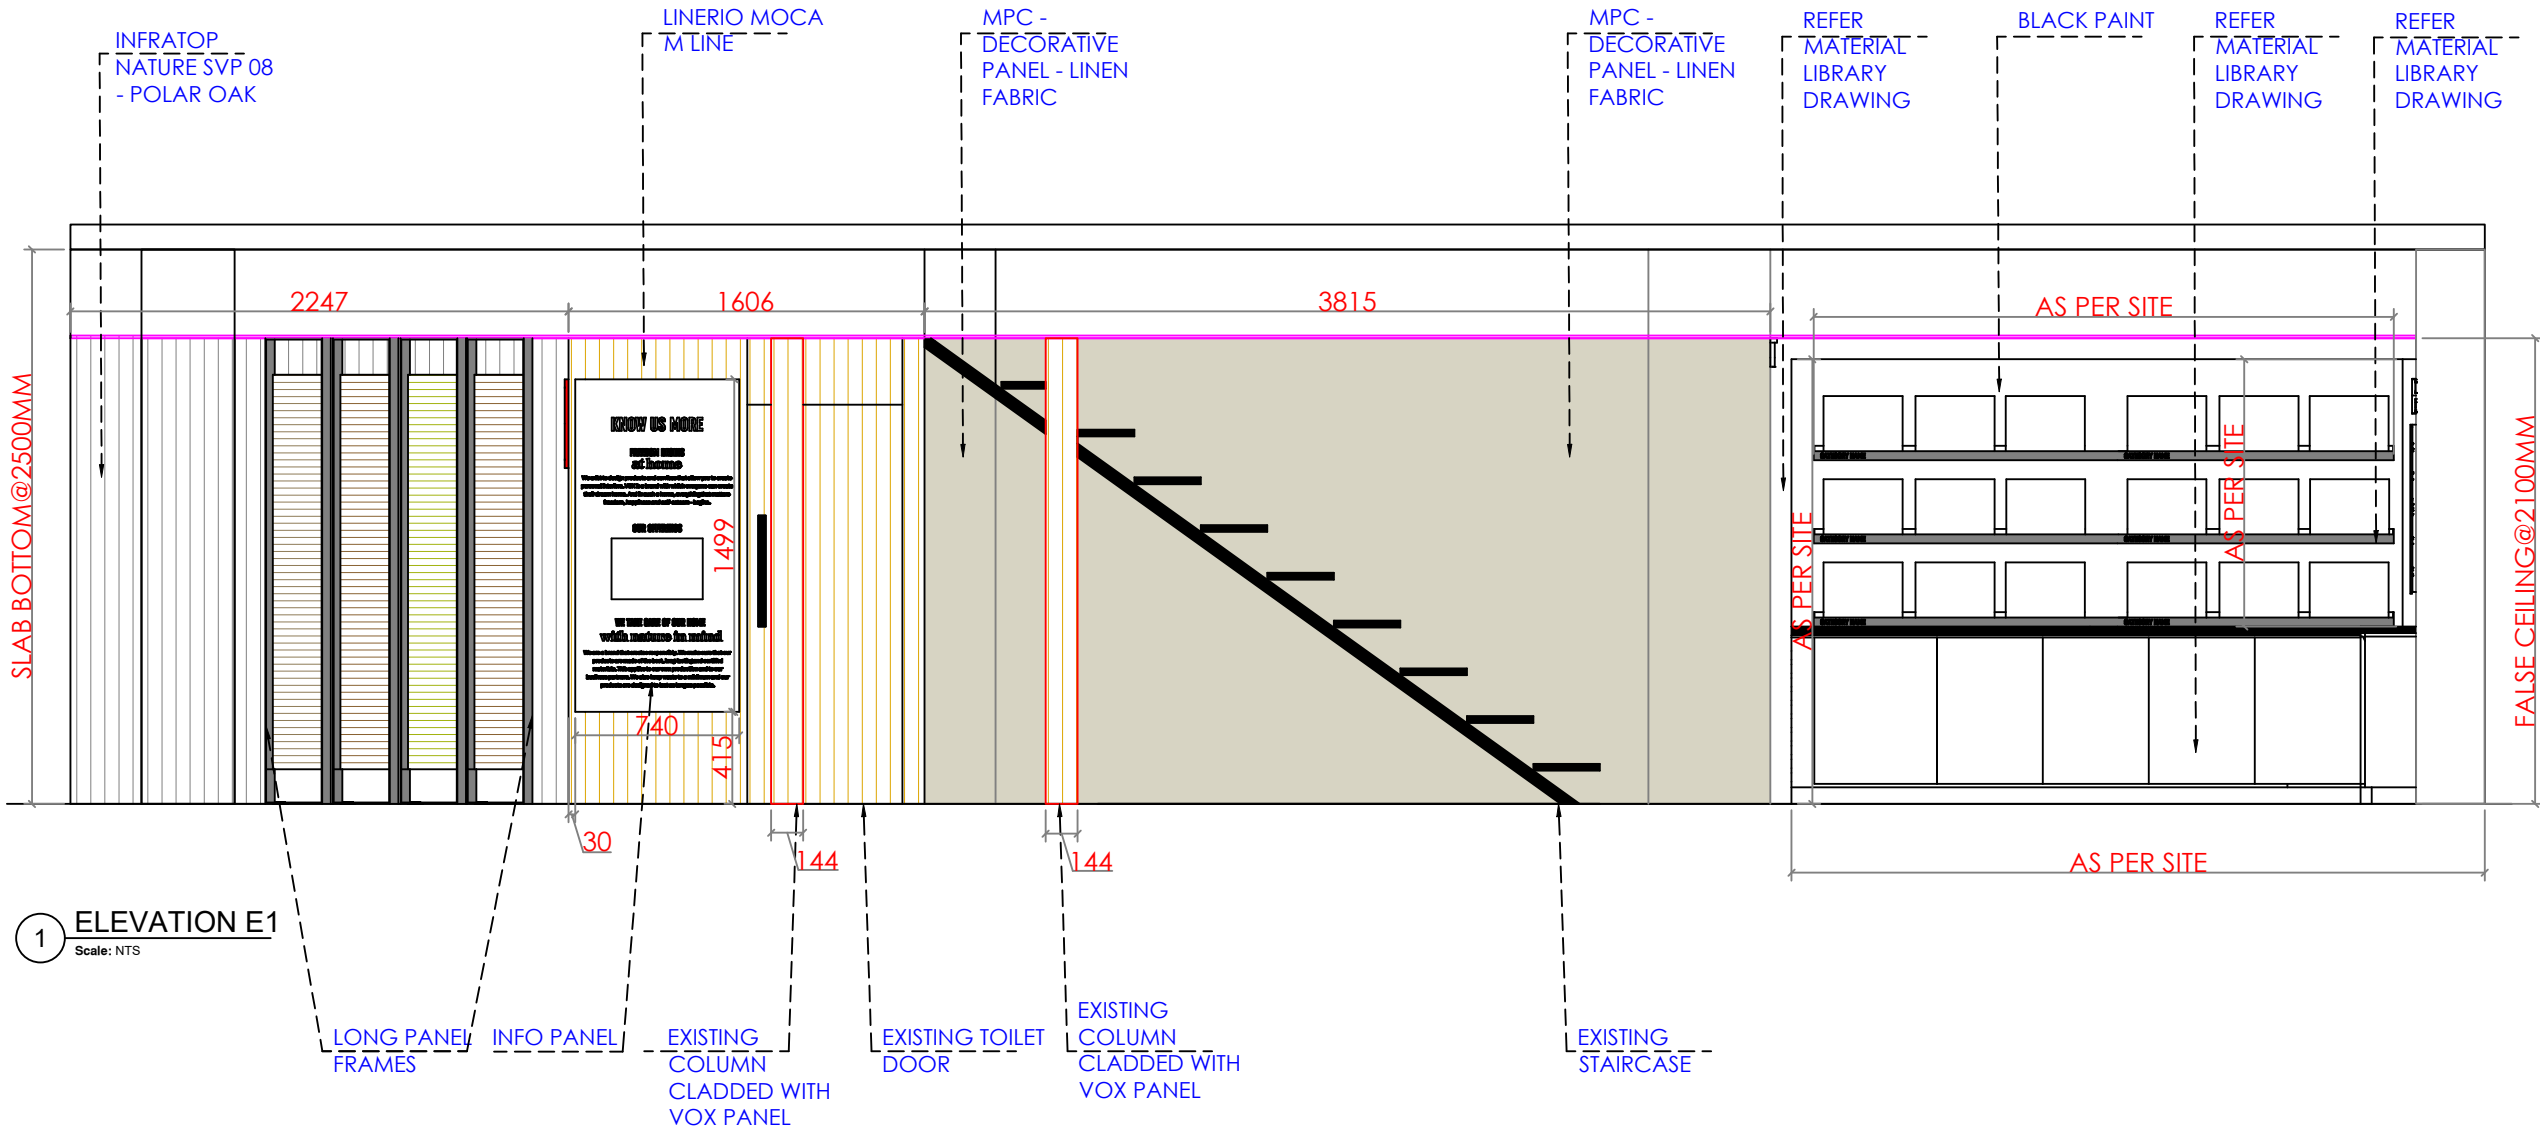

NOTE : 1) MATERIAL LIBRARY DIMENSIONS HAVE BEEN CALCULATED AND MARKED AS PER SITE. THE DISTANCES BETWEEN SHELVES AND THE No. OF STORAGE UNITS HAVE BEEN CALCULATED AS PER SITE AND CLIENT REQUIREMENT DURING THE SITE VISIT.

2) PLEASE REFER MATERIAL LIBRARY DETAILED DRAWINGS FOR FINISHING DETAILS (ALREADY SHARED)

3) FOR FLASE CEILING DETAILS, REFER FALSE & FALSE CEILING DETAIL LAYOUT

LEGEND :



KEY PLAN :

DRAWING NAME:

ELEVATION 1

DESIGNED BY:

RISHAD

DATE:

24-8-2026

CHECKED BY:

AAA

REVISION NO:

R0

DWG NO:

00



DOMORE DESIGN PVT. LTD.
NO.681, SUKHADA, 2ND FLOOR, 2ND PHASE, 2ND BLOCK,
RAILWAY PARALLEL ROAD,
NEAR MALL OF ASIA, BANGALORE, KARNATAKA, 560097
domoredesign.co.in

GENERAL NOTES

THIS DRAWING IS COPYRIGHT & PROPERTY OF DOMORE DESIGN PVT.LTD, AND IS NOT TO BE REPRODUCED, COPIED OR USED FOR ANY OTHER PURPOSE.
WRITTEN DIMENSIONS TO BE FOLLOWED.
DIMENSIONS TO BE CROSS CHECKED PRIOR TO THE COMMENCEMENT OF WORK.
ALL DRAWINGS TO BE READ IN CONJUNCTION TO THE CONSULTANTS AND VENDORS DRAWINGS/DETAILS.
FOR ALL LEGENDS, SYMBOLS, ABBREVIATIONS AND ANNOTATIONS RELATED QUERIES, REFER TO REFERENCE SHEET.
ANY DISCREPANCY OR DOUBT IN DRAWING TO BE BROUGHT TO THE NOTICE OF DOMORE DESIGN PVT.LTD

SCALE : AS MENTIONED

REVISIONS

R01

R02

R03

PROJECT NAME :

TURQUOISE
LUXURYREDEFINED,
MUMBAI

COMPASS:



STORE INFO:

STATE MAHARASHTRA


CITY MUMBAI

HIGHSTREET/MALL TURQUOISE LUXURY REDEFINED


AREA 400 SFT

SLAB BOTTOM: 2500MM

BEAM BOTTOM: 2350 MM

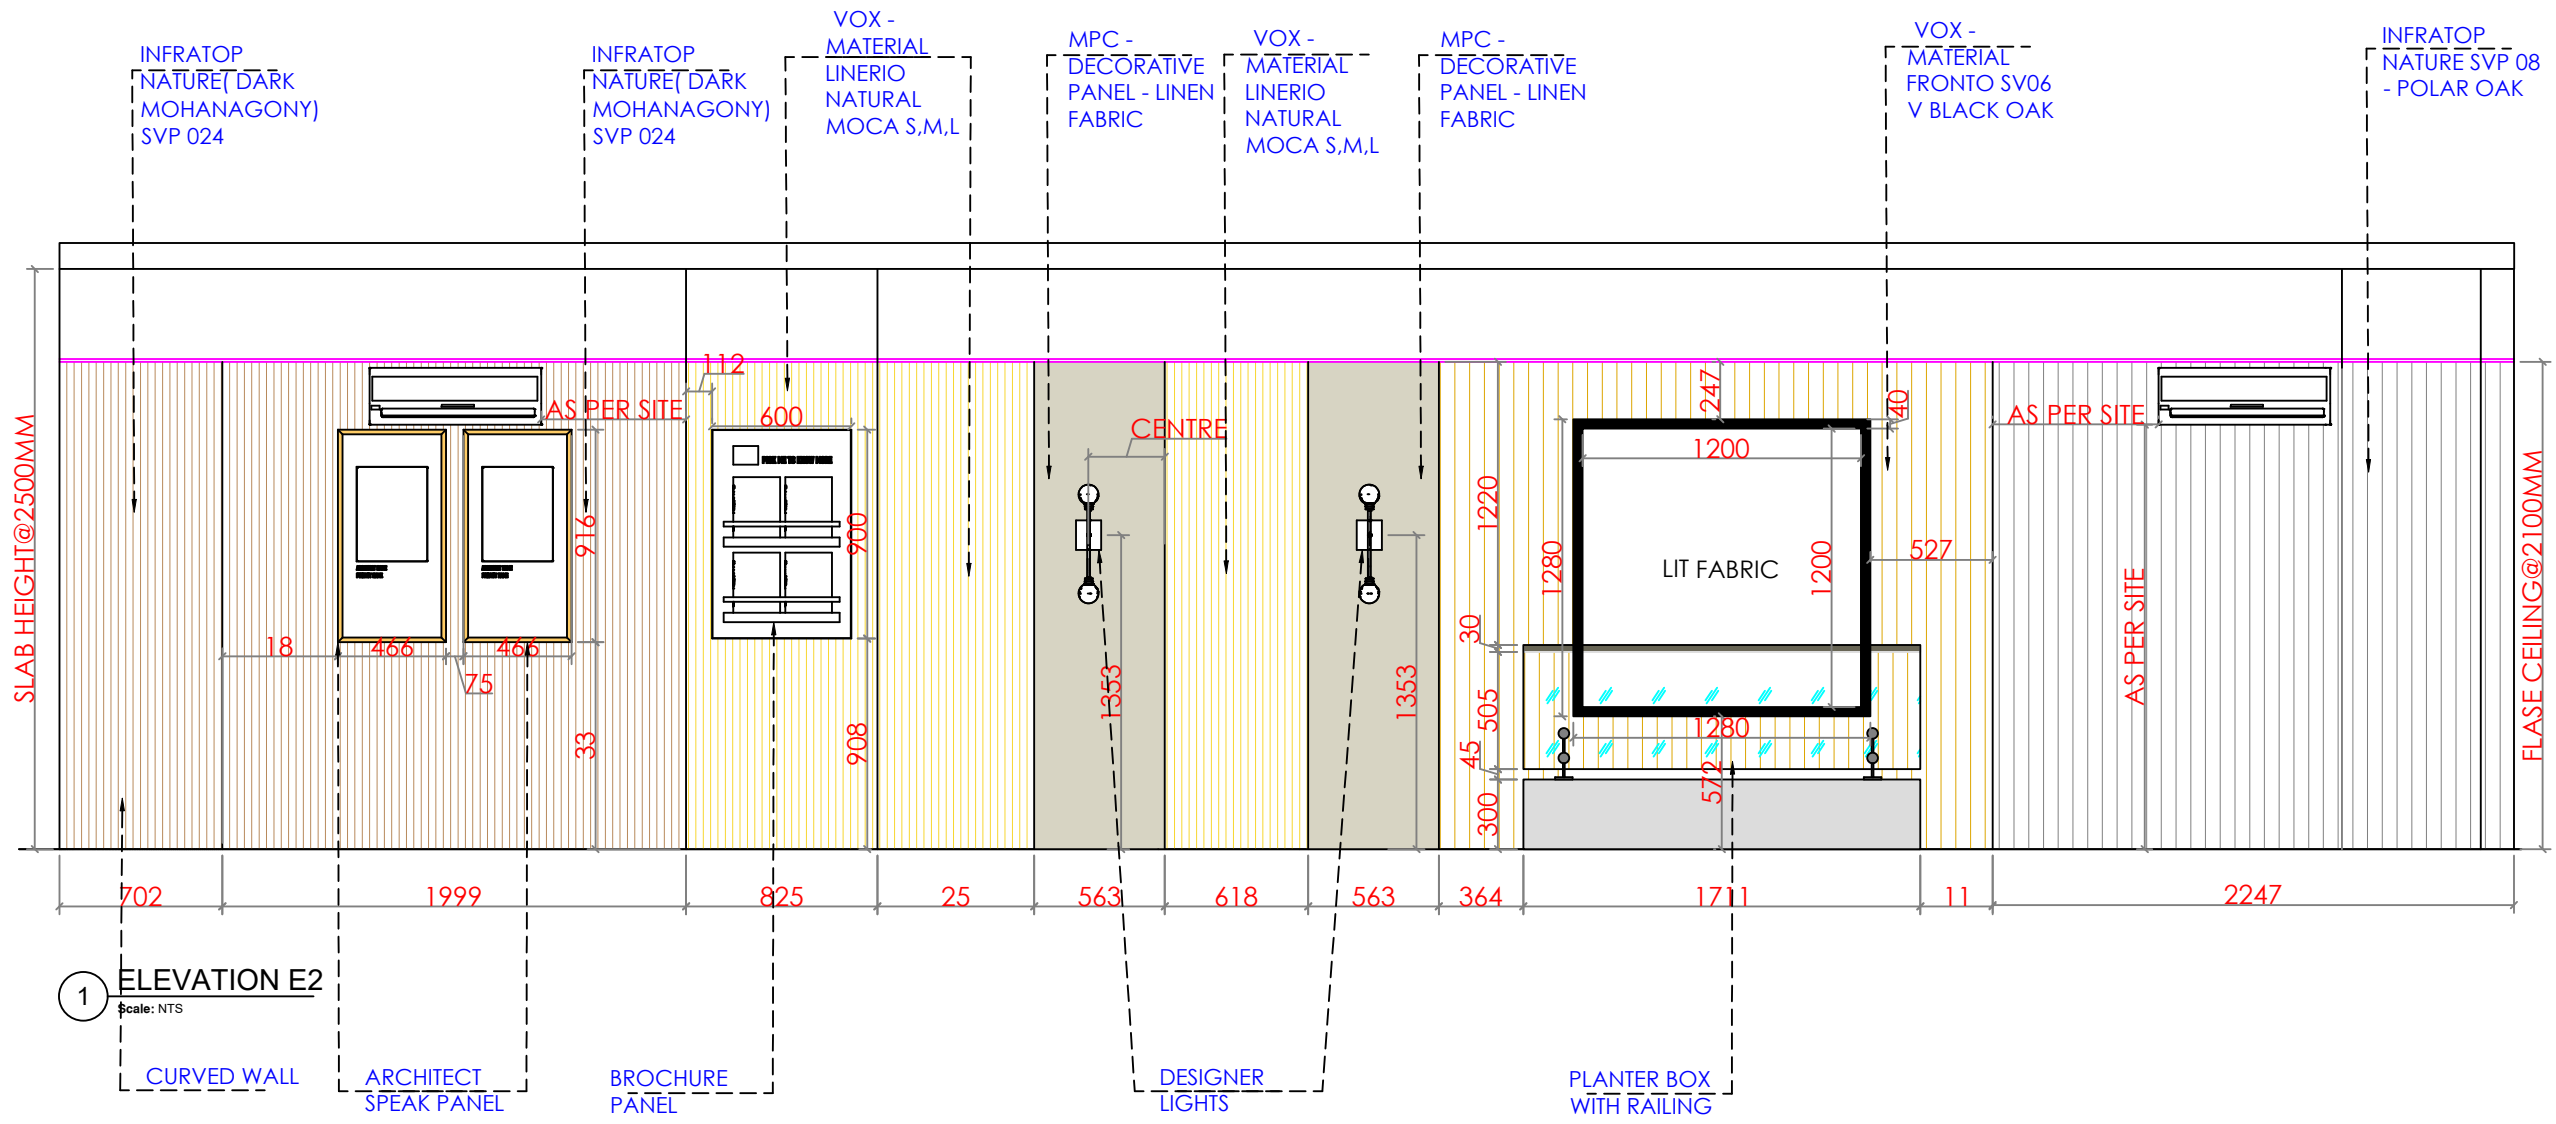

LEGEND :

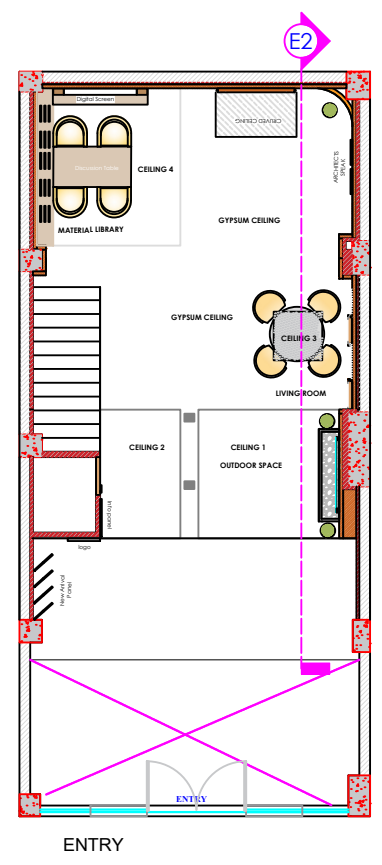

KEY PLAN :

DOMORE
DESIGN PVT LTD

DOMORE DESIGN PVT. LTD.
NO.681, SUKHADA, 2ND FLOOR, 2ND PHASE, 2ND BLOCK,
RAILWAY PARALLEL ROAD,
NEAR MALL OF ASIA, BANGALORE, KARNATAKA, 560097
domoredesign.co.in

GENERAL NOTES


THIS DRAWING IS COPYRIGHT & PROPERTY OF DOMORE DESIGN PVT.LTD. AND IS NOT TO BE REPRODUCED, COPIED OR USED FOR ANY OTHER PURPOSE.
WRITTEN DIMENSIONS TO BE FOLLOWED.
DIMENSIONS TO BE CROSS CHECKED PRIOR TO THE COMMENCEMENT OF WORK.
ALL DRAWINGS TO BE READ IN CONJUNCTION TO THE CONSULTANTS AND VENDORS DRAWINGS/DETAILS.
FOR ALL LEGENDS, SYMBOLS, ABBREVIATIONS AND ANNOTATIONS RELATED QUERIES, REFER TO REFERENCE SHEET.
ANY DISCREPANCY OR DOUBT IN DRAWING TO BE BROUGHT TO THE NOTICE OF DOMORE DESIGN PVT.LTD

SCALE : AS MENTIONED

REVISIONS
R01
R02
R03




PROJECT NAME :

**TURQUOISE
LUXURY REDEFINED,
MUMBAI**

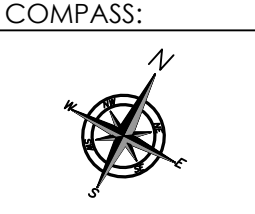


STORE INFO:	
STATE	MAHARASHTRA
CITY	MUMBAI
HIGHSTREET/MALL	TURQUOISE LUXURY REDEFINED
AREA	400 SFT
SLAB BOTTOM: 2500MM	BEAM BOTTOM: 2350 MM


DRAWING NAME:		
ELEVATION 2		
DESIGNED BY:	CHECKED BY:	
RISHAD	AAA	
DATE:	REVISION NO:	DWG NO:
24-8-2026	R0	00

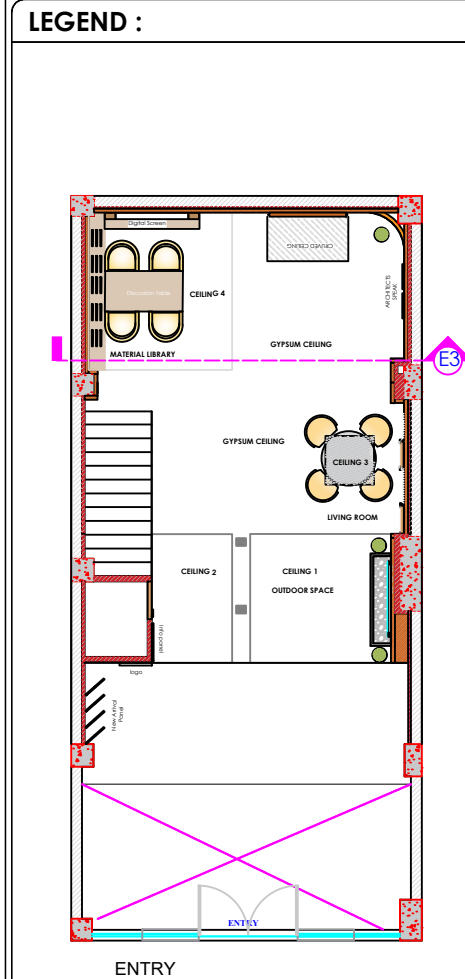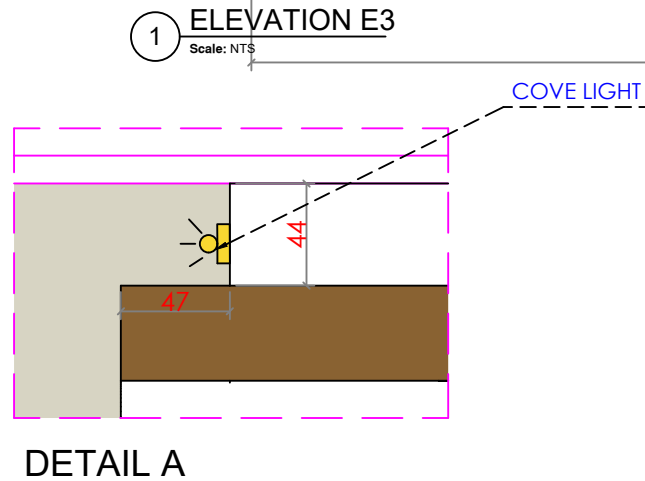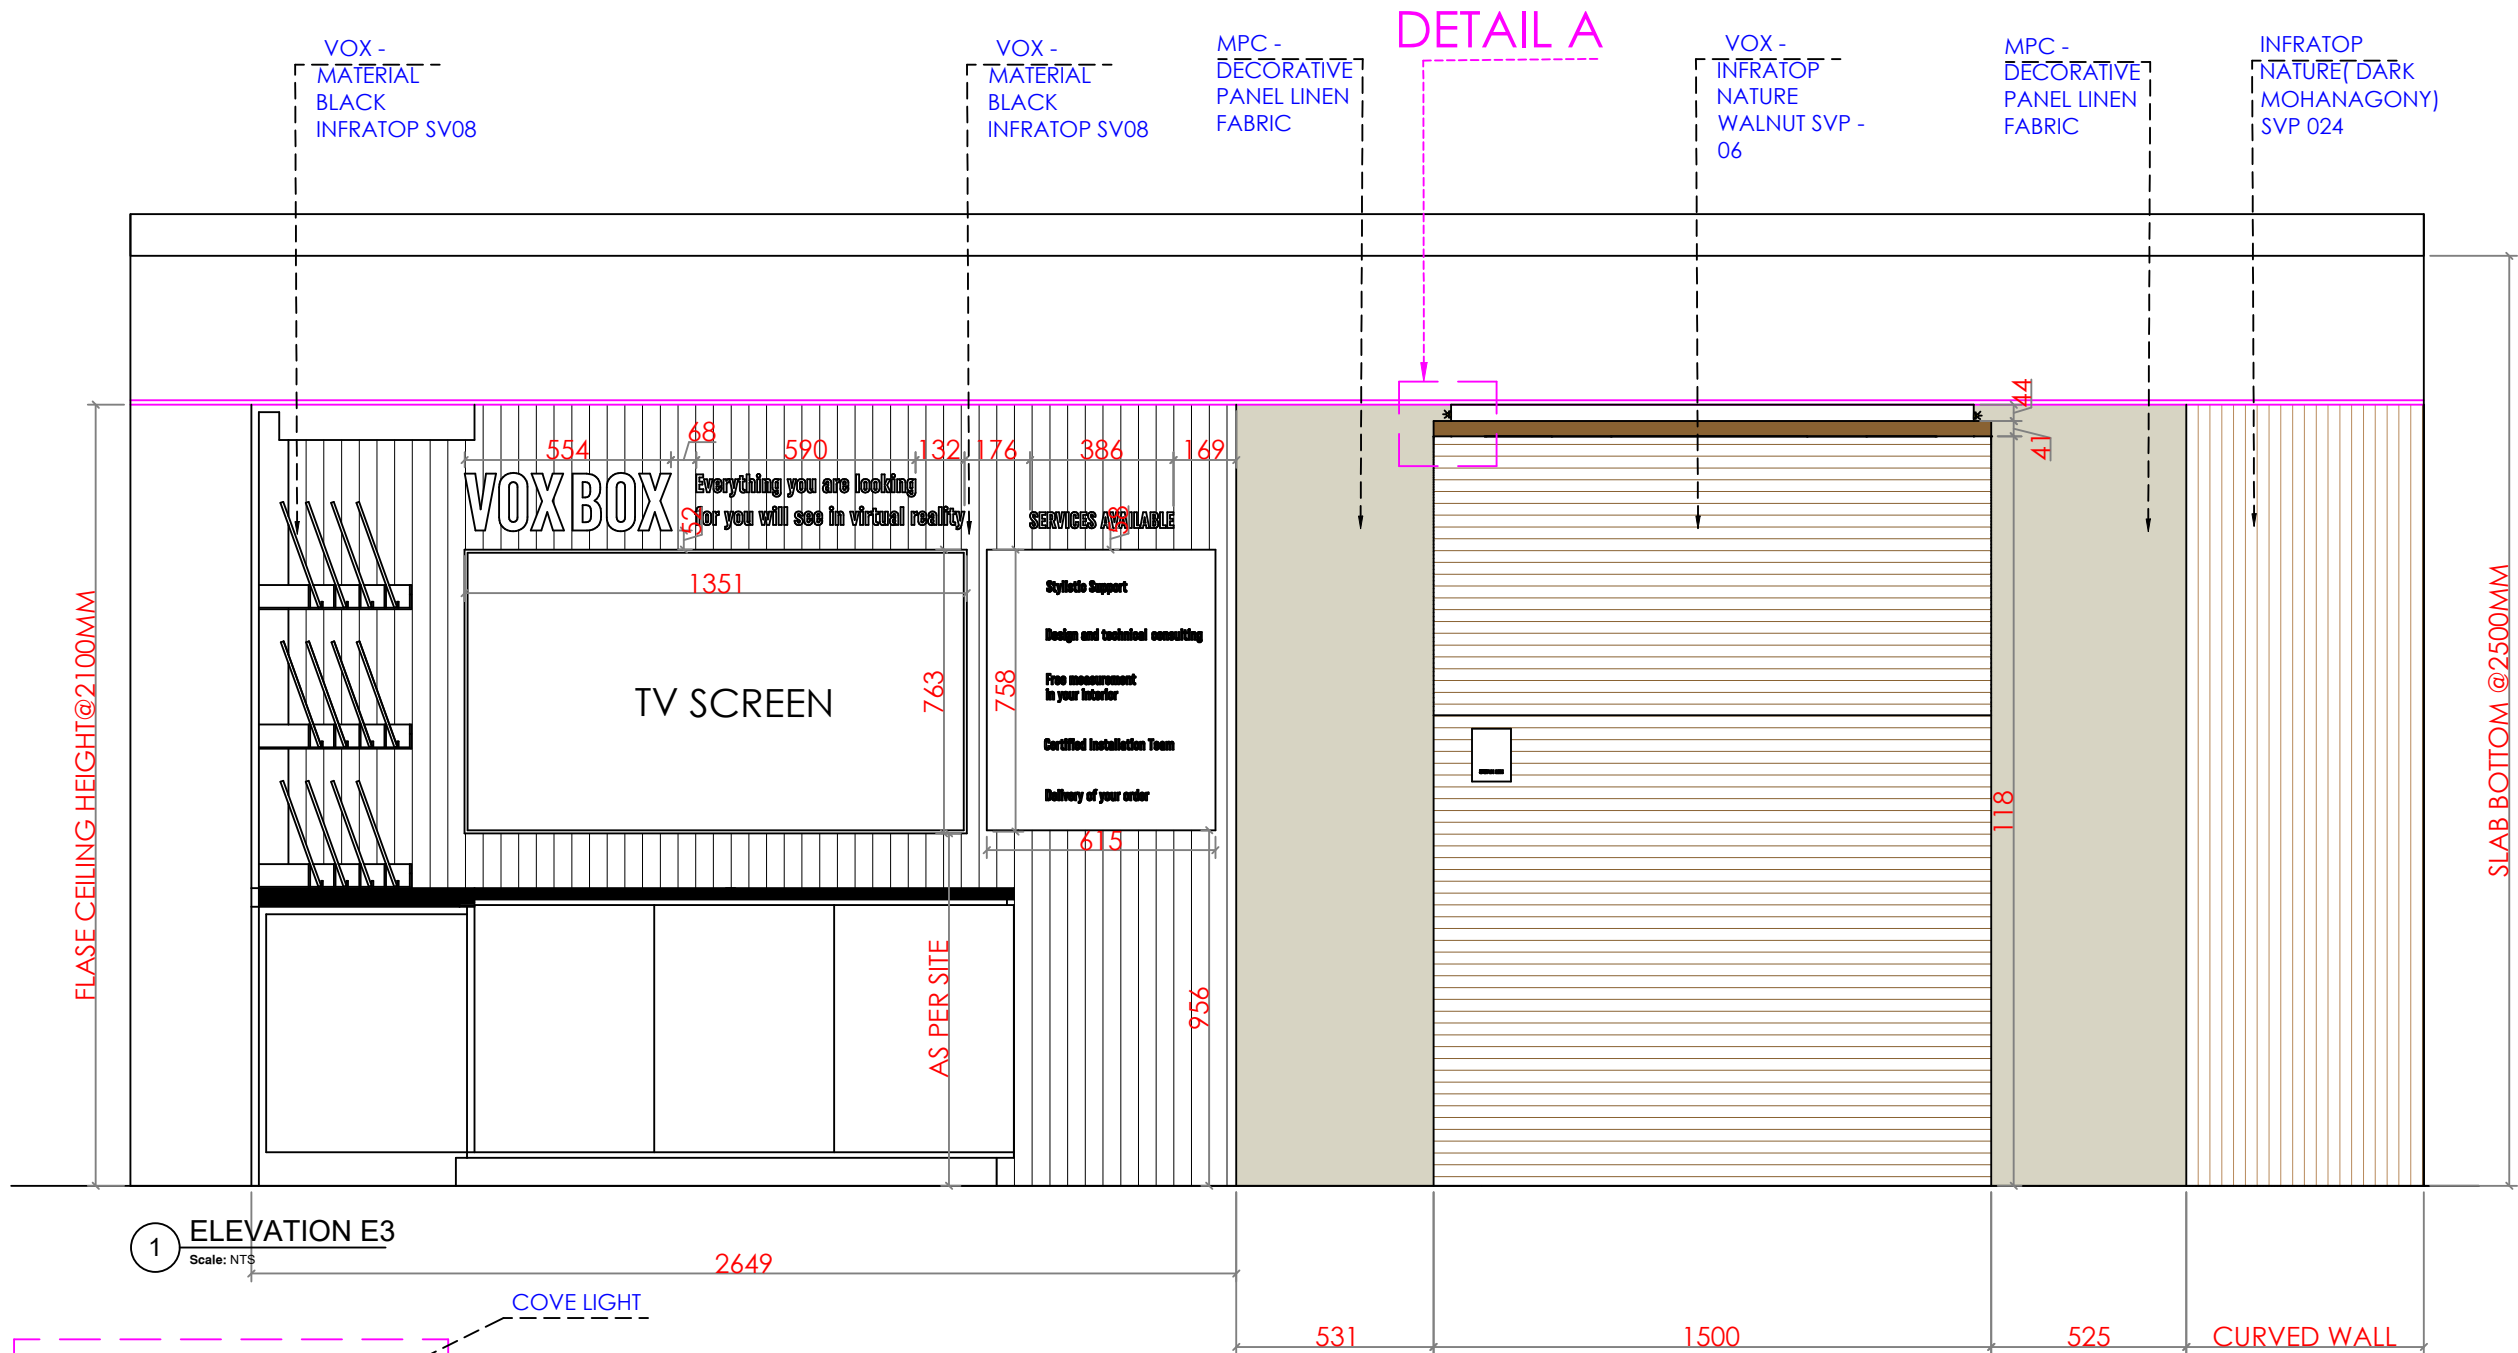

KEY PLAN :

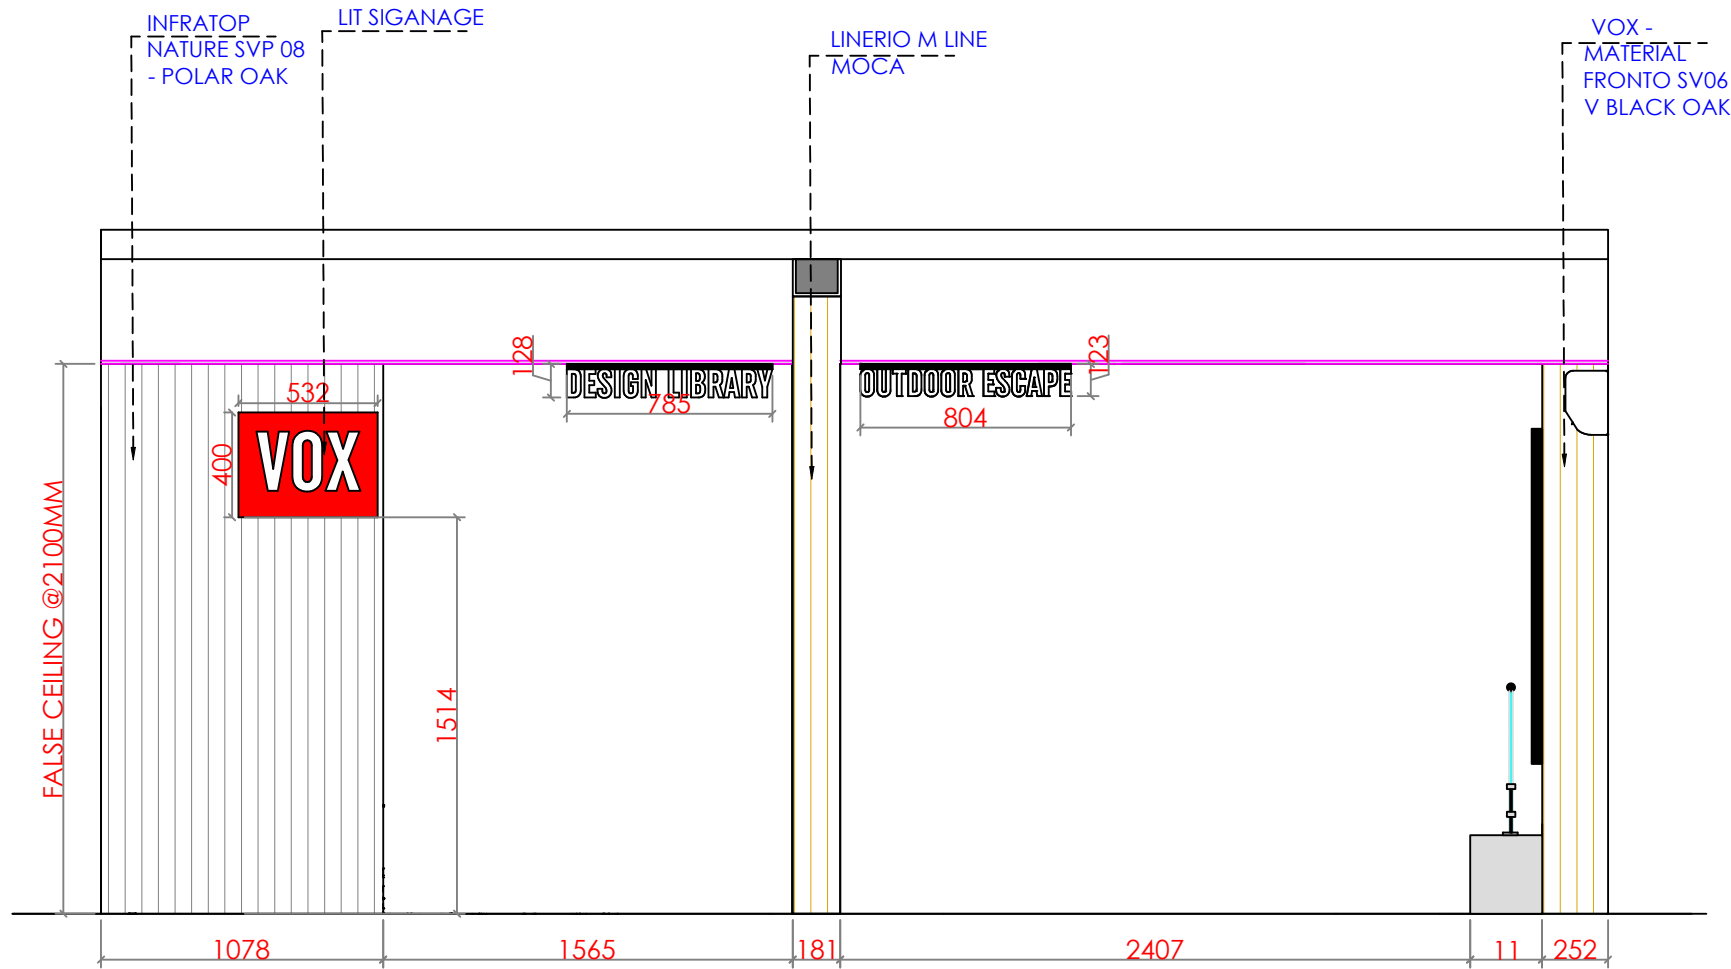


1 ELEVATION E4
Scale: NTS

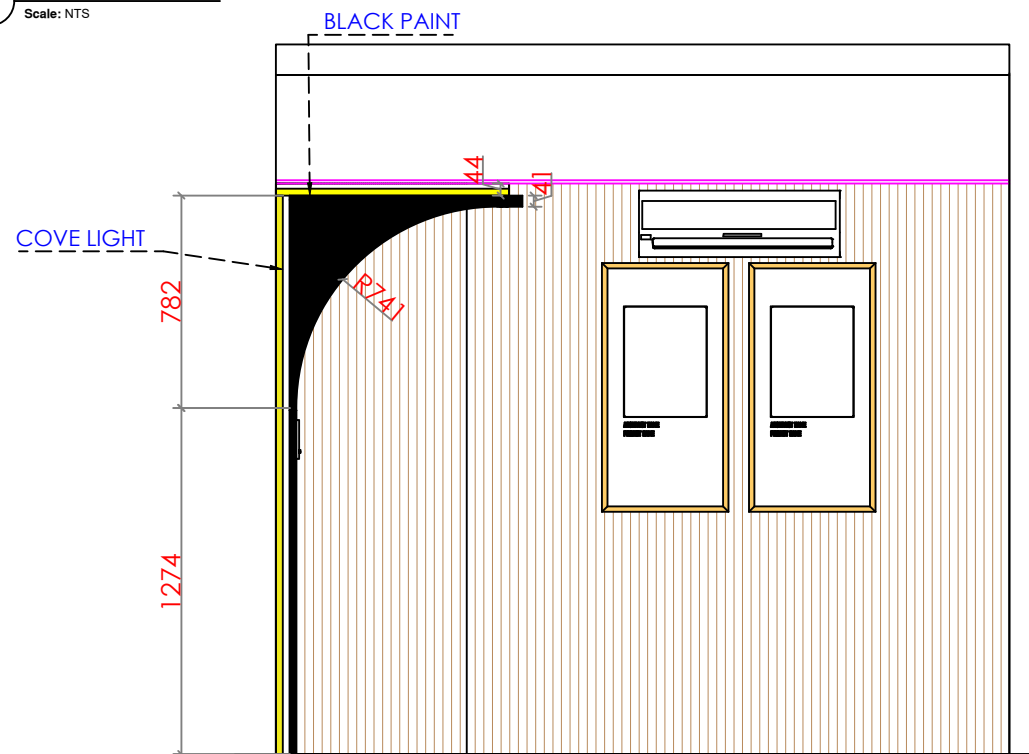

1 ELEVATION E5
Scale: NTS

LEGEND :

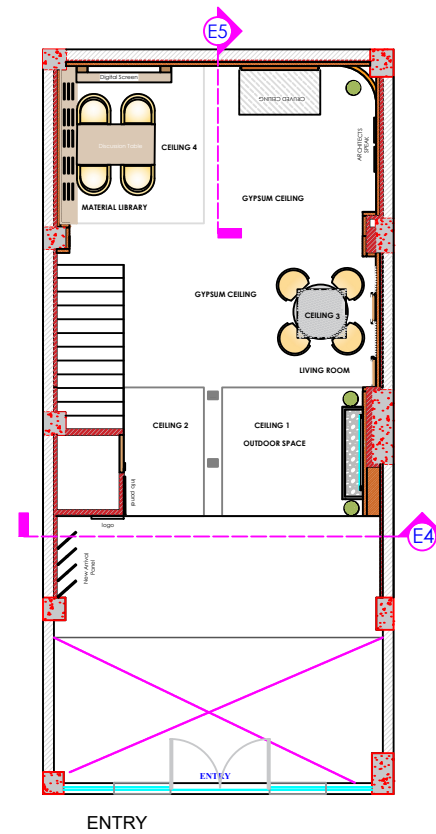

KEY PLAN :

DRAWING NAME:

ELEVATION 4&5

DESIGNED BY:	CHECKED BY:	
RISHAD	AAA	
DATE:	REVISION NO:	DWG NO:
24-8-2026	R0	00



DOMORE DESIGN PVT. LTD.
NO.681, SUKHADA, 2ND FLOOR, 2ND PHASE, 2ND BLOCK,
RAILWAY PARALLEL ROAD,
NEAR MALL OF ASIA, BANGALORE, KARNATAKA, 560097
domoredesign.co.in

GENERAL NOTES

THIS DRAWING IS COPYRIGHT & PROPERTY OF DOMORE DESIGN PVT.LTD. AND IS NOT TO BE REPRODUCED, COPIED OR USED FOR ANY OTHER PURPOSE.
WRITTEN DIMENSIONS TO BE FOLLOWED.
DIMENSIONS TO BE CROSS CHECKED PRIOR TO THE COMMENCEMENT OF WORK.
ALL DRAWINGS TO BE READ IN CONJUNCTION TO THE CONSULTANTS AND VENDORS DRAWINGS/DETAILS.
FOR ALL LEGENDS, SYMBOLS, ABBREVIATIONS AND ANNOTATIONS RELATED QUERIES, REFER TO REFERENCE SHEET.
ANY DISCREPANCY OR DOUBT IN DRAWING TO BE BROUGHT TO THE NOTICE OF DOMORE DESIGN PVT.LTD

SCALE : AS MENTIONED

REVISIONS

R01
R02
R03

PROJECT NAME :

TURQUOISE
LUXURY REDEFINED,
MUMBAI

COMPASS:



STORE INFO:

STATE	MAHARASHTRA
CITY	MUMBAI
HIGHSTREET/MALL	TURQUOISE LUXURY REDEFINED
AREA	400 SFT
SLAB BOTTOM: 2500MM	BEAM BOTTOM: 2350 MM