

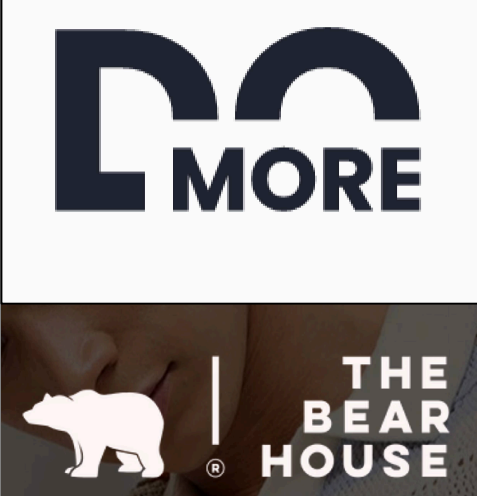


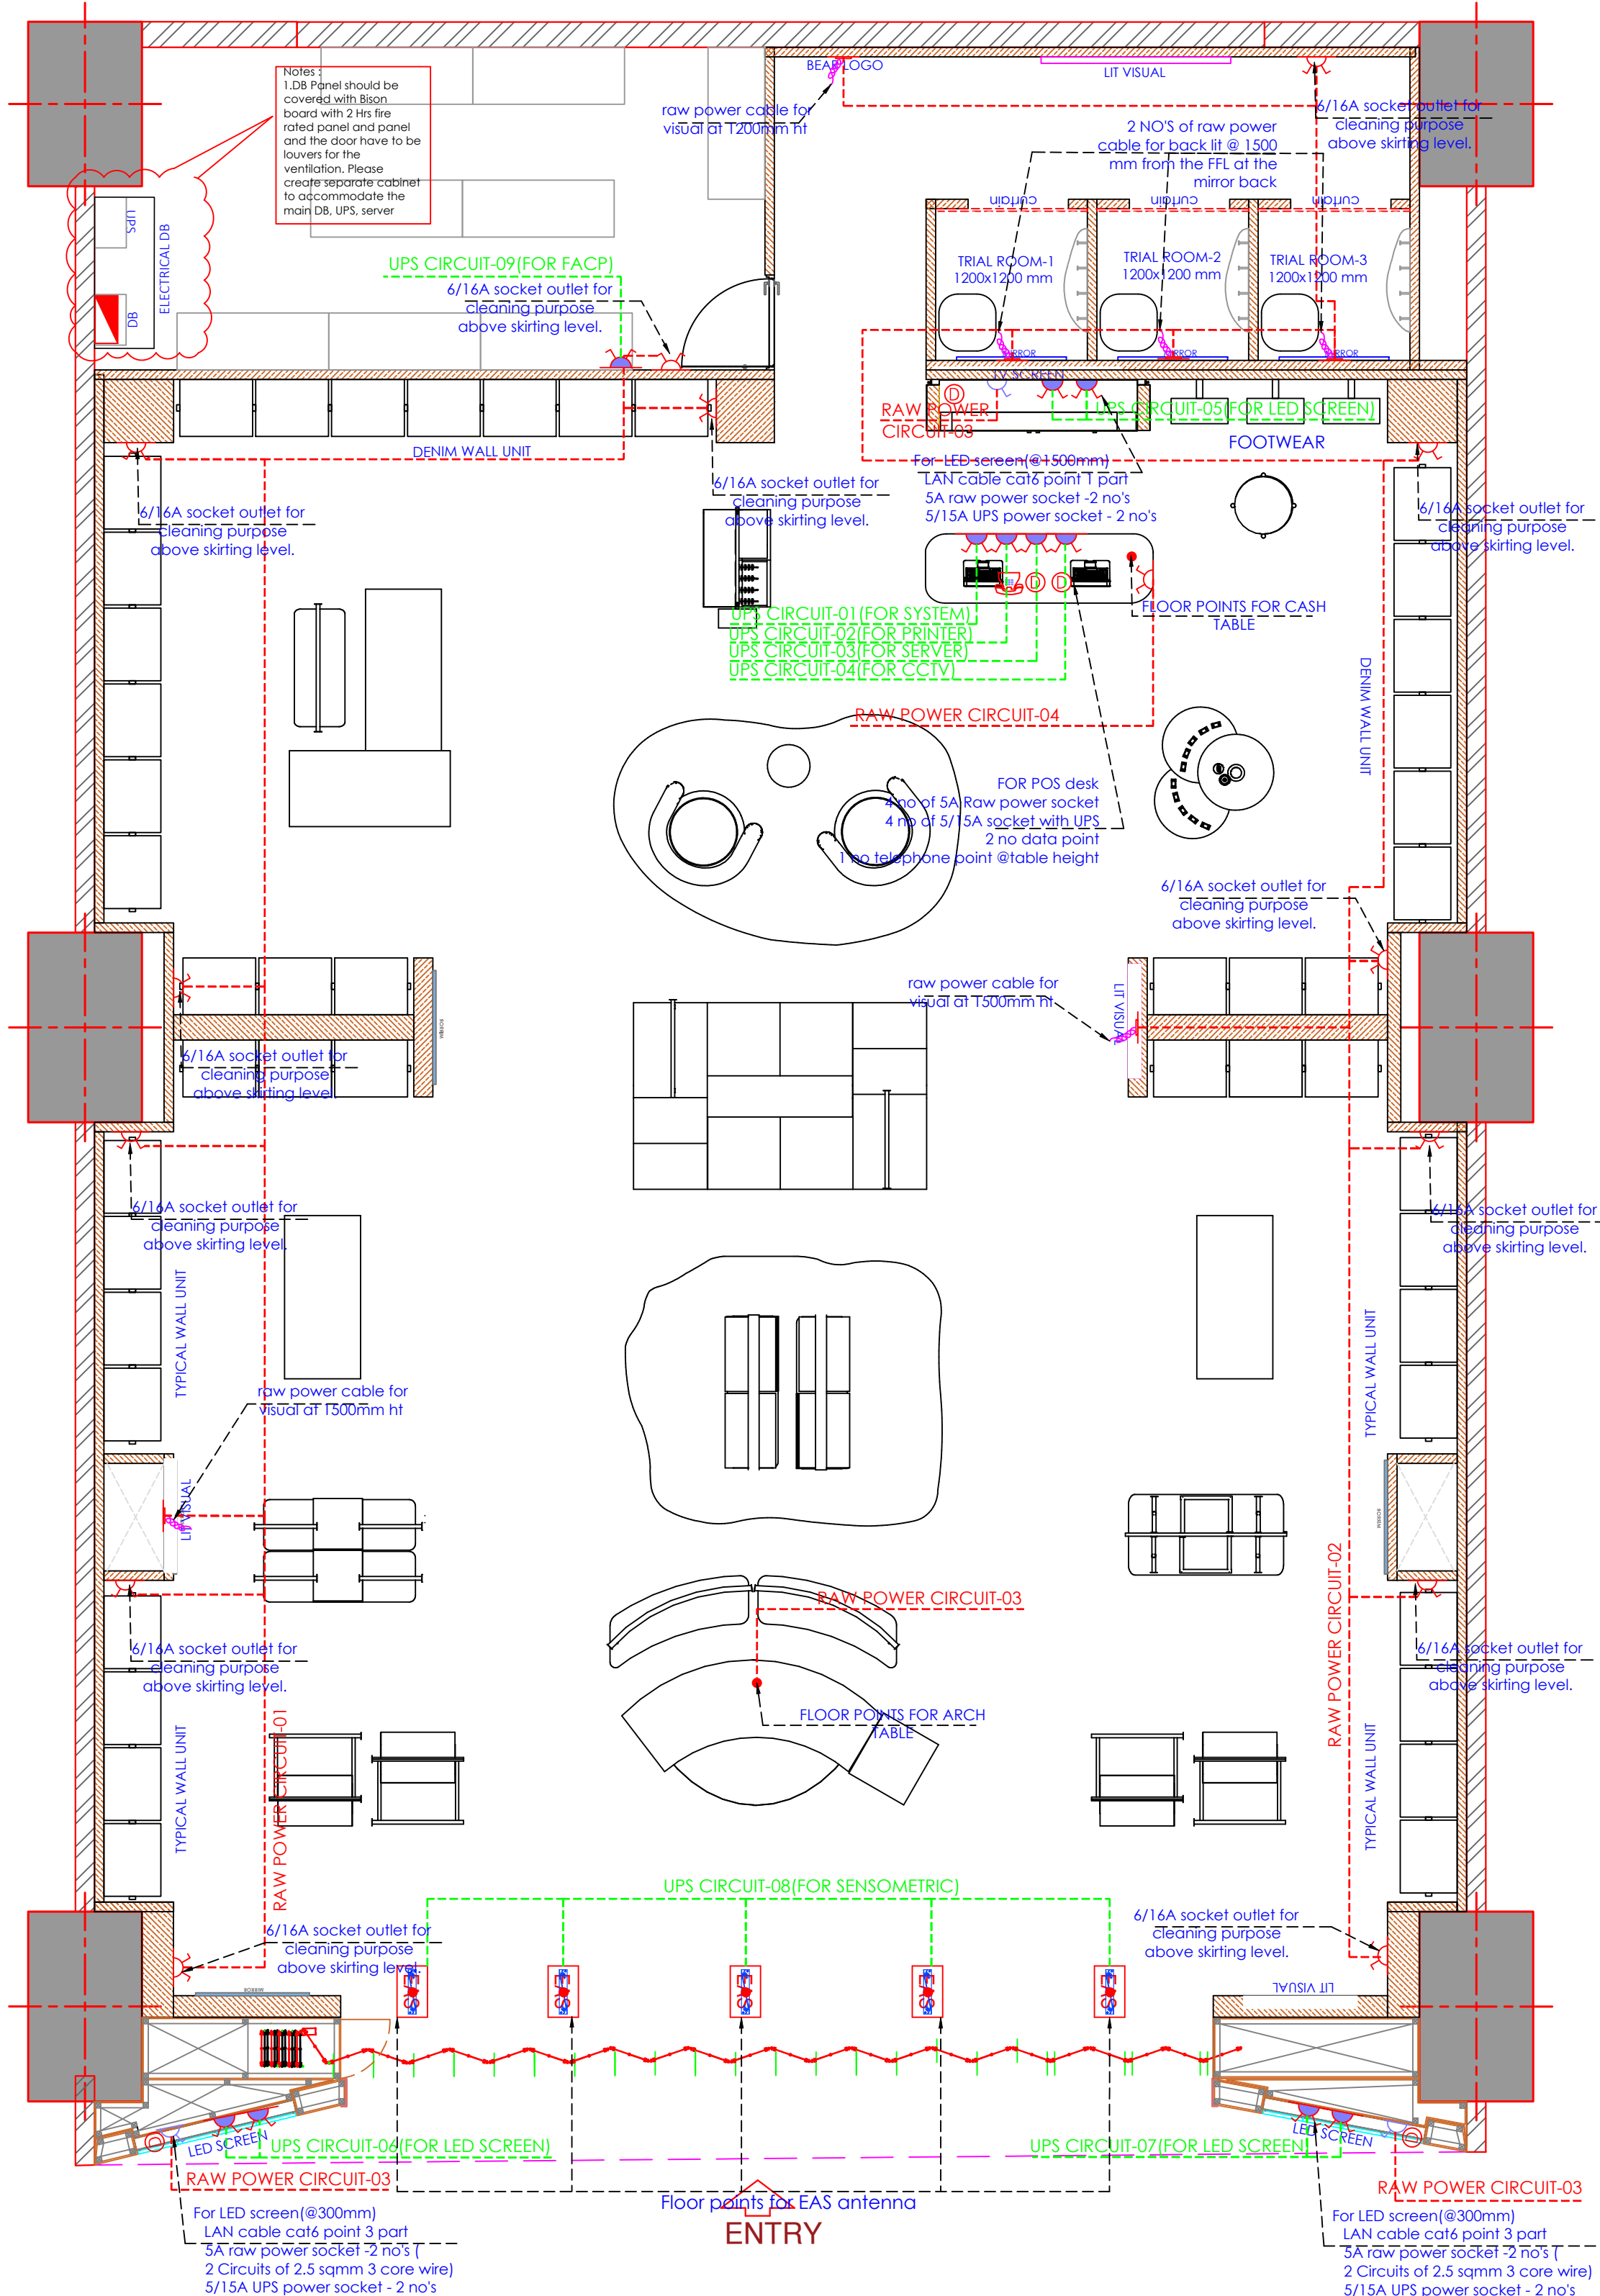



PACIFIC MALL - JAIPUR

Shop info	
Market	INDIA
Province	RAJASTHAN
City	JAIPUR
City tier (tier 1/2/3)	TIER 2
Mall Name	PACIFIC MALL
New /Reno /Relo	NEW
STORE / SIS	STORE
Shop concept	THE BEAR HOUSE
Net size	1916 SQ FT
Slab height	5252 MM
B.O.B height	3769 MM

Drawing info	
Title	POWER LAYOUT
Designed by	RISHAD
Checked by	
Date	28.04.2026
Revision	
Dwg no.	

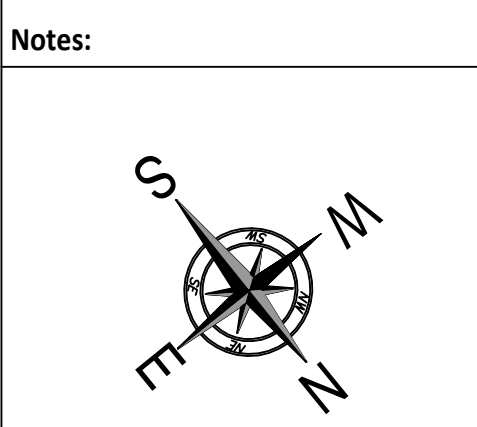

LEGEND : POWERPOINT		
SINO	SYMBOL	DESCRIPTION
1		6A SOCKET WITH SWITCH (RAW)
2		6/16A SOCKET WITH SWITCH (RAW)
3		6A SOCKET WITH SWITCH (UPS)
4		6/16A SOCKET WITH SWITCH (UPS)
5		DISTRIBUTION BOARD
6		WIFI OUTLET
7		VOICE POINT
8		DATA POINT
9		ROLLING SHUTTER POWER POINT
10		POINT FOR SIGNAGE
11		CEILING POINT FOR PROJECTOR (6/16A POWER SOCKET ON UPS)
12		RAW POWER POINTS
12		WALL MOUNTED POINT FOR FOOTFALL DEVICE
12		SENSORMATIC MACHINE

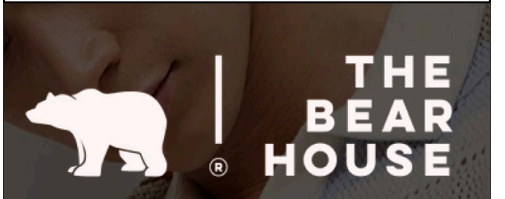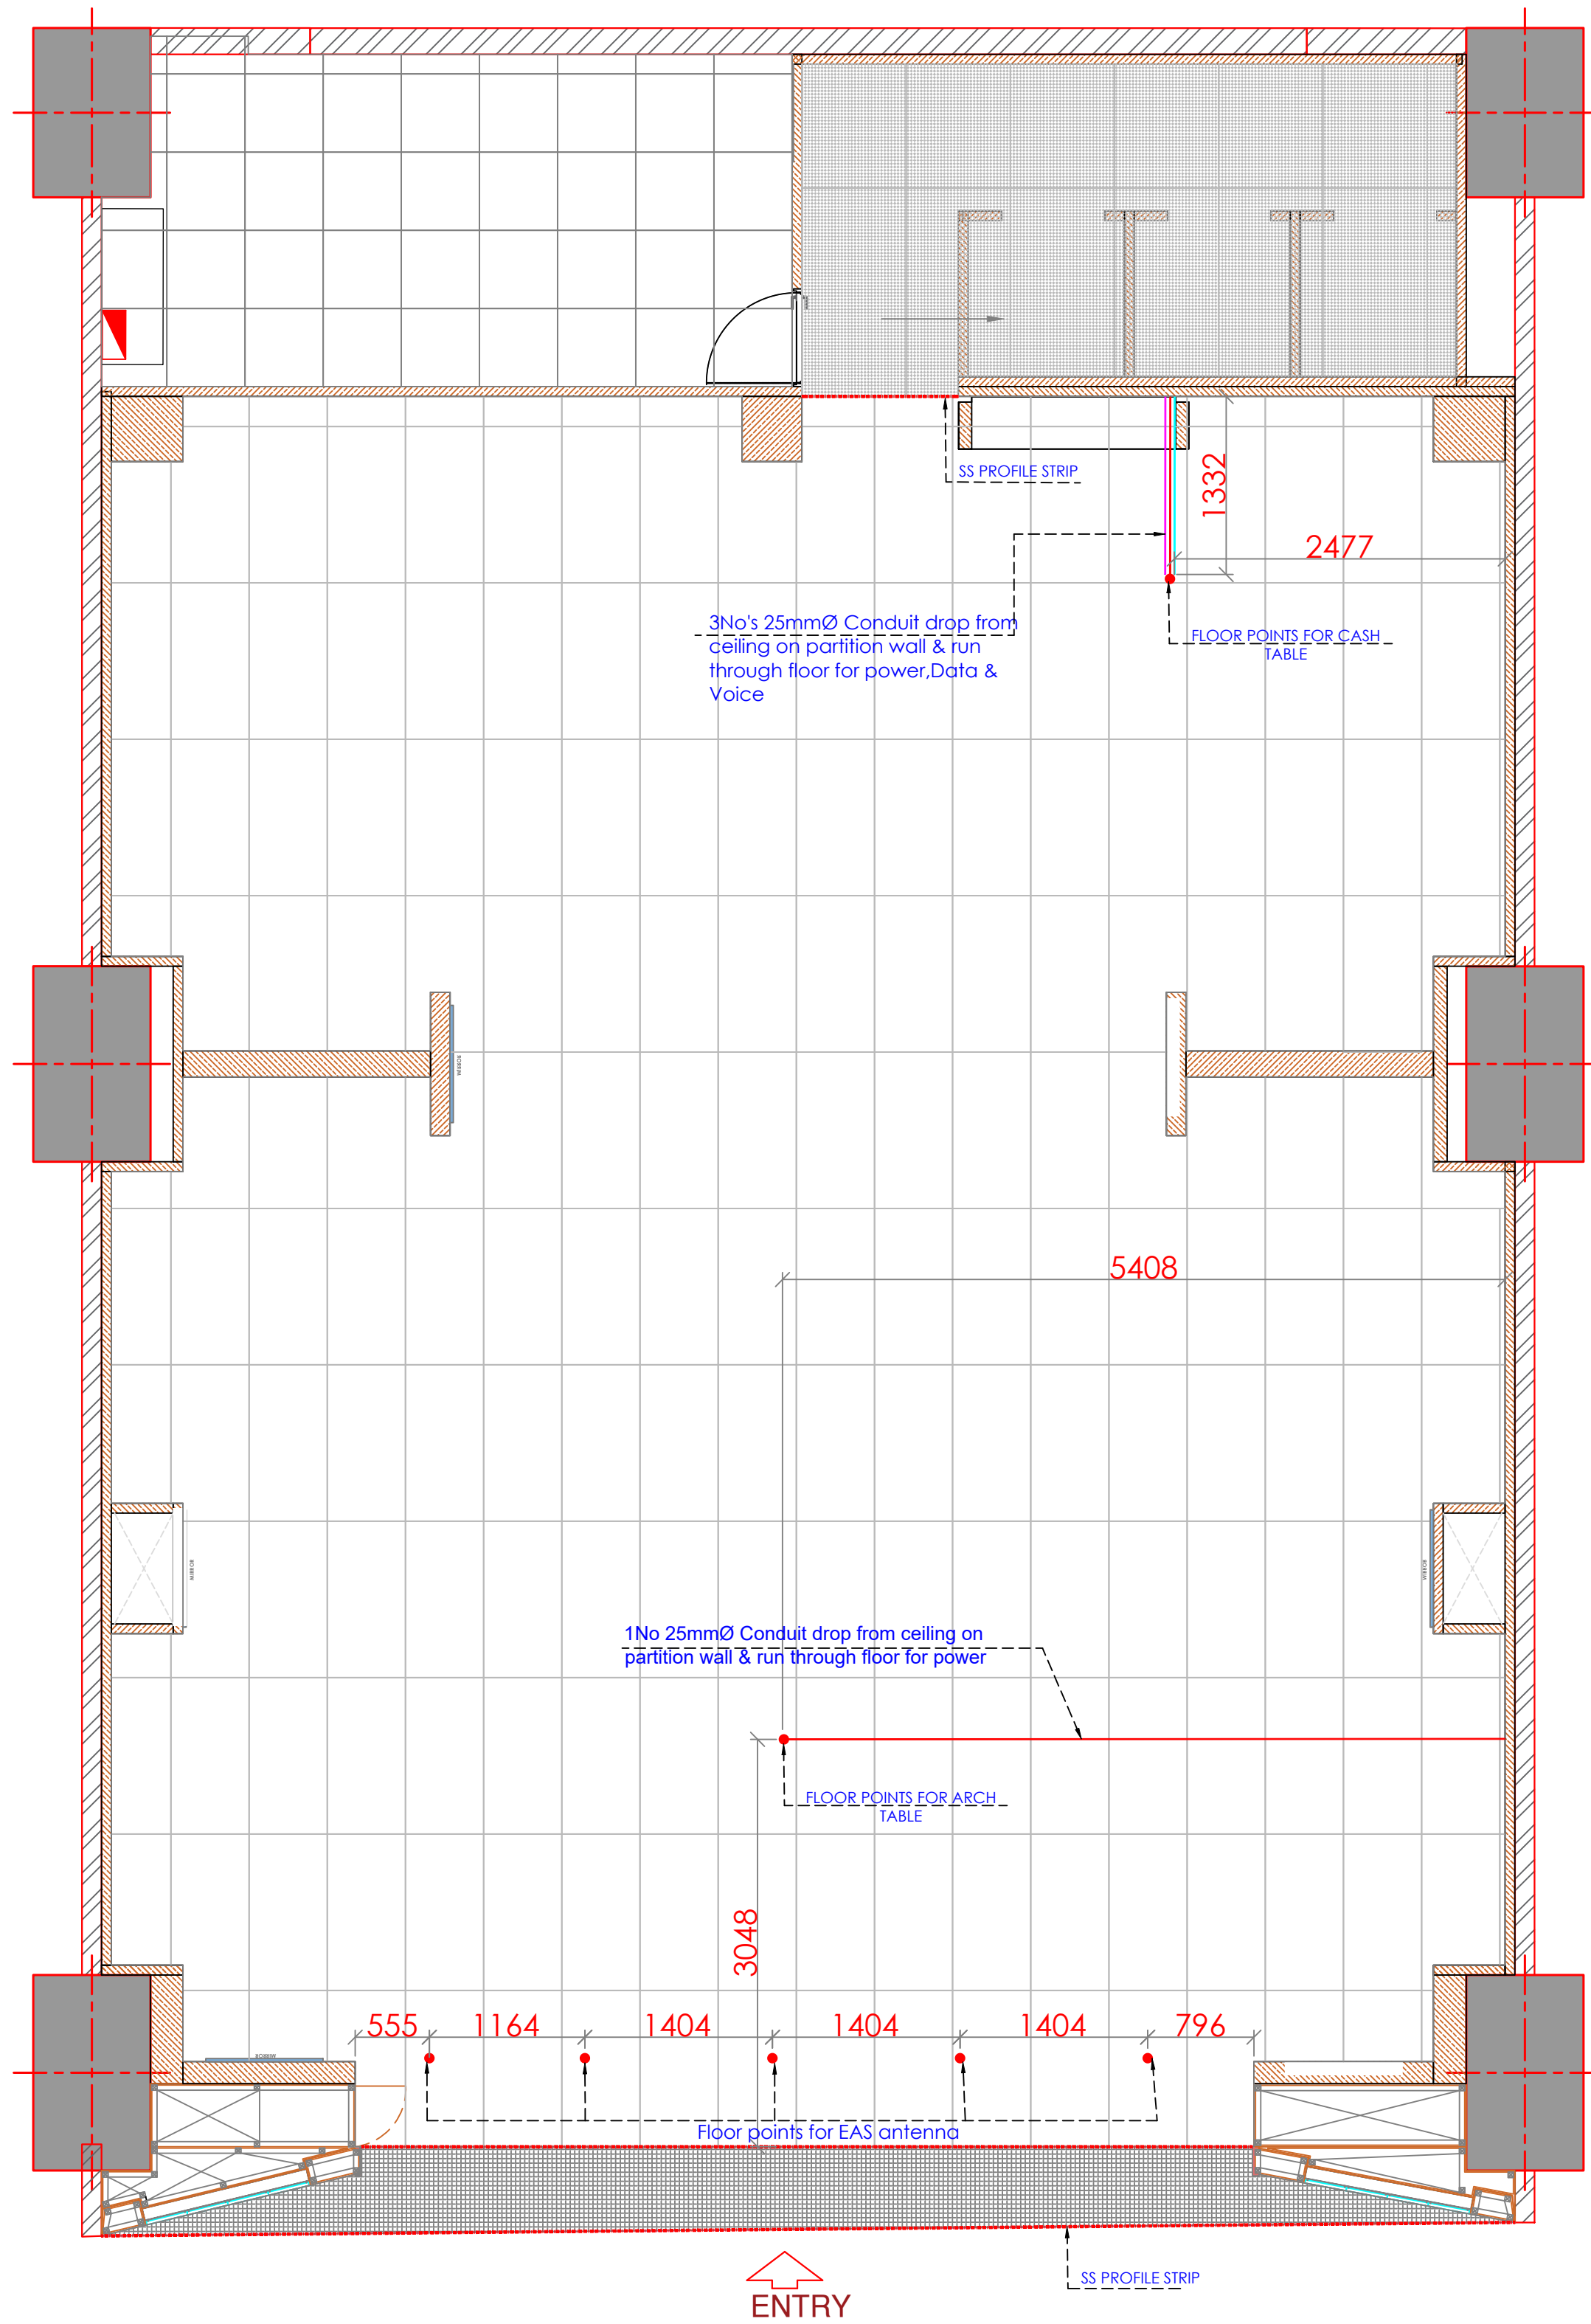

PACIFIC MALL - JAIPUR


Shop info

Market	INDIA
Province	RAJASTHAN
City	JAIPUR
City tier (tier 1/2/3)	TIER 2
Mall Name	PACIFIC MALL
New /Reno /Relo	NEW
STORE / SIS	STORE
Shop concept	THE BEAR HOUSE
Net size	1916 SQ FT
Slab height	5252 MM
B.O.B height	3769 MM


Drawing info

Title	FLOOR POWER POINT LAYOUT
Designed by	RISHAD
Checked by	
Date	28.04.2026
Revision	
Dwg no.	

Notes:

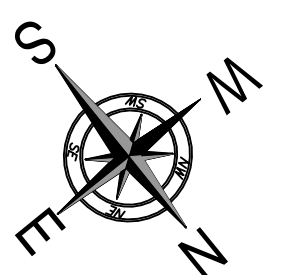


S.NO	SYMBOL	DESCRIPTION
1	●	FLOOR CONDUIT POINTS

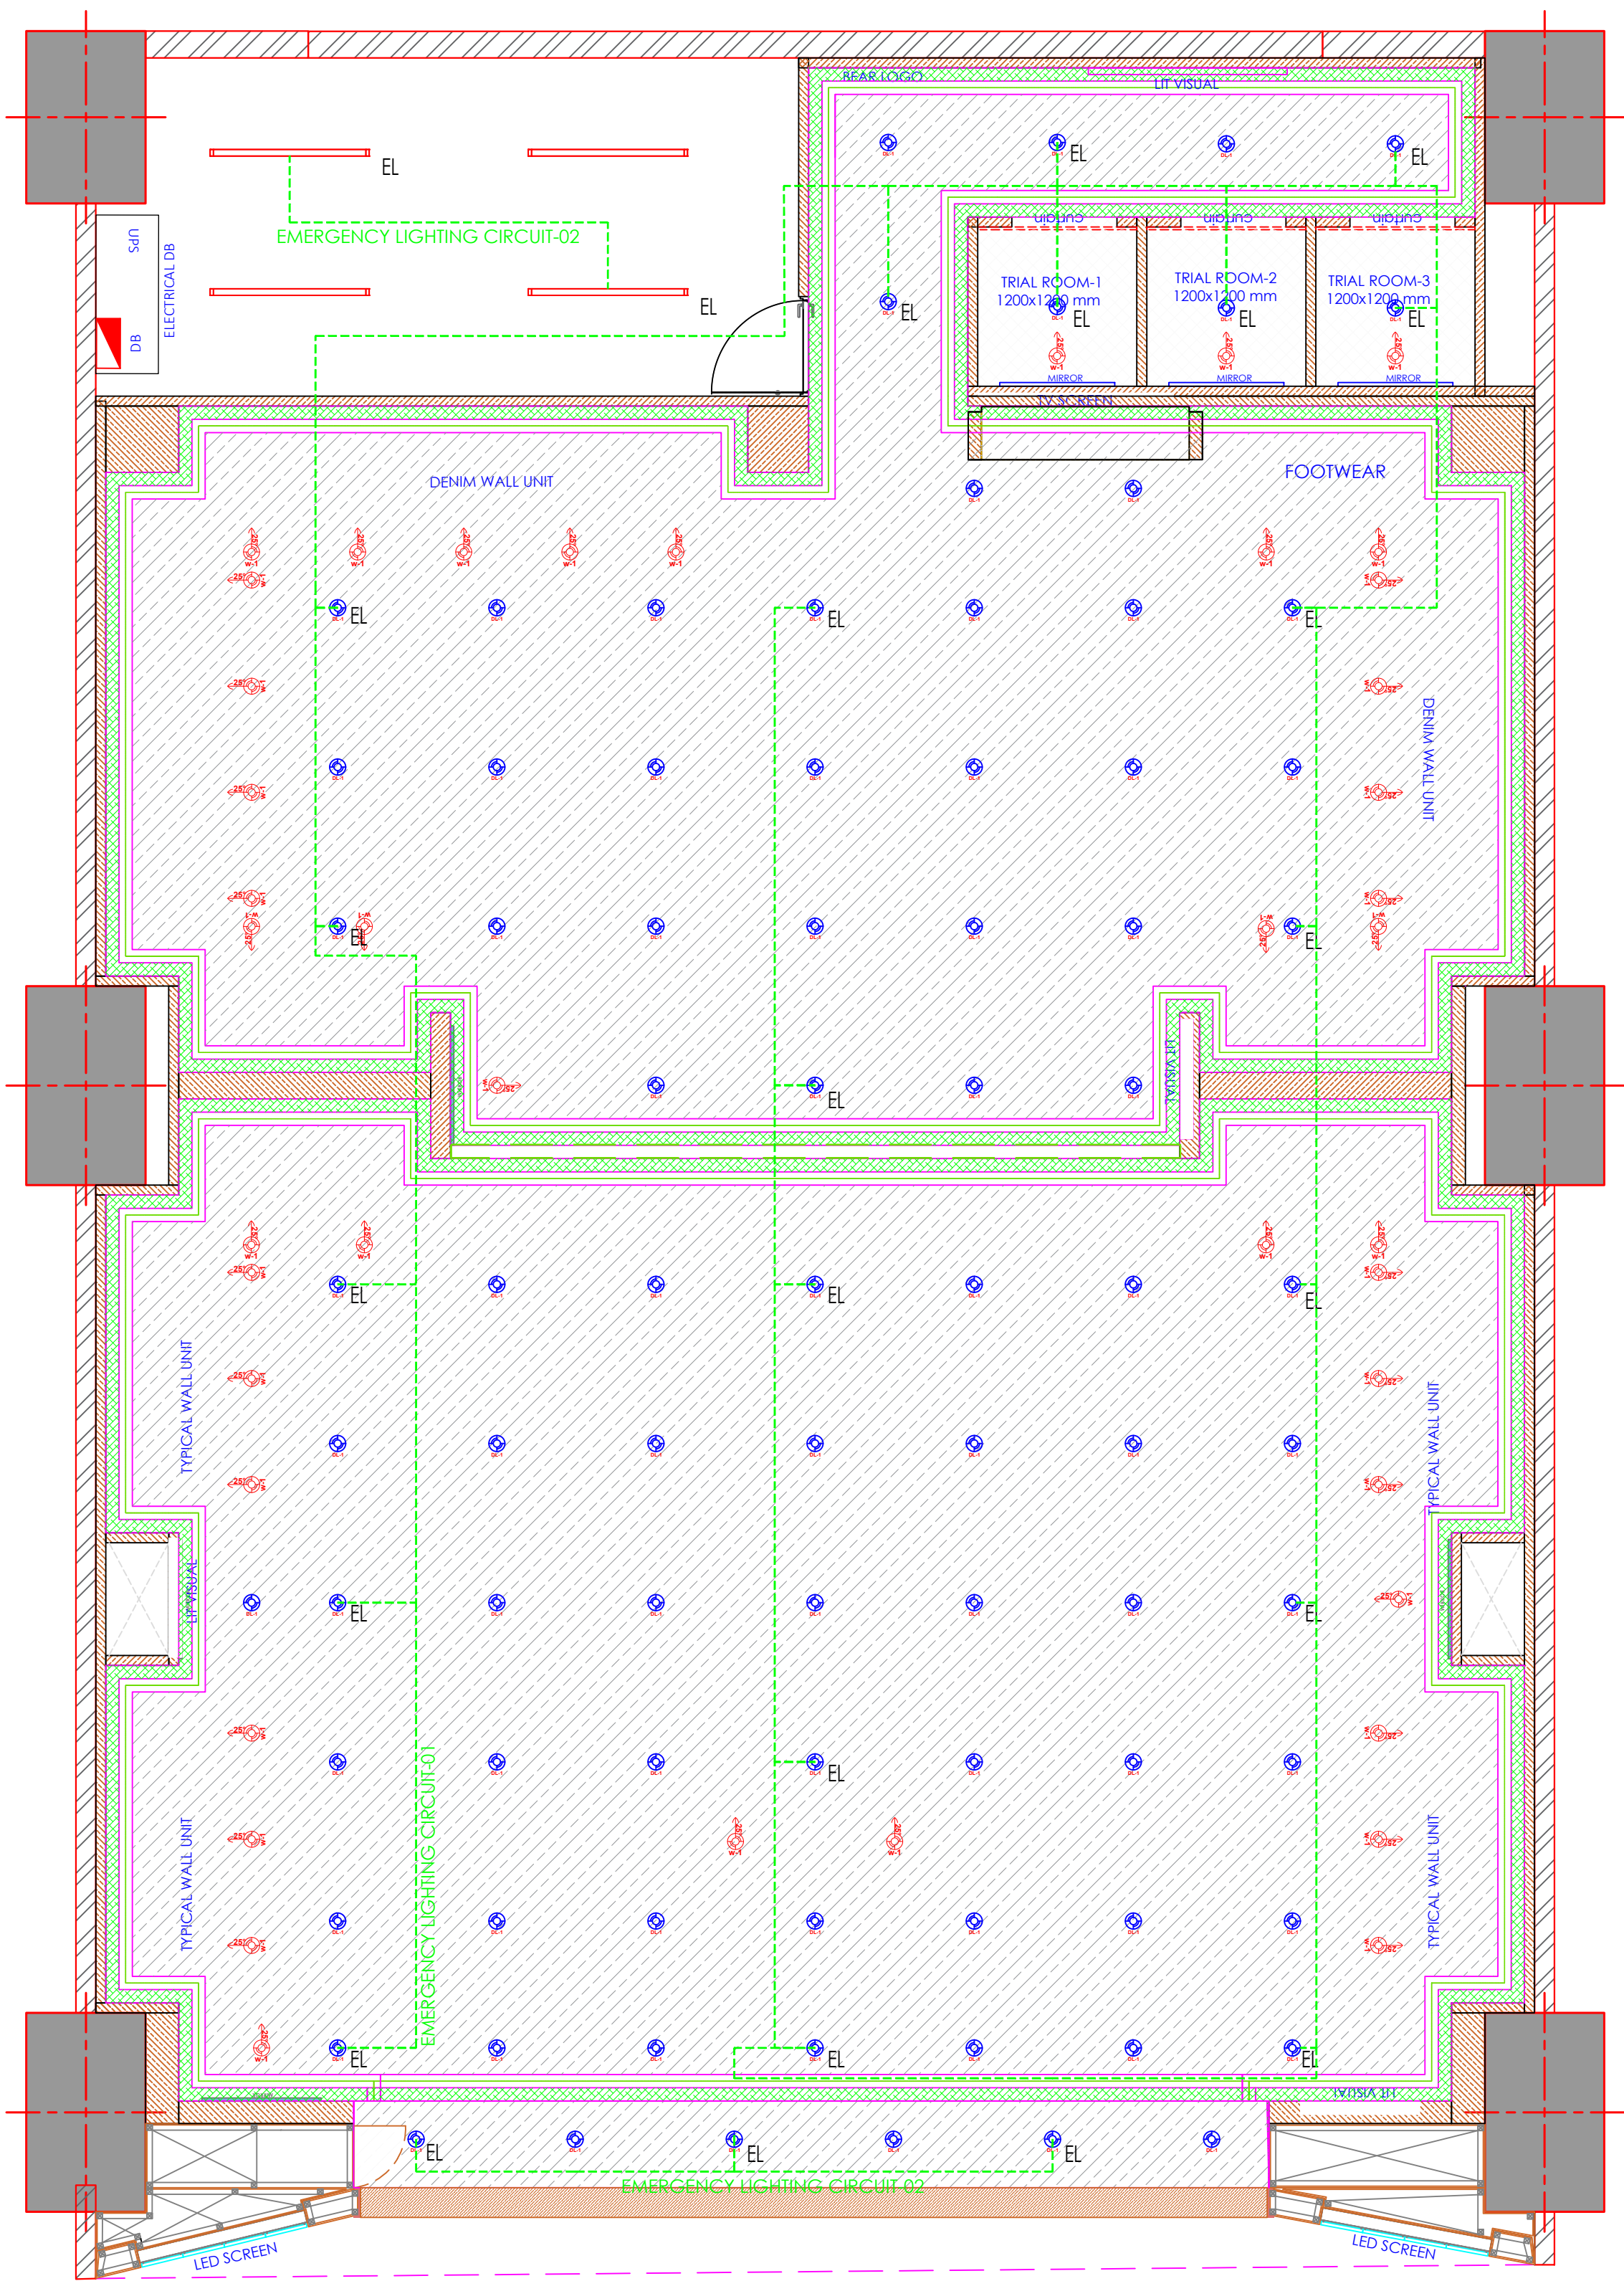

Notes:
1. Lighting & emergency points to keep in UPS for 30 mins backup.

TBH - Pacific mall, Jaipur - Lighting BOQ


S. NO.	SYB	PRODUCT DESCRIPTION	QTY
01		BOOM S 35W 40D RECESS MOUNTED LED WALL WASHER 4000K WHITE	43
02		XTRA M 35W 45D RECESS MOUNTED LED WALL WASHER 4000K WHITE	84
03		NEON STRIP 18W/MT. FLEXIBLE STRIP FOR COVELIGHT 4000K (IN MT.)	60MT
04		SPAN 20W SURFACE MOUNT LED TUBE LIGHT - 4FT 4000K WHITE	04

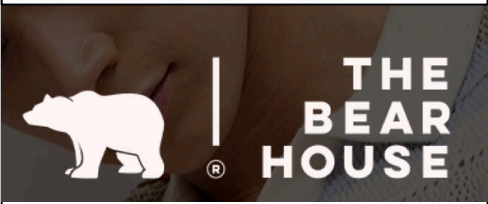


PACIFIC MALL
-
JAIPUR

Shop info	
Market	INDIA
Province	RAJASTHAN
City	JAIPUR
City tier (tier 1/2/3)	TIER 2
Mall Name	PACIFIC MALL
New /Reno /Relo	NEW
STORE / SIS	STORE
Shop concept	THE BEAR HOUSE
Net size	1916 SQ FT
Slab height	5252 MM
B.O.B height	3769 MM

Drawing info	
Title	LIGHTING LAYOUT
Designed by	RISHAD
Checked by	
Date	28.04.2026
Revision	
Dwg no.	

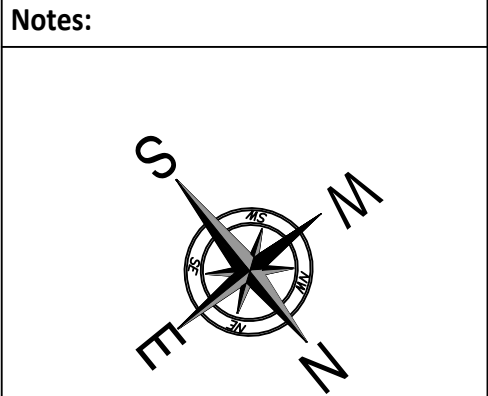


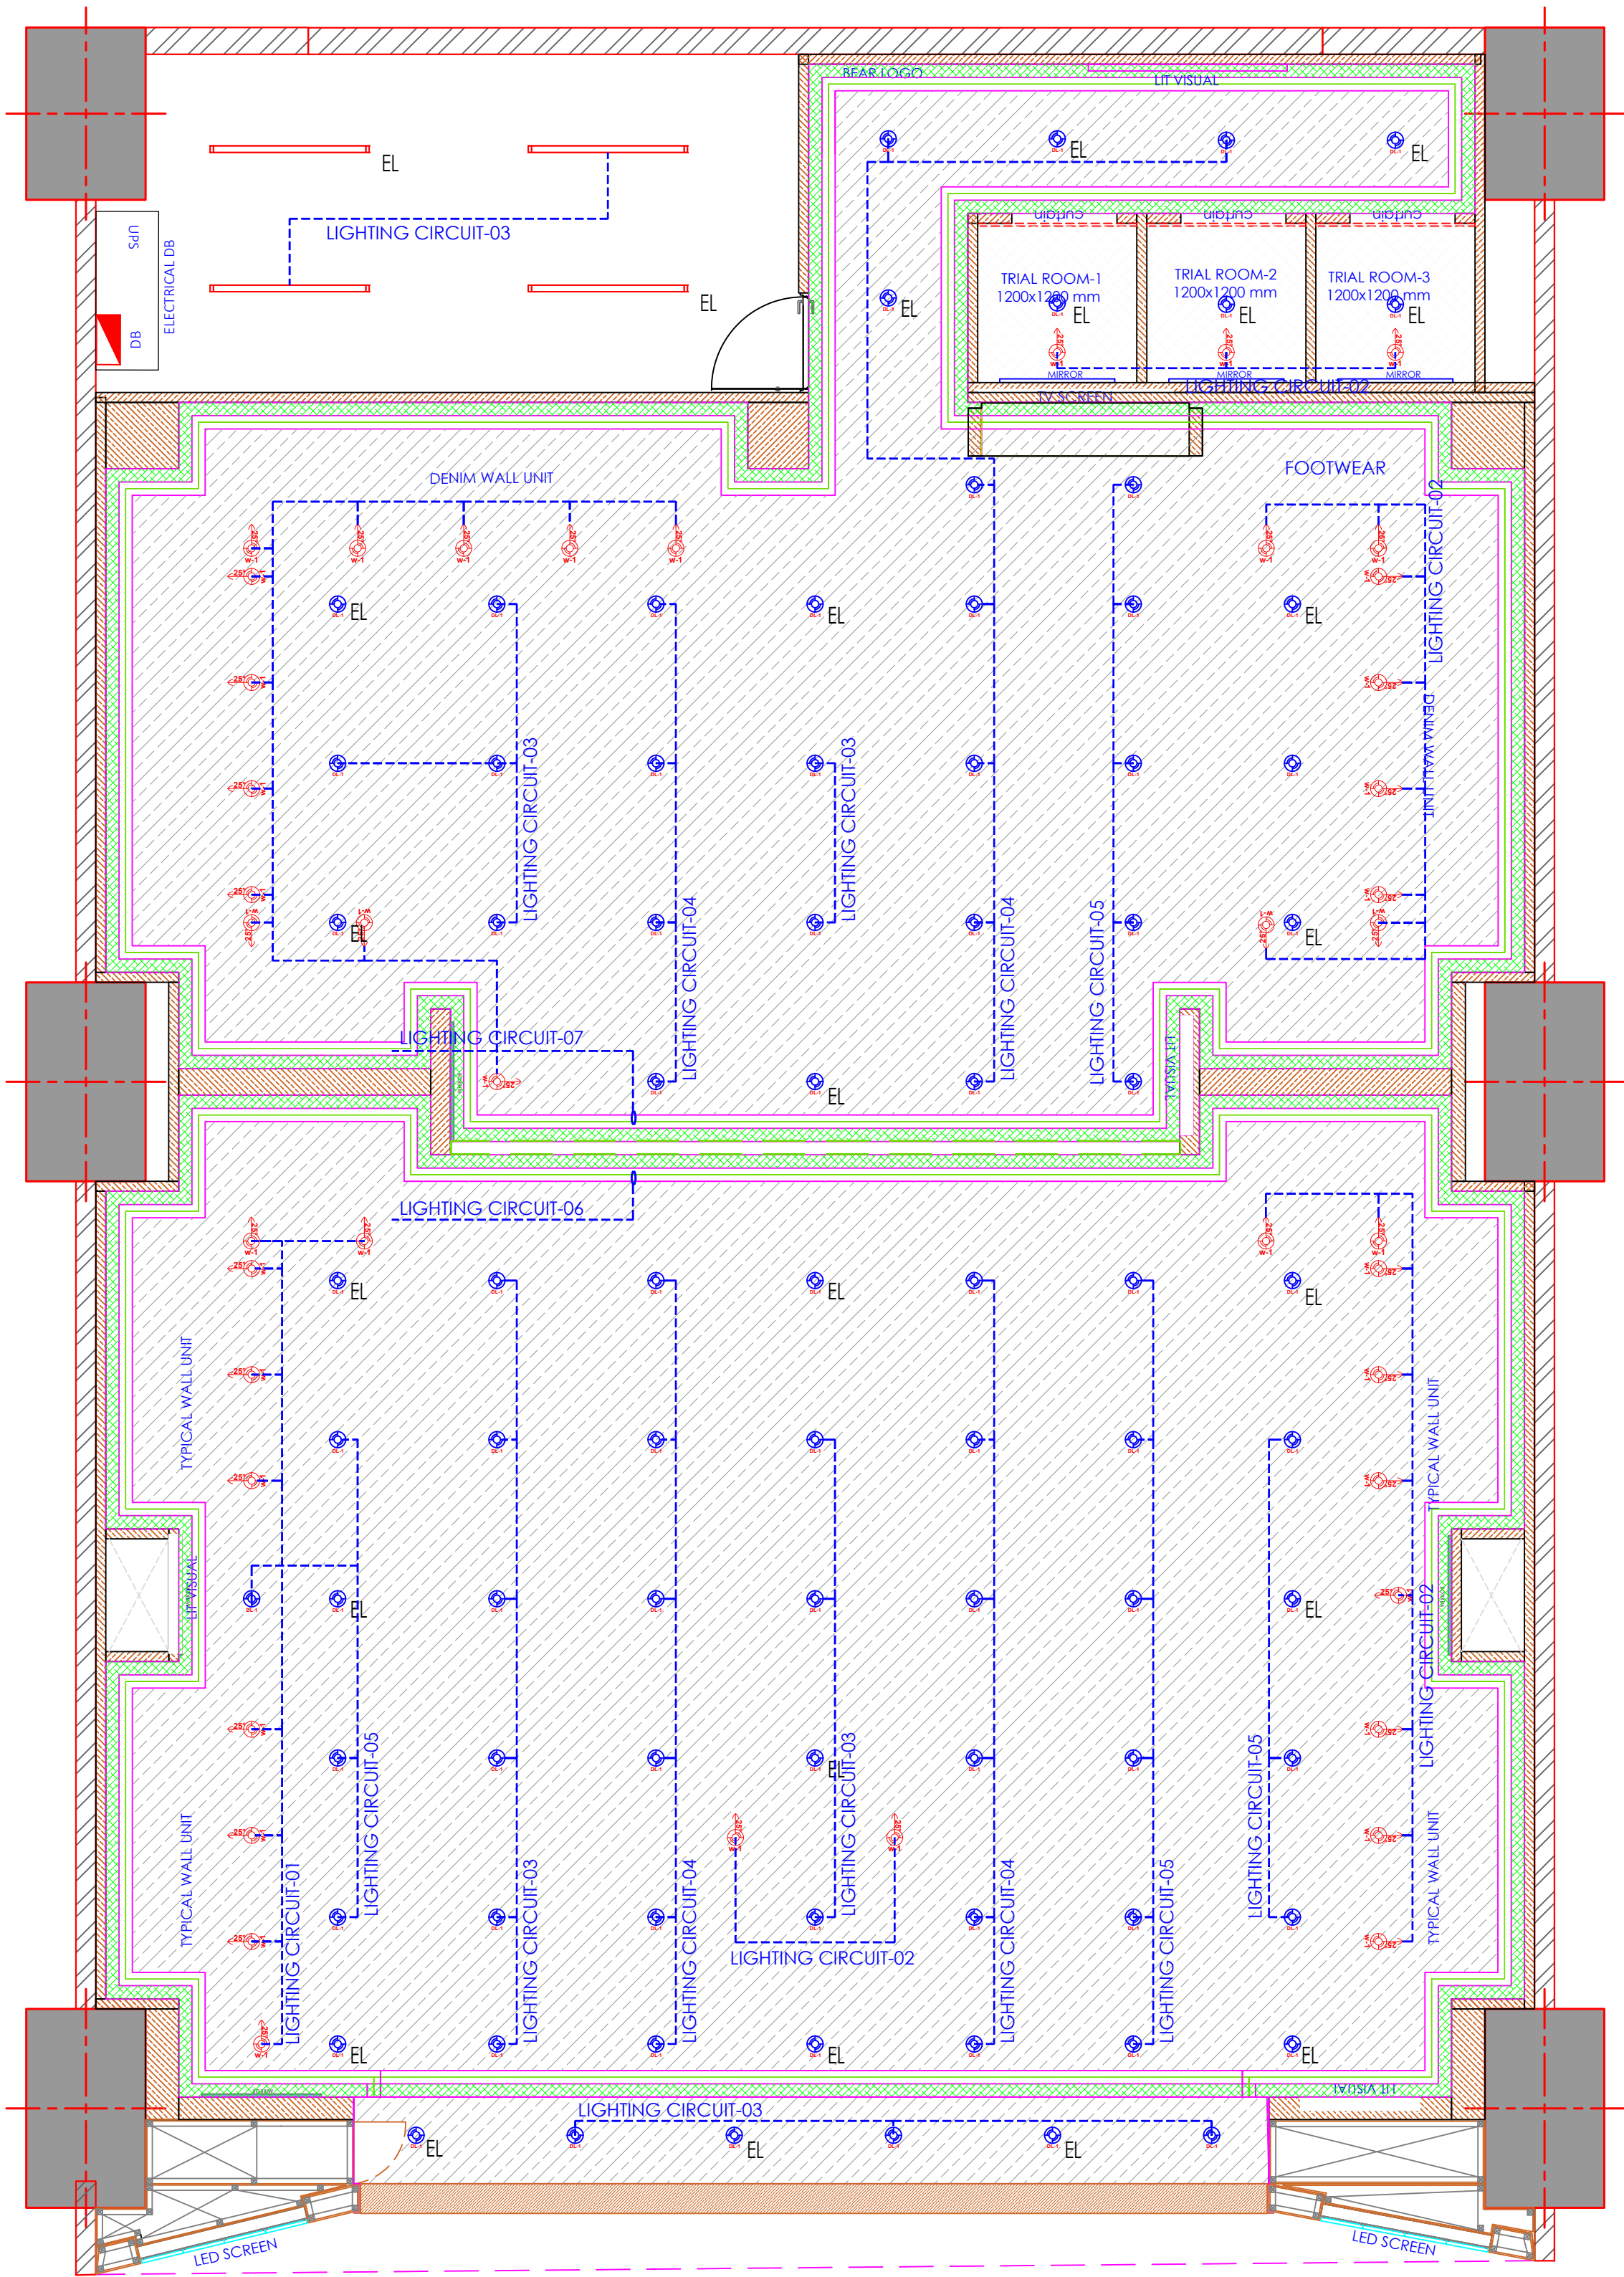

Notes:
1. Lighting & emergency points to keep in UPS for 30 mins backup.

TBH - Pacific mall, Jaipur - Lighting BOQ

S. NO.	SYB	PRODUCT DESCRIPTION	QTY
01		BOOM S 35W 40D RECESS MOUNTED LED WALL WASHER 4000K WHITE	43
02		XTRA M 35W 45D RECESS MOUNTED LED WALL WASHER 4000K WHITE	84
03		NEON STRIP 18W/MT. FLEXIBLE STRIP FOR COVELIGHT 4000K (IN MT.)	60MT
04		SPAN 20W SURFACE MOUNT LED TUBE LIGHT - 4FT 4000K WHITE	04

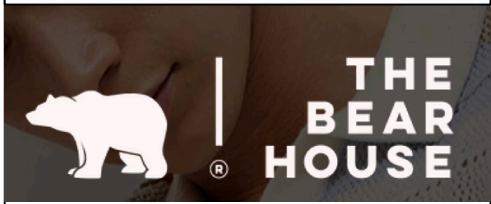

PACIFIC MALL
-
JAIPUR


Shop info

Market	INDIA
Province	RAJASTHAN
City	JAIPUR
City tier (tier 1/2/3)	TIER 2
Mall Name	PACIFIC MALL
New /Reno /Relo	NEW
STORE / SIS	STORE
Shop concept	THE BEAR HOUSE
Net size	1916 SQ FT
Slab height	5252 MM
B.O.B height	3769 MM

Drawing info



Title	LIGHTING LAYOUT
Designed by	RISHAD
Checked by	
Date	28.04.2026
Revision	
Dwg no.	

Notes:

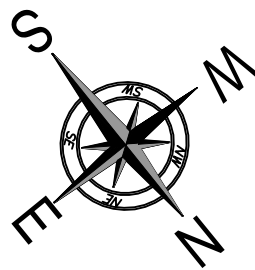

Ø25MM DRAIN PIPE TO BE CONNECTED
TO THE MALL DRAIN POINT.
DRAIN PIPE NEEDS TO BE
INSULATED WITH 6MM THICK
NITRILE RUBBER. SLOPE 1:100

200Wx100H
SA COLLAR WITH
CONTROL DAMPER x
5NO'S 144CFM EACH

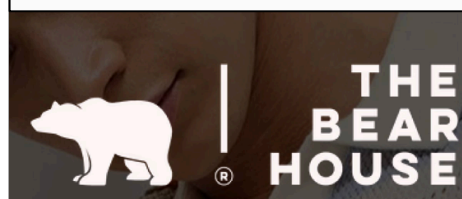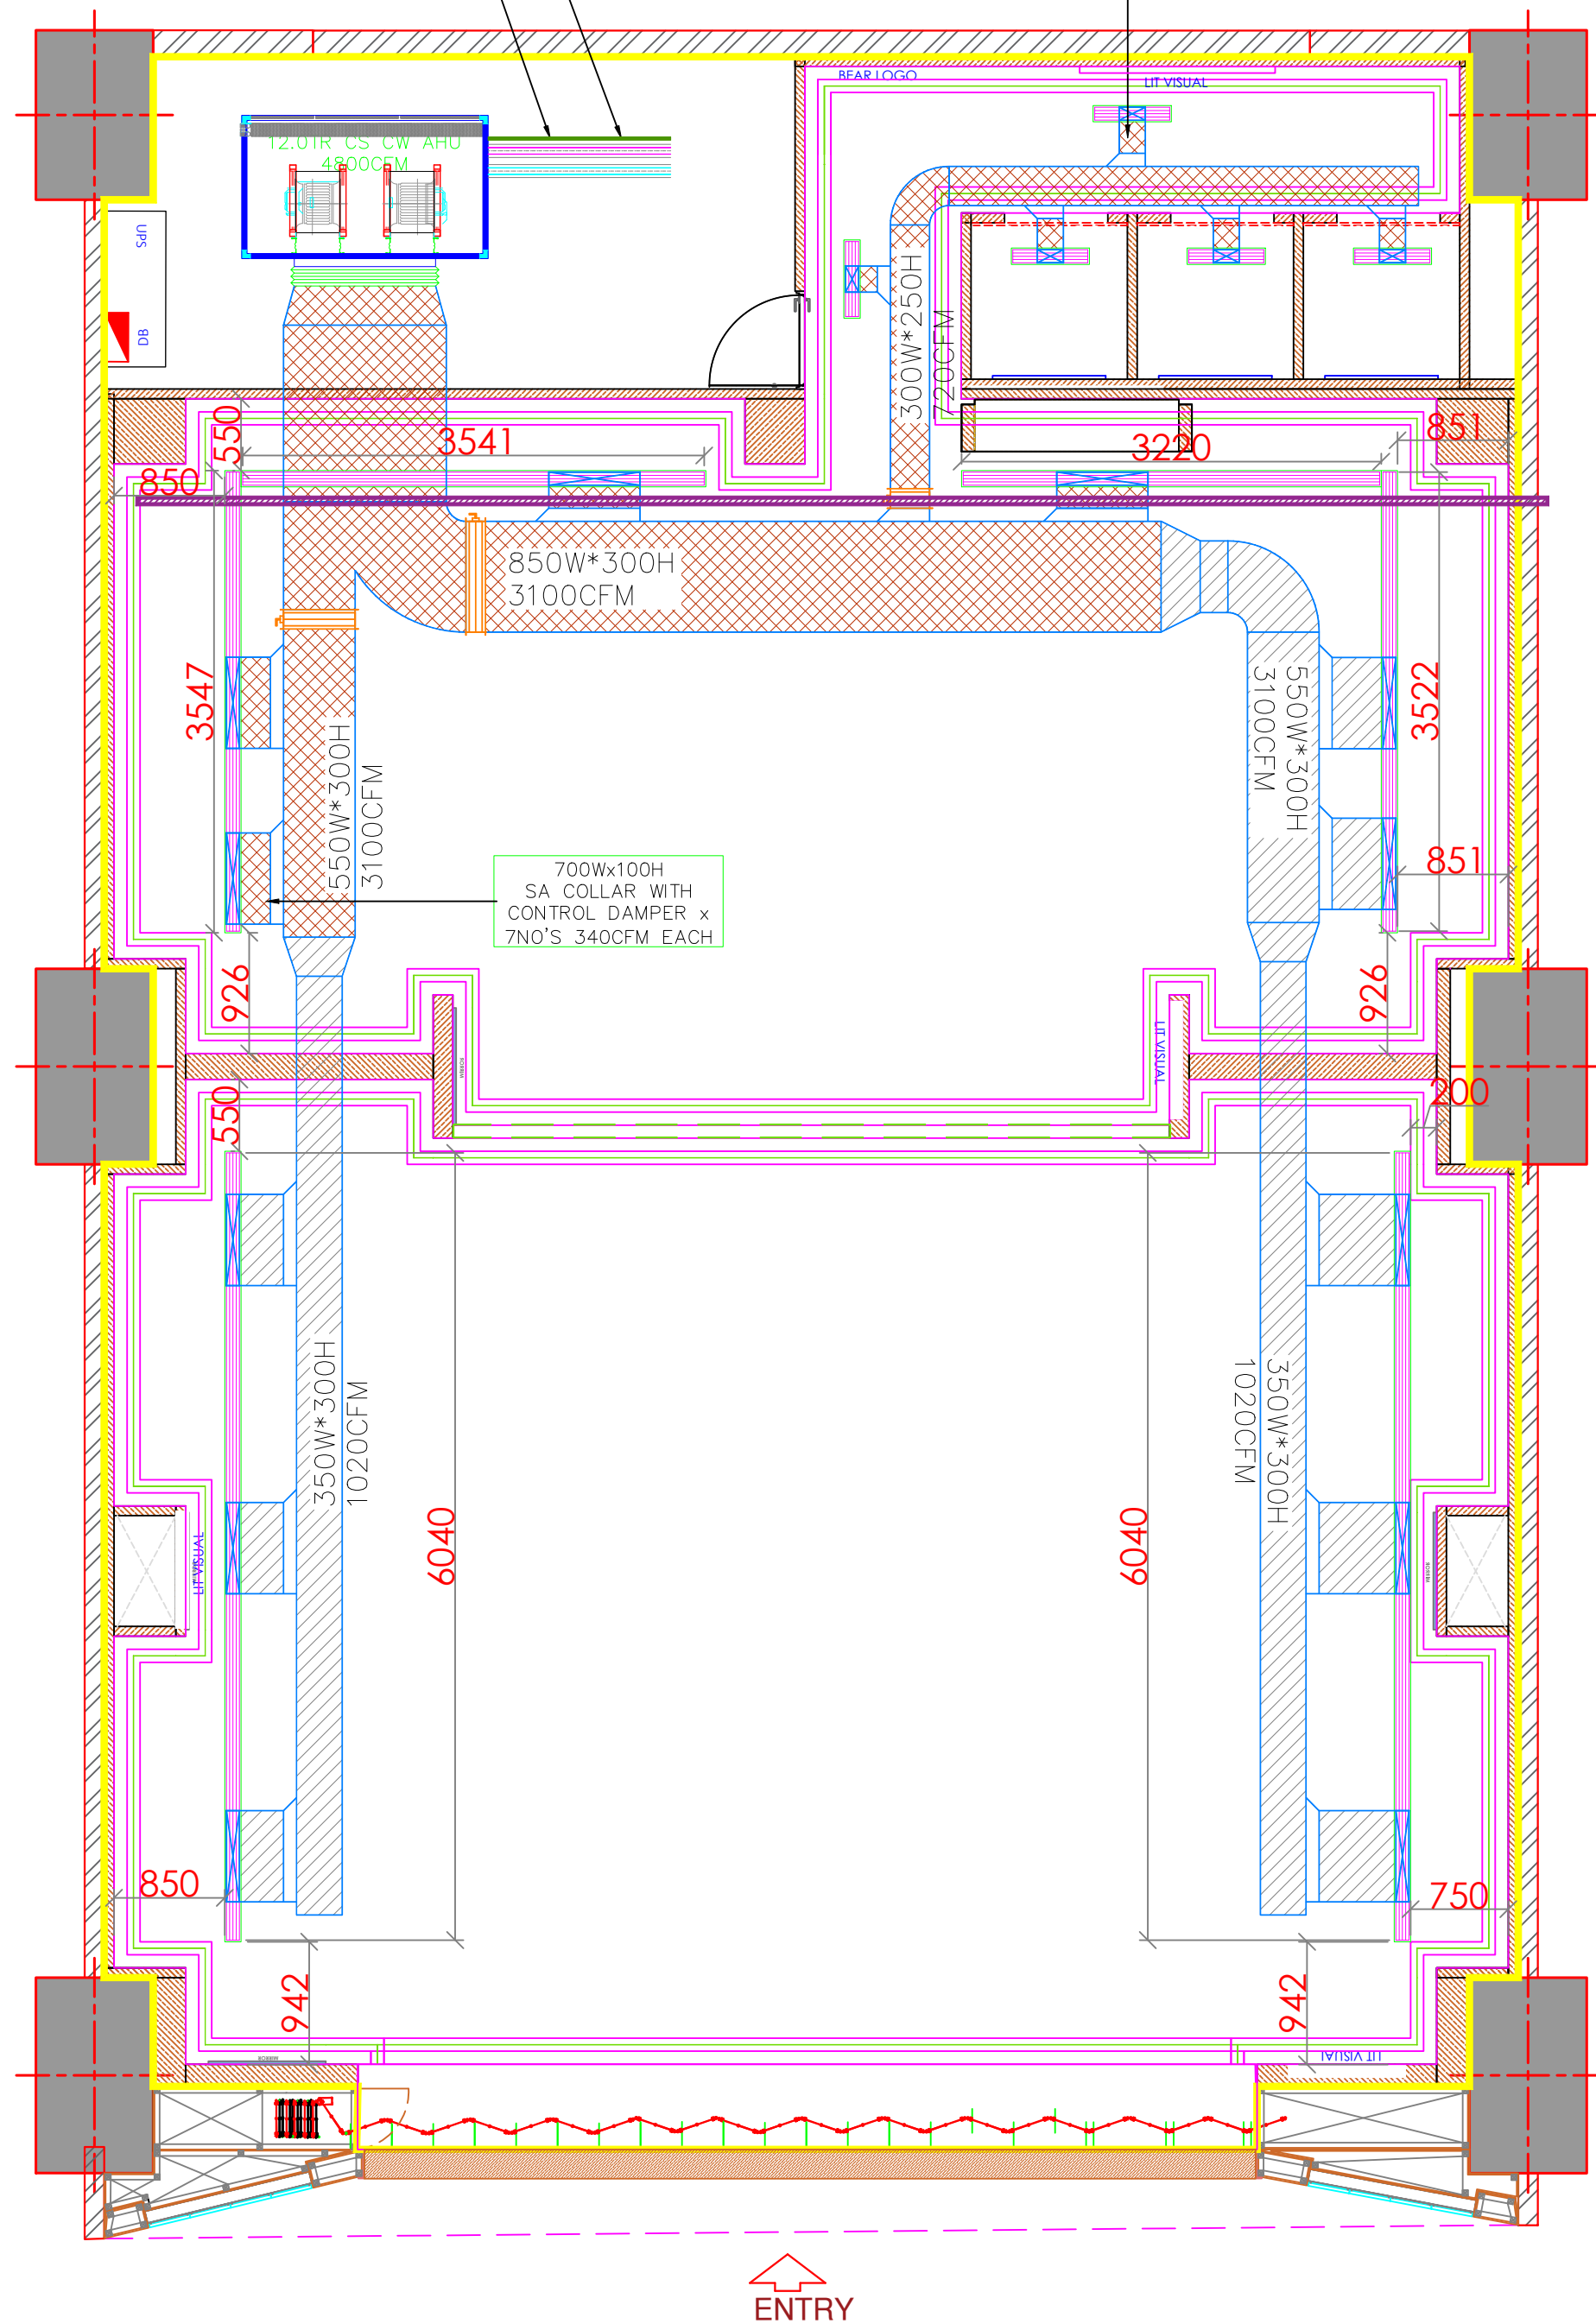

PACIFIC MALL
-
JAIPUR


Shop info

Market	INDIA
Province	RAJASTHAN
City	JAIPUR
City tier (tier 1/2/3)	TIER 2
Mall Name	PACIFIC MALL
New /Reno /Relo	NEW
STORE / SIS	STORE
Shop concept	THE BEAR HOUSE
Net size	1916 SQ FT
Slab height	5252 MM
B.O.B height	3769 MM

Drawing info

Title	HVAC LAYOUT
Designed by	RISHAD
Checked by	
Date	28.04.2026
Revision	
Dwg no.	

Notes:

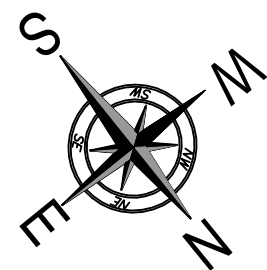




PACIFIC MALL
-
JAIPUR

SCHEDULE OF CHILLED WATER PIPE SUPPORT

NOMINAL PIPE SIZE		MAXIMUM SUPPORT SPACING (mm)	ANCHOR BOLT SIZE (mm)	M.S.ANGLE SIZE (mm)	CLAMP SIZE (mm)
inc	mm				
1/2"	15	2500	8	40 X 40 X 4	2 x 25
3/4"	20	2500	8	40 X 40 X 4	2 x 25
1"	25	2500	8	40 X 40 X 4	2 x 25
1 1/4"	32	2800	8	40 X 40 X 4	2 x 25
1 1/2"	40	2800	8	40 X 40 X 4	2 x 25
2"	50	2800	10	40 X 40 X 4	2 x 25
2 1/2"	65	3200	10	50 X 50 X 4	3 x 40
3"	80	3200	10	50 X 50 X 4	3 x 40
4"	100	4200	12	50 X 50 X 4	3 x 50
5"	125	4200	16	50 X 50 X 4	3 x 50
6"	150	5200	16	50 X 50 X 4	3 x 50
8" TO 10"	200 TO 250	5200	16	50 X 50 X 4	4 x 50

SCHEDULE OF TRAPEZE HANGER

NOMINAL PIPE SIZE		MAXIMUM HANGER SPACING (mm)	MINIMUM ROD SIZE (mm)	M.S.ANGLE SIZE (mm)
inc	mm			
1/2"	15	2500	8	40 X 40 X 4
3/4"	20	2500	8	40 X 40 X 4
1"	25	2500	8	40 X 40 X 4
1 1/4"	32	2800	8	40 X 40 X 4
1 1/2"	40	2800	8	40 X 40 X 4
2"	50	2800	10	40 X 40 X 4
2 1/2"	65	3200	10	50 X 50 X 4
3"	80	3200	10	50 X 50 X 4
4"	100	4200	12	50 X 50 X 4
5"	125	4200	16	50 X 50 X 4
6"	150	5200	16	50 X 50 X 4

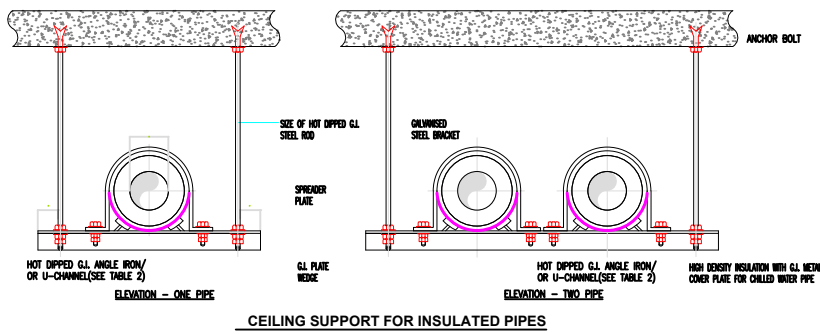


1. ALL DIMENSIONS ARE IN MM.
2. DRAIN PIPE TO BE CONNECTED TO NEAREST DRAIN POINT.

SL No.	LOCATION	MODEL	Cooling capacity TR	AIR FLOW CFM	ESP (Max of WC)	*AIR ON COIL DB/WB*°C	*AIR OFF COIL DB/WB*°C	WATER FLOW GPM	*UNIT TYPE*	Power I/P Watts	Dimensions (mm) H D W	Electrical Power Supply	Weight Kg	QTY Nos
1	THE BEAR HOUSE@ PACIFIC MALL JAIPUR	—	12.0	4800	18	24.0 / 17.1	13.39/12.04	28.8	Ducted	—	— — —	—	—	1

HVAC Legend

1		Ceiling Suspended Chilled Water AHU
2		Supply Rectangular Air Duct
3		Supply Elliptical Air Duct
4		Acoustic Insulation
5		Thermal Insulation
6		SA/RA Linear Grill
7		Rectangular VCD
8		S/R Chilled Water Pipe
9		Drain pipe connected to nearest drain point.
10		

Valves Connections

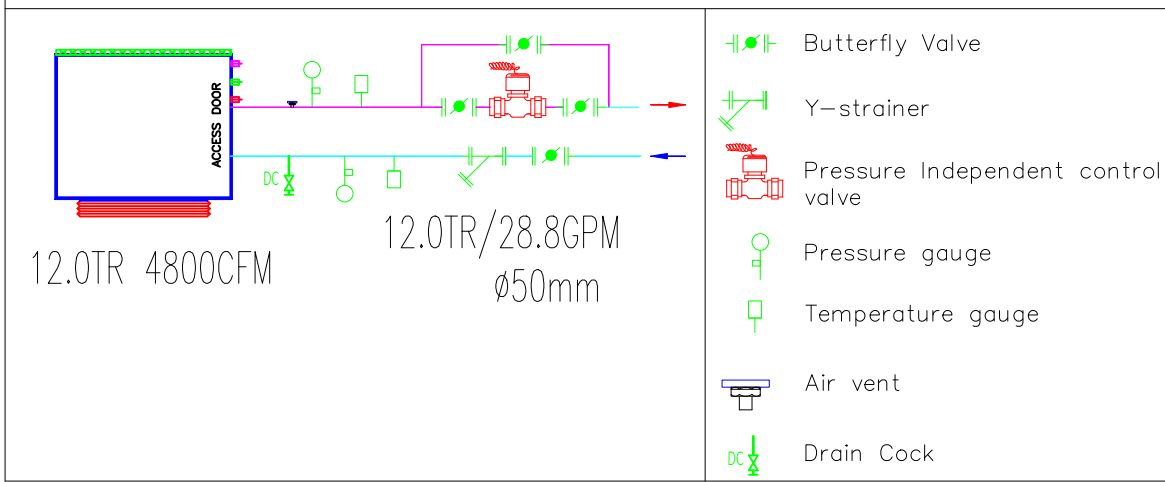


Shop info


Market	INDIA
Province	RAJASTHAN
City	JAIPUR
City tier (tier 1/2/3)	TIER 2
Mall Name	PACIFIC MALL
New /Reno /Relo	NEW
STORE / SIS	STORE
Shop concept	THE BEAR HOUSE
Net size	1916 SQ FT
Slab height	5252 MM
B.O.B height	3769 MM

Drawing info

Title	HVAC LAYOUT
Designed by	RISHAD
Checked by	
Date	28.04.2026
Revision	
Dwg no.	

Notes:

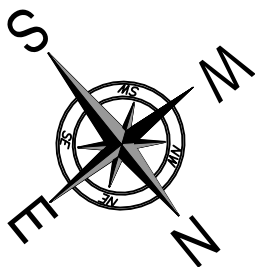


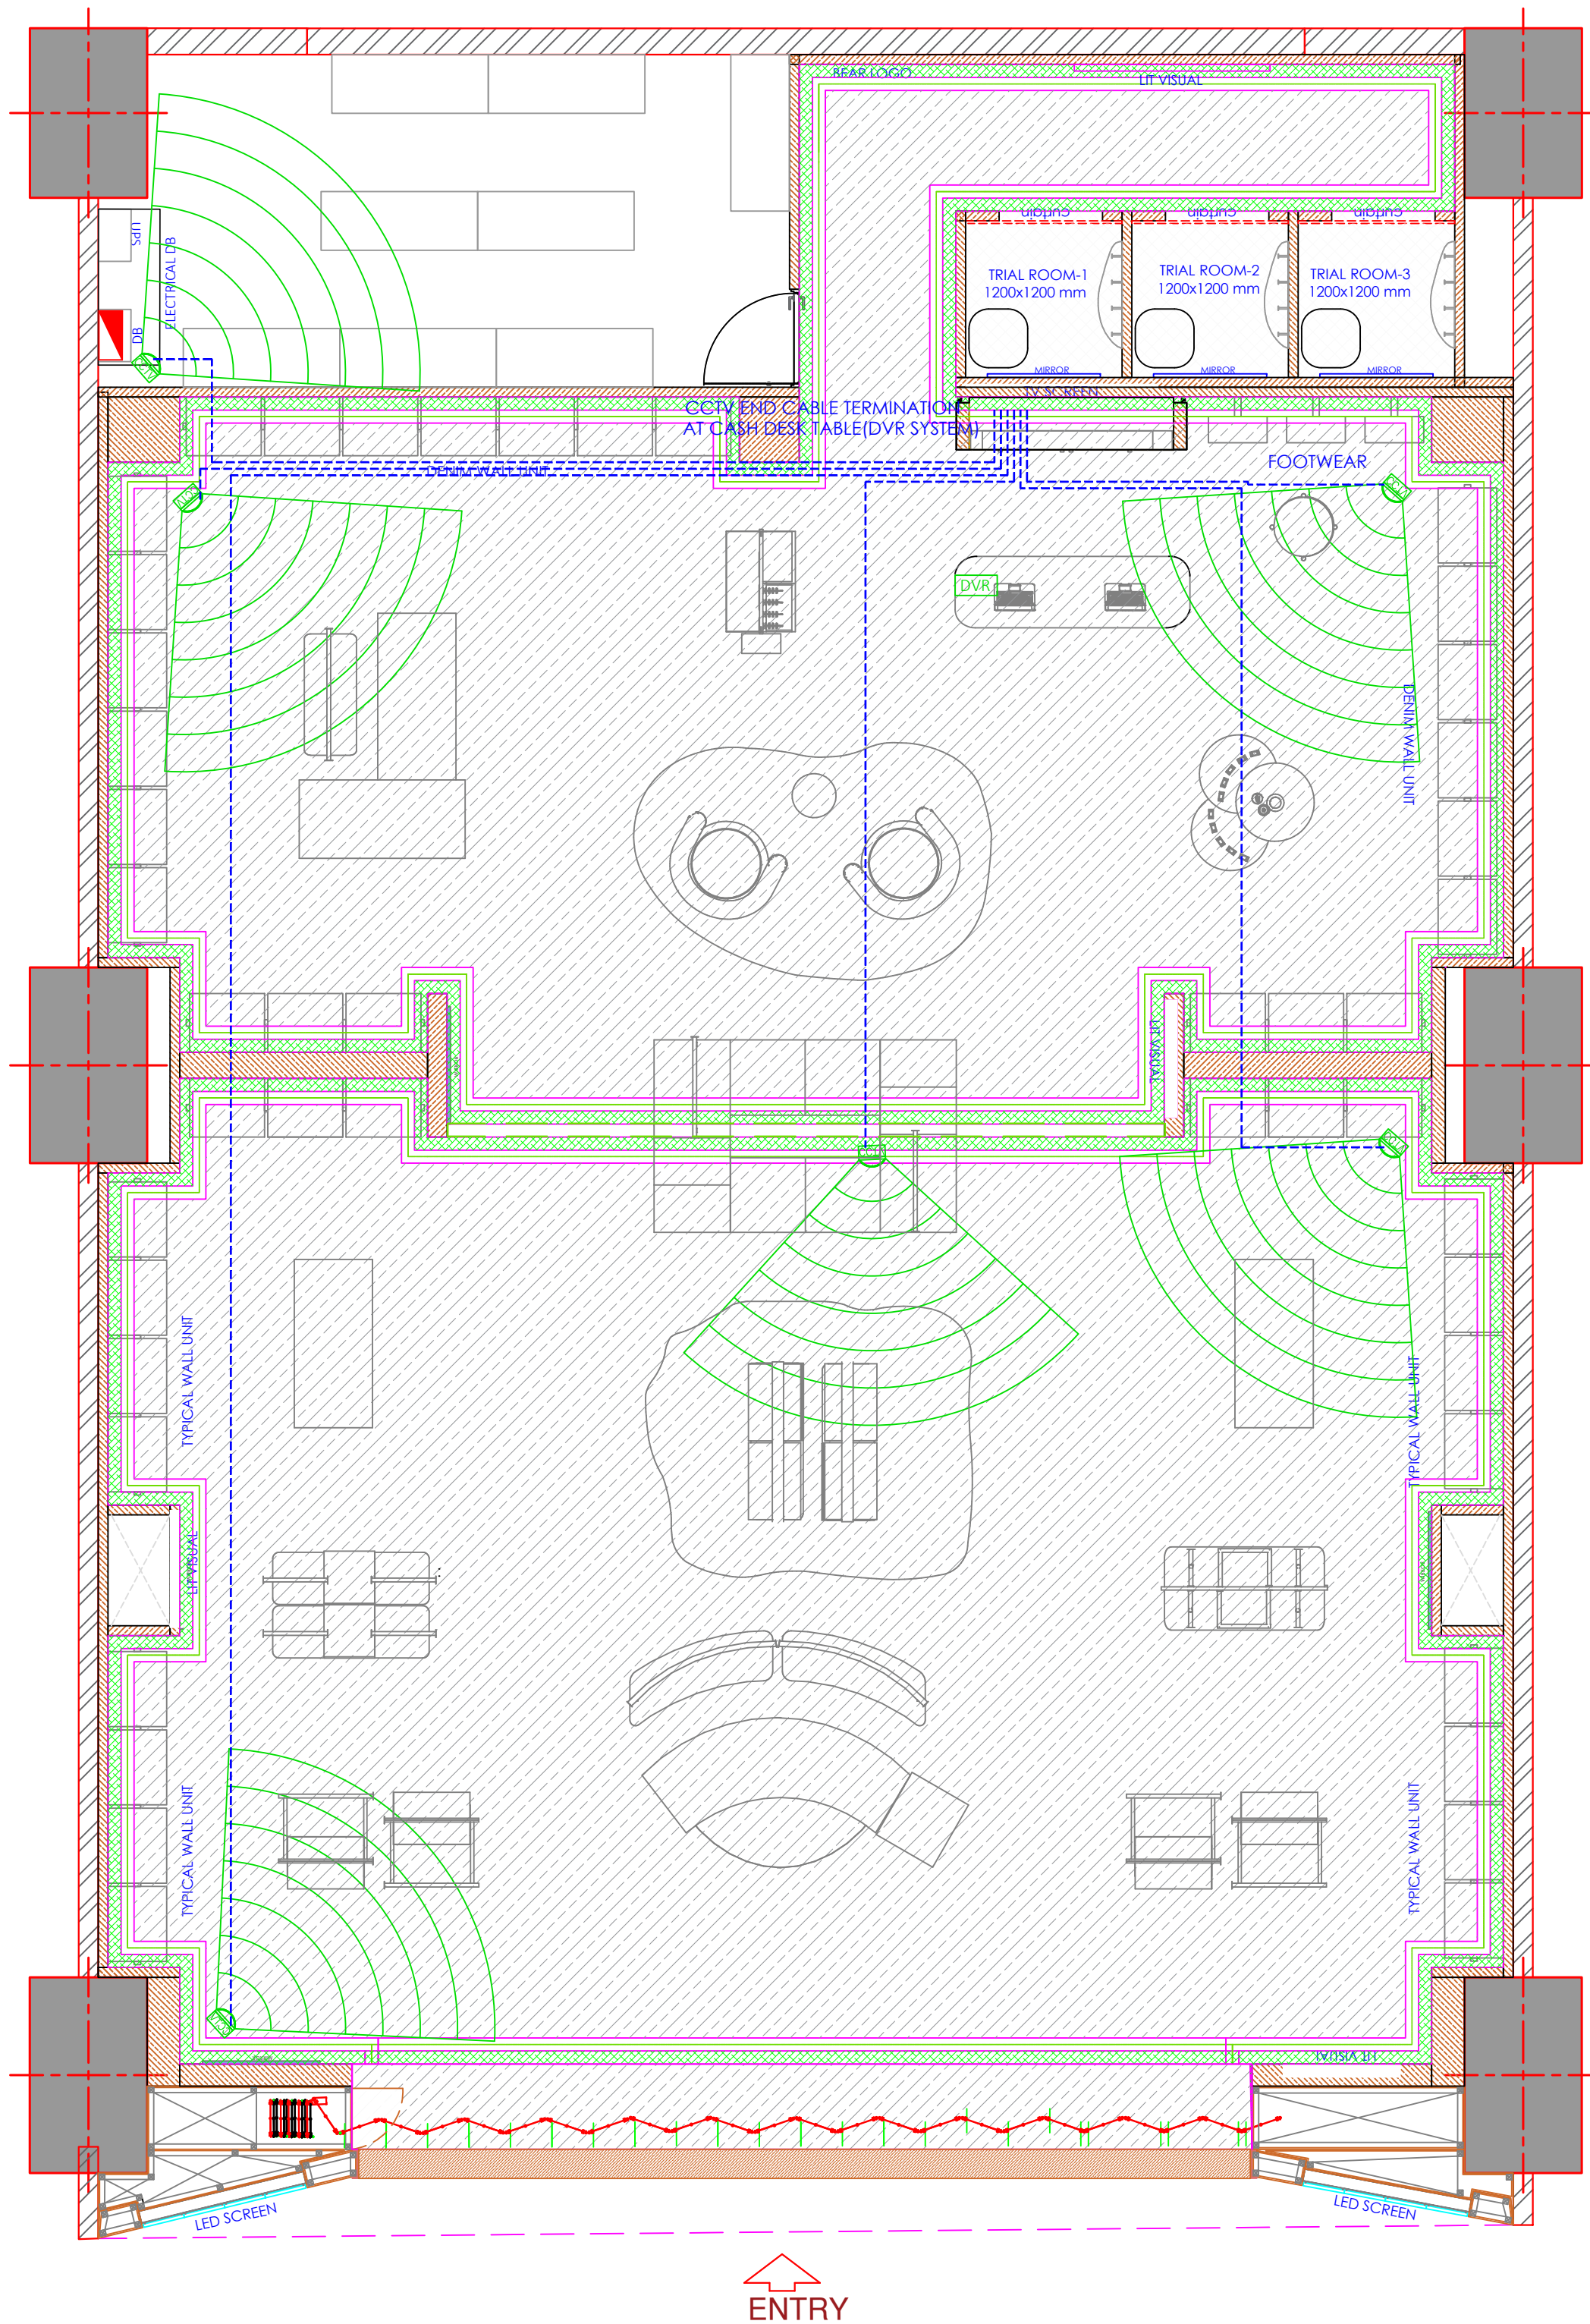

LEGEND : CCTV

SINO	SYMBOL	DESCRIPTION	QTY.
1		HIK VISION MAKE ,INFRA RED ENABLED ONE HIGH RESOLUTION , FIXED 6.0MM LENS DOME CAMERA	06
2		FISH EYE CAMERA	00
3		BULLET-PROOF CAMERA FOR OUTSIDE	00
4		DVR UNIT	01

Notes:
1.31days backup in the DVR to be provided

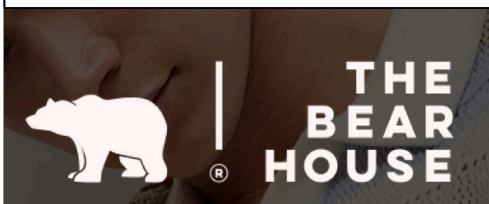

PACIFIC MALL
-
JAIPUR


Shop info


Market	INDIA
Province	RAJASTHAN
City	JAIPUR
City tier (tier 1/2/3)	TIER 2
Mall Name	PACIFIC MALL
New /Reno /Relo	NEW
STORE / SIS	STORE
Shop concept	THE BEAR HOUSE
Net size	1916 SQ FT
Slab height	5252 MM
B.O.B height	3769 MM

Drawing info

Title	CCTV LAYOUT
Designed by	RISHAD
Checked by	
Date	28.04.2026
Revision	
Dwg no.	


Notes:

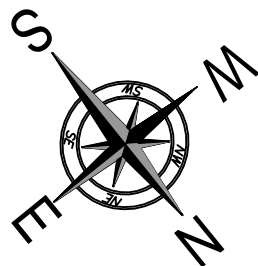

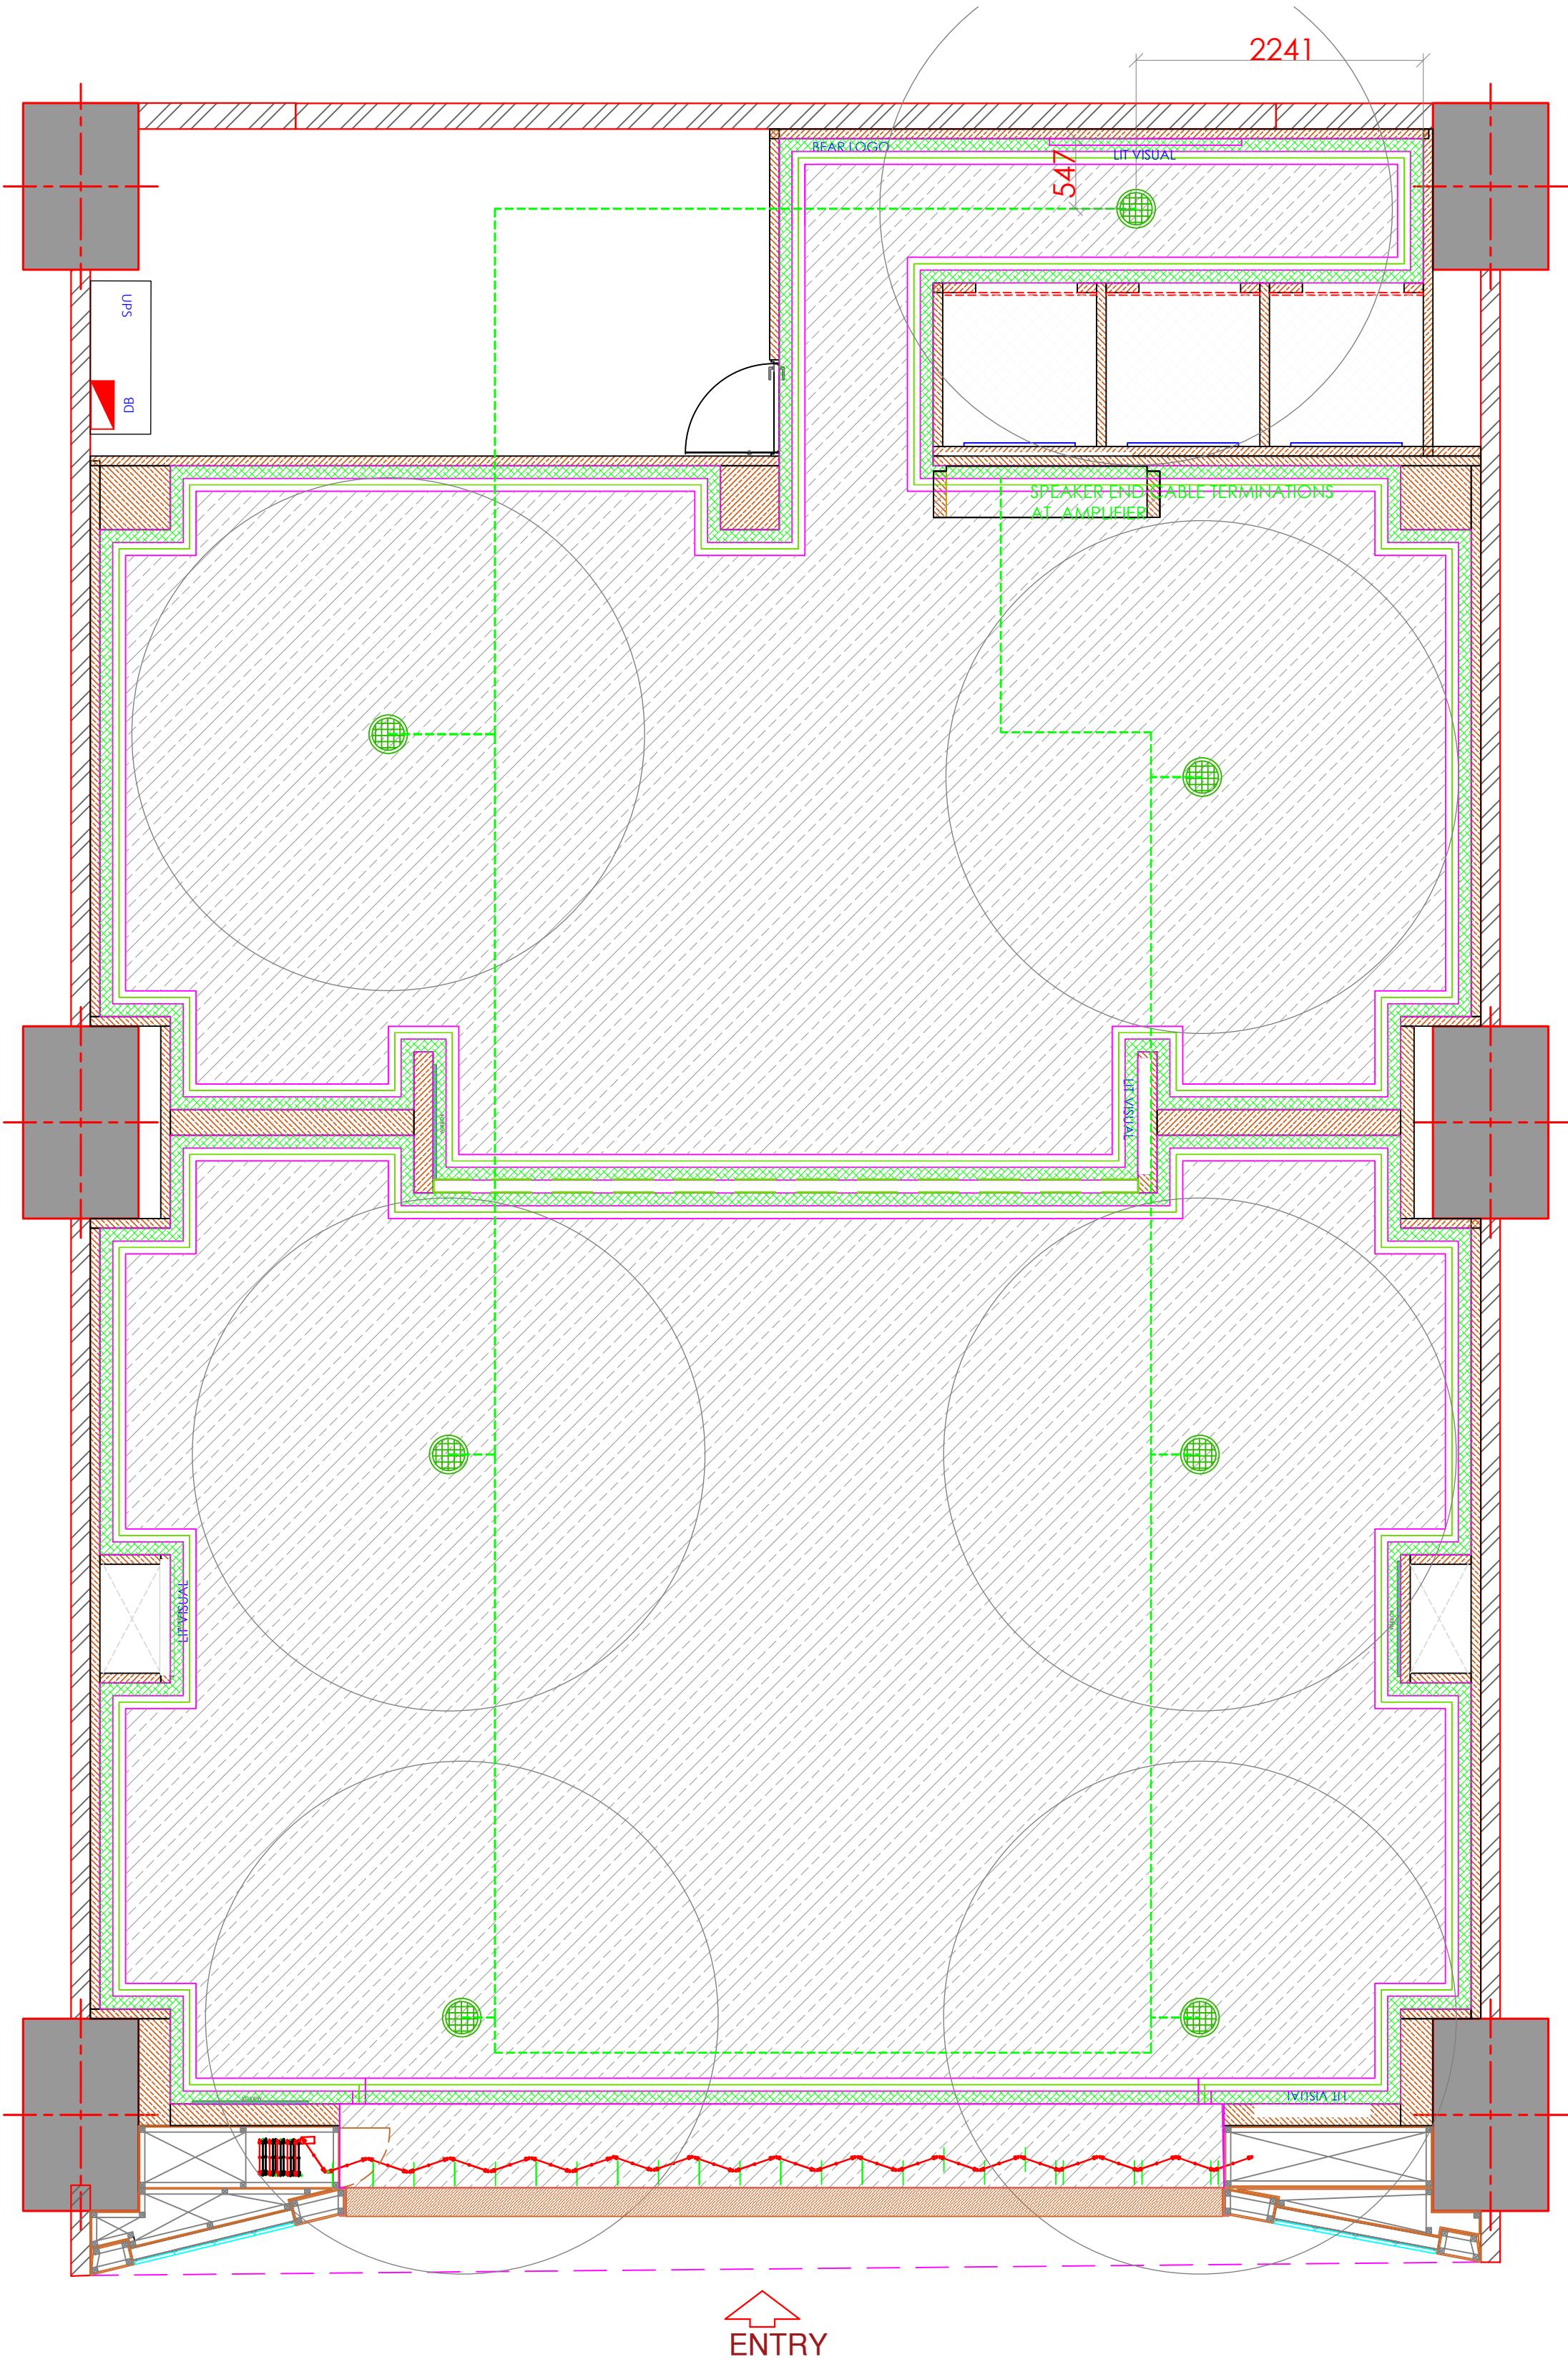

LEGEND : AUDIO

SINO	SYMBOL	DESCRIPTION	QTY.
1		CEILING MOUNTED SPEAKERS	07
2		SURFACE MOUNTED SPEAKERS	00
3		AMPLIFIER	01

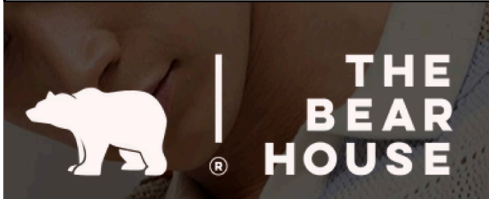



PACIFIC MALL
-
JAIPUR

Shop info	
Market	INDIA
Province	RAJASTHAN
City	JAIPUR
City tier (tier 1/2/3)	TIER 2
Mall Name	PACIFIC MALL
New /Reno /Relo	NEW
STORE / SIS	STORE
Shop concept	THE BEAR HOUSE
Net size	1916 SQ.FT
Slab height	5252 MM
B.O.B height	3769 MM

Drawing info	
Title	AUDIO LAYOUT
Designed by	RISHAD
Checked by	
Date	28.04.2026
Revision	
Dwg no.	

Notes:

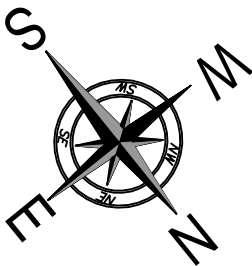

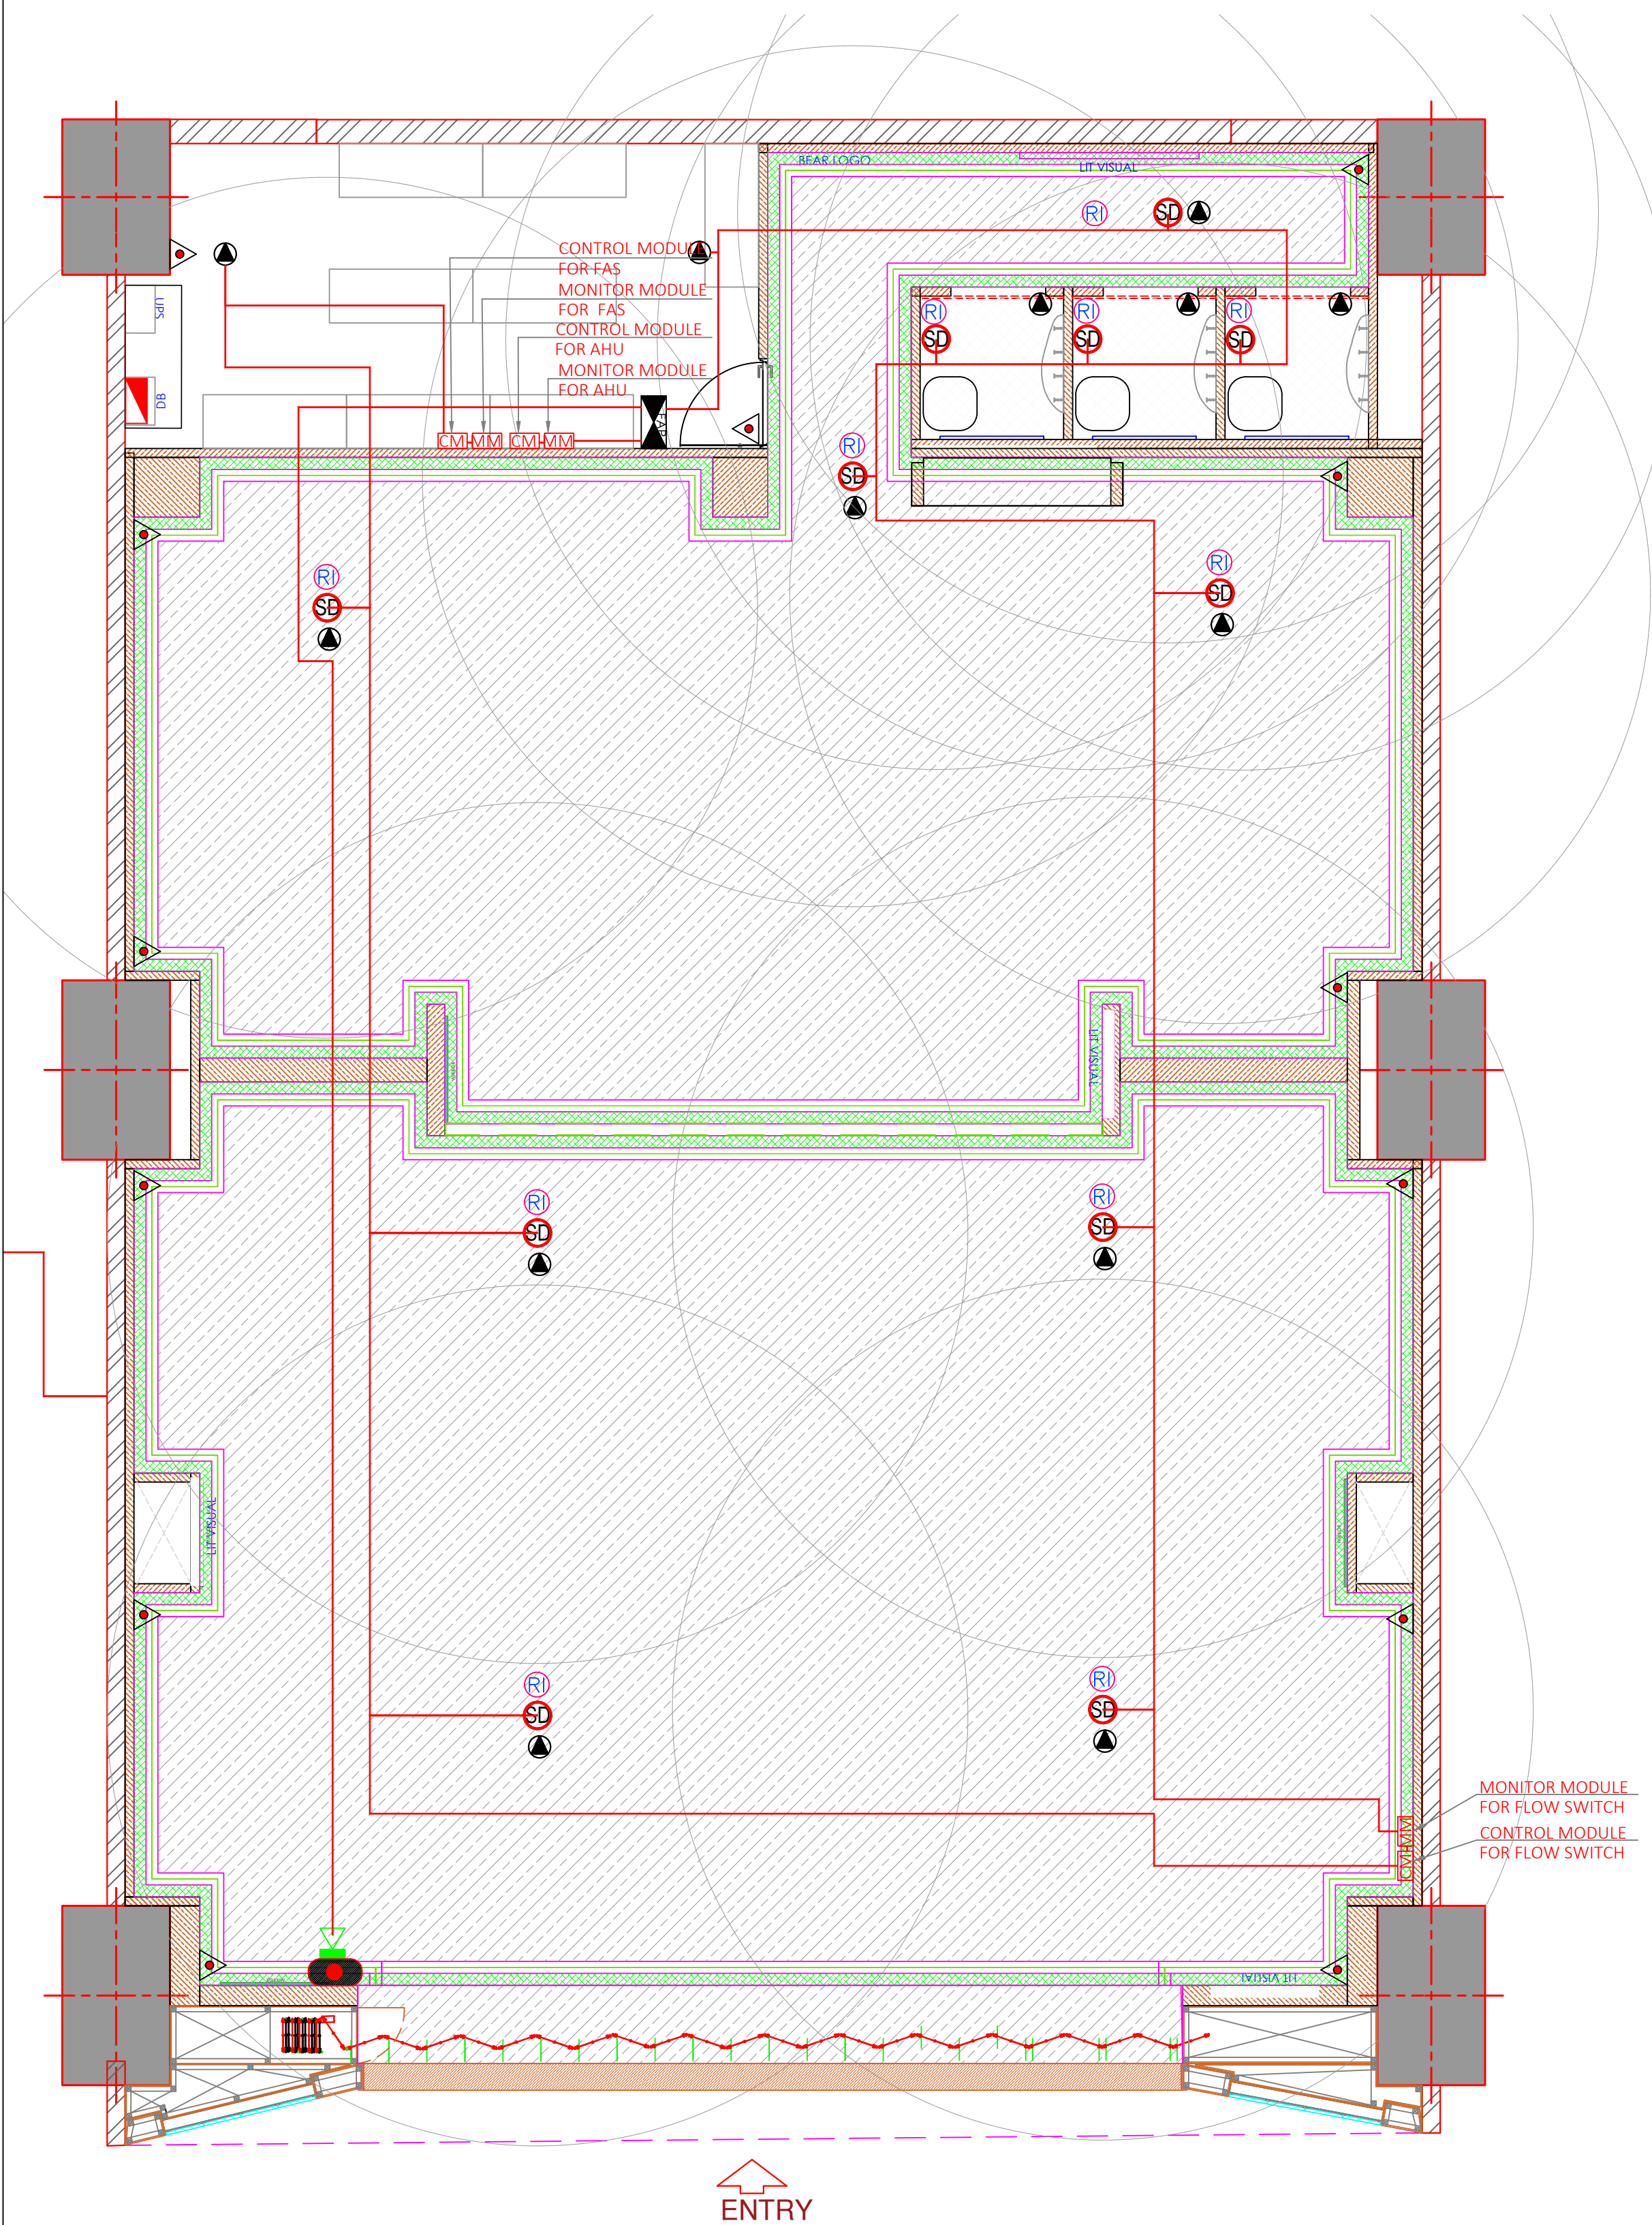

LEGEND : FAS

SINO	SYMBOL	DESCRIPTION	QTY.
1		PROPOSED SMOKE DETECTOR BELOW FALSE CEILING	11
2		PROPOSED ABOVE FALSE CEILING SMOKE DETECTOR	13
3		RESPONSE INDICATOR	11
4		AUTOMATIC EXTINGUISHER CEILING MOUNTED	00
5		FIRE EXTINGUISHER CO2 5KGWITH AUTOGLOW SIGNAGE	01
6		MANUAL CALL POINT @ 1350MM FROM FFL(Break Glass Type)	01
7		HOOTER @ FALSE CEILING LEVEL	01
8		FIRE ALARM CONTROL PANEL-	01
9		FIRE EXTINGUISHER ABC 5KG WITH AUTOGLOW SIGNAGE	14
9		FIRE EXTINGUISHER DRY WITH AUTOGLOW SIGNAGE	00



PACIFIC MALL
-
JAIPUR


Shop info


Market	INDIA
Province	RAJASTHAN
City	JAIPUR
City tier (tier 1/2/3)	TIER 2
Mall Name	PACIFIC MALL
New /Reno /Relo	NEW
STORE / SIS	STORE
Shop concept	THE BEAR HOUSE
Net size	1916 SQ FT
Slab height	5252 MM
B.O.B height	3769 MM

Drawing info

Title	FAS LAYOUT
Designed by	RISHAD
Checked by	
Date	28.04.2026
Revision	
Dwg no.	

Notes:

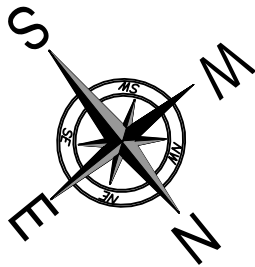

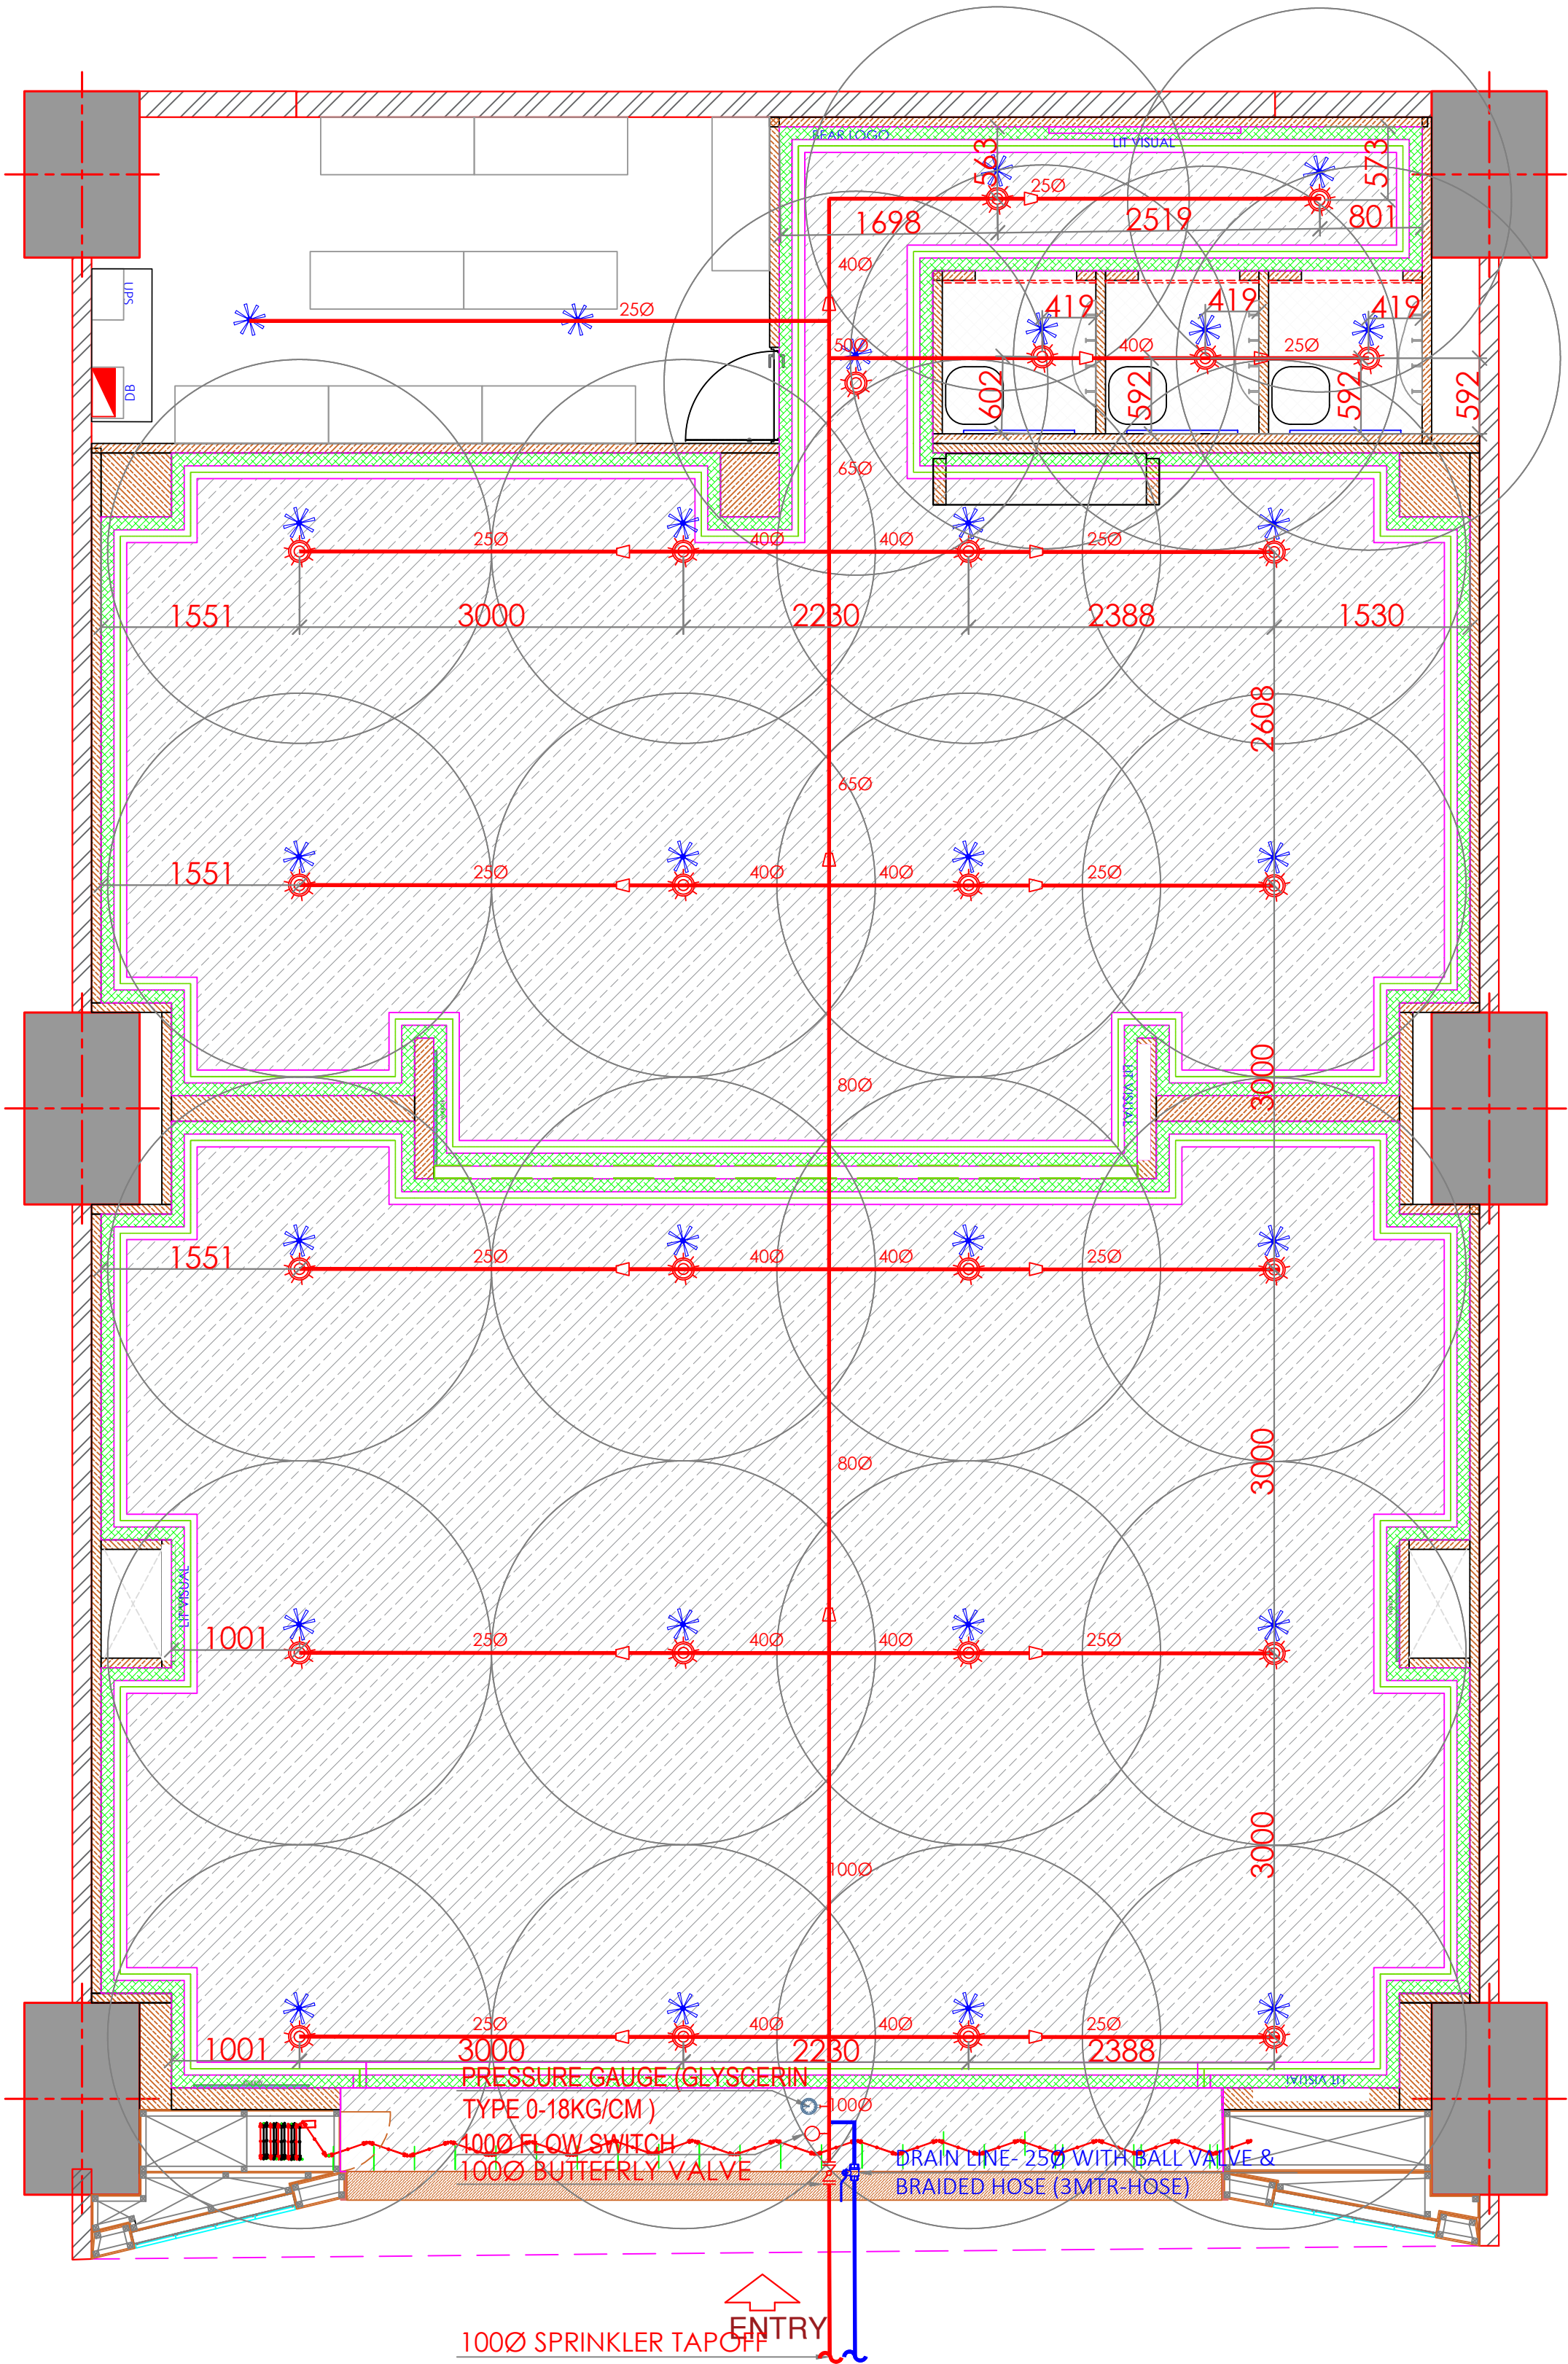

LEGEND : FAS

SINO	SYMBOL	DESCRIPTION	QTY.
1		PROPOSED SMOKE DETECTOR BELOW FALSE CEILING	11
2		PROPOSED ABOVE FALSE CEILING SMOKE DETECTOR	13
3		RESPONSE INDICATOR	11
4		AUTOMATIC EXTINGUISHER CEILING MOUNTED	00
5		FIRE EXTINGUISHER CO2 5KG WITH AUTO GLOW SIGNAGE	01
6		MANUAL CALL POINT @ 1350MM FROM FFL(Break Glass Type)	01
7		HOOTER @ FALSE CEILING LEVEL	01
8		FIRE ALARM CONTROL PANEL-	01
9		FIRE EXTINGUISHER ABC 5KG WITH AUTO GLOW SIGNAGE	14
9		FIRE EXTINGUISHER DRY WITH AUTO GLOW SIGNAGE	00



PACIFIC MALL
-
JAIPUR


Shop info


Market	INDIA
Province	RAJASTHAN
City	JAIPUR
City tier (tier 1/2/3)	TIER 2
Mall Name	PACIFIC MALL
New /Reno /Relo	NEW
STORE / SIS	STORE
Shop concept	THE BEAR HOUSE
Net size	1916 SQ FT
Slab height	5252 MM
B.O.B height	3769 MM

Drawing info

Title	FAS LAYOUT
Designed by	RISHAD
Checked by	
Date	28.04.2026
Revision	
Dwg no.	


Notes:

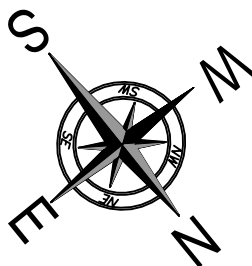

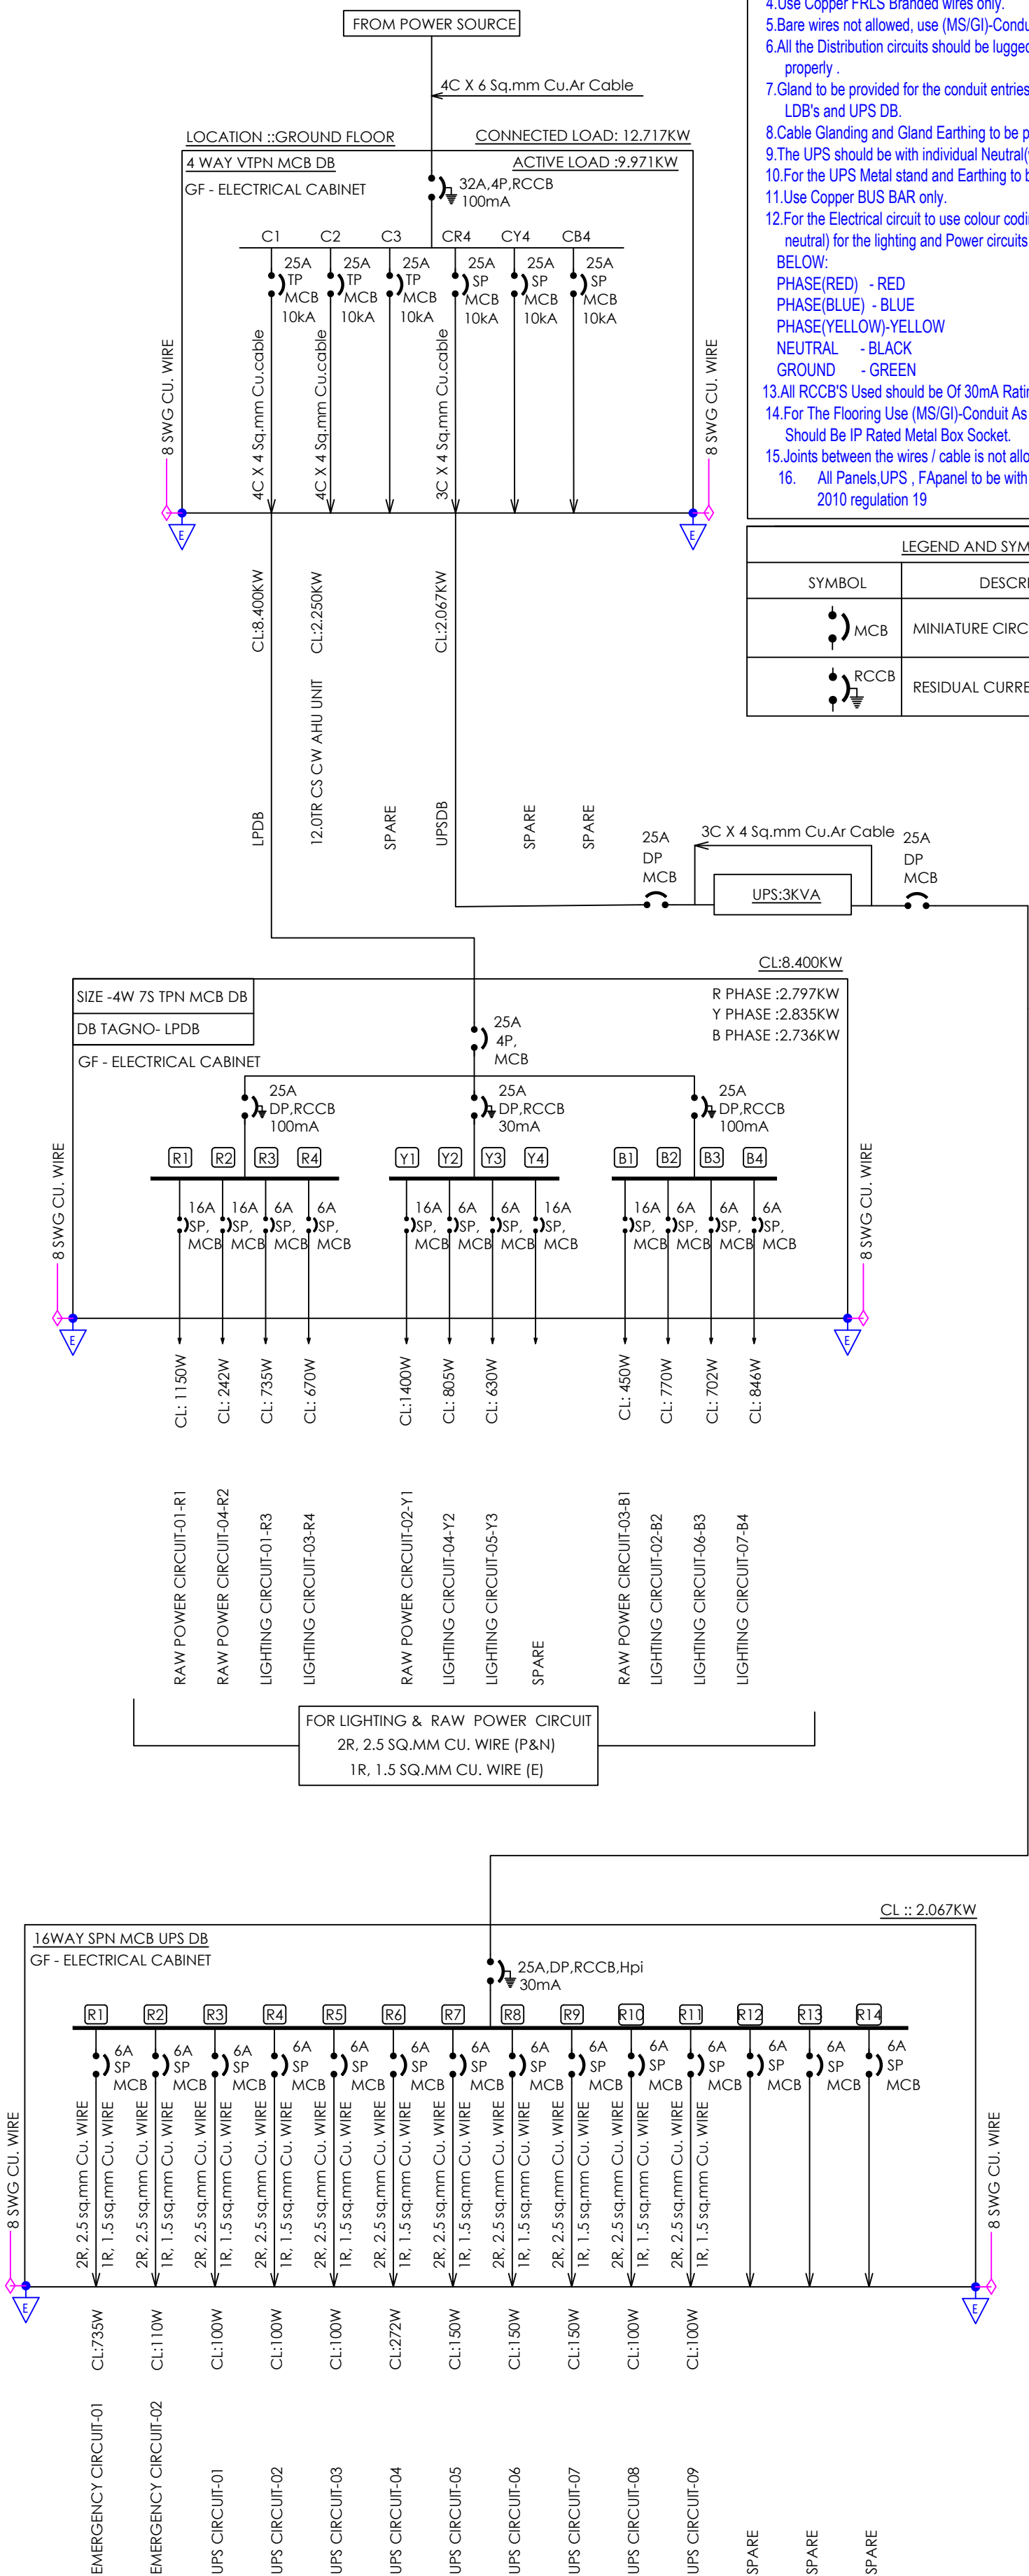

- GENERAL NOTES FOR DISTRIBUTION BOARDS:
- All Electrical installation to be as per IS 3594
- 1.DB's and DOL starter panel if proposed should be fixed at operational height (1500MM) with proper operational clearance and on permanent wall only.
 - 2.The DB/Electrical panels/circuits should not be below or near to AC Units(HI Wall split,Cassette&AHU),/condensate drain line/any water source as per the electrical instruction.
 - 3.Use Armored copper XLPE cable only.
 - 4.Use Copper FRLS Branded wires only.
 - 5.Bare wires not allowed, use (MS/GI)-Conduits and Metal flexible hoses.
 - 6.All the Distribution circuits should be lugged and the dressing to be done properly .
 - 7.Gland to be provided for the conduit entries in the sockets and PDB's , LDB's and UPS DB.
 - 8.Cable Glanding and Gland Earthing to be provided.
 - 9.The UPS should be with individual Neutral(with isolation transformer).
 - 10.For the UPS Metal stand and Earthing to be provided.
 - 11.Use Copper BUS BAR only.
 - 12.For the Electrical circuit to use colour coding wires (R, Y, B, earth and neutral) for the lighting and Power circuits.
- BELOW:
- PHASE(RED) - RED
 - PHASE(BLUE) - BLUE
 - PHASE(YELLOW)-YELLOW
 - NEUTRAL - BLACK
 - GROUND - GREEN
- 13.All RCCB'S Used should be Of 30mA Rating.
 - 14.For The Flooring Use (MS/GI)-Conduit As Per Requirement And Socket Should Be IP Rated Metal Box Socket.
 - 15.Joints between the wires / cable is not allowed.
 16. All Panels,UPS , FApanel to be with double earthing as per CEA 2010 regulation 19

LEGEND AND SYMBOLS	
SYMBOL	DESCRIPTION
	MINIATURE CIRCUIT BREAKER
	RESIDUAL CURRENT CIRCUIT BREAKER

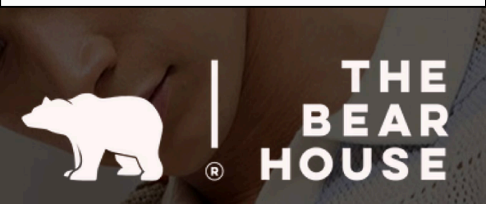


PACIFIC MALL


-

JAIPUR

Shop info	
Market	INDIA
Province	RAJASTHAN
City	JAIPUR
City tier (tier 1/2/3)	TIER 2
Mall Name	PACIFIC MALL
New /Reno /Relo	NEW
STORE / SIS	STORE
Shop concept	THE BEAR HOUSE
Net size	1916 SQ. FT
Slab height	5252 MM
B.O.B height	3769 MM

Drawing info	
Title	MSLD
Designed by	RISHAD
Checked by	
Date	28.04.2026
Revision	
Dwg no.	

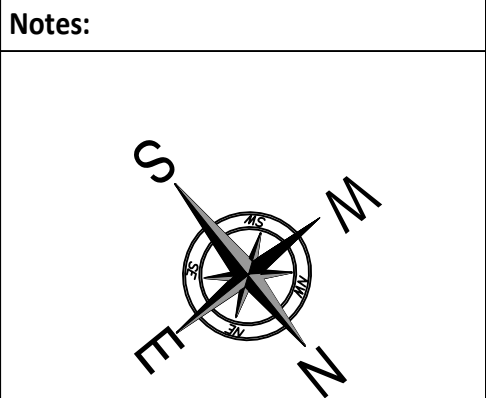

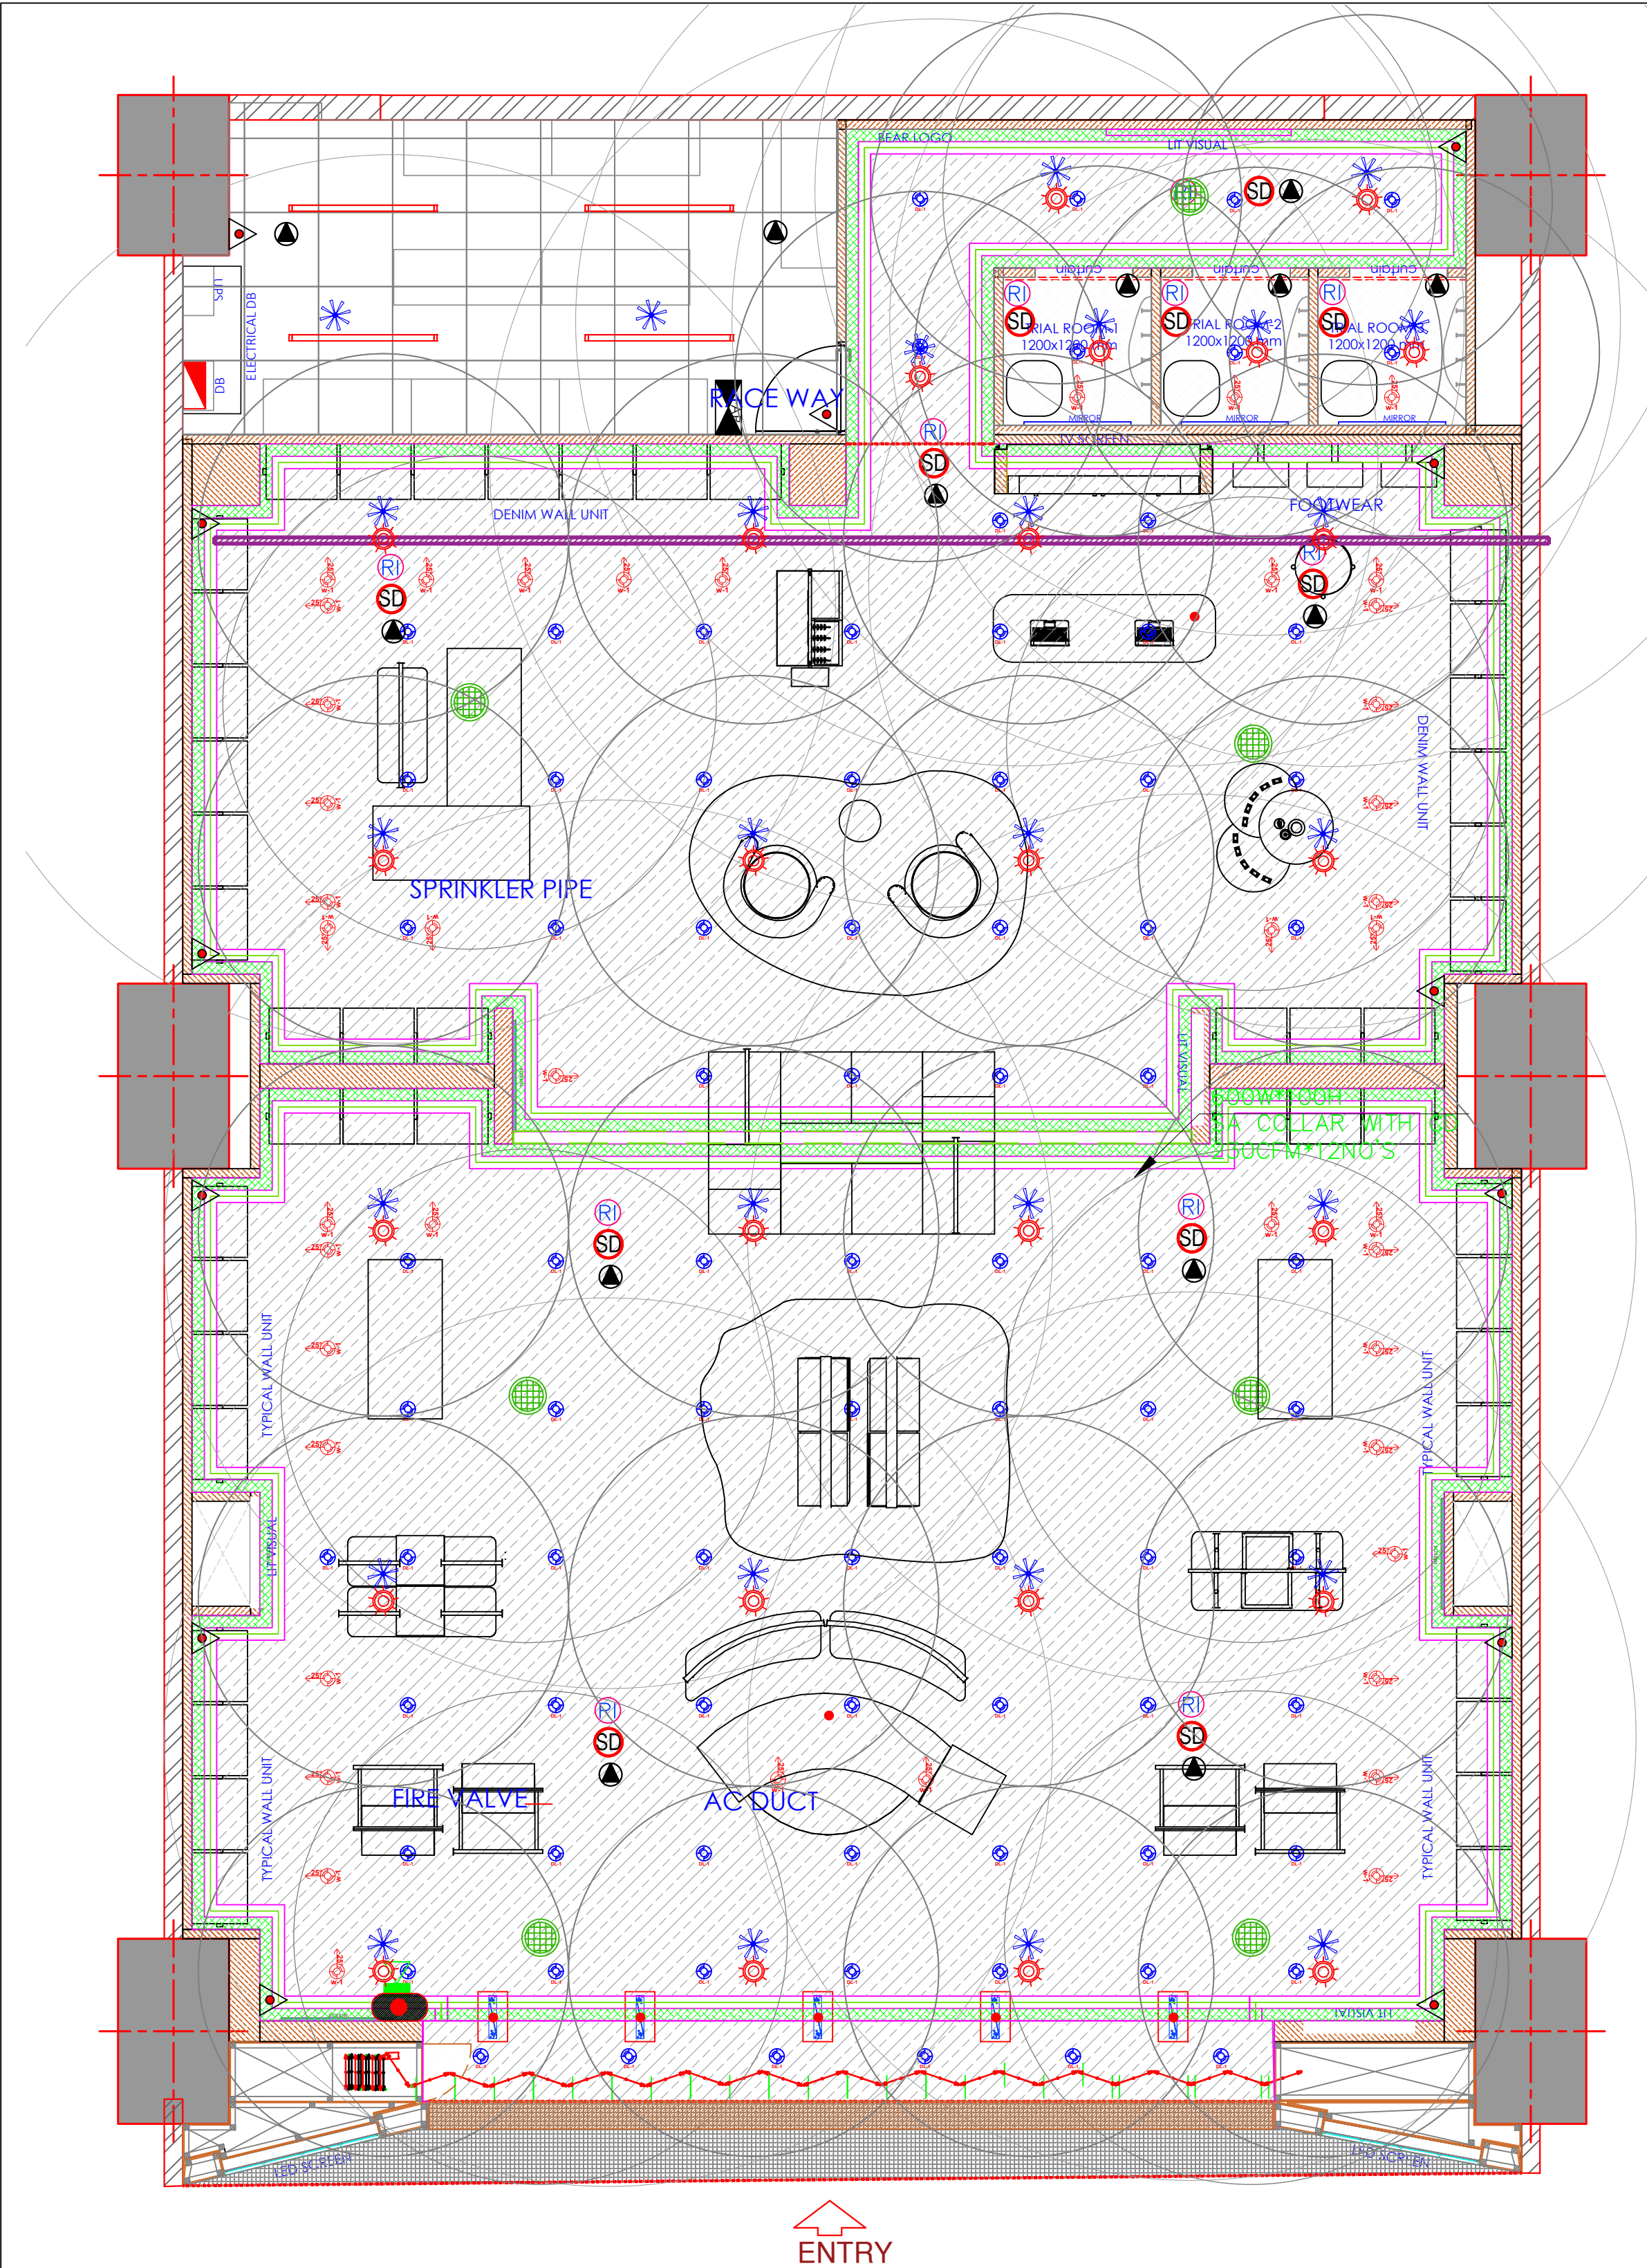

ENTRY

Lighting BOQ

S. NO.	SYB	PRODUCT DESCRIPTION	QTY
01		BOOM S 35W 40D RECESS MOUNTED LED WALL WASHER 4000K WHITE	31
02		XTRA M 35W 45D RECESS MOUNTED LED DOWNLIGHT 4000K WHITE	59
03		BOOM S 30W 40D RECESS MOUNTED LED WALL WASHER 4000K WHITE	02
04		XTRA M 30W 60D RECESS MOUNTED LED WALL WASHER 4000K WHITE	02
05		BEZEL 20W RECESSED LED DOWNLIGHT 4000K WHITE	00
06		NEON Strip 18W/Mt. Flexible Strip for Cove/light 4000K (in Mt.)-> 45 MTR	45 Mtr
07		SPAN 20W SURFACE MOUNT LED TUBE LIGHT - 4FT 4000K WHITE	04

LEGEND : CCTV


SINO	SYMBOL	DESCRIPTION	QTY.
1		HIK VISION MAKE ,INFRA RED ENABLED ONE HIGH RESOLUTION , FIXED 6.0MM LENS DOME CAMERA	06
2		FISH EYE CAMERA	00
3		BULLET-PROOF CAMERA FOR OUTSIDE	00
4		DVR UNIT	01

LEGEND : AUDIO

SINO	SYMBOL	DESCRIPTION	QTY.
1		CEILING MOUNTED SPEAKERS	07
2		SURFACE MOUNTED SPEAKERS	00
3		AMPLIFIER	01

LEGEND : FAS

SINO	SYMBOL	DESCRIPTION	QTY.
1		PROPOSED SMOKE DETECTOR BELOW FALSE CEILING	11
2		PROPOSED ABOVE FALSE CEILING SMOKE DETECTOR	13
3		RESPONSE INDICATOR	11
4		AUTOMATIC EXTINGUISHER CEILING MOUNTED	00
5		FIRE EXTINGUISHER CO2 5KG WITH AUTO GLOW SIGNAGE	01
6		MANUAL CALL POINT @ 1350MM FROM FFL(Break Glass Type)	01
7		HOOTER @ FALSE CEILING LEVEL	01
8		FIRE ALARM CONTROL PANEL-	01
9		FIRE EXTINGUISHER ABC 5KG WITH AUTO GLOW SIGNAGE	14
9		FIRE EXTINGUISHER DRY WITH AUTO GLOW SIGNAGE	00

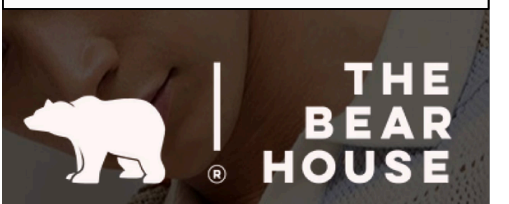

PACIFIC MALL
-
JAIPUR


Shop info

Market	INDIA
Province	RAJASTHAN
City	JAIPUR
City tier (tier 1/2/3)	TIER 2
Mall Name	PACIFIC MALL
New /Reno /Relo	NEW
STORE / SIS	STORE
Shop concept	THE BEAR HOUSE
Net size	1916 SQ FT
Slab height	5252 MM
B.O.B height	3769 MM

Drawing info


Title	RCP LAYOUT
Designed by	RISHAD
Checked by	
Date	28.04.2026
Revision	
Dwg no.	

Notes:

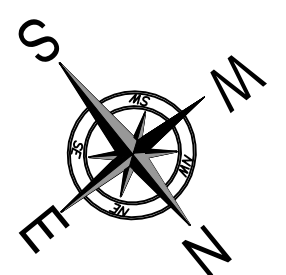

DRAIN PIPE NEEDS TO BE INSULATED WITH 6MM THICK RILE RUBBER. SLOPE 1:100

200Wx100H SA COLLAR WITH CONTROL DAMPER x 5NO'S 144CFM EACH

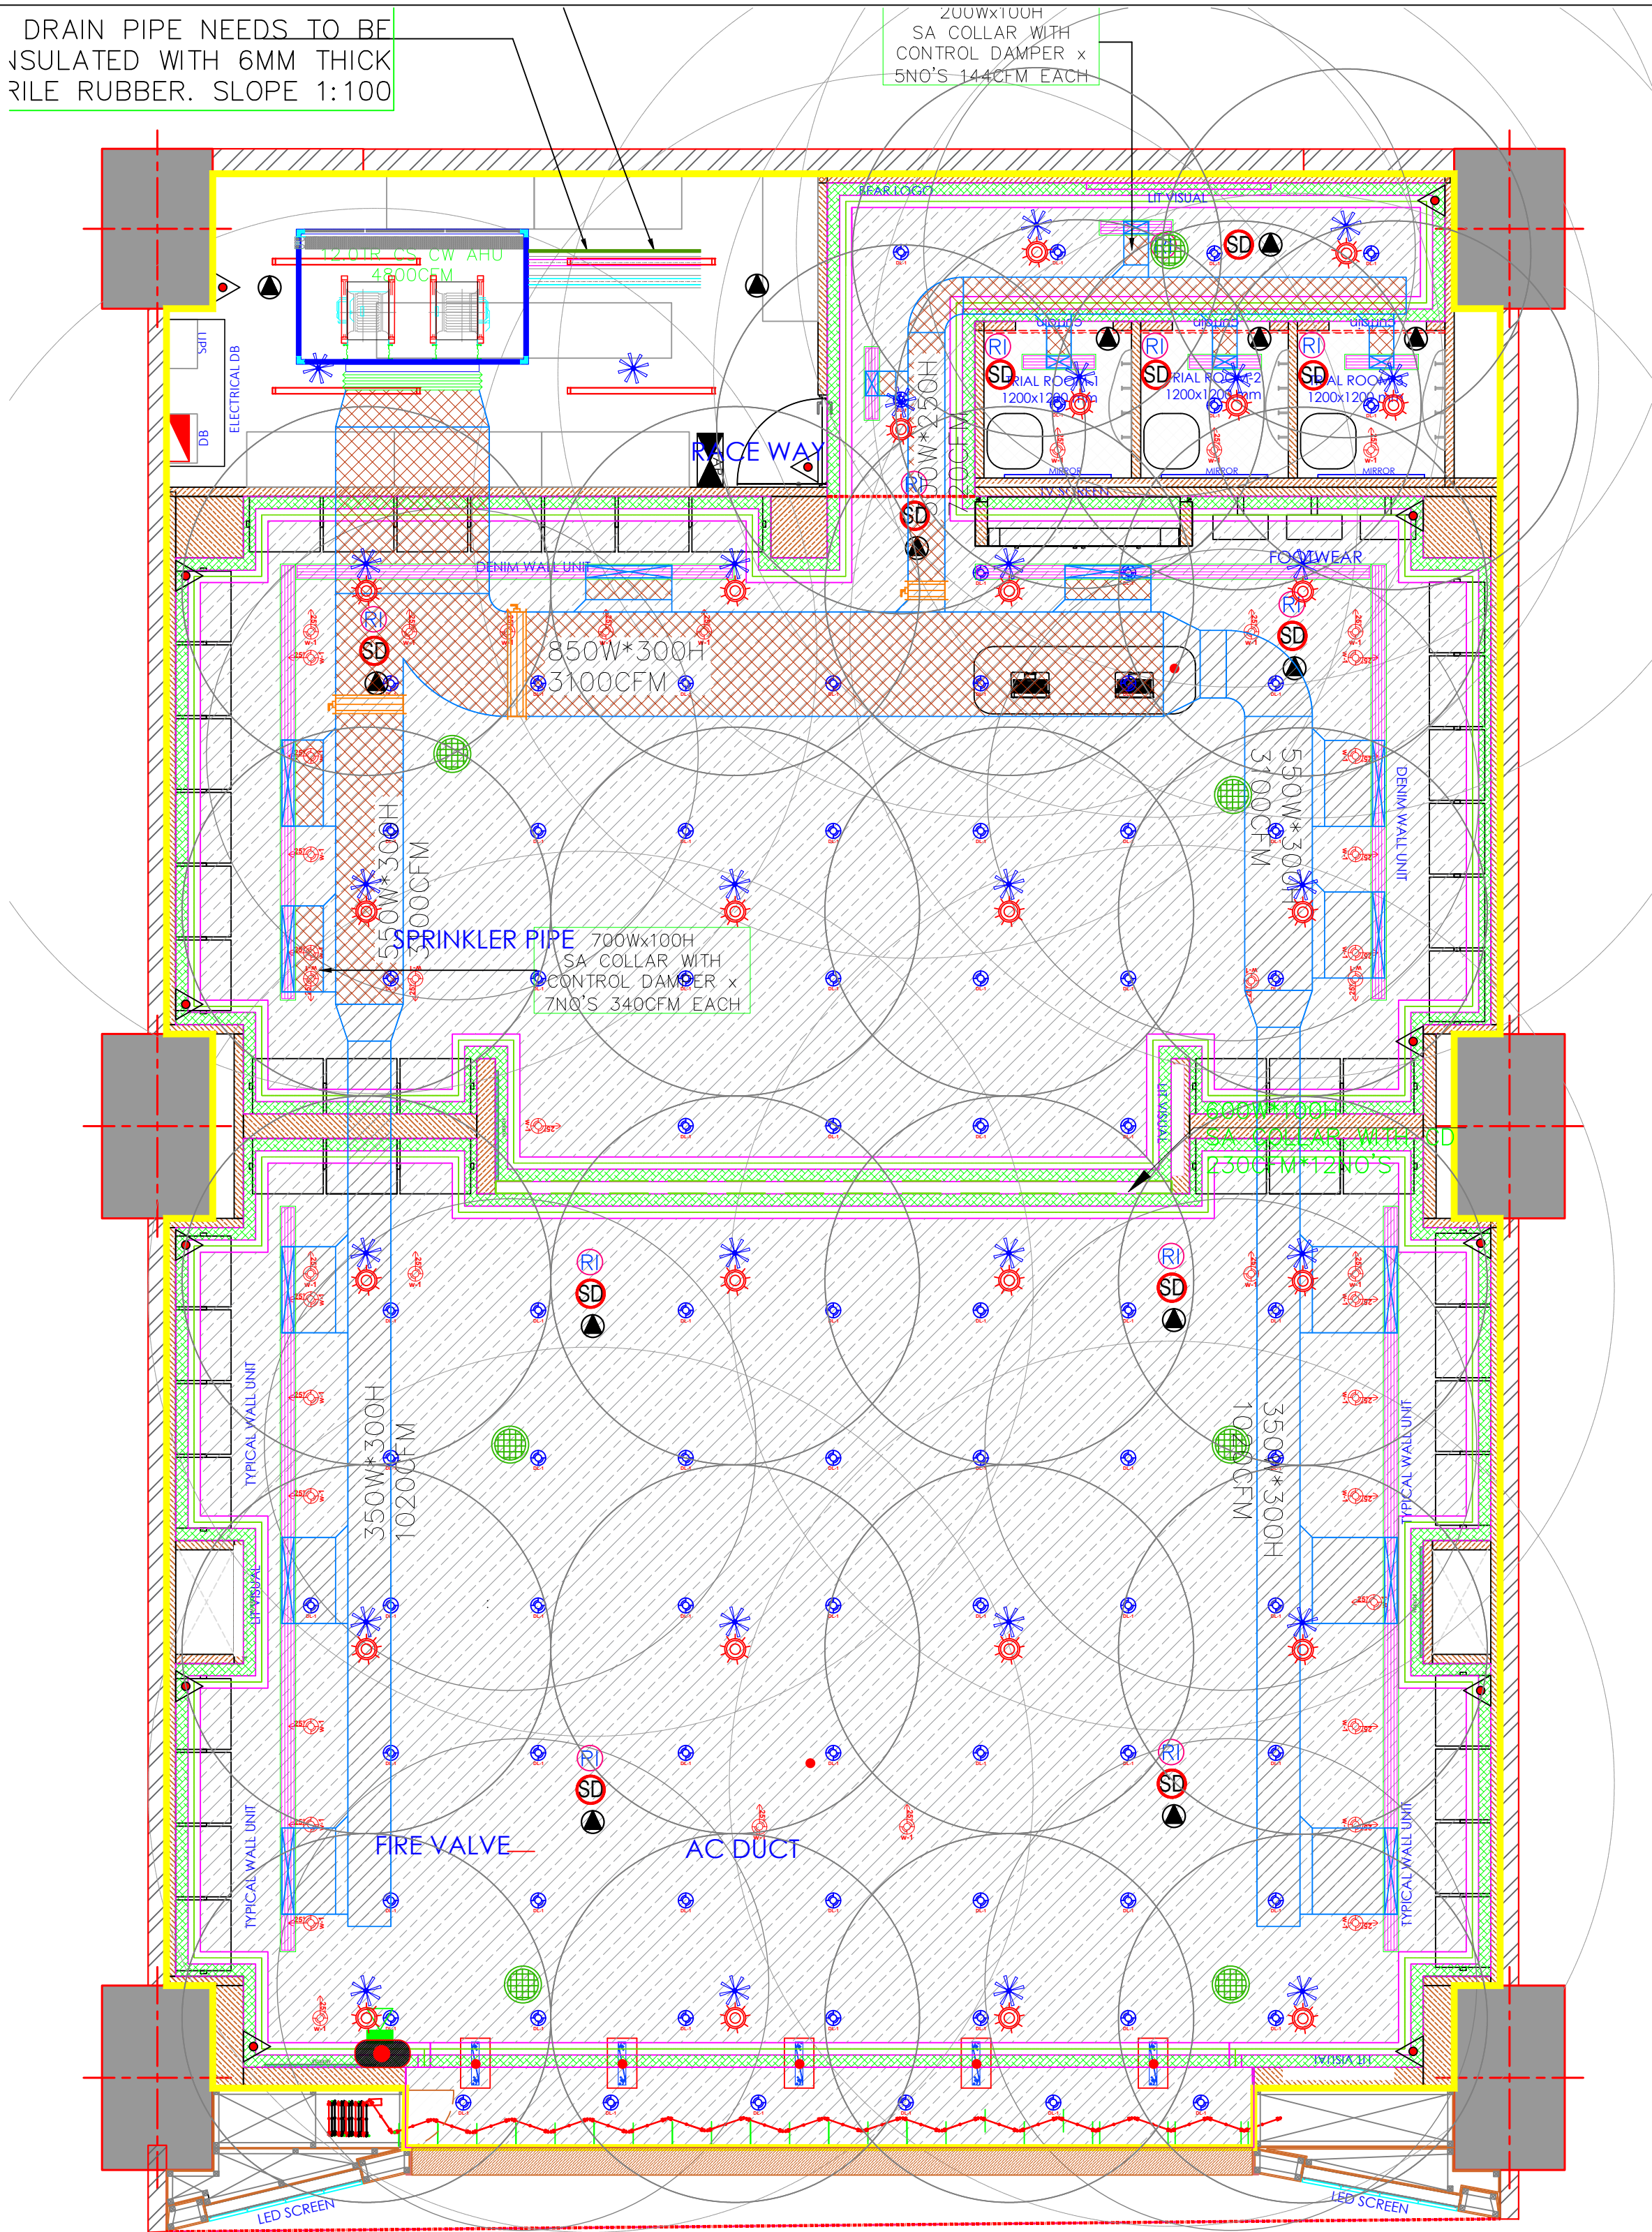

Lighting BOQ

S. NO.	SYB	PRODUCT DESCRIPTION	QTY
01		BOOM S 35W 40D RECESS MOUNTED LED WALL WASHER 4000K WHITE	31
02		XTRA M 35W 45D RECESS MOUNTED LED DOWNLIGHT 4000K WHITE	59
03		BOOM S 30W 40D RECESS MOUNTED LED WALL WASHER 4000K WHITE	02
04		XTRA M 30W 60D RECESS MOUNTED LED WALL WASHER 4000K WHITE	02
05		BEZEL 20W RECESSED LED DOWNLIGHT 4000K WHITE	00
06		NEON Strip 18W/Mt. Flexible Strip for Cove/light 4000K (in Mt.)-> 45 MTR	45 Mtr
07		SPAN 20W SURFACE MOUNT LED TUBE LIGHT - 4FT 4000K WHITE	04

LEGEND : CCTV

SINO	SYMBOL	DESCRIPTION	QTY.
1		HIK VISION MAKE ,INFRA RED ENABLED ONE HIGH RESOLUTION , FIXED 6.0MM LENS DOME CAMERA	06
2		FISH EYE CAMERA	00
3		BULLET-PROOF CAMERA FOR OUTSIDE	00
4		DVR UNIT	01

LEGEND : AUDIO

SINO	SYMBOL	DESCRIPTION	QTY.
1		CEILING MOUNTED SPEAKERS	07
2		SURFACE MOUNTED SPEAKERS	00
3		AMPLIFIER	01

LEGEND : FAS

SINO	SYMBOL	DESCRIPTION	QTY.
1		PROPOSED SMOKE DETECTOR BELOW FALSE CEILING	11
2		PROPOSED ABOVE FALSE CEILING SMOKE DETECTOR	13
3		RESPONSE INDICATOR	11
4		AUTOMATIC EXTINGUISHER CEILING MOUNTED	00
5		FIRE EXTINGUISHER CO2 5KG WITH AUTO GLOW SIGNAGE	01
6		MANUAL CALL POINT @ 1350MM FROM FFL(Break Glass Type)	01
7		HOOTER @ FALSE CEILING LEVEL	01
8		FIRE ALARM CONTROL PANEL-	01
9		FIRE EXTINGUISHER ABC 5KG WITH AUTO GLOW SIGNAGE	14
9		FIRE EXTINGUISHER DRY WITH AUTO GLOW SIGNAGE	00



PACIFIC MALL - JAIPUR

Shop info

Market	INDIA
Province	RAJASTHAN
City	JAIPUR
City tier (tier 1/2/3)	TIER 2
Mall Name	PACIFIC MALL
New /Reno /Relo	NEW
STORE / SIS	STORE
Shop concept	THE BEAR HOUSE
Net size	1916 SQ. FT
Slab height	5252 MM
B.O.B height	3769 MM

Drawing info

Title	RCP LAYOUT
Designed by	RISHAD
Checked by	
Date	28.04.2026
Revision	
Dwg no.	

Notes:

