



SUREENA CHOWDHRI
(GFC SET 01)(R2)

Date: MARCH 27, 2026

PROJECT DRAWING LIST				
PROJECT NAME		SUREEN CHOWDHRI		
LOCATION		JAIPUR		
CARPET AREA (in SFT)		957		
Sl. No.	Drawing List	DWG.NO	STATUS	REMARKS
A	FIRST CUT FURNITURE LAYOUT			
1	Layout Approved	1	Attached	
B	ARCHITECTURAL DRAWINGS(1st SET)			
1	BARE SHELL	1	Attached	
2	FIXTURE LAYOUT	2	Attached	
3	POWER POINT LAYOUT	3	Attached	
4	PARTITION LAYOUT	4	Attached	
5	FALSE CEILING	5	Attached	
6	FALSE CEILING WITH FURNITURE	6	Attached	
7	FC SECTION	7	Attached	
8	FLOORING	8	Attached	
9	HVAC Layout	9	Attached	
10	LIGHTING	10	Attached	
11	LIGHTING WITH FURNITURE	11	Attached	
12	CCTV	12	Attached	
13	AUDIO	13	Attached	
14	FAS	14	Attached	
15	RCP	15	Attached	
C	ARCHITECTURAL DRAWINGS(2nd SET)			
16	ELEVATION 1	16	Attached	
17	ELEVATION 2	17	Attached	
18	ELEVATION 3	18	Attached	
19	ELEVATION 4	19	Attached	
20	ELEVATION 5	20	Attached	
21	ELEVATION 6	21	Attached	
22	FAÇADE	22	Attached	



Sureena Chowdhri
-
Jaipur

Brand Info

Shop info


Market	INDIA
Province	RAJASTHAN
City	JAIPUR
City tier (tier 1/2/3)	TIER 1
Mall Name	HIGH STREET
New /Reno /Relo	NEW
FSS / SIS	FSS
Shop concept	SUREENA CHOWDHRI
Net size	957 SFT
Slab height	4395MM
B.O.B height	4267MM


Drawing info

Title	
Designed by	RISHAD
Checked by	SOUMYA
Date	
Revision	R1
Dwg no.	

Notes:

Direction:

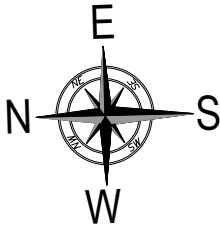

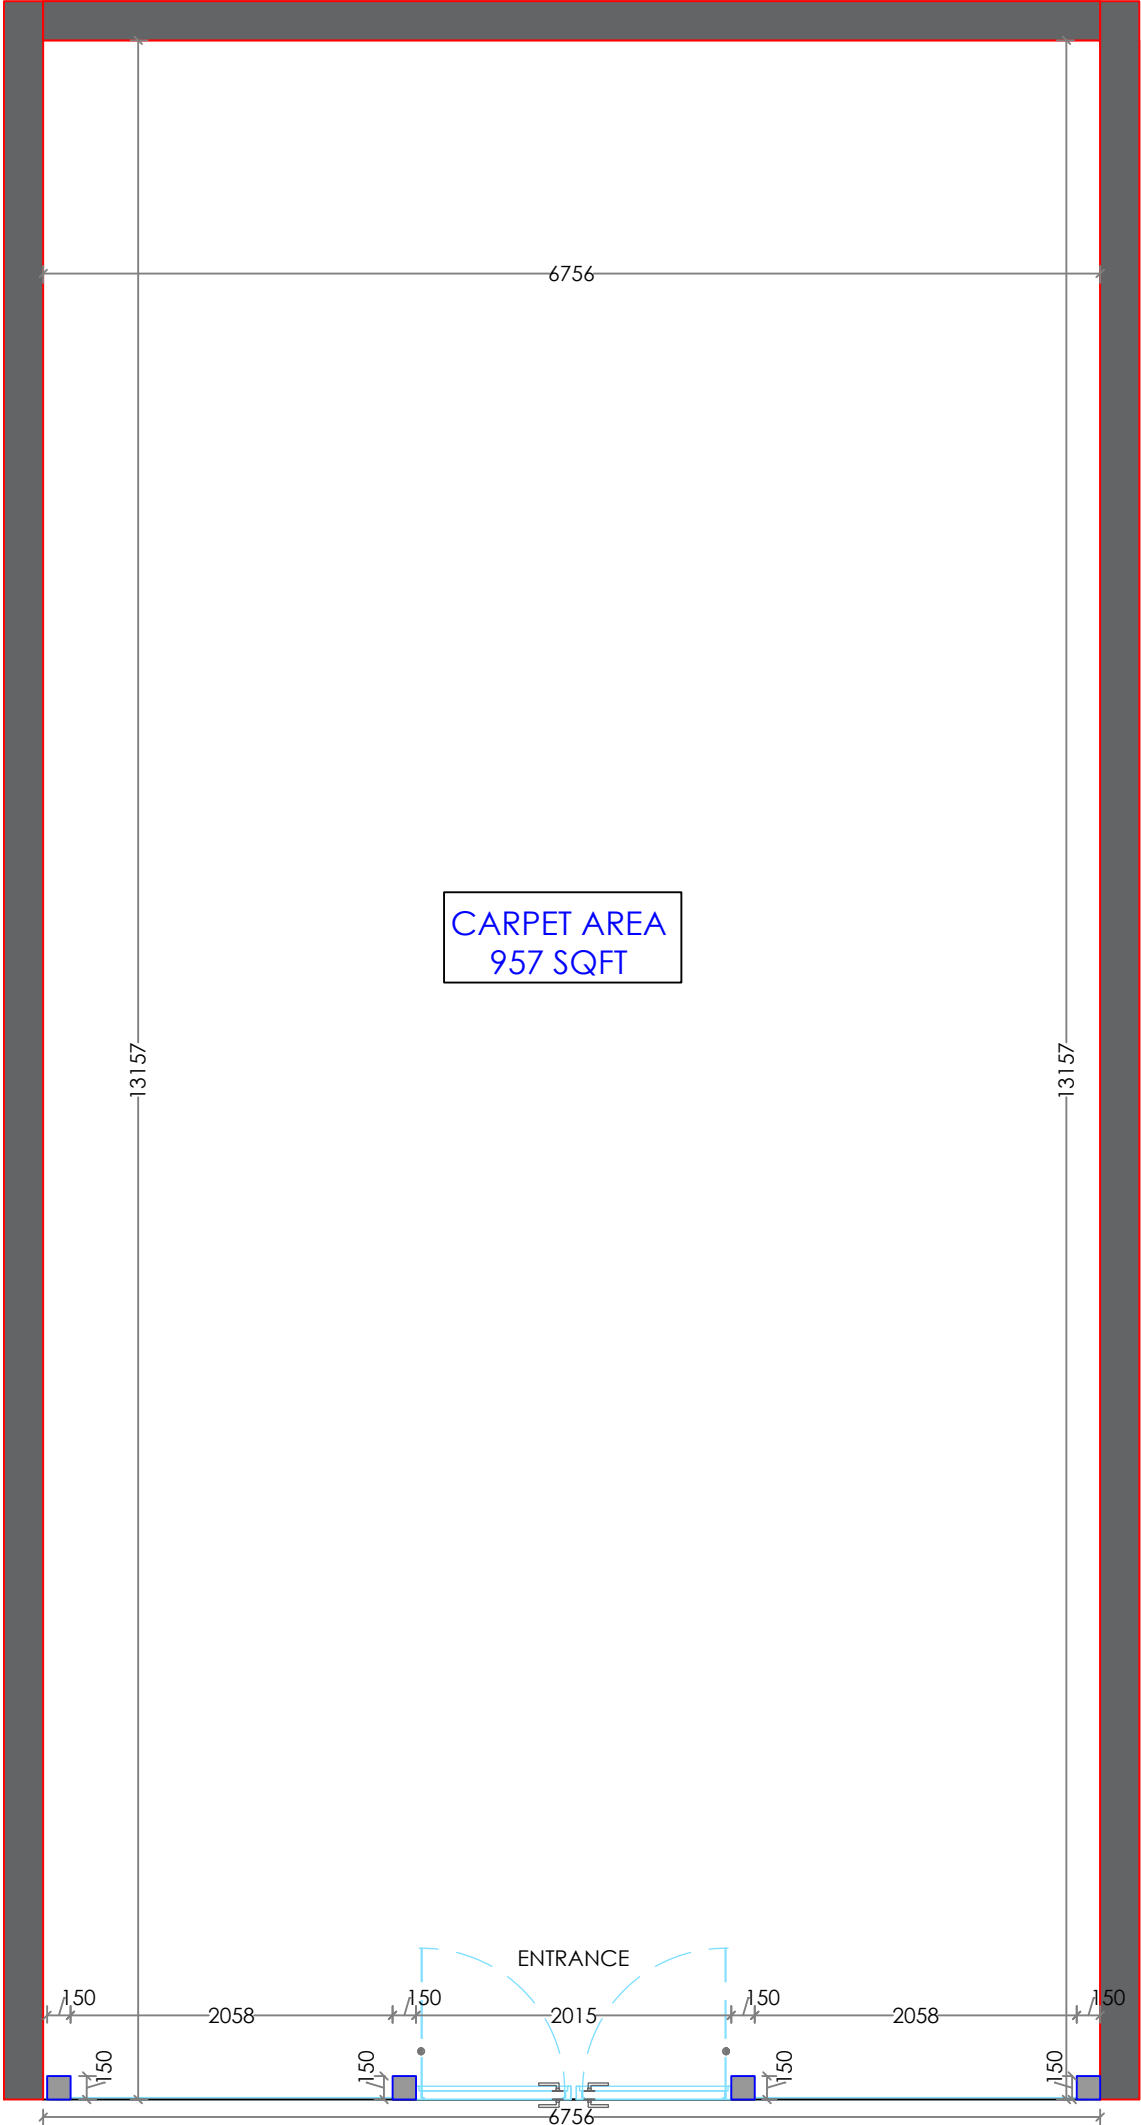

Sureena Chowdhri
-
Jaipur

Brand Info

Shop info


Market	INDIA
Province	RAJASTHAN
City	JAIPUR
City tier (tier 1/2/3)	TIER 1
Mall Name	HIGH STREET
New /Reno /Relo	NEW
FSS / SIS	FSS
Shop concept	SUREENA CHOWDHRI
Net size	957 SFT
Slab height	4395MM
B.O.B height	4267MM


Drawing info

Title	EXISTING LAYOUT
Designed by	RISHAD
Checked by	SOUMYA
Date	
Revision	R1
Dwg no.	01

Notes:

Direction:

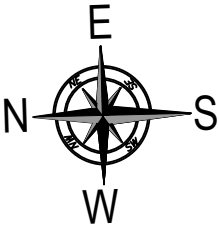

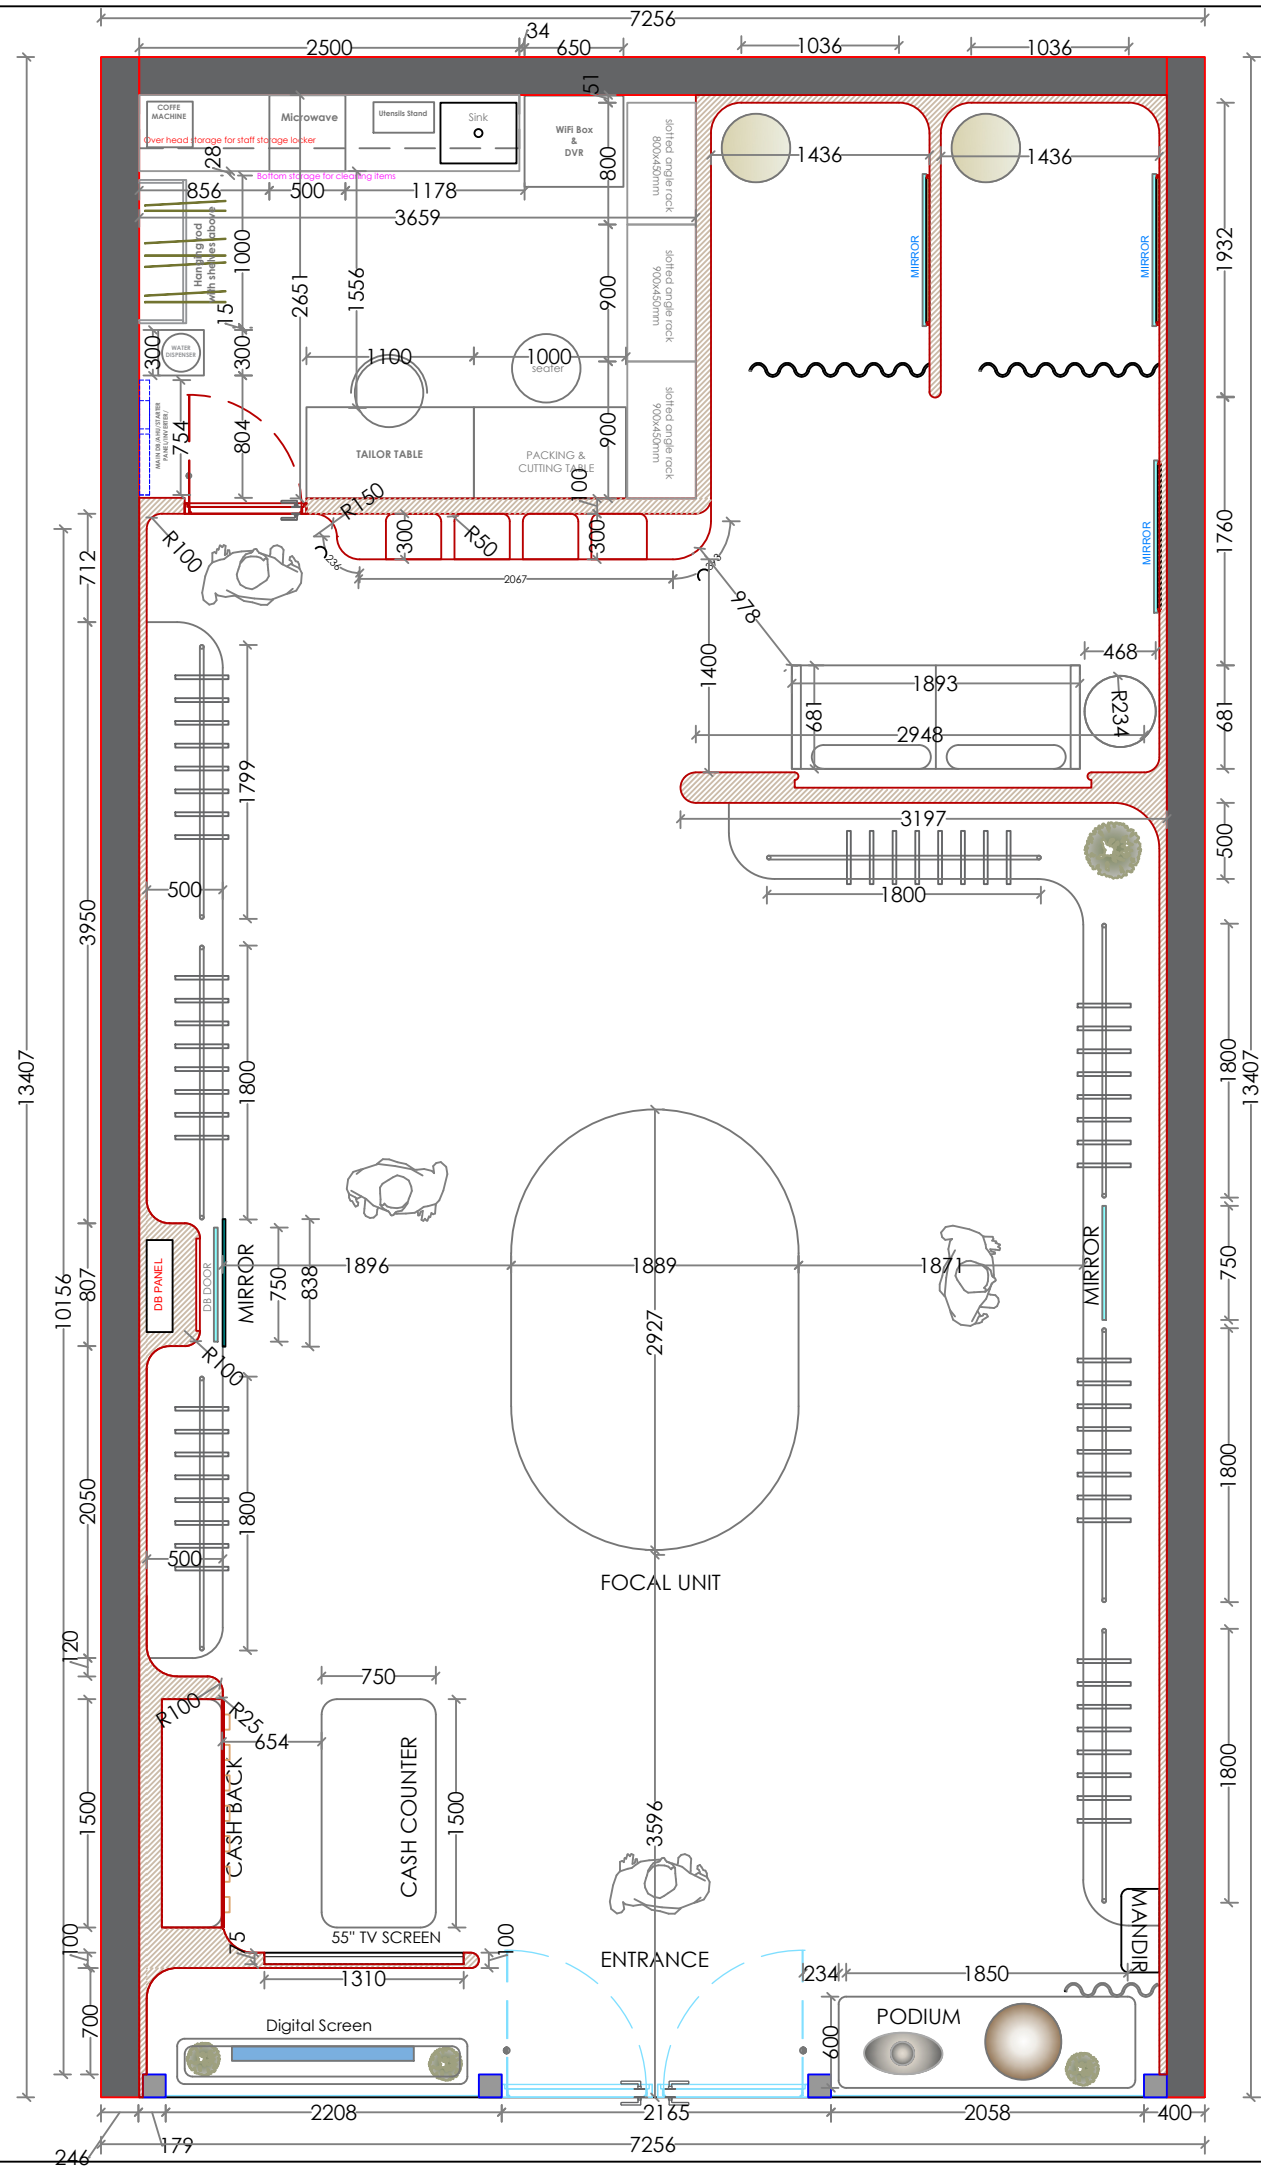

Sureena Chowdhri
-
Jaipur

Brand Info

Shop info


Market	INDIA
Province	RAJASTHAN
City	JAIPUR
City tier (tier 1/2/3)	TIER 1
Mall Name	HIGH STREET
New /Reno /Relo	NEW
FSS / SIS	FSS
Shop concept	SUREENA CHOWDHRI
Net size	957 SFT
Slab height	4395MM
B.O.B height	4267MM


Drawing info

Title	FIXTURE LAYOUT
Designed by	RISHAD
Checked by	SOUMYA
Date	
Revision	R1
Dwg no.	02

Notes:

Direction:

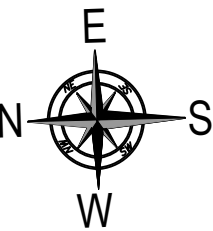

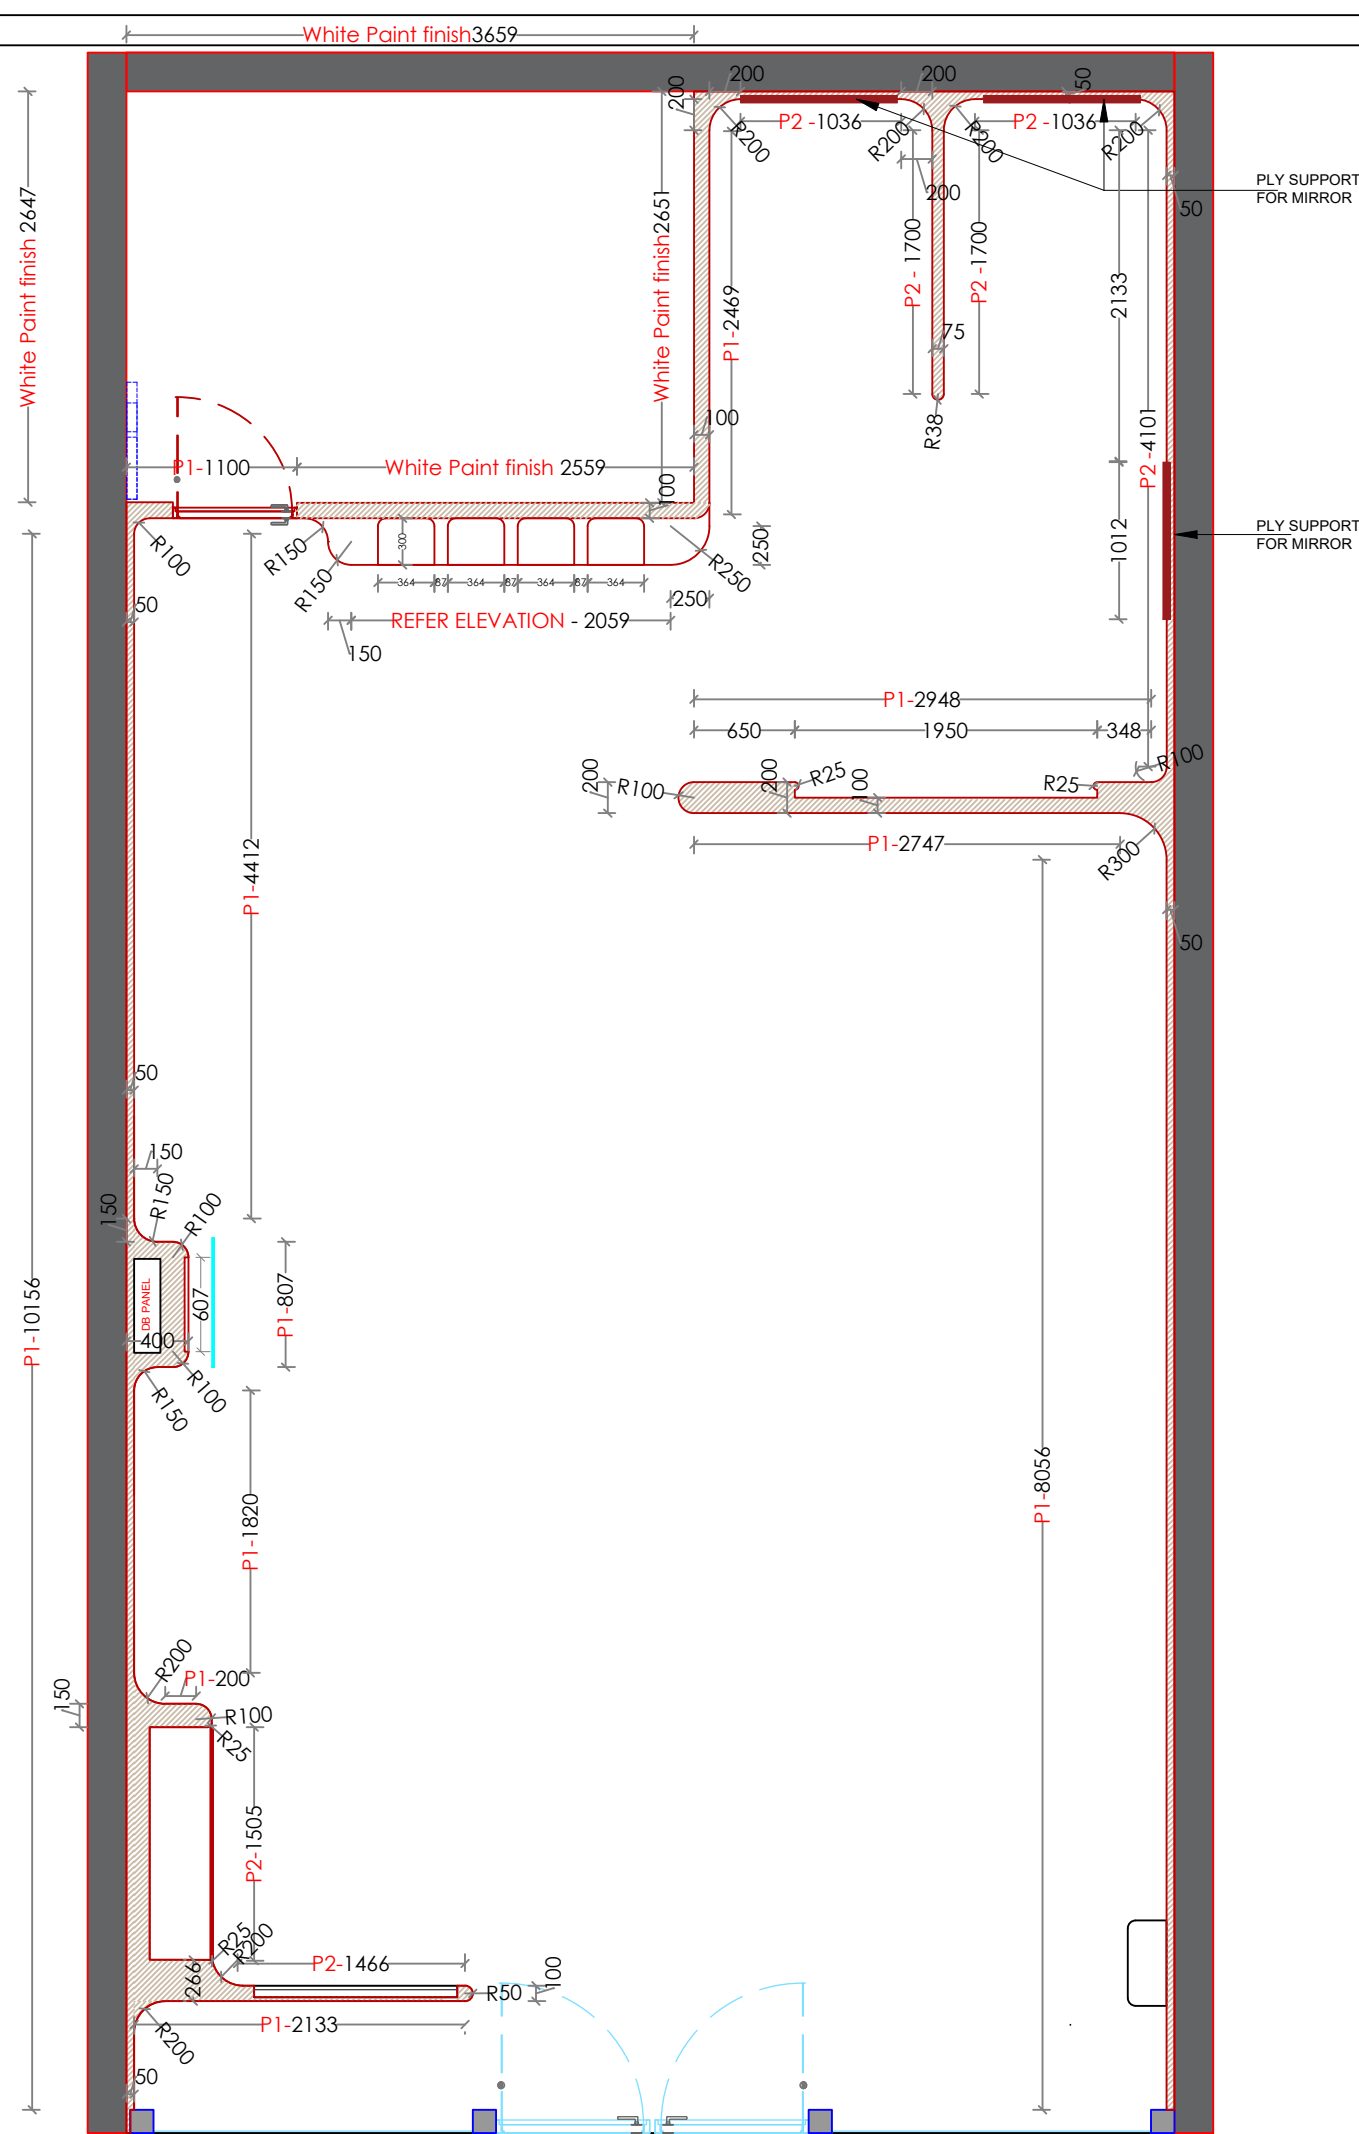

PARTITION LEGEND

SL.NO	SYMBOL	DESCRIPTION
P1		P1 - PARTITION FRAMEWORK (50 x 50mm GI FRAME WORK UP TO TRUE CEILING HORIZONTALS @ 600MM C/C & VERTICALS @ 450MM C/C) WITH 12MM THICK GYPSUM CLADDING AND 600X600MM PLY SUPPORT ONLY FOR WALL FIXTURES AS MENTIONED IN ELEVATIONS.
P2		PARTITION FRAMEWORK (50 x 50mm GI FRAME WORK UP TO TRUE CEILING HORIZONTALS @ 600MM C/C & VERTICALS @ 450MM C/C) WITH ONLY 12MM THICK GYPSUM CLADDING.
P3		POP punning
P4		12mm thk. MDF +Gypsumcladding up to 150mm above false ceiling from ffl. (For finishes Refer surface finishes layout)

NOTE: PLEASE
CROSSCHECK PARTITION
THICKNESS BEFORE
EXCECUTION



Sureena Chowdhri
-
Jaipur

Brand Info

Shop info


Market	INDIA
Province	RAJASTHAN
City	JAIPUR
City tier (tier 1/2/3)	TIER 1
Mall Name	HIGH STREET
New /Reno /Relo	NEW
FSS / SIS	FSS
Shop concept	SUREENA CHOWDHRI
Net size	957 SFT
Slab height	4395MM
B.O.B height	4267MM


Drawing info


Title	PARTITION LAYOUT
Designed by	RISHAD
Checked by	SOUMYA
Date	
Revision	R1
Dwg no.	04


Notes:

Direction:

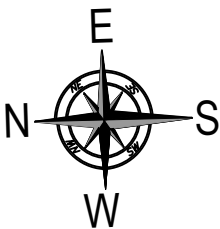

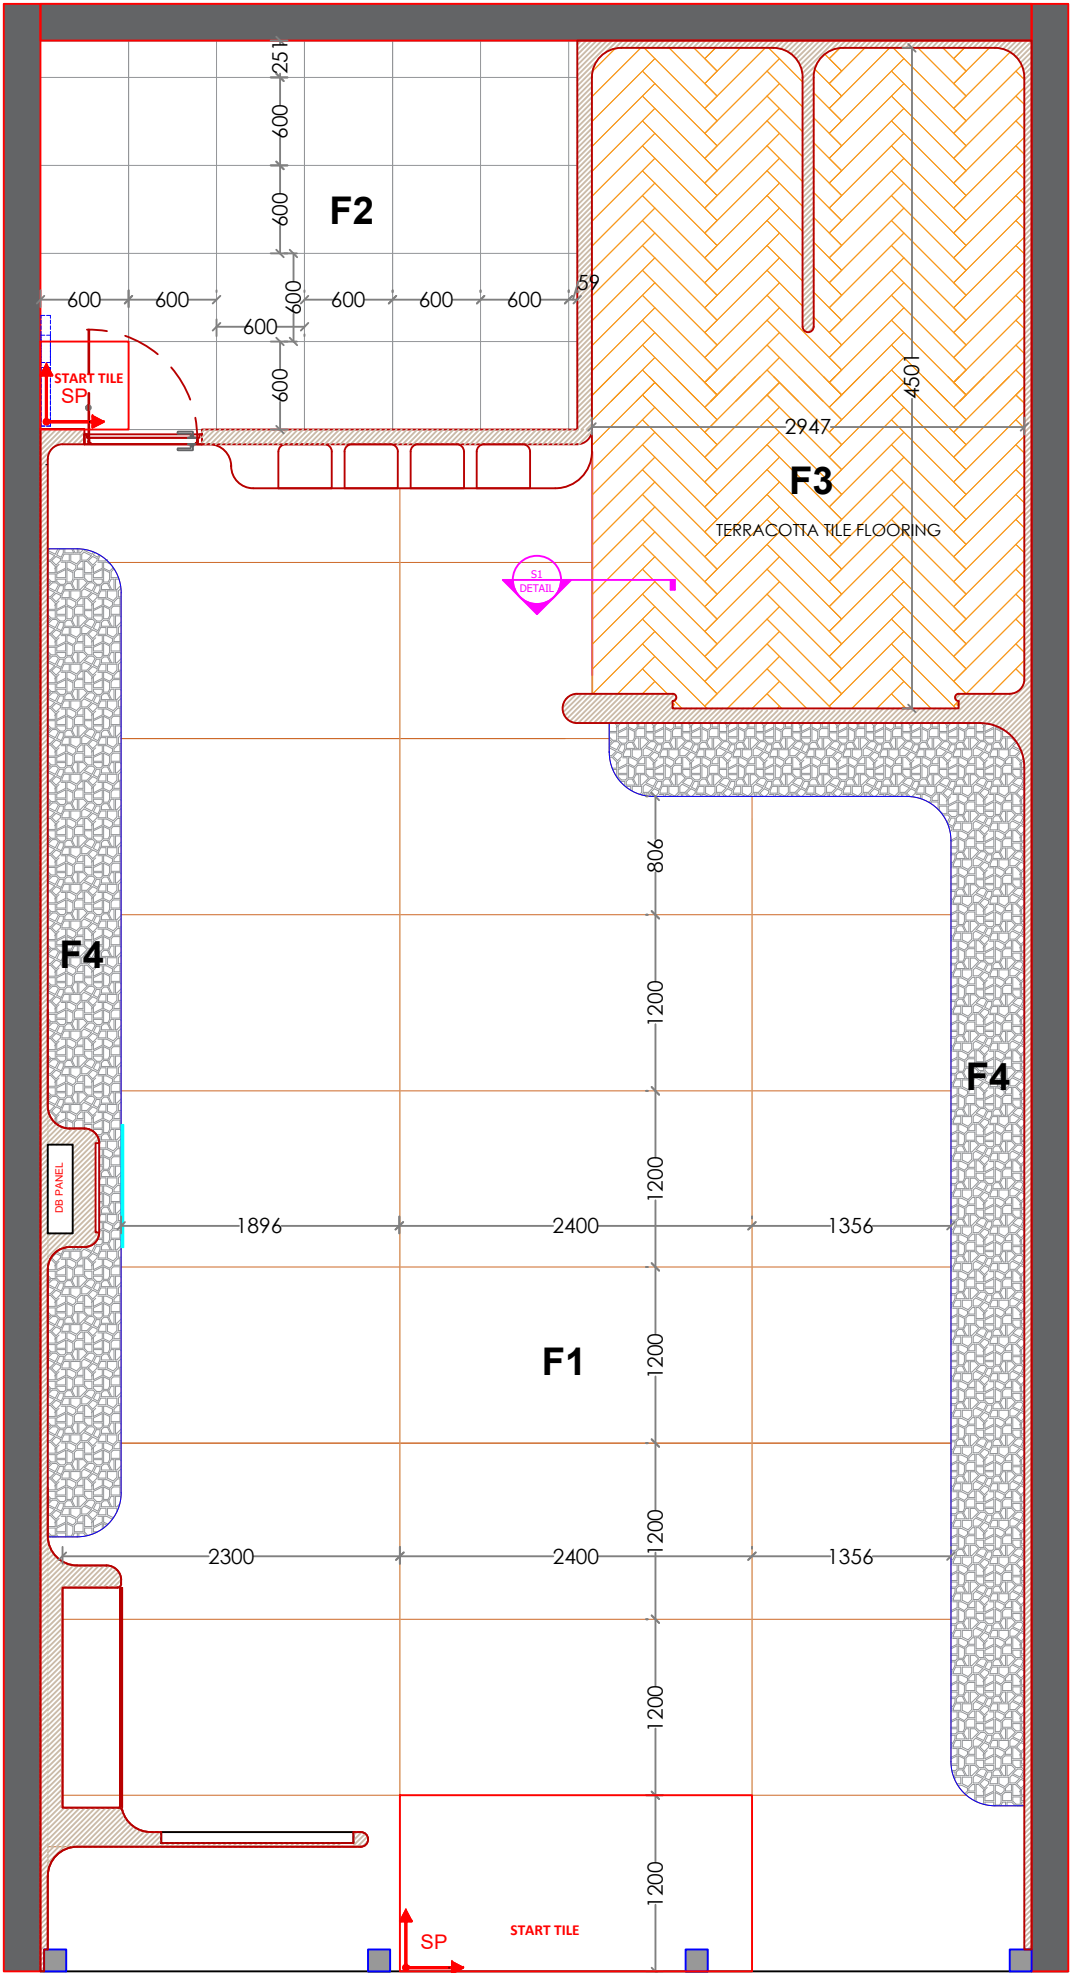

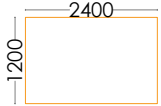FLOORING LEGEND			QTY	+10%
	REF.	DESCRIPTION		
F1		1200MMX2400MM VETRIFIED FLOORING MAKE - NEXION ENDLESS BEIGE (QTY INCLUDING RETAI+ WINDOW DISPLAY)	573 SFT	631 SFT
F2		BOH FLOORING	105 SFT	116 SFT
F3		TERRACOTTA TILE FLOORING	140 SFT	154 SFT
F4		DESIGNER MOSAIC FLOORING.	85 SFT	94 SFT

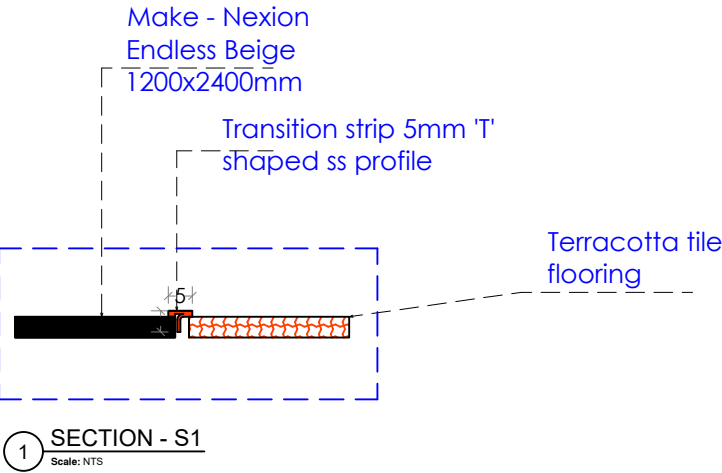

Sureena Chowdhri
-
Jaipur

Brand Info

Shop info


Market	INDIA
Province	RAJASTHAN
City	JAIPUR
City tier (tier 1/2/3)	TIER 1
Mall Name	HIGH STREET
New /Reno /Relo	NEW
FSS / SIS	FSS
Shop concept	SUREENA CHOWDHRI
Net size	957 SFT
Slab height	4395MM
B.O.B height	4267MM


Drawing info

Title	FLOORING LAYOUT
Designed by	RISHAD
Checked by	SOUMYA
Date	
Revision	R1
Dwg no.	08

Notes:


Direction:

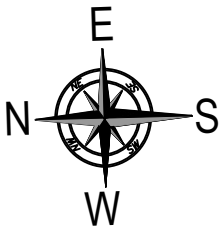

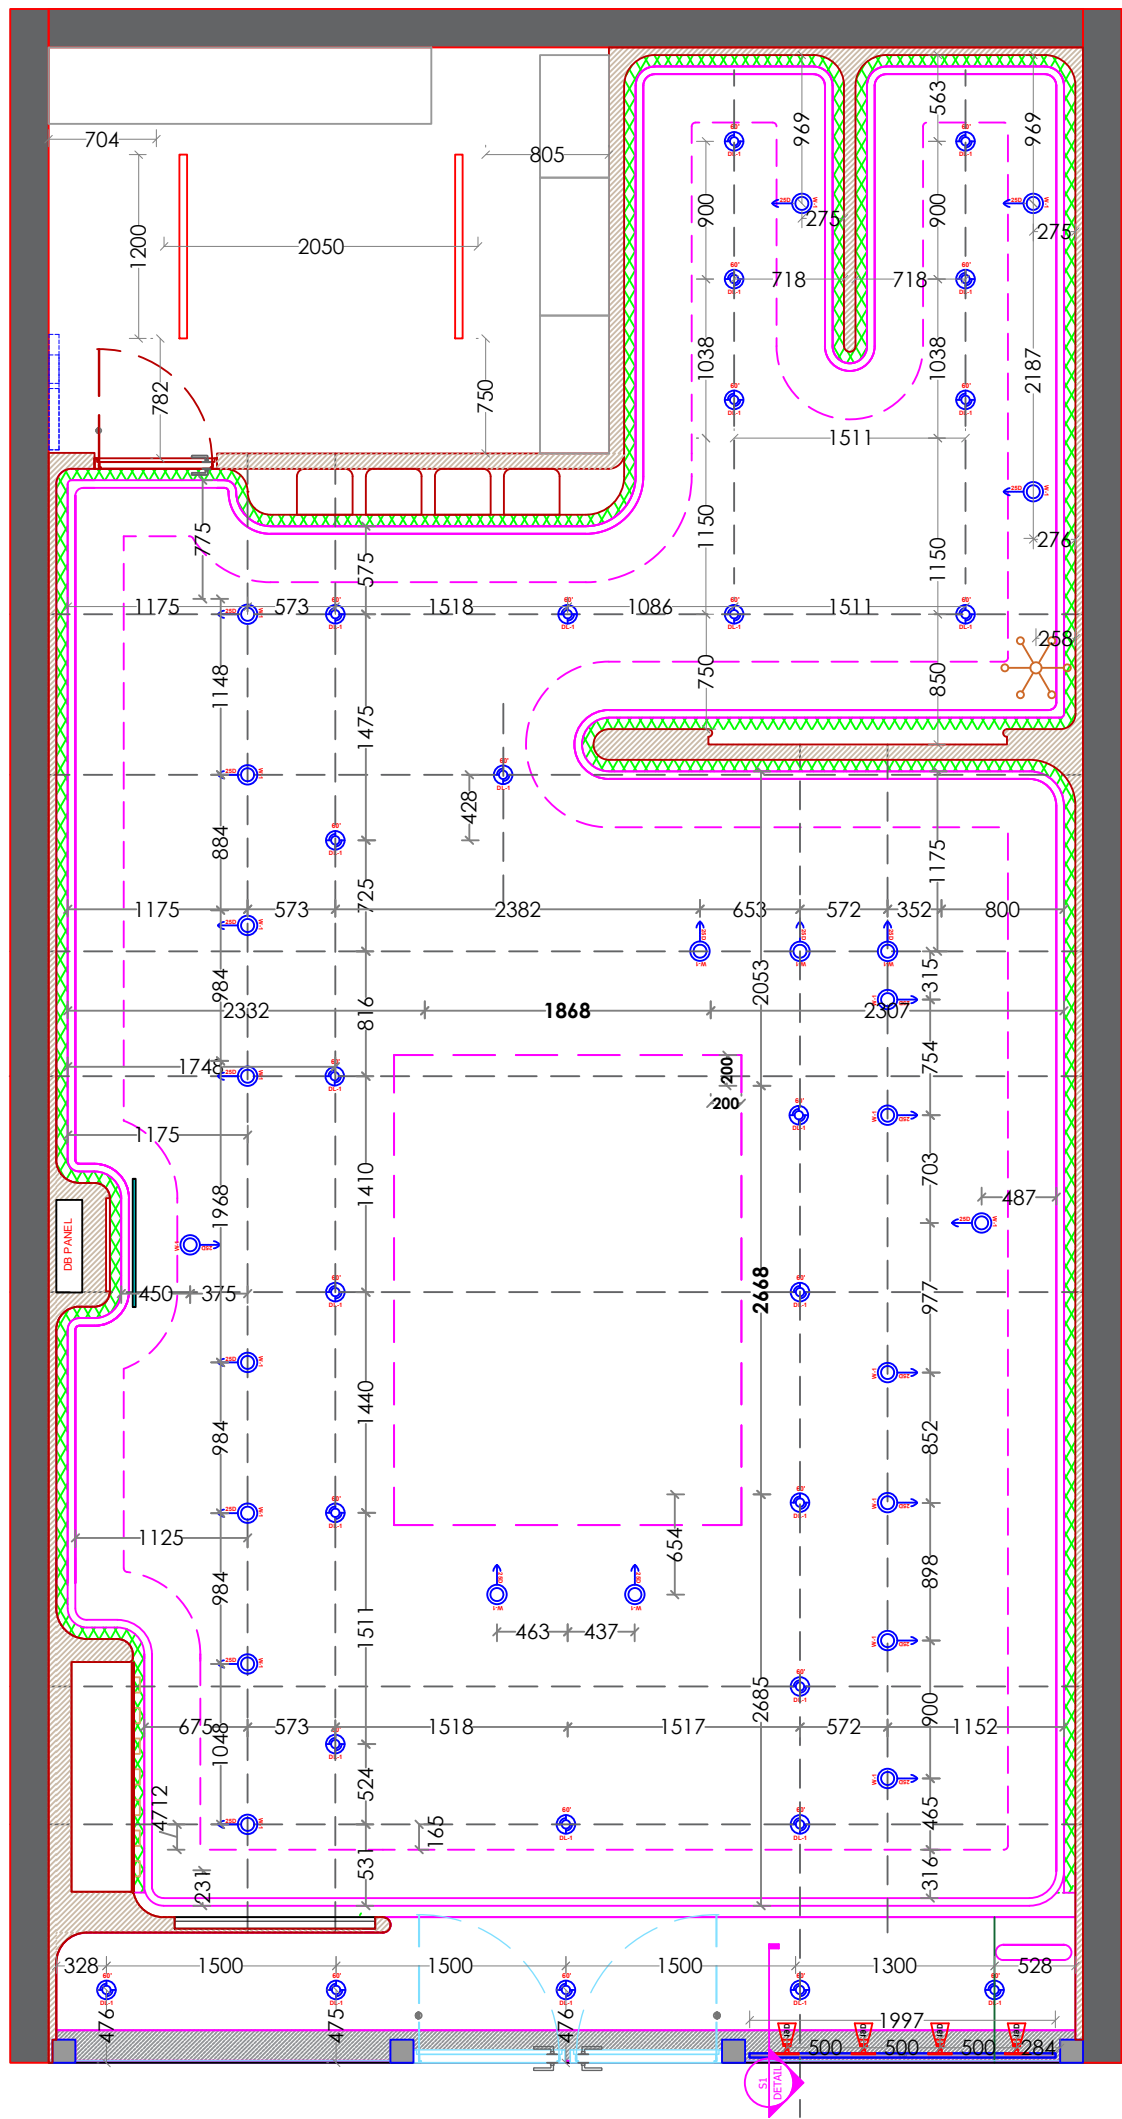

Lighting BOQ

S. NO.	SYB	PRODUCT DESCRIPTION	QTY
01		AVIO NX 30W 25D RECESS MOUNTED LED WALL WASHER -3000K - FIXTURE COLOR-WHITE	25
02		XTRA M 30W 60D RECESS MOUNTED LED DOWNLIGHT - 3000K - FIXTURE COLOR-WHITE	28
03		CANE 30W 24D LED TRACK SPOT-3000K - FIXTURE COLOR-WHITE	04
04		DECORATIVE LIGHT	01
05		SPAN 20W LED TUBELIGHT - 4FT	02

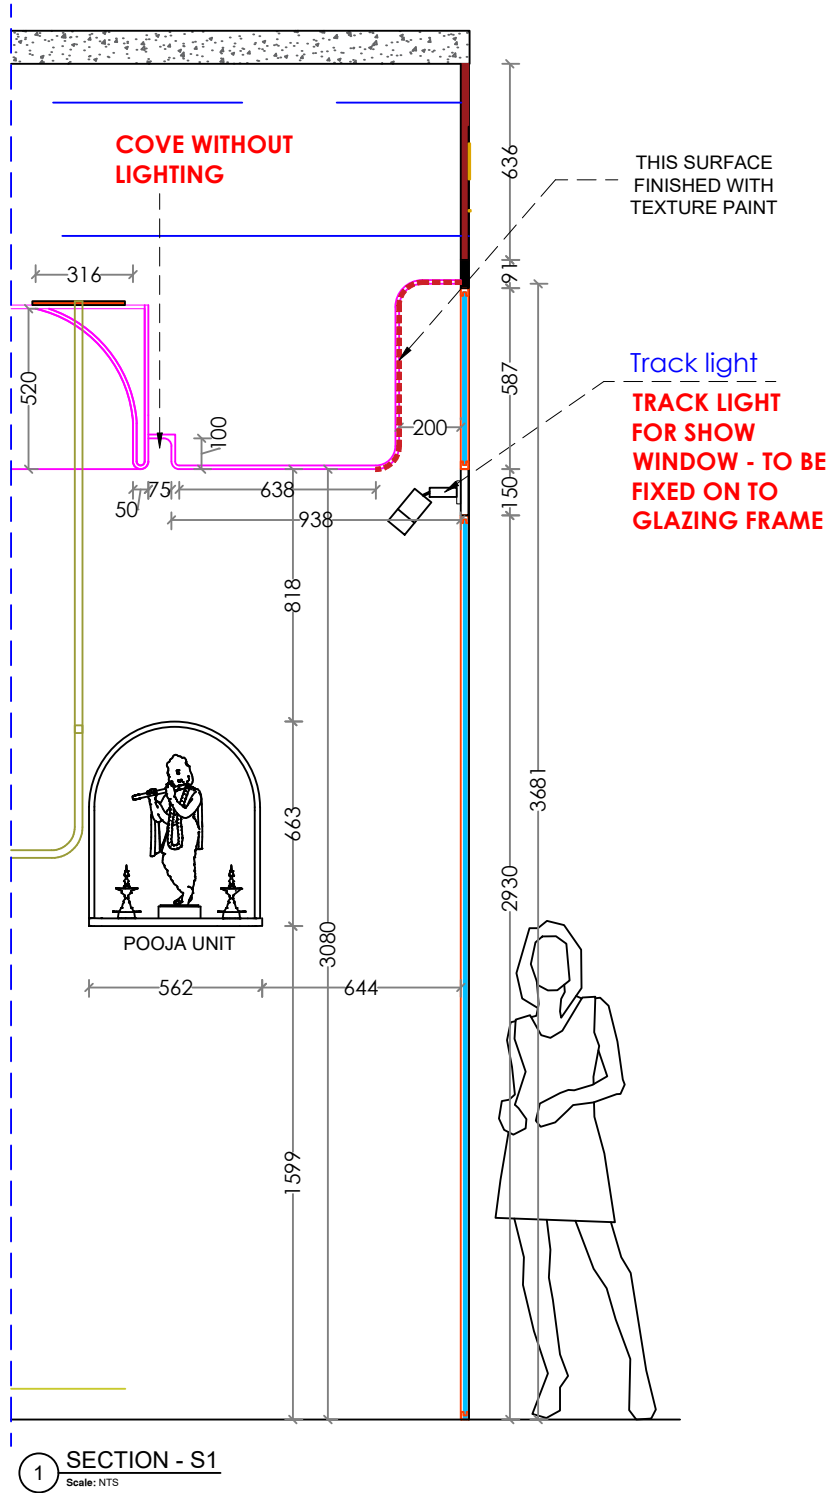

Sureena Chowdhri
-
Jaipur

Brand Info

Shop info

Market	INDIA
Province	RAJASTHAN
City	JAIPUR
City tier (tier 1/2/3)	TIER 1
Mall Name	HIGH STREET
New /Reno /Relo	NEW
FSS / SIS	FSS
Shop concept	SUREENA CHOWDHRI
Net size	957 SFT
Slab height	4395MM
B.O.B height	4267MM


Drawing info

Title	LIGHTING LAYOUT
Designed by	RISHAD
Checked by	SOUMYA
Date	
Revision	R1
Dwg no.	10

Notes:

Direction:



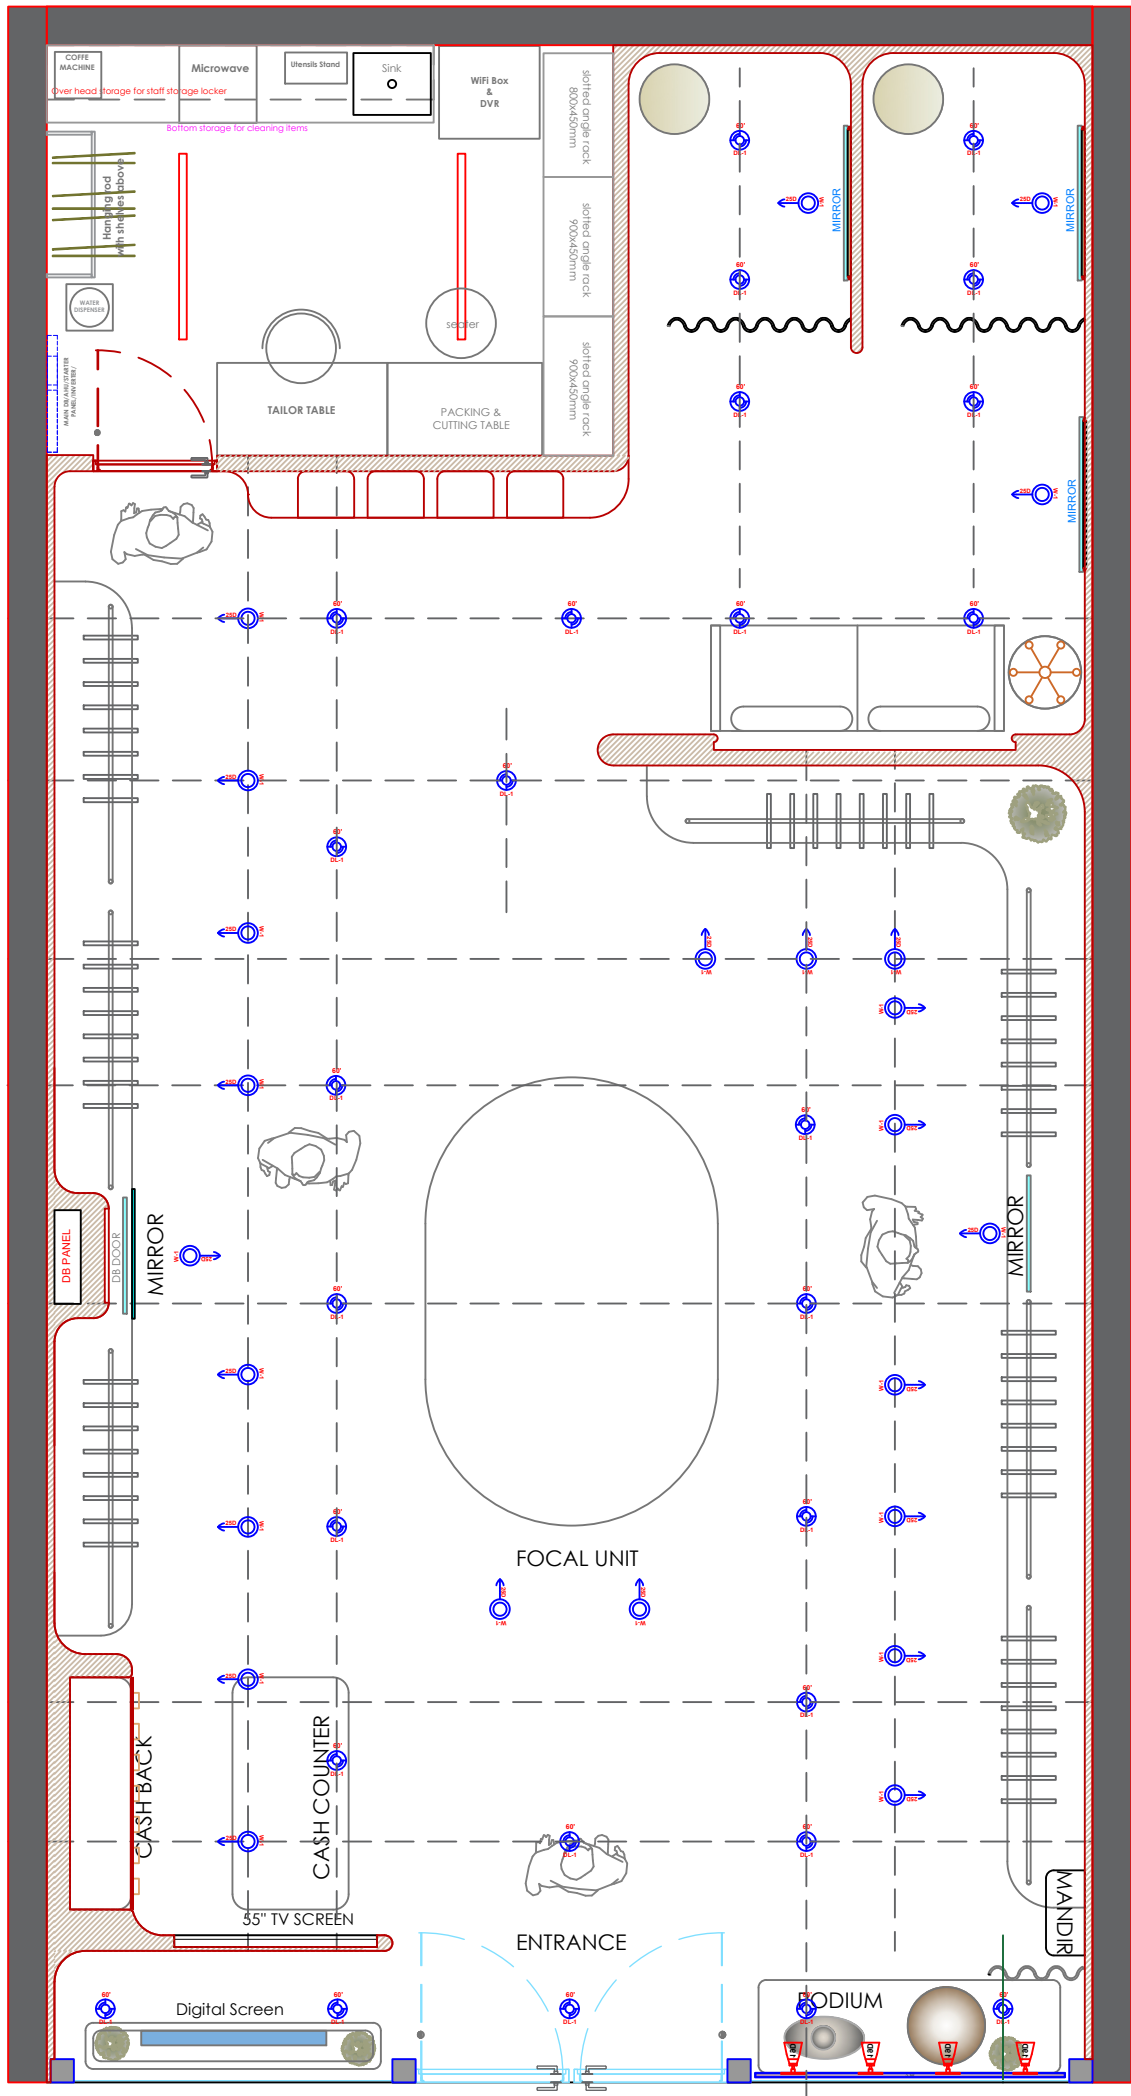

Lighting BOQ

S. NO.	SYB	PRODUCT DESCRIPTION	QTY
01		AVIO NX 30W 25D RECESS MOUNTED LED WALL WASHER -3000K - FIXTURE COLOR-WHITE	25
02		XTRA M 30W 60D RECESS MOUNTED LED DOWNLIGHT - 3000K - FIXTURE COLOR-WHITE	28
03		CANE 30W 24D LED TRACK SPOT-3000K - FIXTURE COLOR-WHITE	04
04		DECORATIVE LIGHT	01
05		SPAN 20W LED TUBELIGHT - 4FT	02



Sureena Chowdhri
-
Jaipur

Brand Info

Shop info


Market	INDIA
Province	RAJASTHAN
City	JAIPUR
City tier (tier 1/2/3)	TIER 1
Mall Name	HIGH STREET
New /Reno /Relo	NEW
FSS / SIS	FSS
Shop concept	SUREENA CHOWDHRI
Net size	957 SFT
Slab height	4395MM
B.O.B height	4267MM


Drawing info

Title	LIGHTING LAYOUT WITH FURNITURE
Designed by	RISHAD
Checked by	SOUMYA
Date	
Revision	R1
Dwg no.	11

Notes:

Direction:

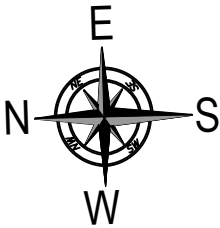

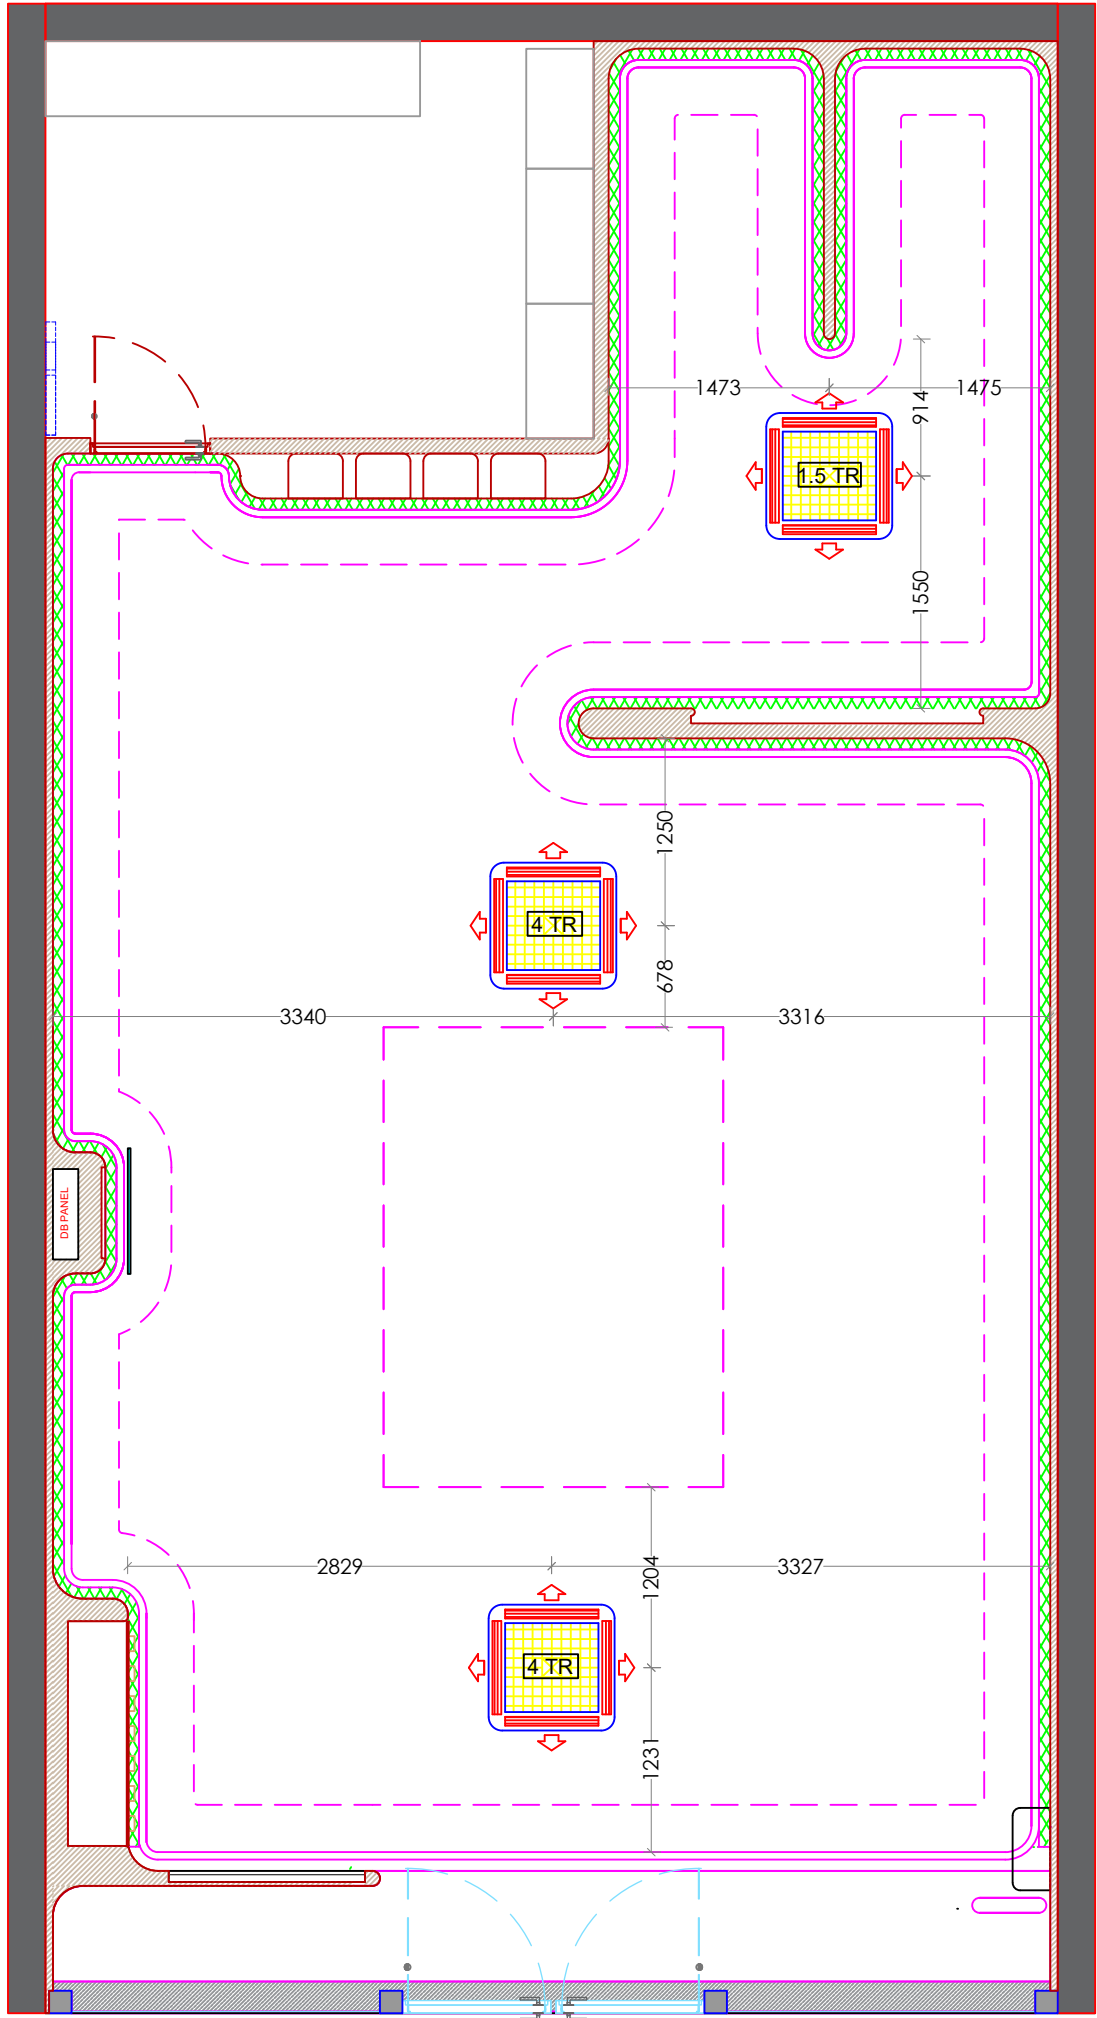

HVAC LEGEND

SL NO	SYMBOL	DESCRIPTION	QTY
1		CASSETTE UNITS-4 TR	2
2		CASSETTE UNITS- 1.5 TR	1



Sureena Chowdhri
-
Jaipur

Brand Info

Shop info

Market	INDIA
Province	RAJASTHAN
City	JAIPUR
City tier (tier 1/2/3)	TIER 1
Mall Name	HIGH STREET
New /Reno /Relo	NEW
FSS / SIS	FSS
Shop concept	SUREENA CHOWDHRI
Net size	957 SFT
Slab height	4395MM
B.O.B height	4267MM


Drawing info

Title	HVAC LAYOUT
Designed by	RISHAD
Checked by	SOUMYA
Date	
Revision	R1
Dwg no.	09

Notes:

Direction:



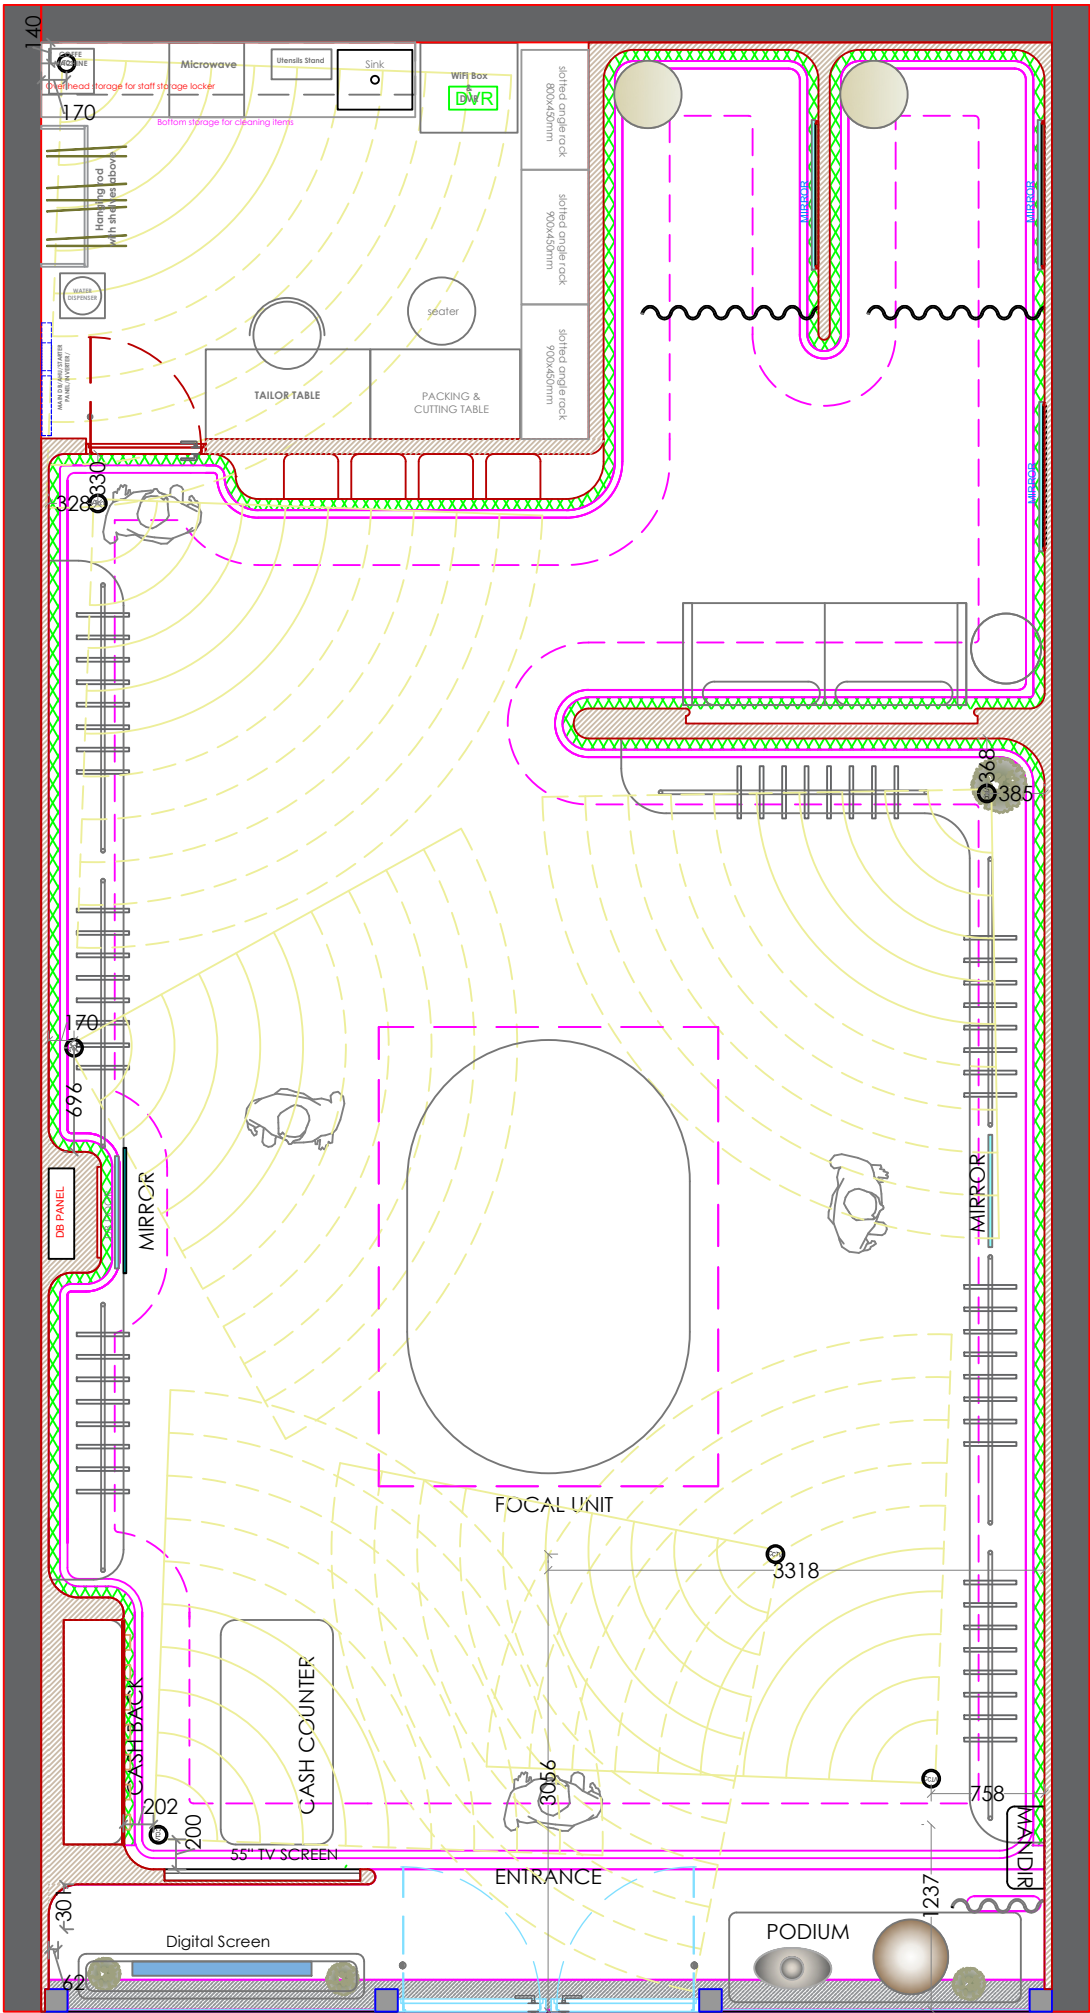

CCTV LEGEND		
REF.	DESCRIPTION	QTY
	CEILING MOUNTED WITH ADJUSTABLE FRAME HIGH RESOLUTION CAMERA.	07 no
	DVR	01 no



Sureena Chowdhri
-
Jaipur

Brand Info

Shop info


Market	INDIA
Province	RAJASTHAN
City	JAIPUR
City tier (tier 1/2/3)	TIER 1
Mall Name	HIGH STREET
New /Reno /Relo	NEW
FSS / SIS	FSS
Shop concept	SUREENA CHOWDHRI
Net size	957 SFT
Slab height	4395MM
B.O.B height	4267MM


Drawing info

Title	CCTV LAYOUT
Designed by	RISHAD
Checked by	SOUMYA
Date	
Revision	R1
Dwg no.	12

Notes:

Direction:

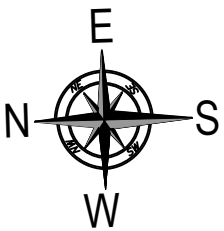

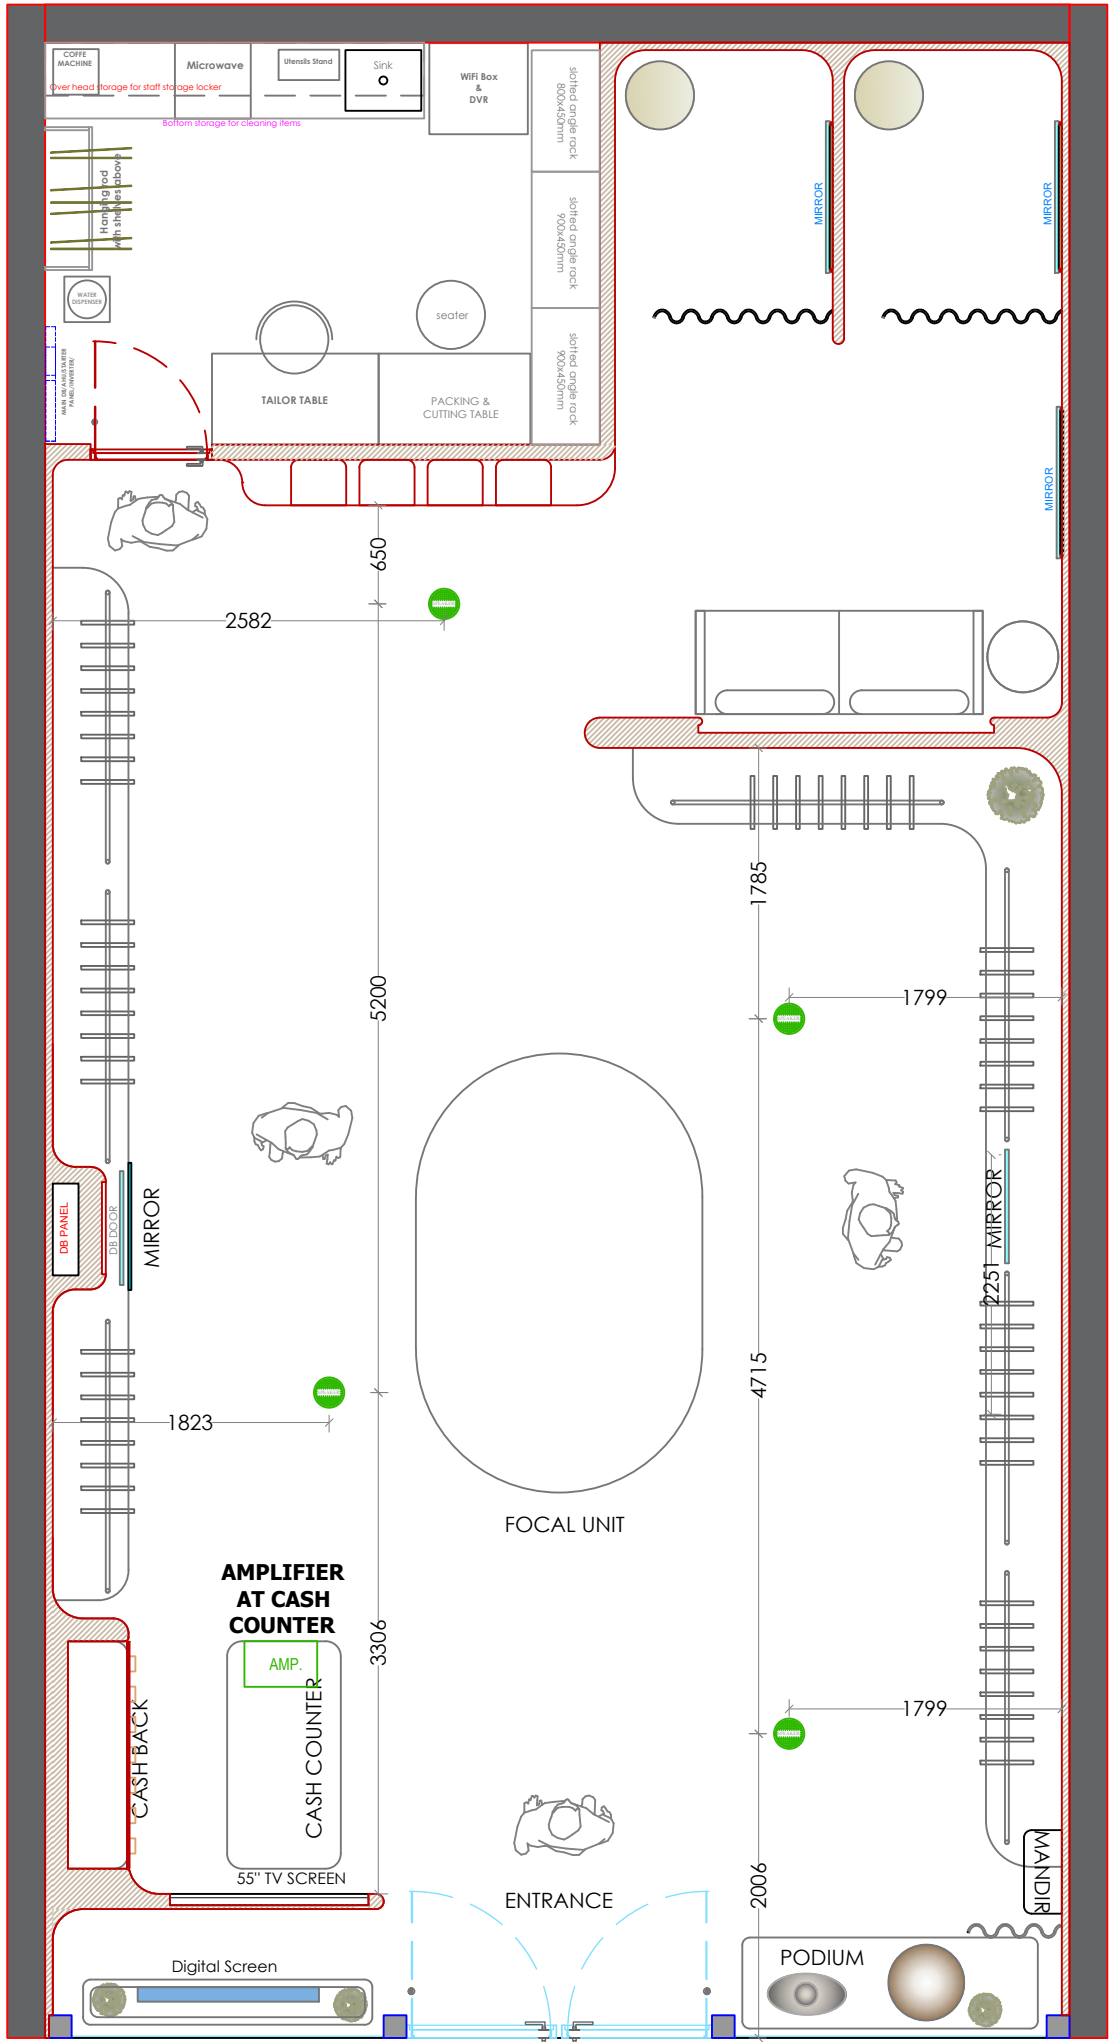

AUDIO LEGEND		
SYMBOL	DESCRIPTION	GF QTY
	CEILING MOUNTED SPEAKERS	04
	AMPLIFIER AT CASH COUNTER	01
	SUB-WOOFER	00
	20mm Ø CONDUIT FOR SPEAKERS	



Sureena Chowdhri
-
Jaipur

Brand Info

Shop info


Market	INDIA
Province	RAJASTHAN
City	JAIPUR
City tier (tier 1/2/3)	TIER 1
Mall Name	HIGH STREET
New /Reno /Relo	NEW
FSS / SIS	FSS
Shop concept	SUREENA CHOWDHRI
Net size	957 SFT
Slab height	4395MM
B.O.B height	4267MM


Drawing info

Title	AUDIO LAYOUT
Designed by	RISHAD
Checked by	SOUMYA
Date	
Revision	R1
Dwg no.	13

Notes:

Direction:

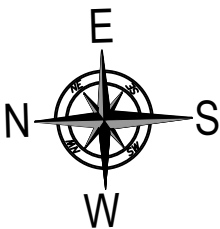

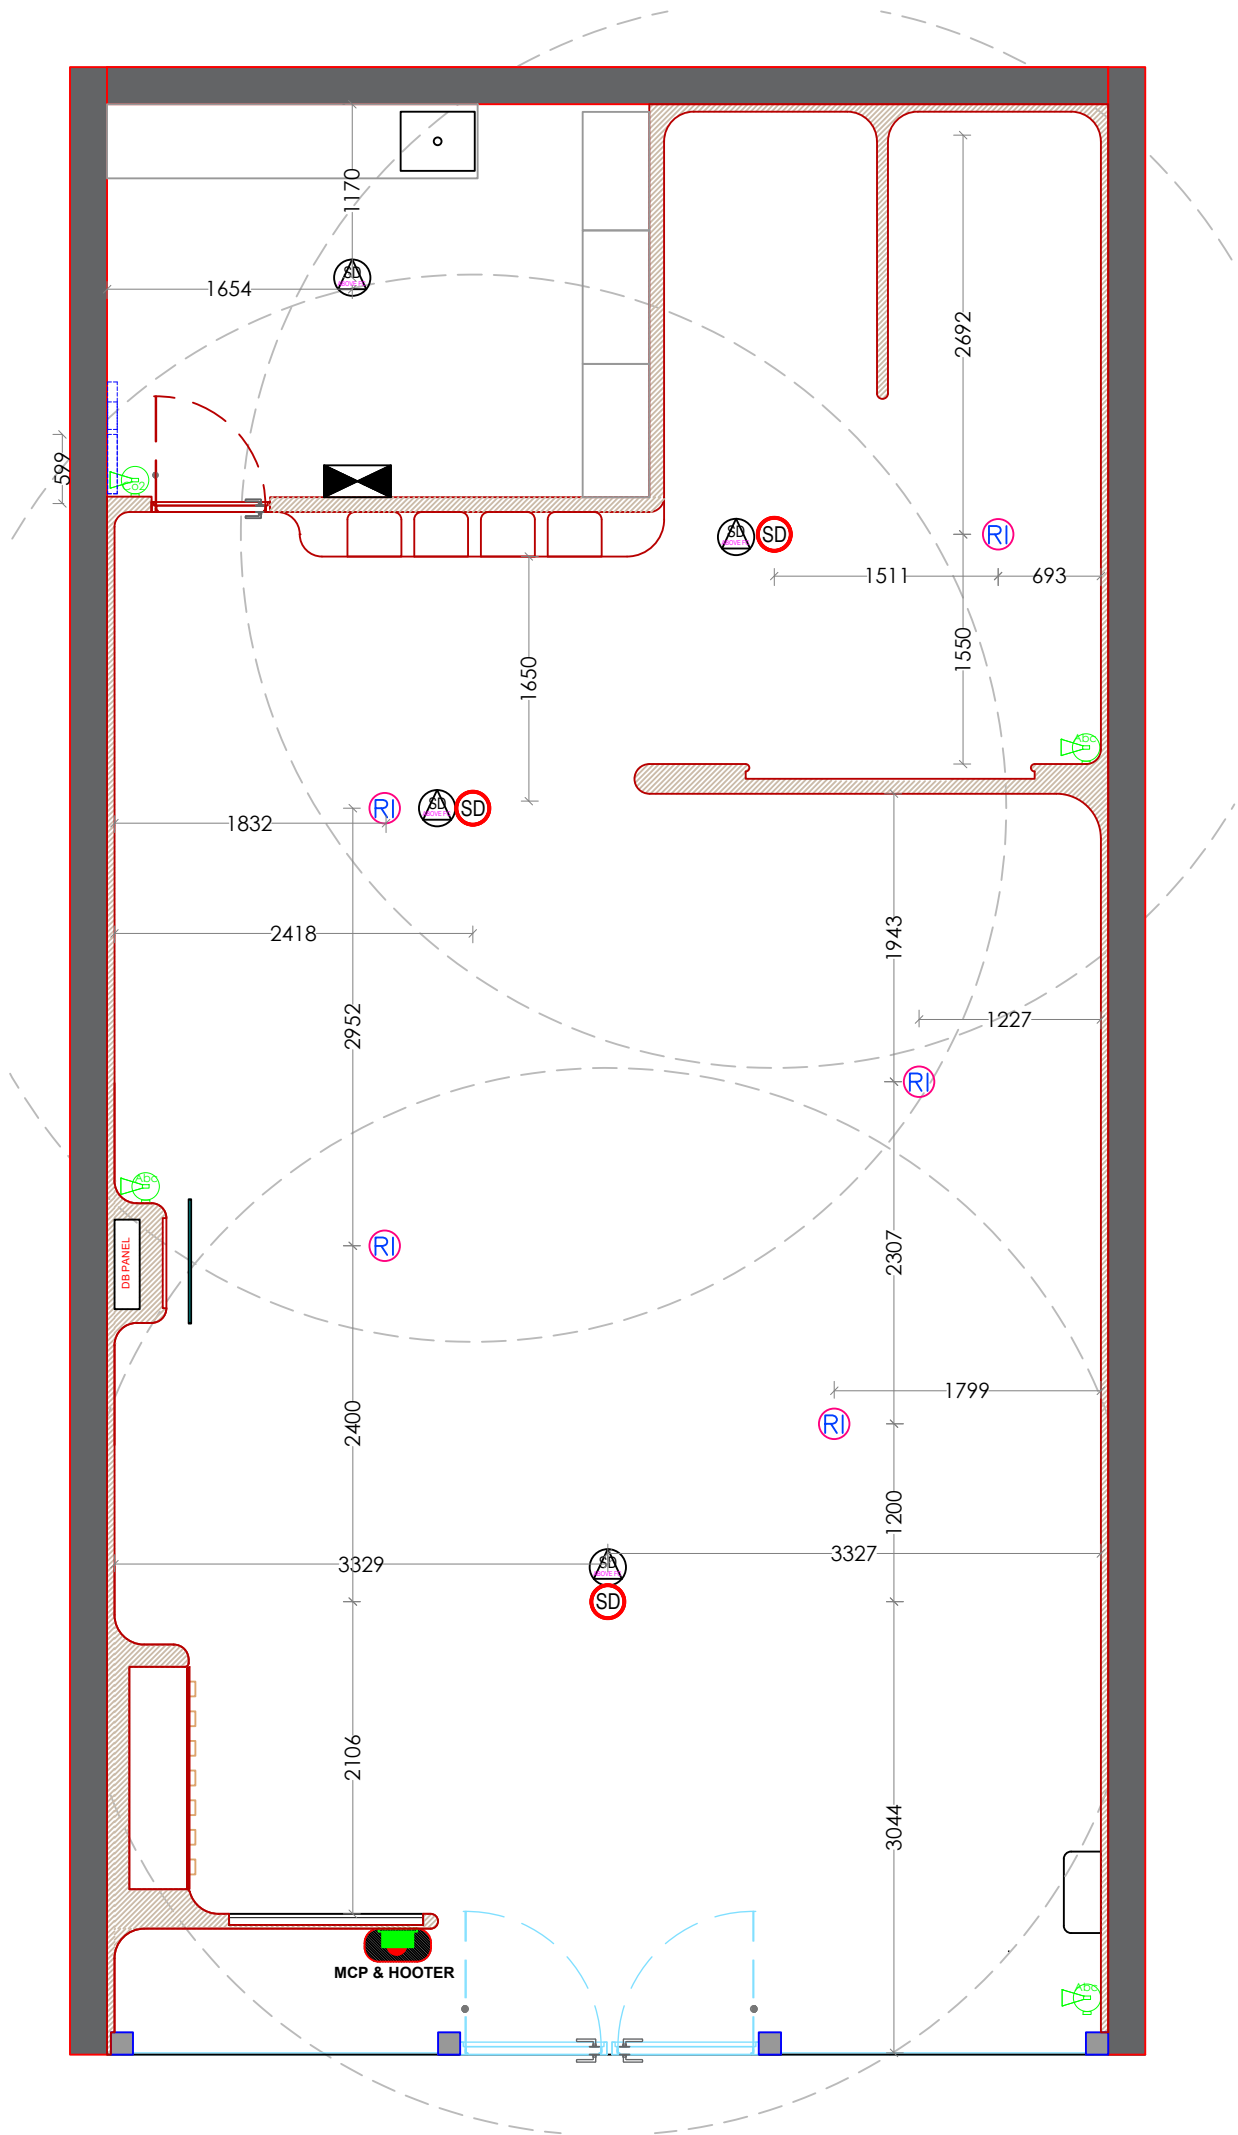

SLP LEGEND		
PATTERN	DESCRIPTION	QTY
	PROPOSED SMOKE DETECTORS BELOW FALSE CEILING	03
	PROPOSED SMOKE DETECTORS ABOVE CEILING	04
	MANUAL CALL POINT @ 1500mm from FFL	01
	HOOTER @ 2100mm FROM FFL.	01
	FAS PANEL	01
	ABC FIRE EXTINGUISHER 5KG WITH AUTOGLOW SIGNAGE	03
	CLEAN AGENT FIRE EXTINGUISHER WITH AUTOGLOW SIGNAGE	00
	CO2- FIRE EXTINGUISHER 4.5 KG WITH AUTOGLOW SIGNAGE	01
	RESPONSE INDICATOR	03
	DRY AGENT CEILING MOUNTED 4 KG	00



Sureena Chowdhri
-
Jaipur

Brand Info

Shop info


Market	INDIA
Province	RAJASTHAN
City	JAIPUR
City tier (tier 1/2/3)	TIER 1
Mall Name	HIGH STREET
New /Reno /Relo	NEW
FSS / SIS	FSS
Shop concept	SUREENA CHOWDHRI
Net size	957 SFT
Slab height	4395MM
B.O.B height	4267MM

Drawing info

Title	FAS LAYOUT
Designed by	RISHAD
Checked by	SOUMYA
Date	
Revision	R1
Dwg no.	14

Notes:

Direction:

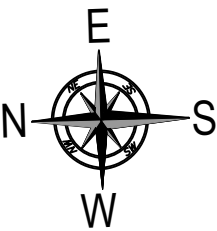



Sureena Chowdhri
-
Jaipur

Brand Info

Shop info



Market	INDIA
Province	RAJASTHAN
City	JAIPUR
City tier (tier 1/2/3)	TIER 1
Mall Name	HIGH STREET
New /Reno /Relo	NEW
FSS / SIS	FSS
Shop concept	SUREENA CHOWDHRI
Net size	957 SFT
Slab height	4395MM
B.O.B height	4267MM

Drawing info


Title	ELEVATION 1
Designed by	RISHAD
Checked by	SOUMYA
Date	MARCH 20,2026
Revision	R1
Dwg no.	15

Notes:




Direction:

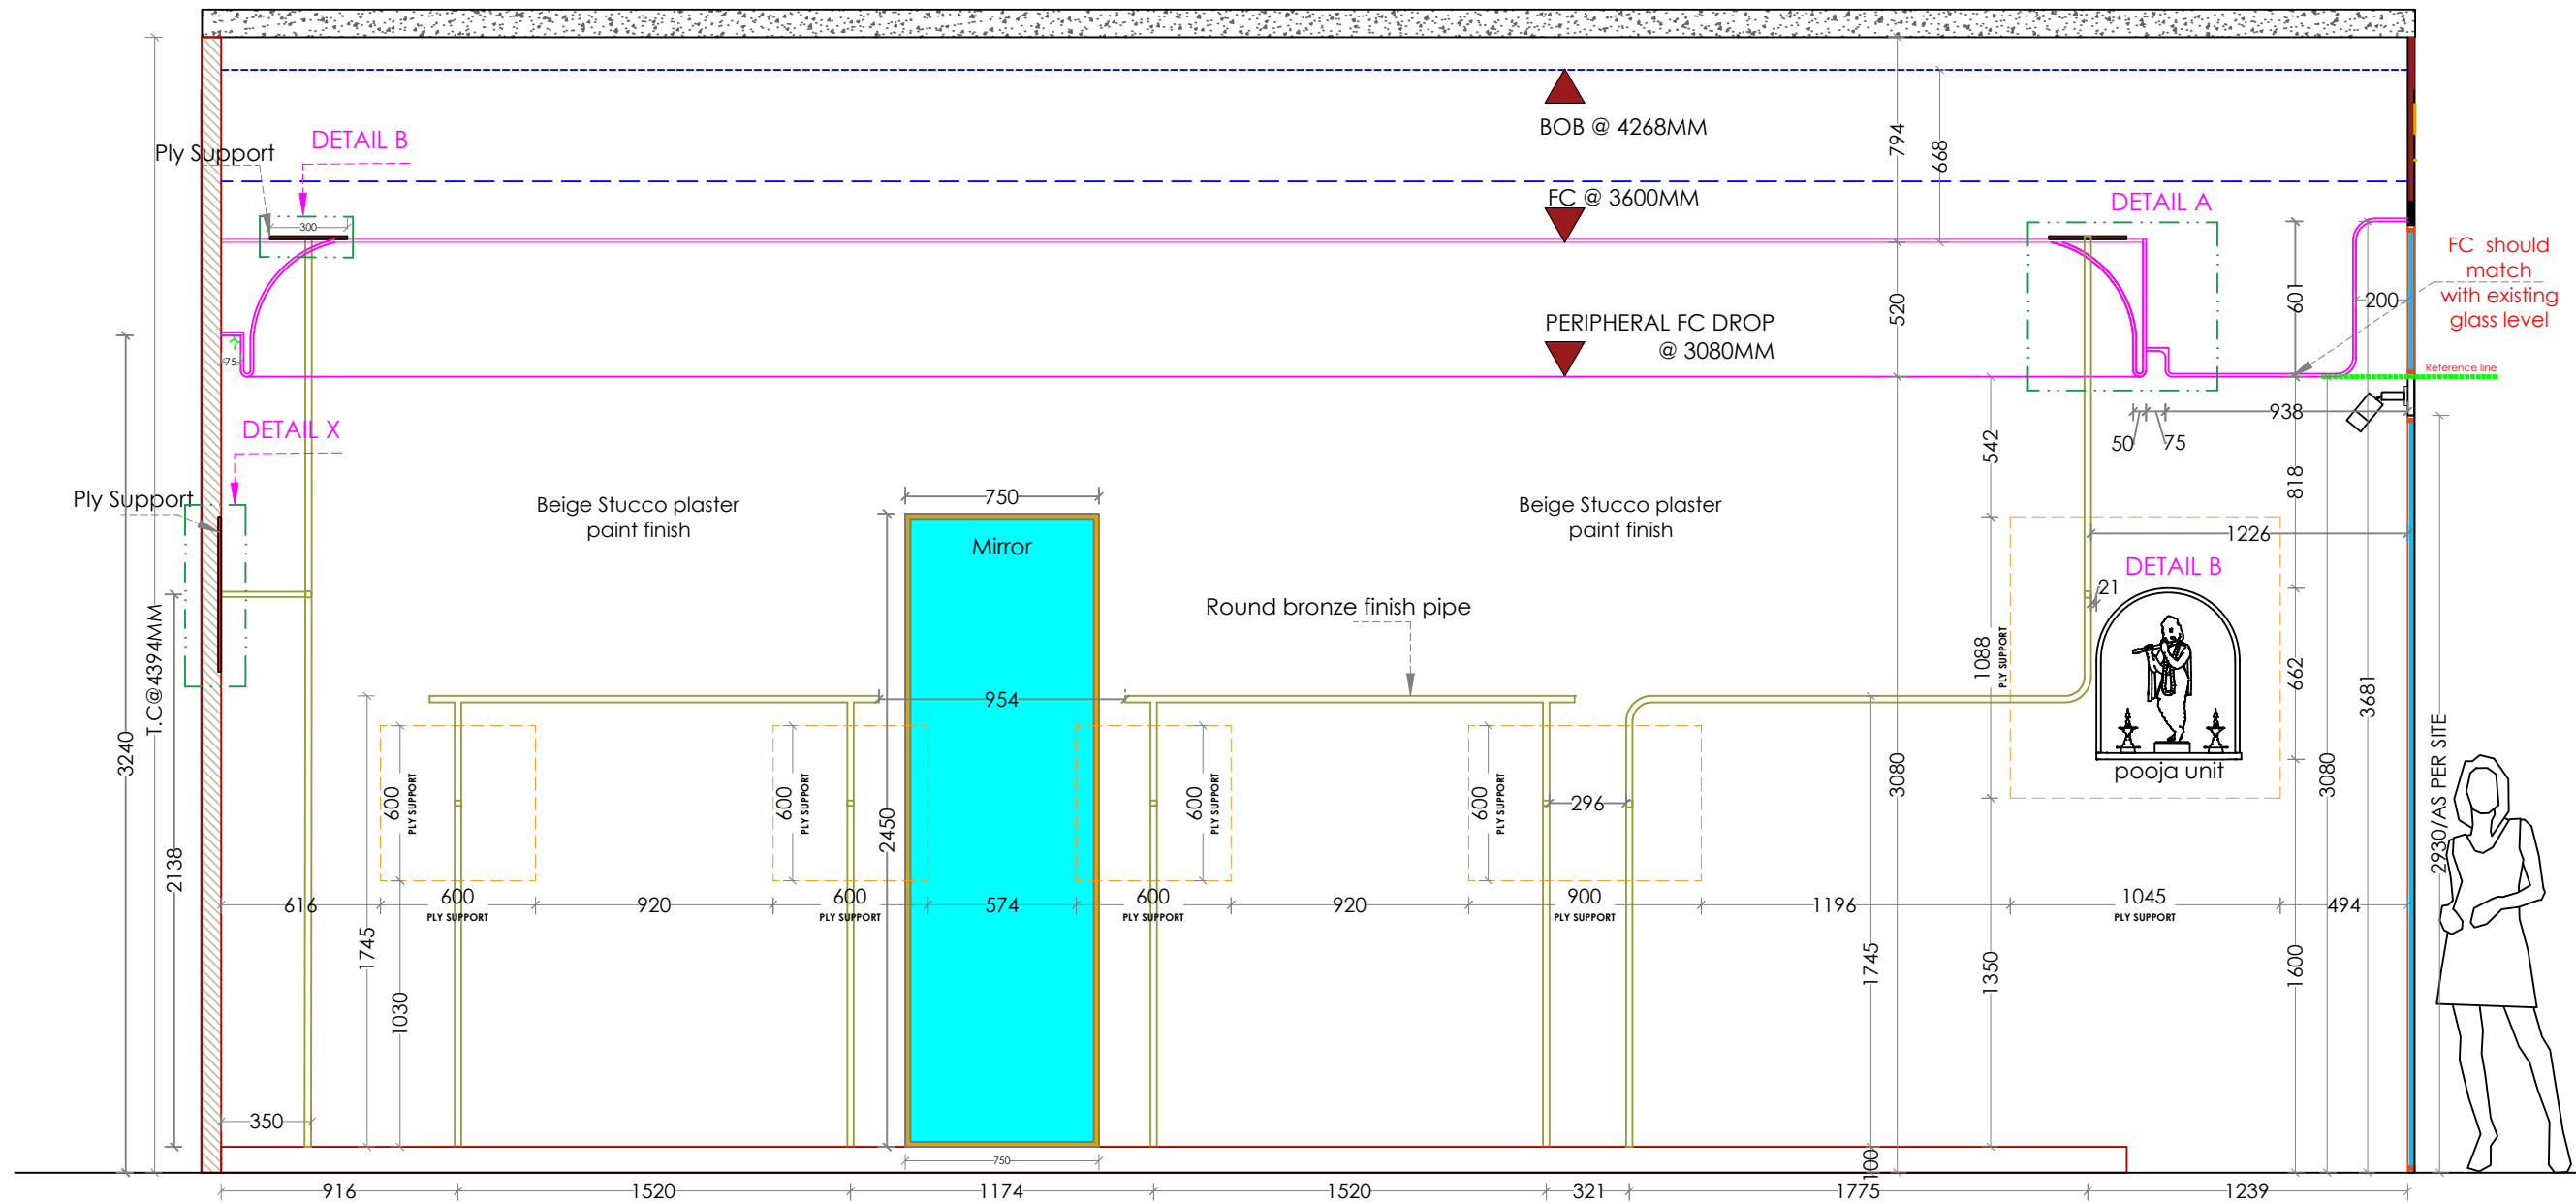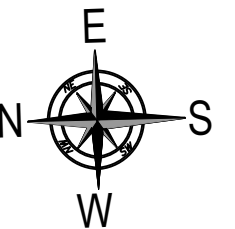


1 ELEVATION E1
Scale: NTS

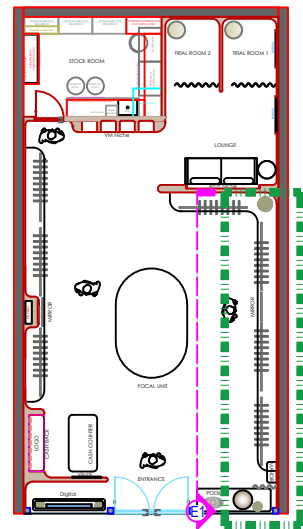


1 KEY PLAN
Scale: NTS

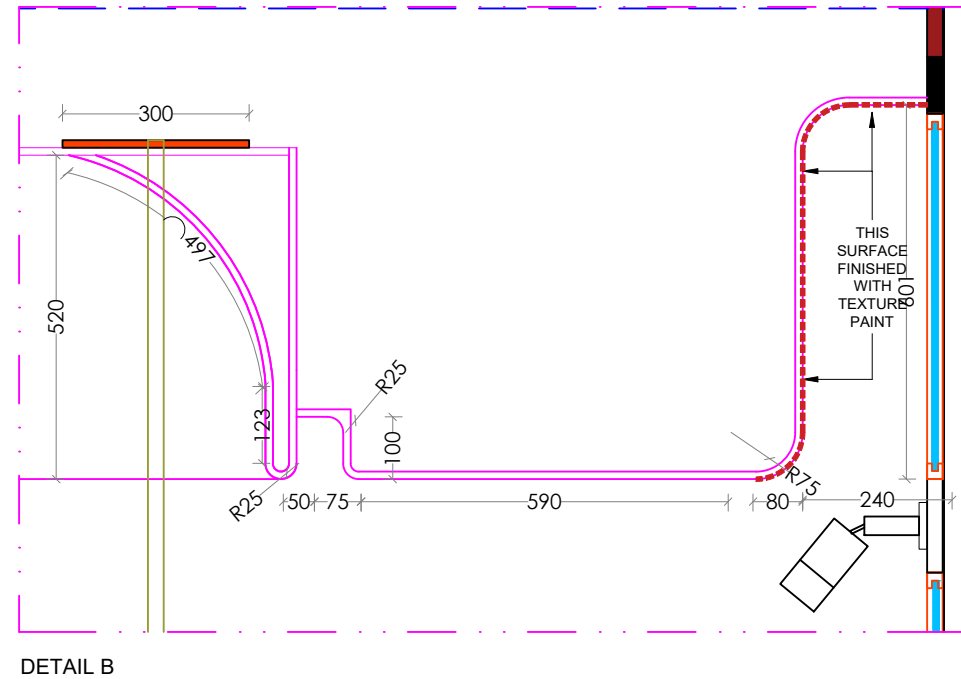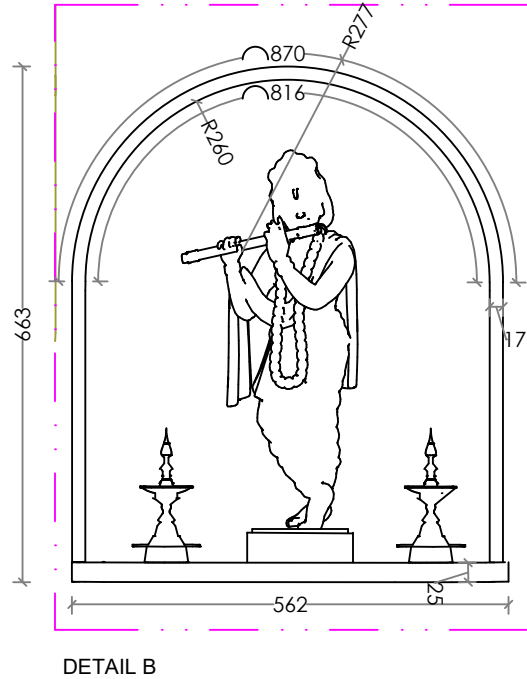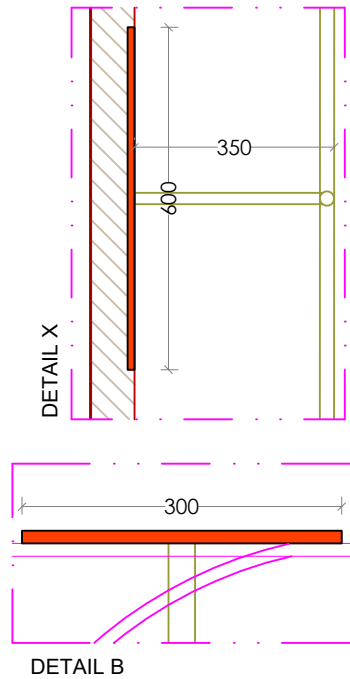




NOTE : The plywood support on the ceiling is sized at 300 × 300 mm, while the plywood support on the wall for fixtures is sized at 600 × 600 mm.

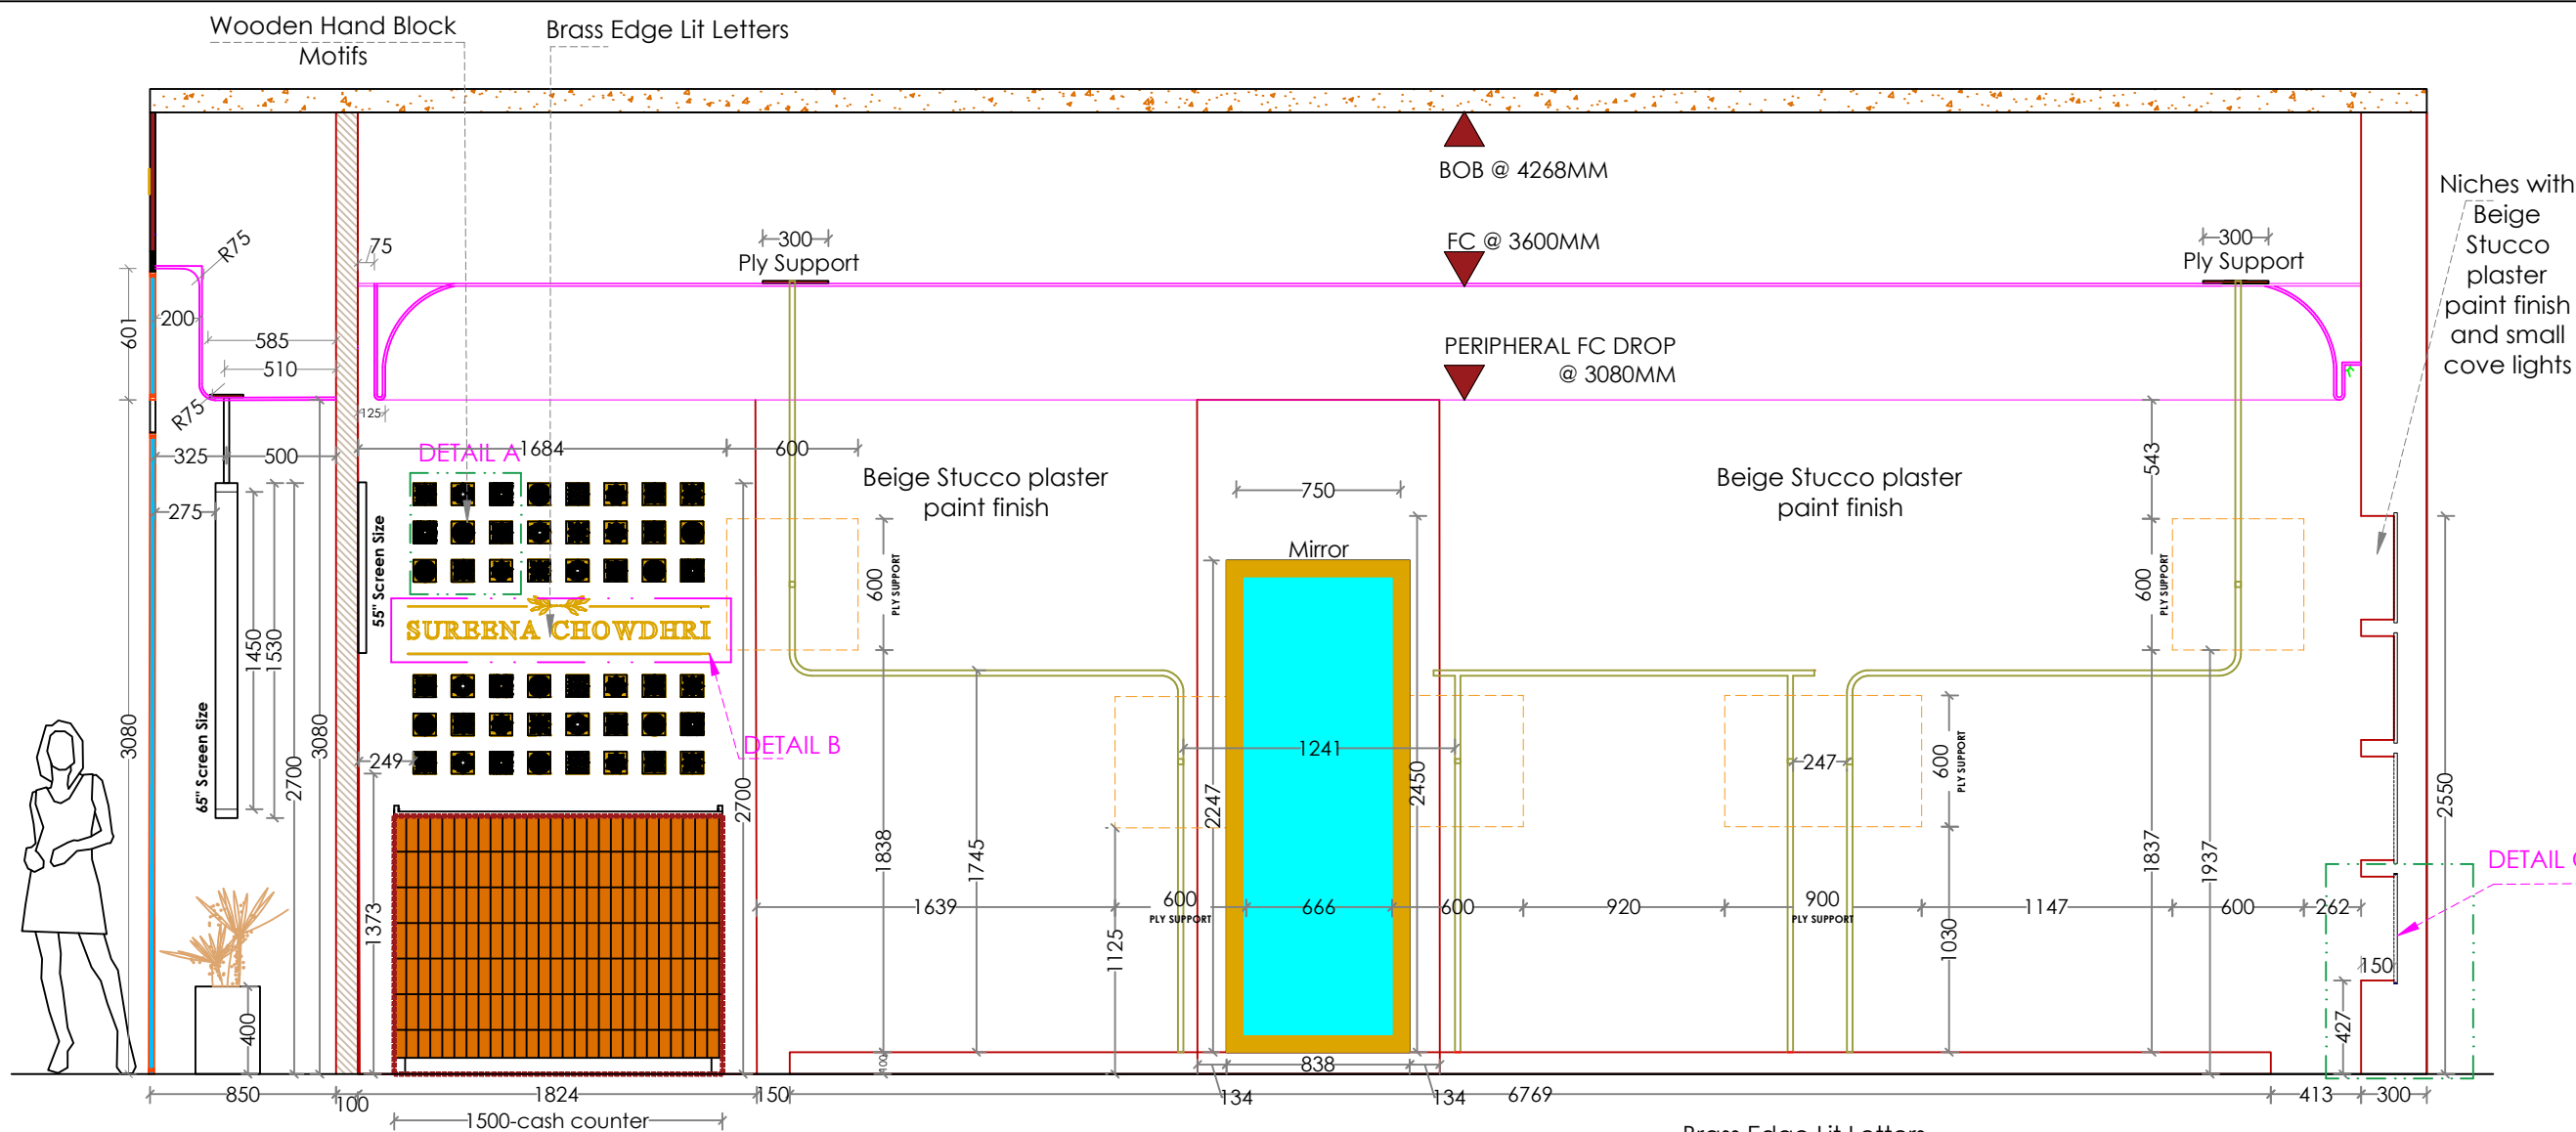

2 ELEVATION E2
Scale: NTS

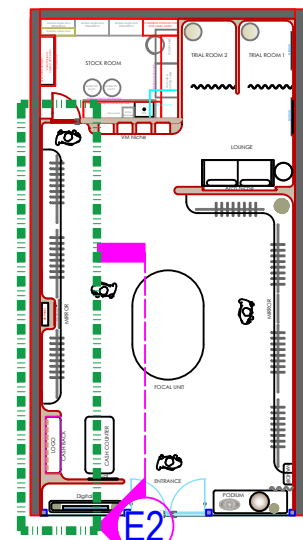

1 KEY PLAN
Scale: NTS

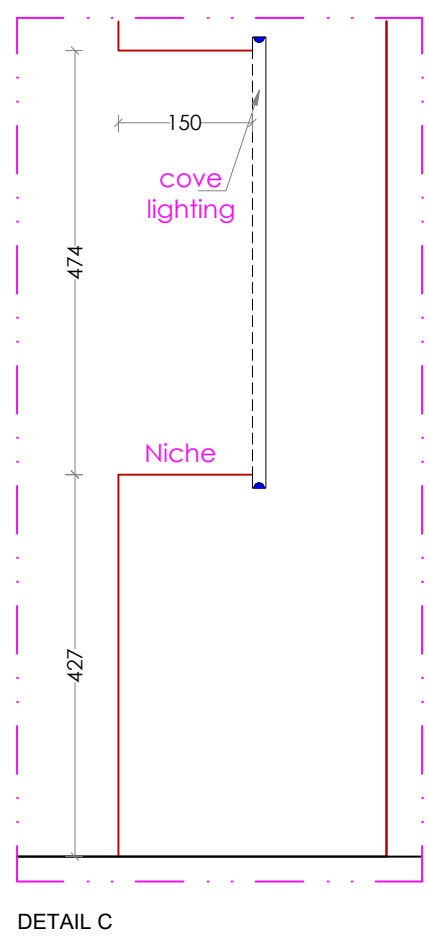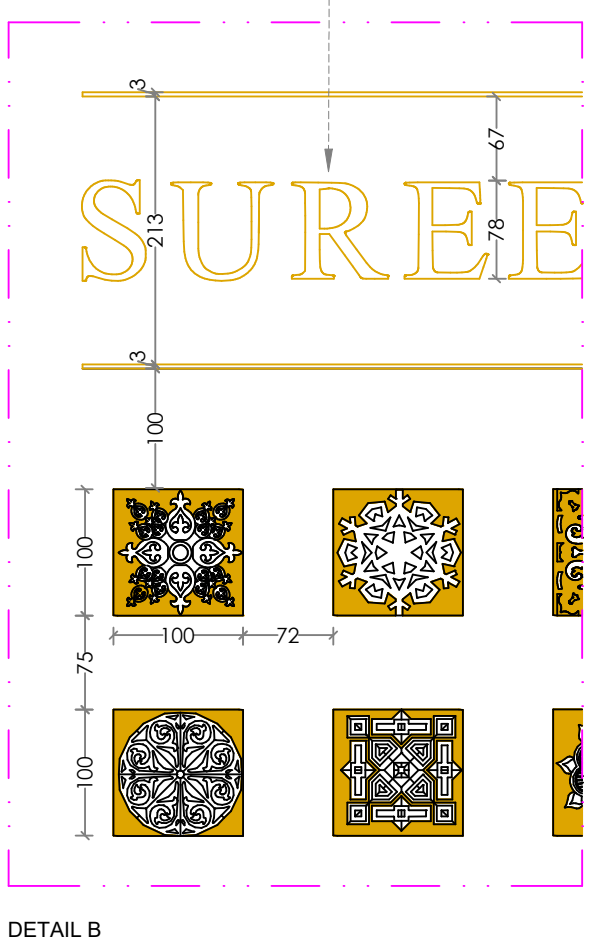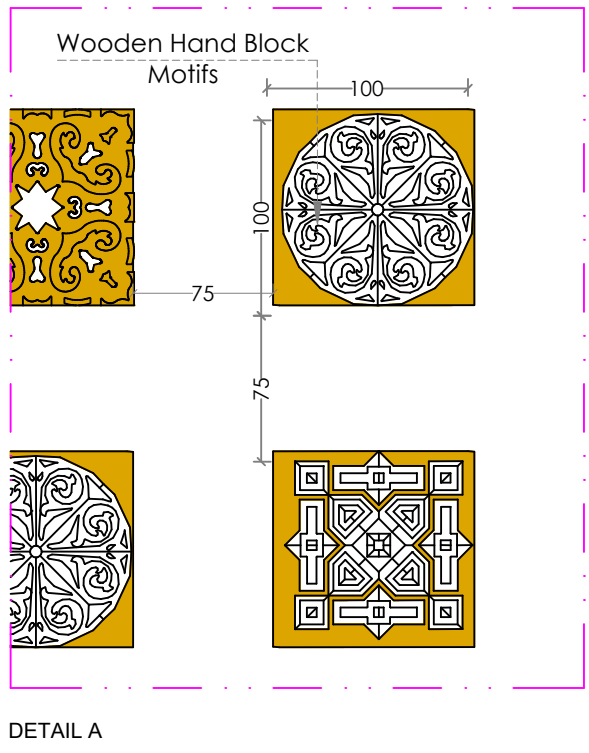

Sureena Chowdhri
-
Jaipur

Brand Info

Shop info


Market	INDIA
Province	RAJASTHAN
City	JAIPUR
City tier (tier 1/2/3)	TIER 1
Mall Name	HIGH STREET
New /Reno /Relo	NEW
FSS / SIS	FSS
Shop concept	SUREENA CHOWDHRI
Net size	957 SFT
Slab height	4395MM
B.O.B height	4267MM


Drawing info

Title	ELEVATION 2
Designed by	RISHAD
Checked by	SOUMYA
Date	MARCH 20,2026
Revision	R1
Dwg no.	16

Notes:

Direction:

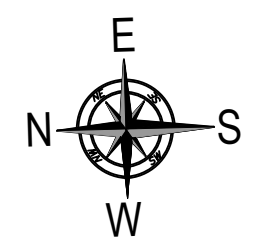

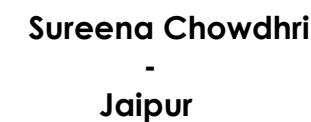



Sureena Chowdhri
-
Jaipur

Brand Info

Shop info



Market	INDIA
Province	RAJASTHAN
City	JAIPUR
City tier (tier 1/2/3)	TIER 1
Mall Name	HIGH STREET
New /Reno /Relo	NEW
FSS / SIS	FSS
Shop concept	SUREENA CHOWDHRI
Net size	957 SFT
Slab height	4395MM
B.O.B height	4267MM

Drawing info


Title	ELEVATION
Designed by	RISHAD
Checked by	SOUMYA
Date	
Revision	R1
Dwg no.	18

Notes:

Direction:

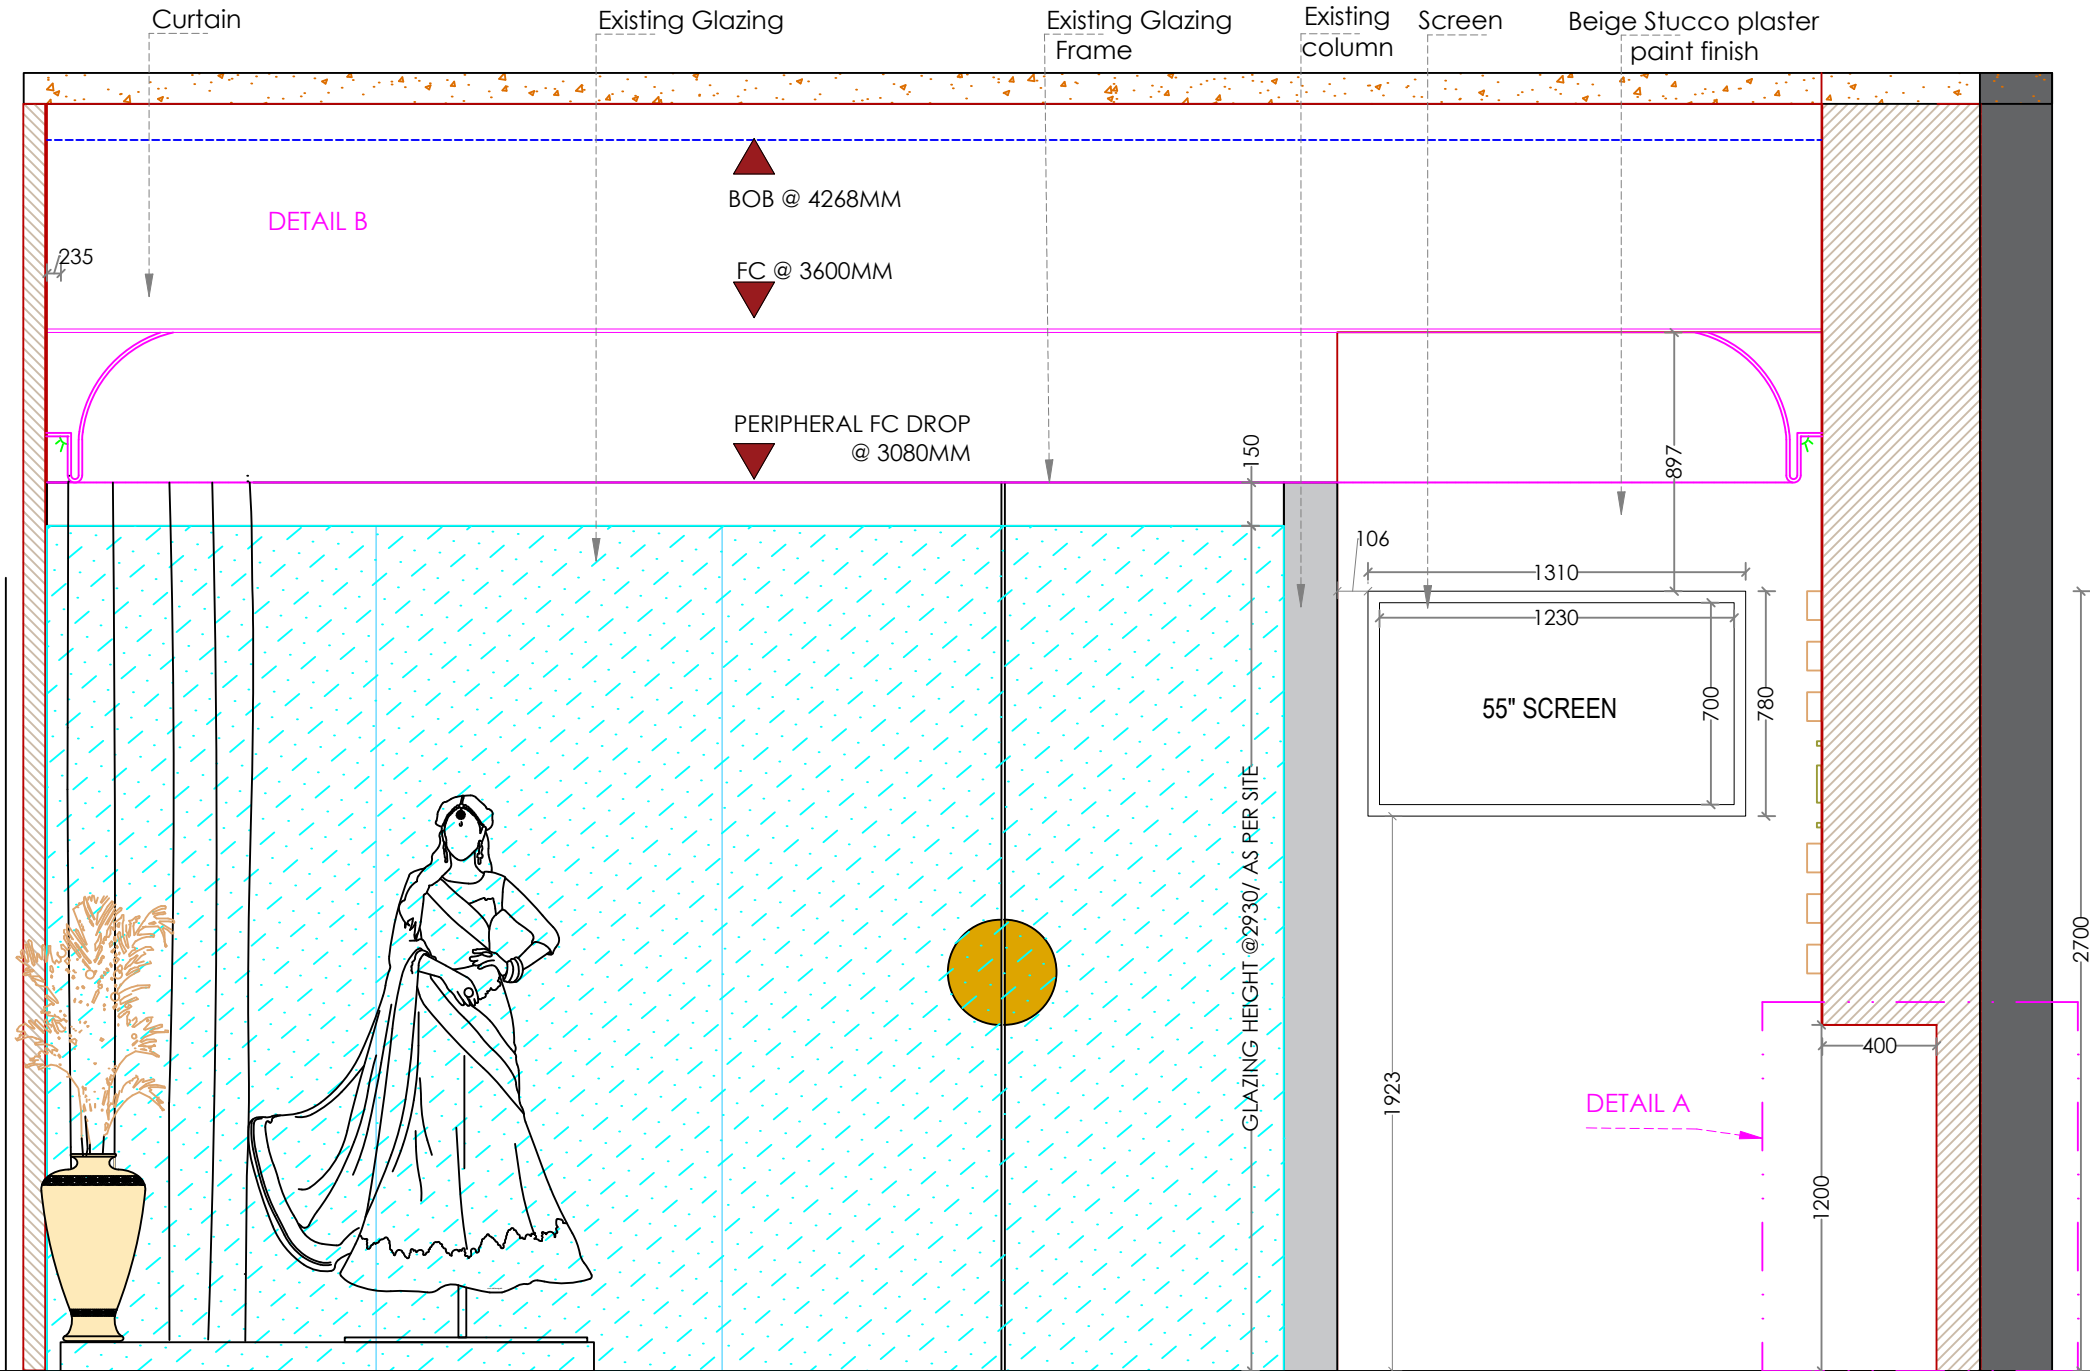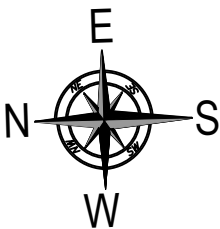

4 ELEVATION E4
Scale: NTS

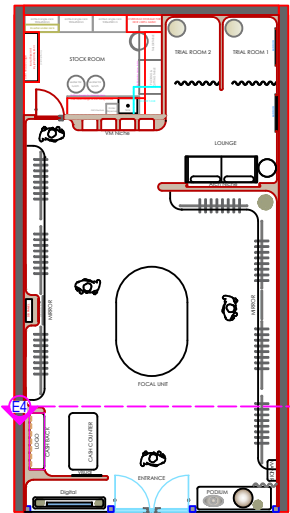

1 KEY PLAN
Scale: NTS

SPACE FOR CASH
BACK UNIT

DETAIL A

Sureena Chowdhri
-
Jaipur

Brand Info

Shop info



Market	INDIA
Province	RAJASTHAN
City	JAIPUR
City tier (tier 1/2/3)	TIER 1
Mall Name	HIGH STREET
New /Reno /Relo	NEW
FSS / SIS	FSS
Shop concept	SUREENA CHOWDHRI
Net size	957 SFT
Slab height	4395MM
B.O.B height	4267MM

Drawing info


Title	ELEVATION
Designed by	RISHAD
Checked by	SOUMYA
Date	
Revision	R1
Dwg no.	19

Notes:


Direction:

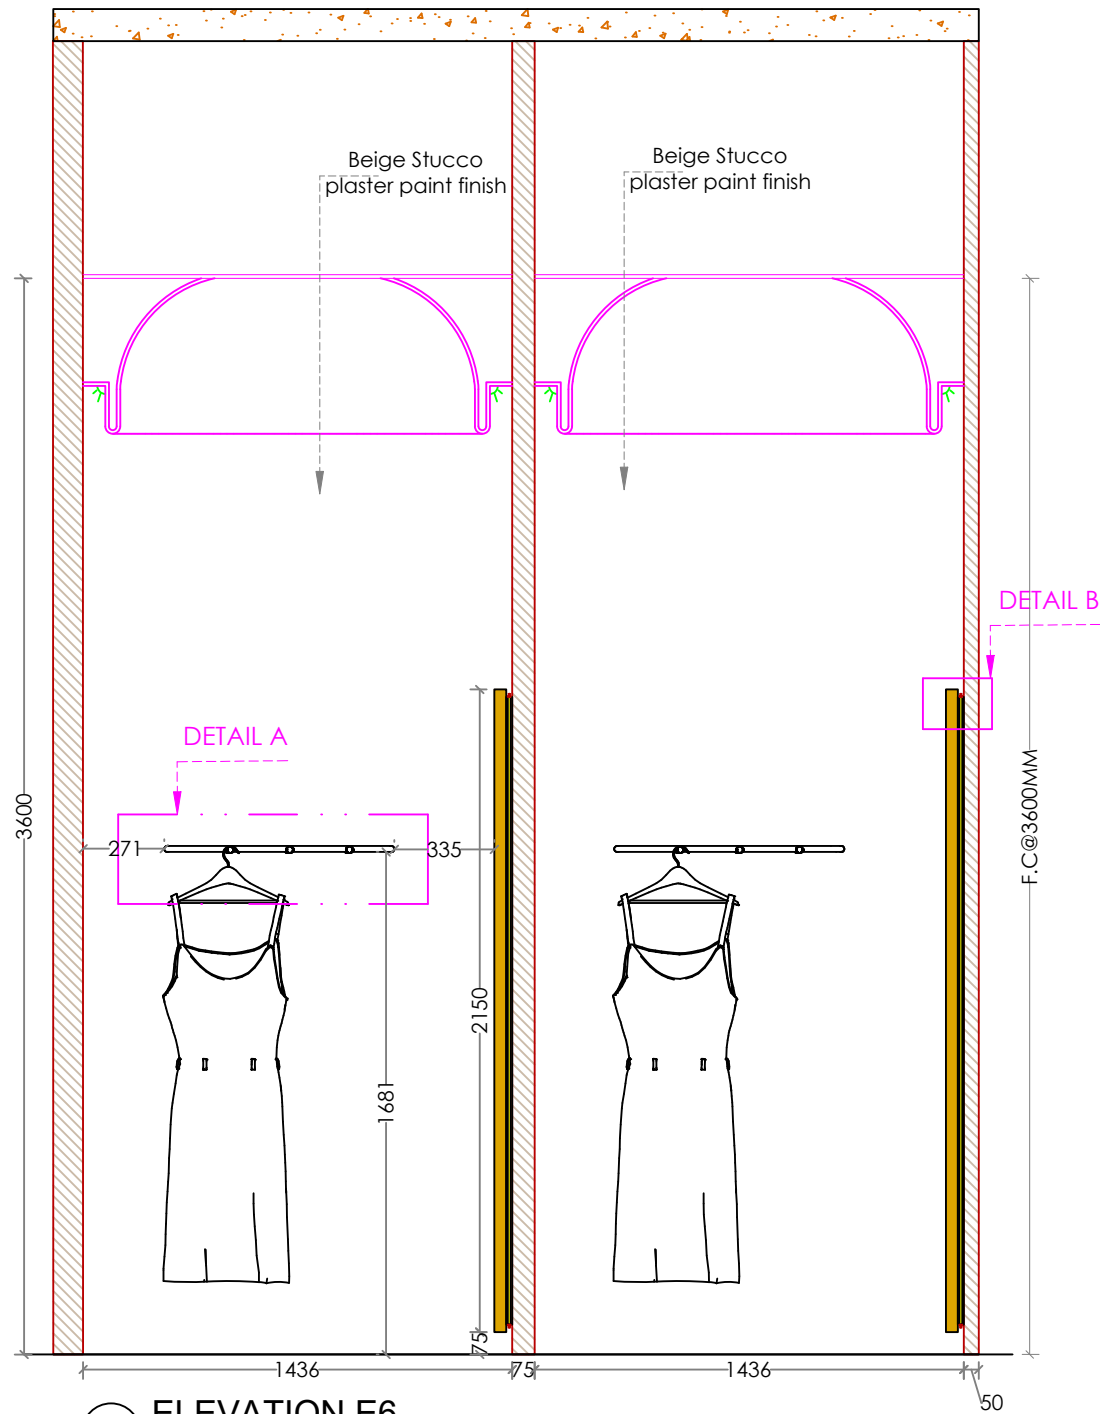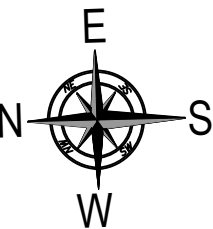


6 ELEVATION E6
Scale: NTS

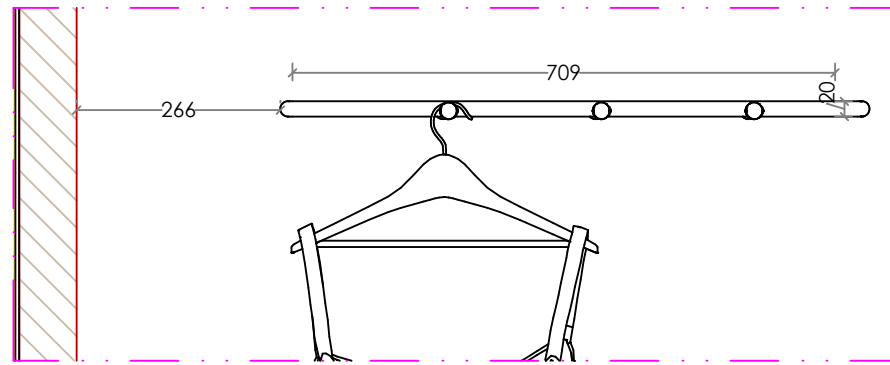


DETAIL A

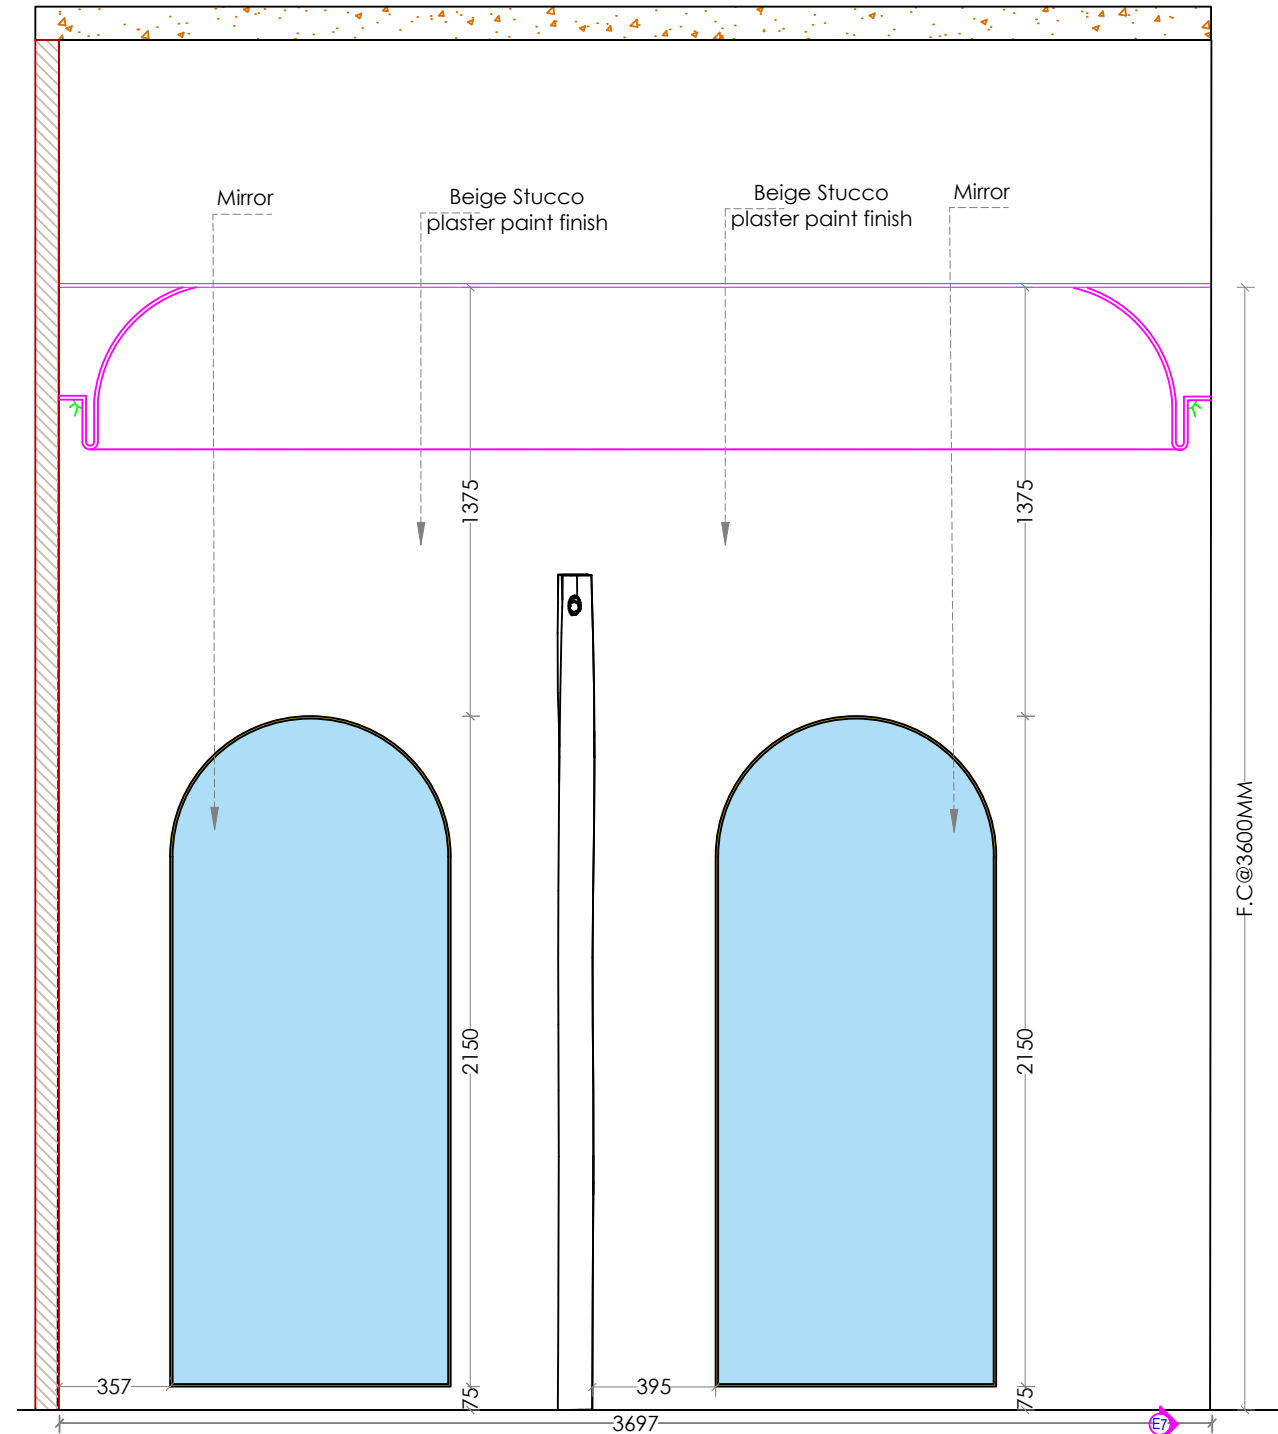


7 ELEVATION E7
Scale: NTS

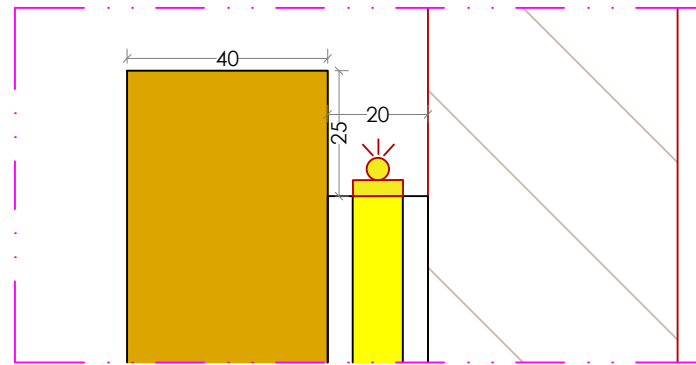


DETAIL B

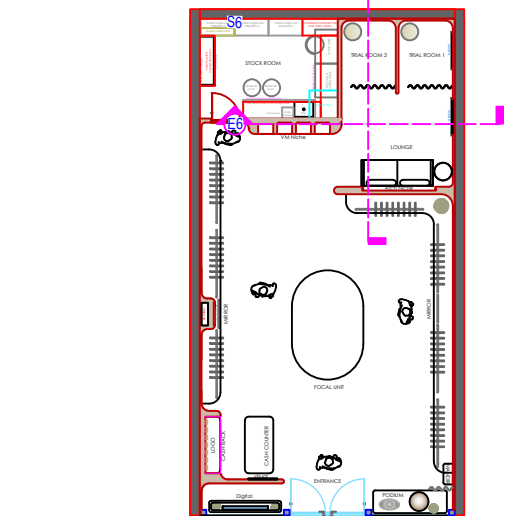


1 KEY PLAN
Scale: NTS

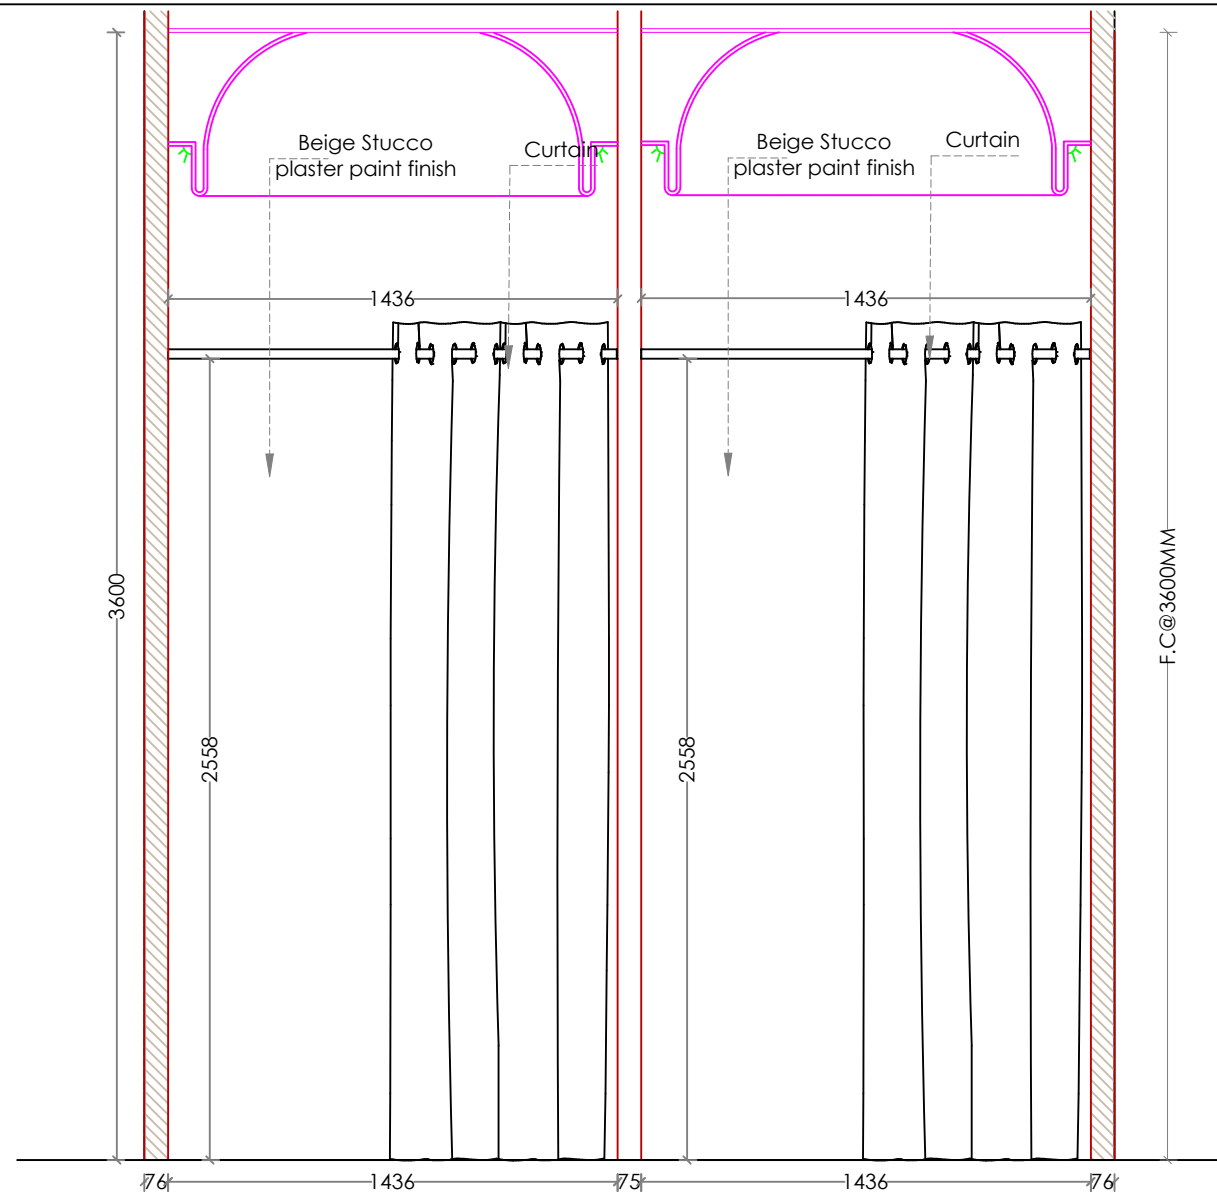


8 ELEVATION E8
Scale: NTS

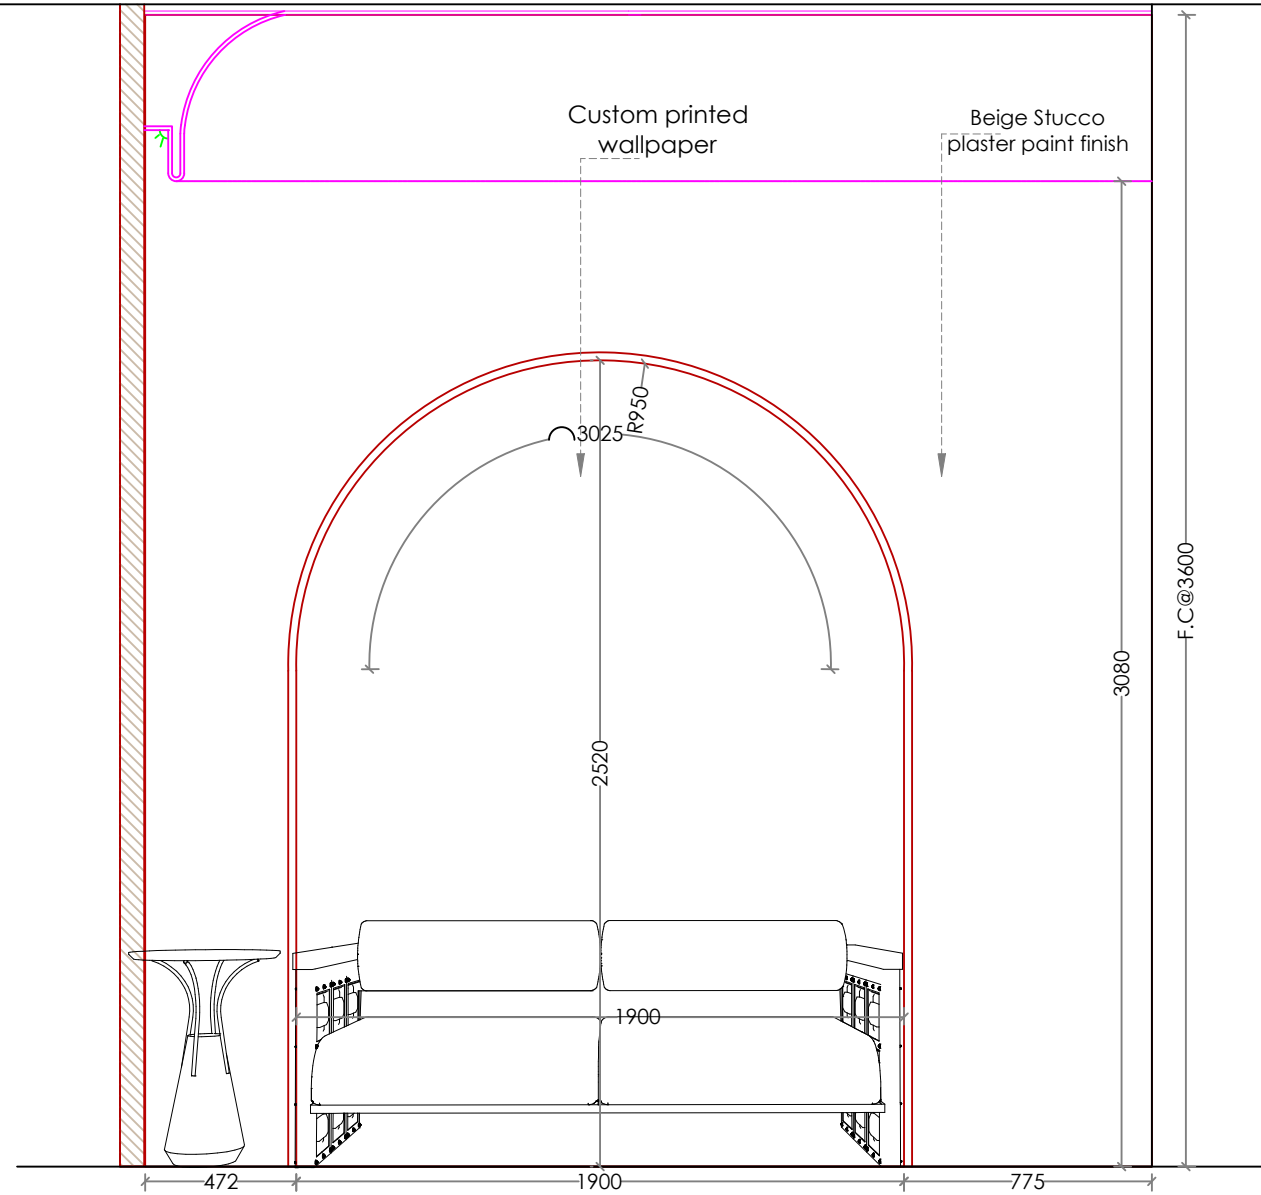

9 ELEVATION E9
Scale: NTS

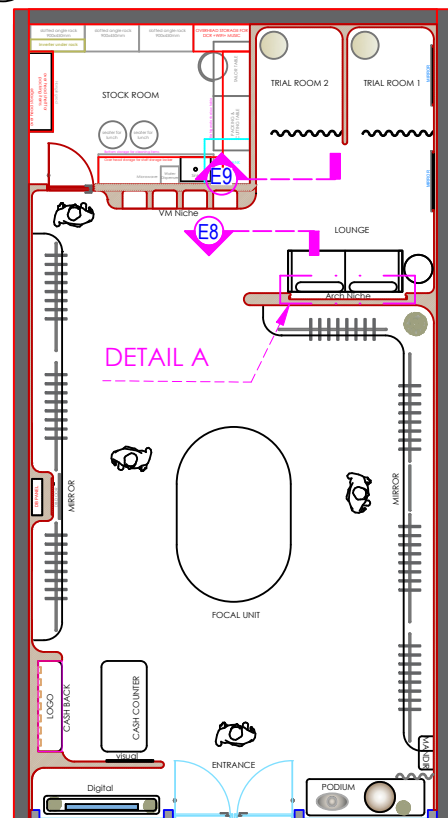



1 KEY PLAN
Scale: NTS

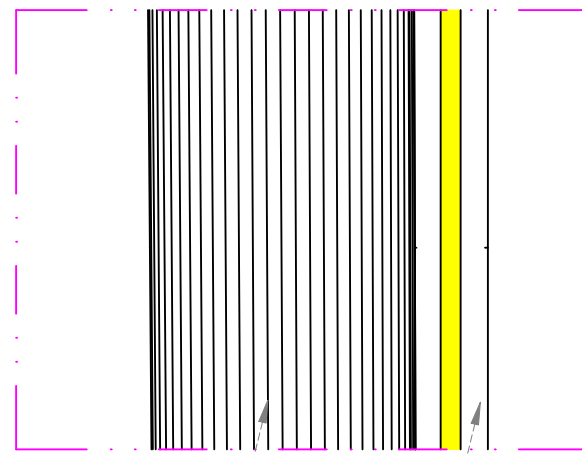

10 SECTION S1
Scale: NTS

50 MM
CURVE

50 MM
COVE FOR
STRIP LIGHT

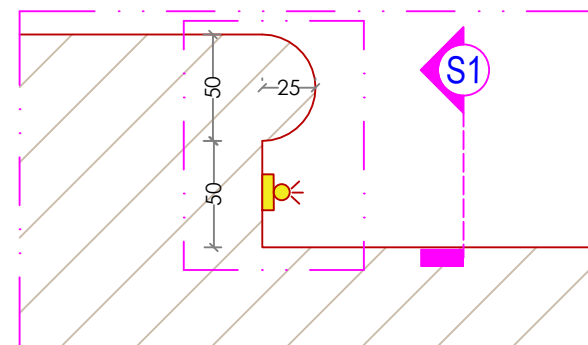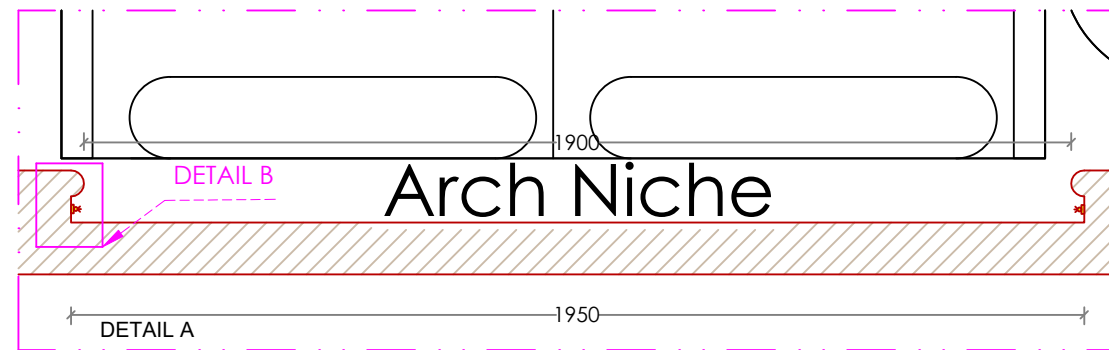

DETAIL B



Sureena Chowdhri
-
Jaipur

Brand Info

Shop info


Market	INDIA
Province	RAJASTHAN
City	JAIPUR
City tier (tier 1/2/3)	TIER 1
Mall Name	HIGH STREET
New /Reno /Relo	NEW
FSS / SIS	FSS
Shop concept	SUREENA CHOWDHRI
Net size	957 SFT
Slab height	4395MM
B.O.B height	4267MM

Drawing info

Title	ELEVATION
Designed by	RISHAD
Checked by	SOURYA
Date	
Revision	R1
Dwg no.	20

Notes:

Direction:

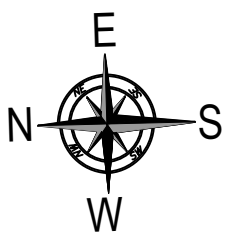



Sureena Chowdhri
-
Jaipur

Brand Info

Shop info



Market	INDIA
Province	RAJASTHAN
City	JAIPUR
City tier (tier 1/2/3)	TIER 1
Mall Name	HIGH STREET
New /Reno /Relo	NEW
FSS / SIS	FSS
Shop concept	SUREENA CHOWDHRI
Net size	957 SFT
Slab height	4395MM
B.O.B height	4267MM

Drawing info


Title	SHOW WINDOW ELEVATION
Designed by	RISHAD
Checked by	SOUMYA
Date	
Revision	R1
Dwg no.	21

Notes:


Direction:

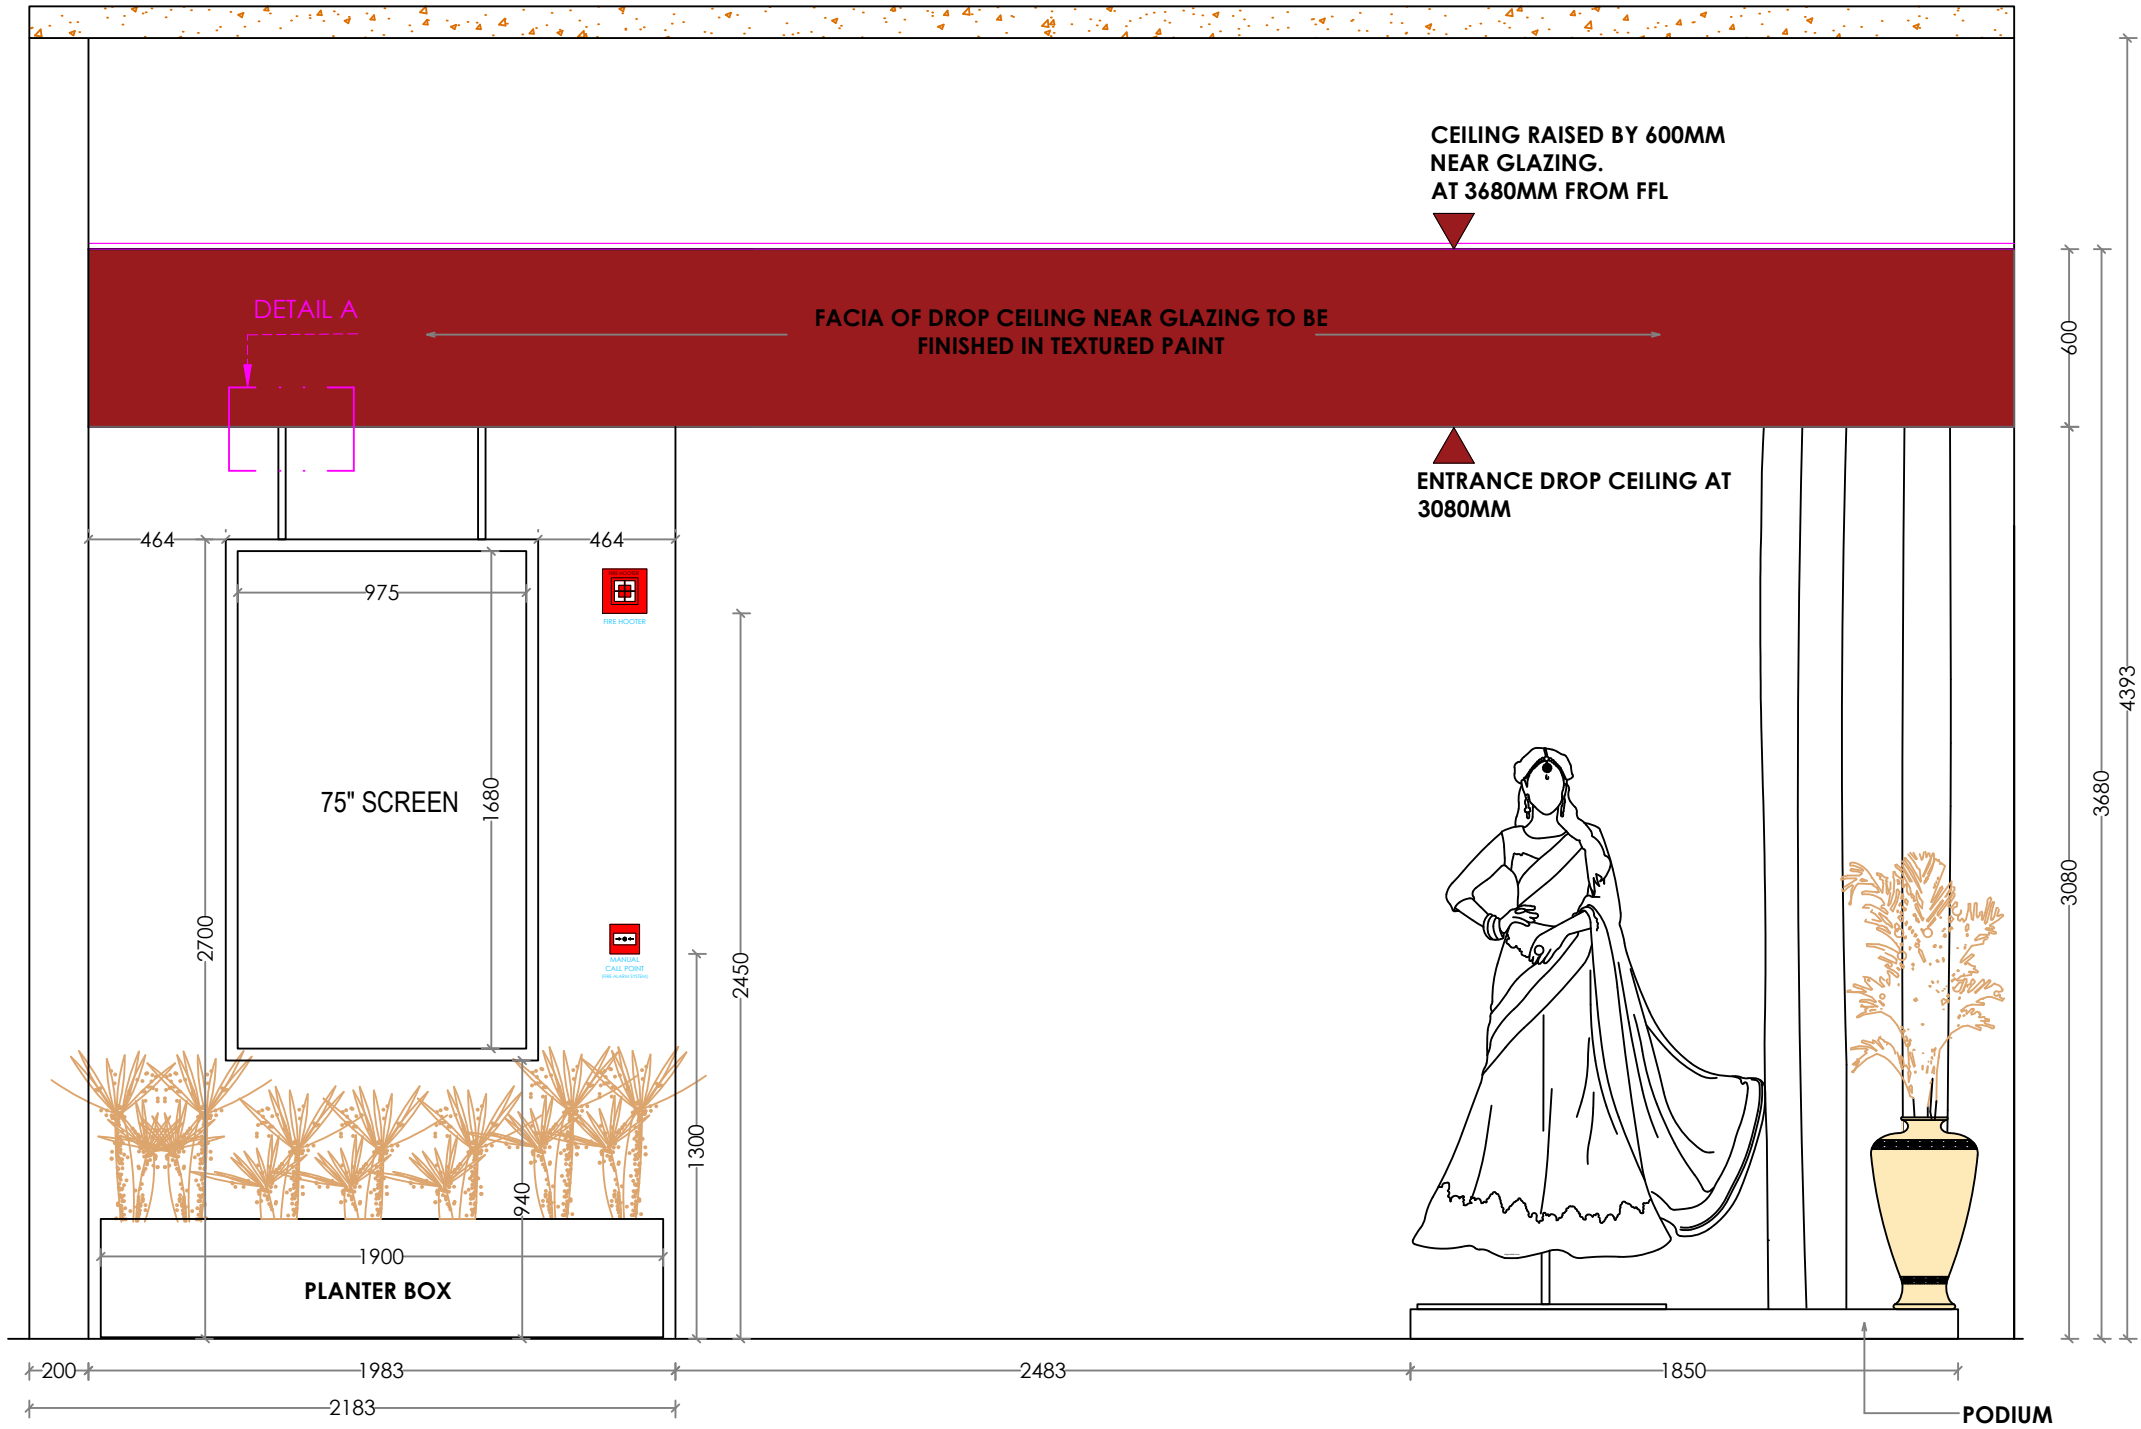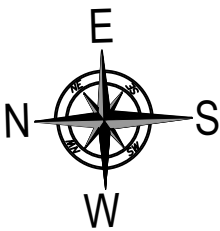

10 ELEVATION S10
Scale: NTS

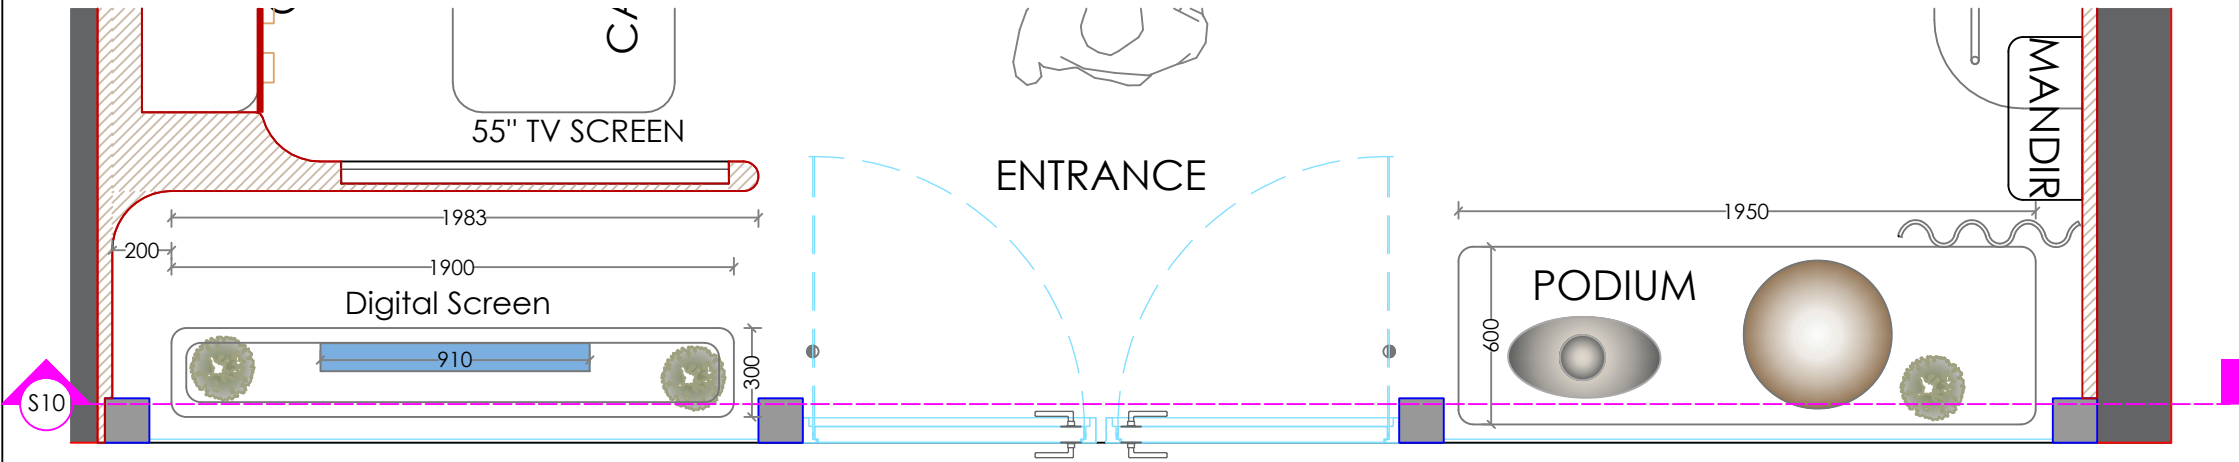

1 KEY PLAN
Scale: NTS

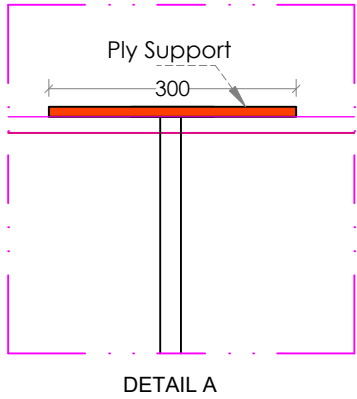



Sureena Chowdhri
-
Jaipur

Brand Info

Shop info



Market	INDIA
Province	RAJASTHAN
City	JAIPUR
City tier (tier 1/2/3)	TIER 1
Mall Name	HIGH STREET
New /Reno /Relo	NEW
FSS / SIS	FSS
Shop concept	SUREENA CHOWDHRI
Net size	957 SFT
Slab height	4395MM
B.O.B height	4267MM

Drawing info


Title	
Designed by	RISHAD
Checked by	SOUMYA
Date	
Revision	R1
Dwg no.	21

Notes:


Direction:

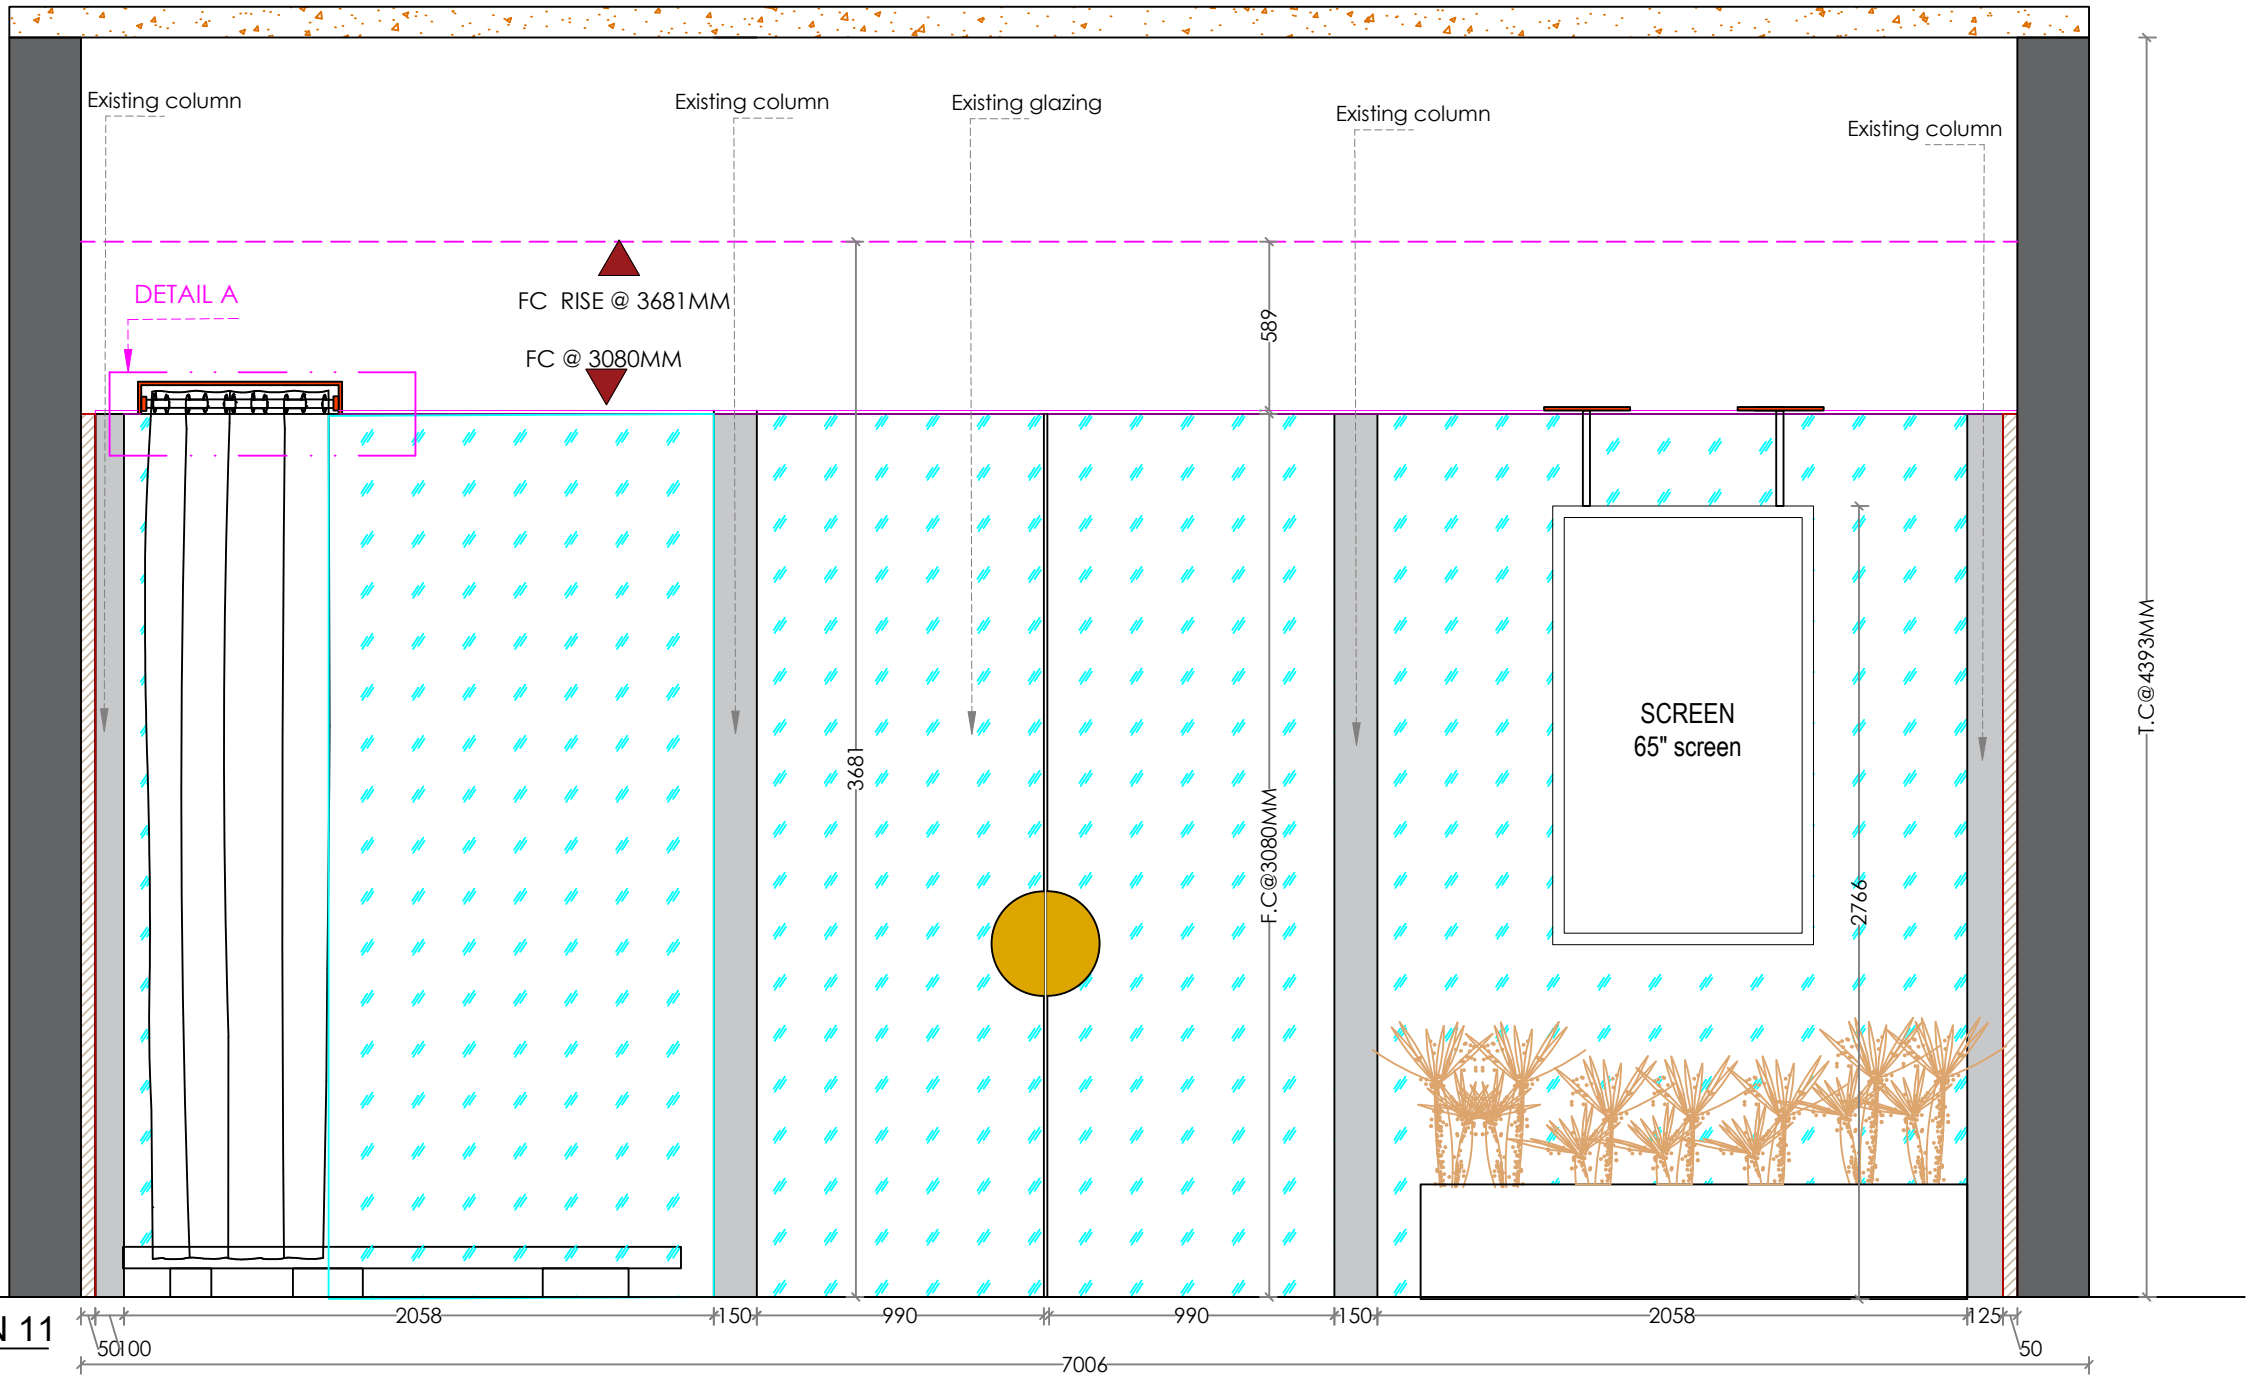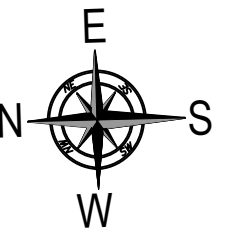

10 ELEVATION 11
Scale: NTS

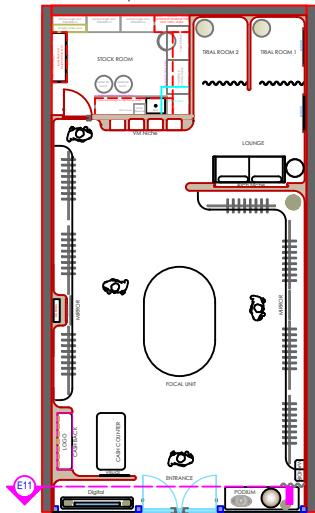

1 KEY PLAN
Scale: NTS

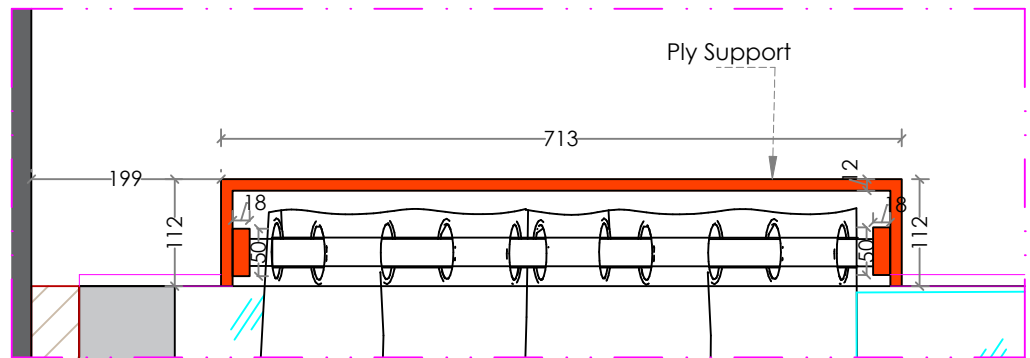

DETAIL A



EXISTING SIGNAGE



PROPOSED SIGNAGE



Sureena Chowdhri
-
Jaipur

Brand Info

--

Shop info


Market	INDIA
Province	RAJASTHAN
City	JAIPUR
City tier (tier 1/2/3)	TIER 1
Mall Name	HIGH STREET
New /Reno /Relo	NEW
FSS / SIS	FSS
Shop concept	SUREENA CHOWDHRI
Net size	957 SFT
Slab height	4395MM
B.O.B height	4267MM


Drawing info

Title	EXTERNAL FACADE
Designed by	RISHAD
Checked by	SOUMYA
Date	
Revision	R1
Dwg no.	

Notes:

Direction:

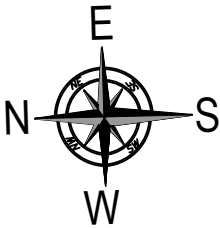

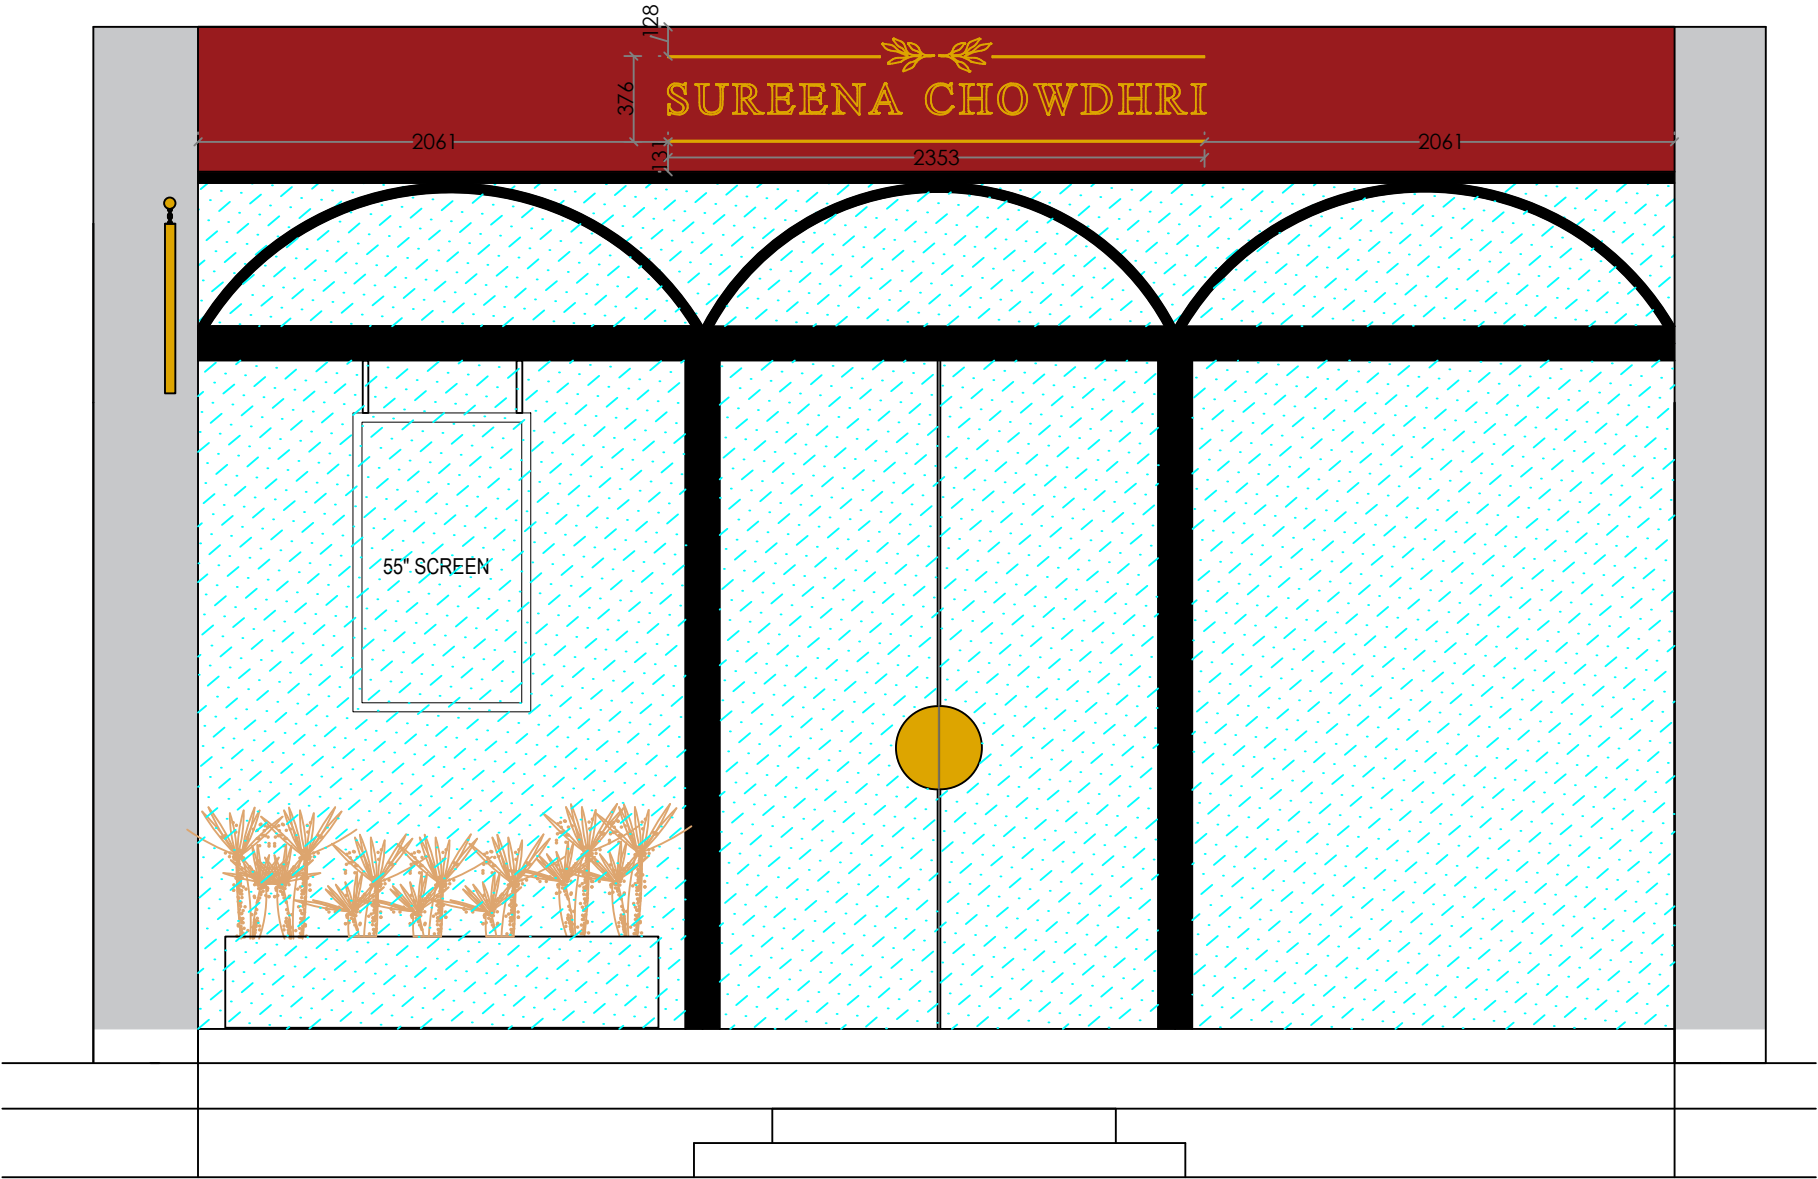

EXTERNAL FACADE ELEVATION WITH PROPOSED SIGNAGE 375 mm height



Sureena Chowdhri
-
Jaipur

Brand Info

Shop info


Market	INDIA
Province	RAJASTHAN
City	JAIPUR
City tier (tier 1/2/3)	TIER 1
Mall Name	HIGH STREET
New /Reno /Relo	NEW
FSS / SIS	FSS
Shop concept	SUREENA CHOWDHRI
Net size	957 SFT
Slab height	4395MM
B.O.B height	4267MM

Drawing info

Title	EXTERNAL FACADE
Designed by	RISHAD
Checked by	SOUMYA
Date	
Revision	R1
Dwg no.	

Notes:

Direction:

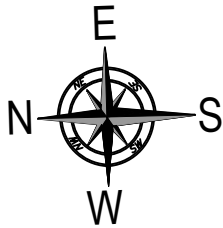



Sureena Chowdhri
-
Jaipur

Brand Info

Shop info



Market	INDIA
Province	RAJASTHAN
City	JAIPUR
City tier (tier 1/2/3)	TIER 1
Mall Name	HIGH STREET
New /Reno /Relo	NEW
FSS / SIS	FSS
Shop concept	SUREENA CHOWDHRI
Net size	957 SFT
Slab height	4395MM
B.O.B height	4267MM

Drawing info


Title	EXTERNAL FACADE
Designed by	RISHAD
Checked by	SOUMYA
Date	
Revision	R1
Dwg no.	

Notes:

Direction:

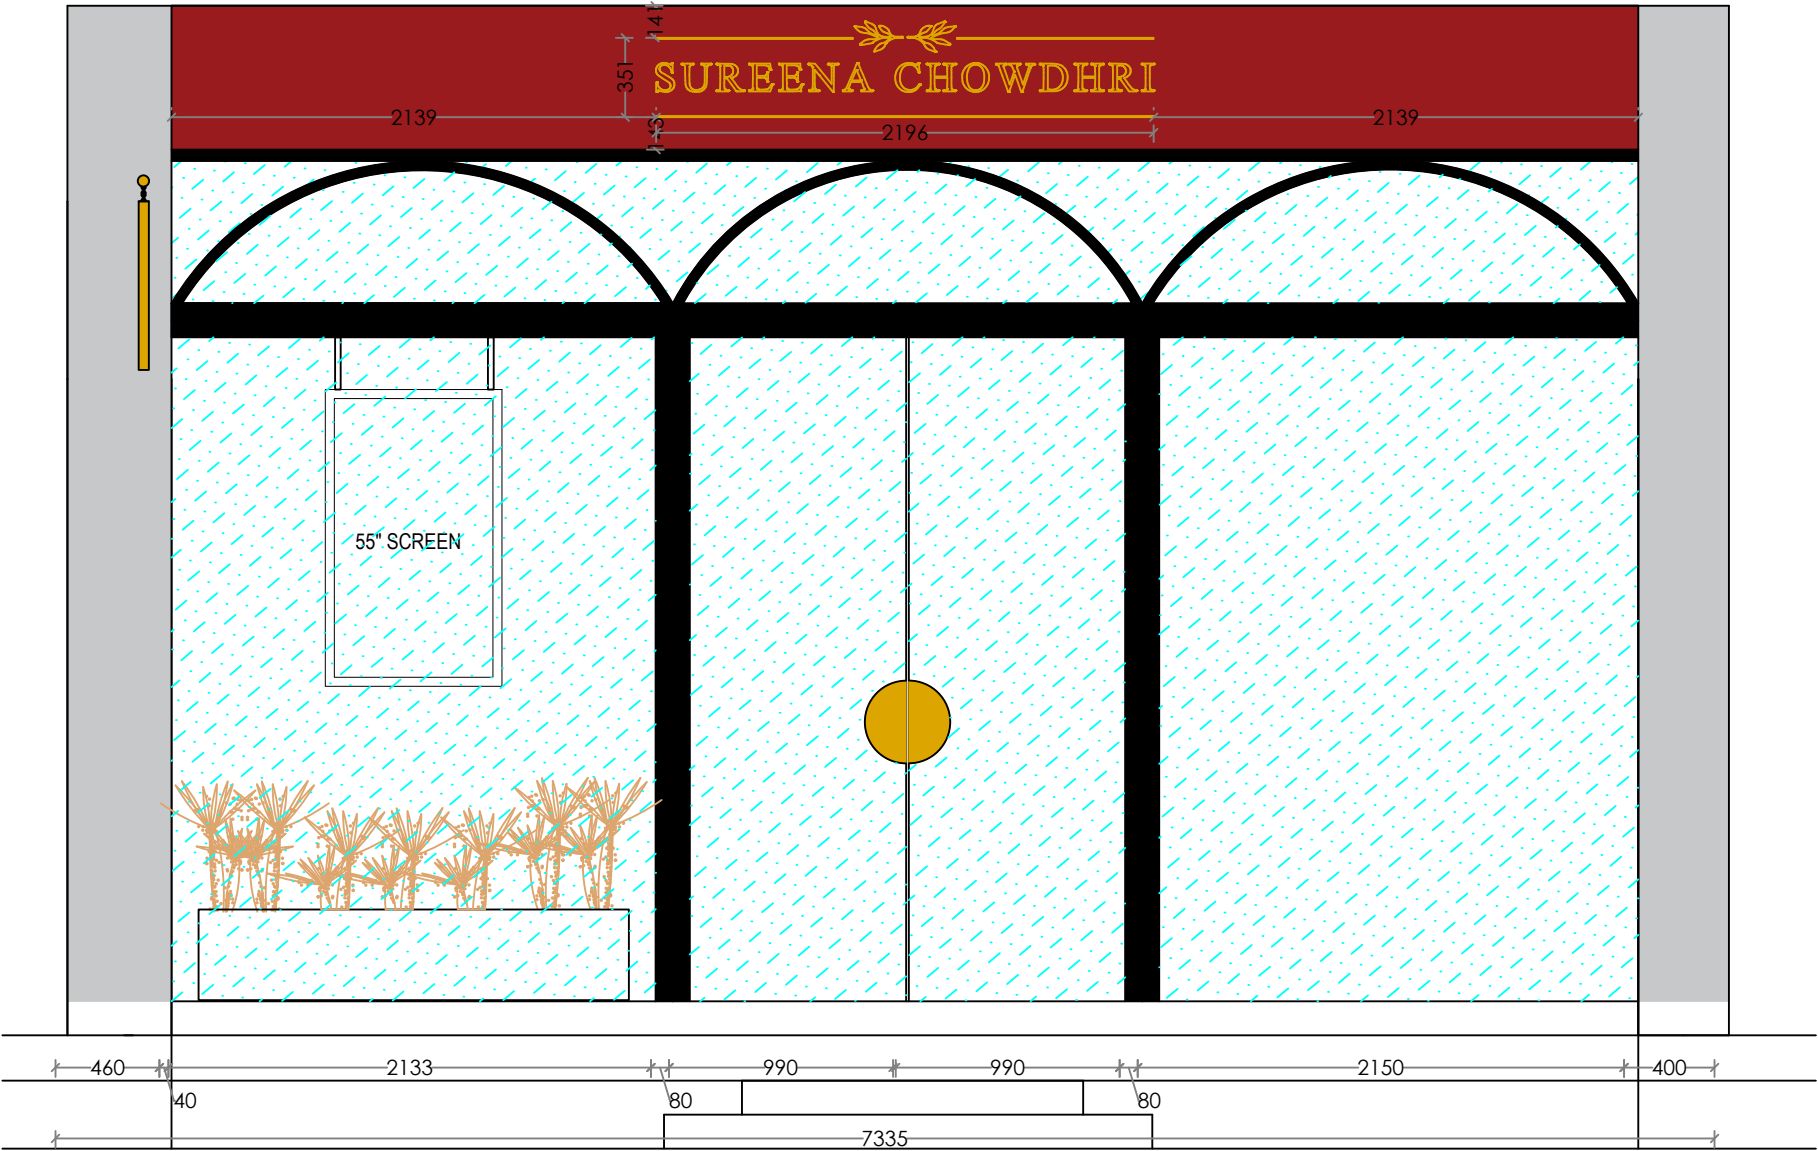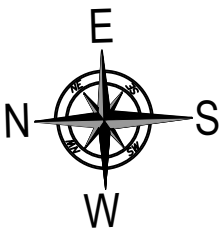


EXTERNAL FACADE ELEVATION WITH PROPOSED SIGNAGE

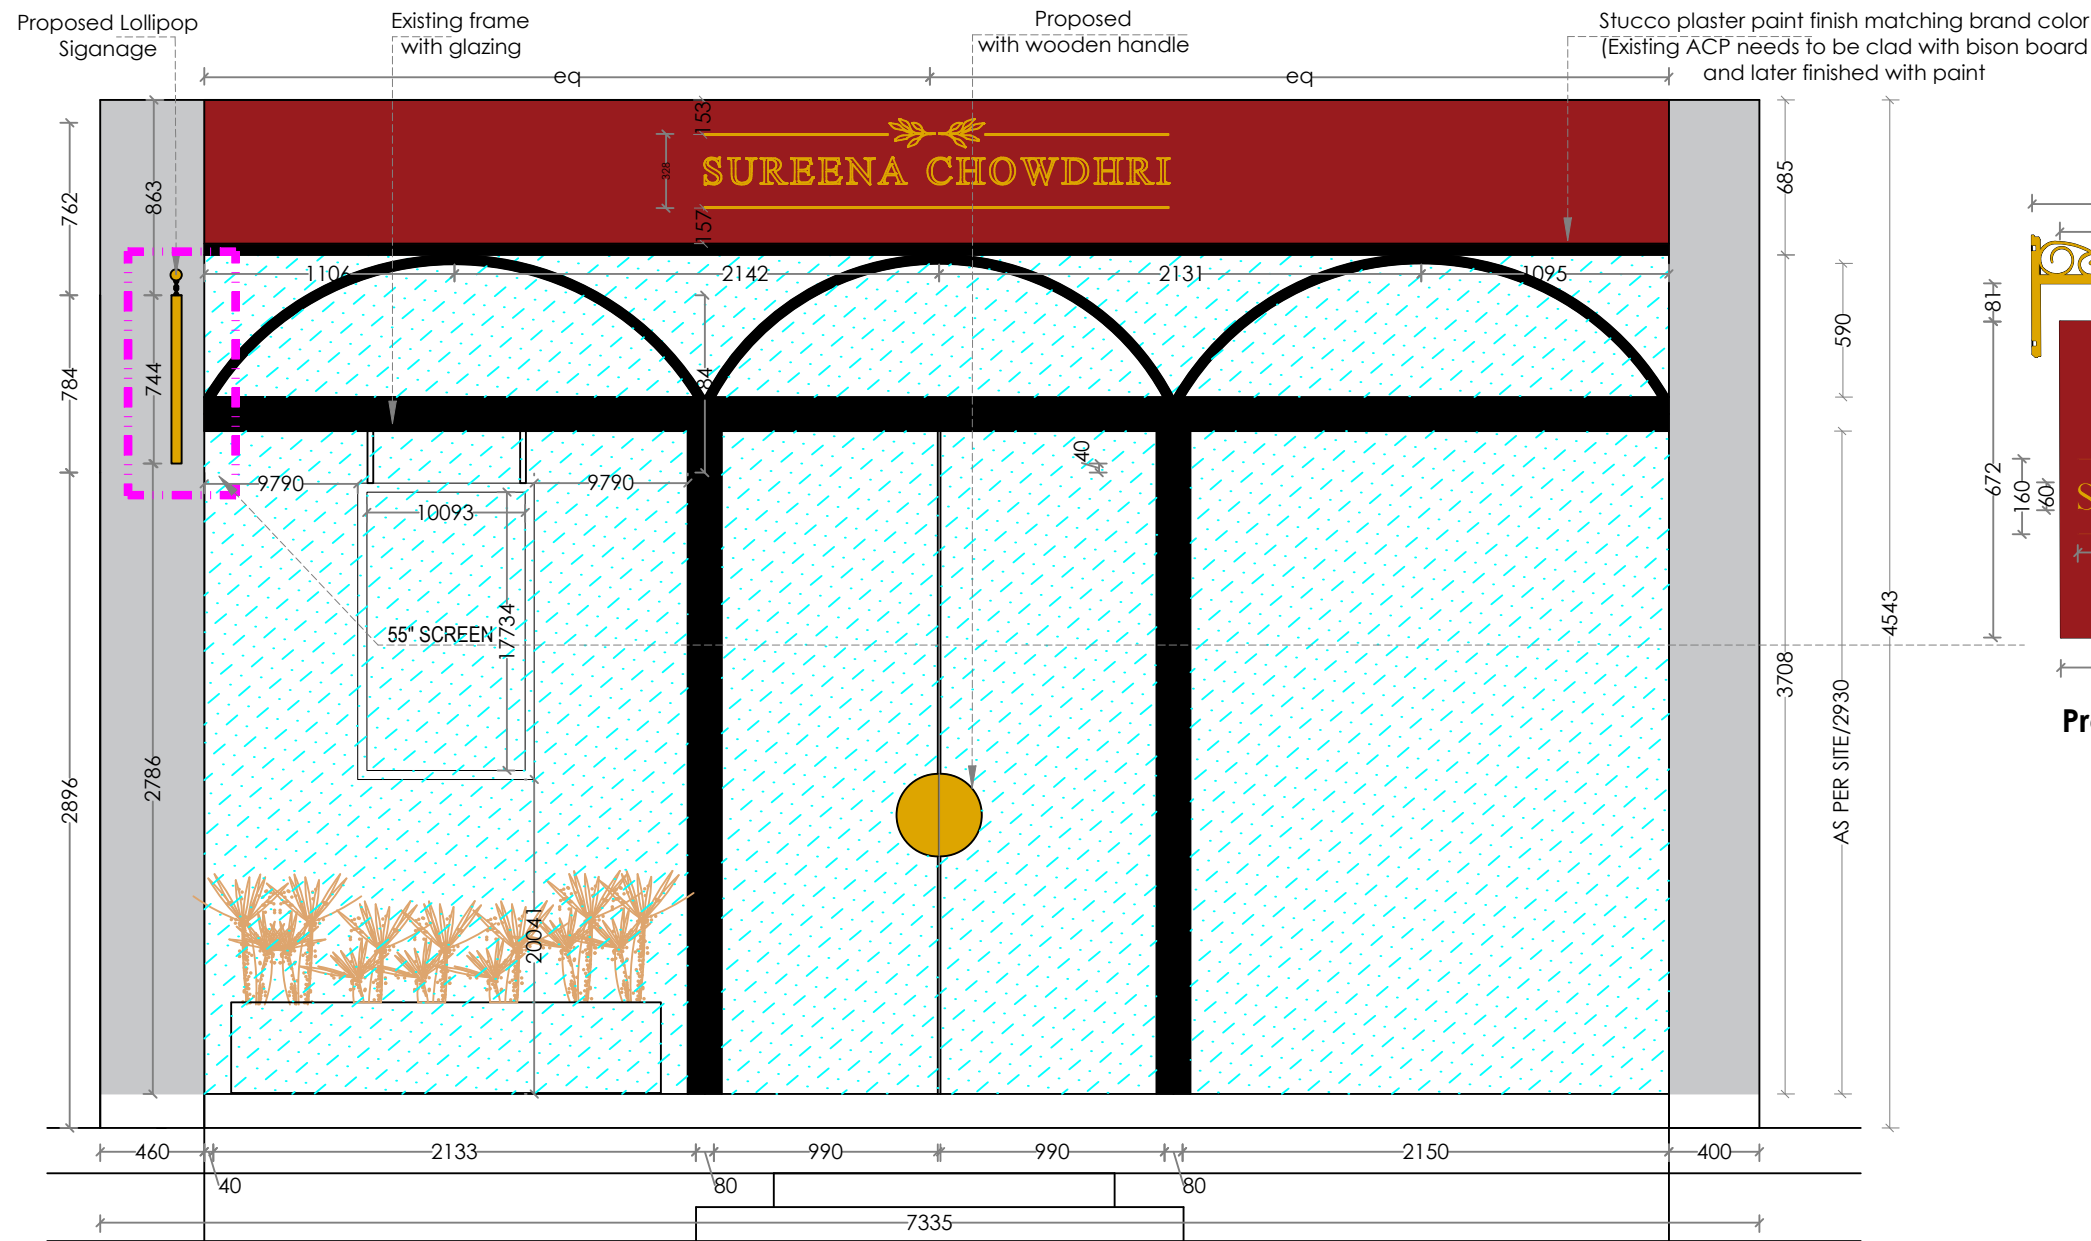

EXTERNAL FACADE ELEVATION



SIGNAGE

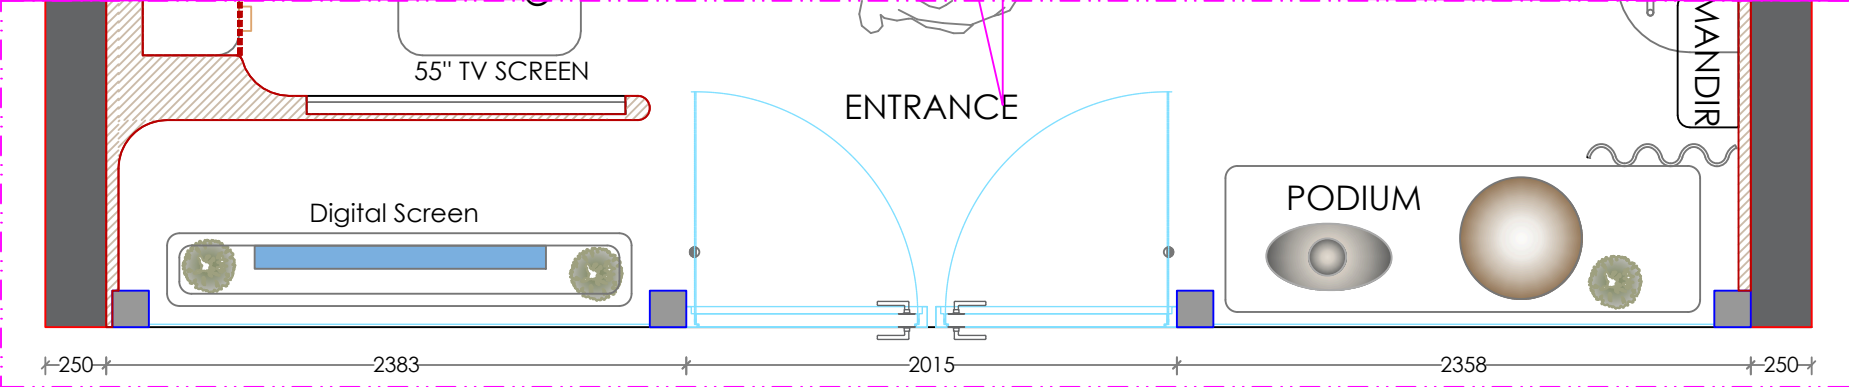

EXTERNAL FACADE PLAN



Sureena Chowdhri
-
Jaipur

Brand Info

Shop info


Market	INDIA
Province	RAJASTHAN
City	JAIPUR
City tier (tier 1/2/3)	TIER 1
Mall Name	HIGH STREET
New /Reno /Relo	NEW
FSS / SIS	FSS
Shop concept	SUREENA CHOWDHRI
Net size	957 SFT
Slab height	4395MM
B.O.B height	4267MM


Drawing info

Title	EXTERNAL FACADE
Designed by	RISHAD
Checked by	SOUMYA
Date	
Revision	R1
Dwg no.	

Notes:

Direction:

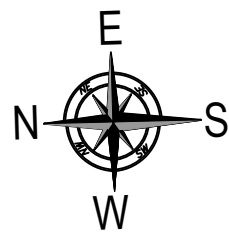

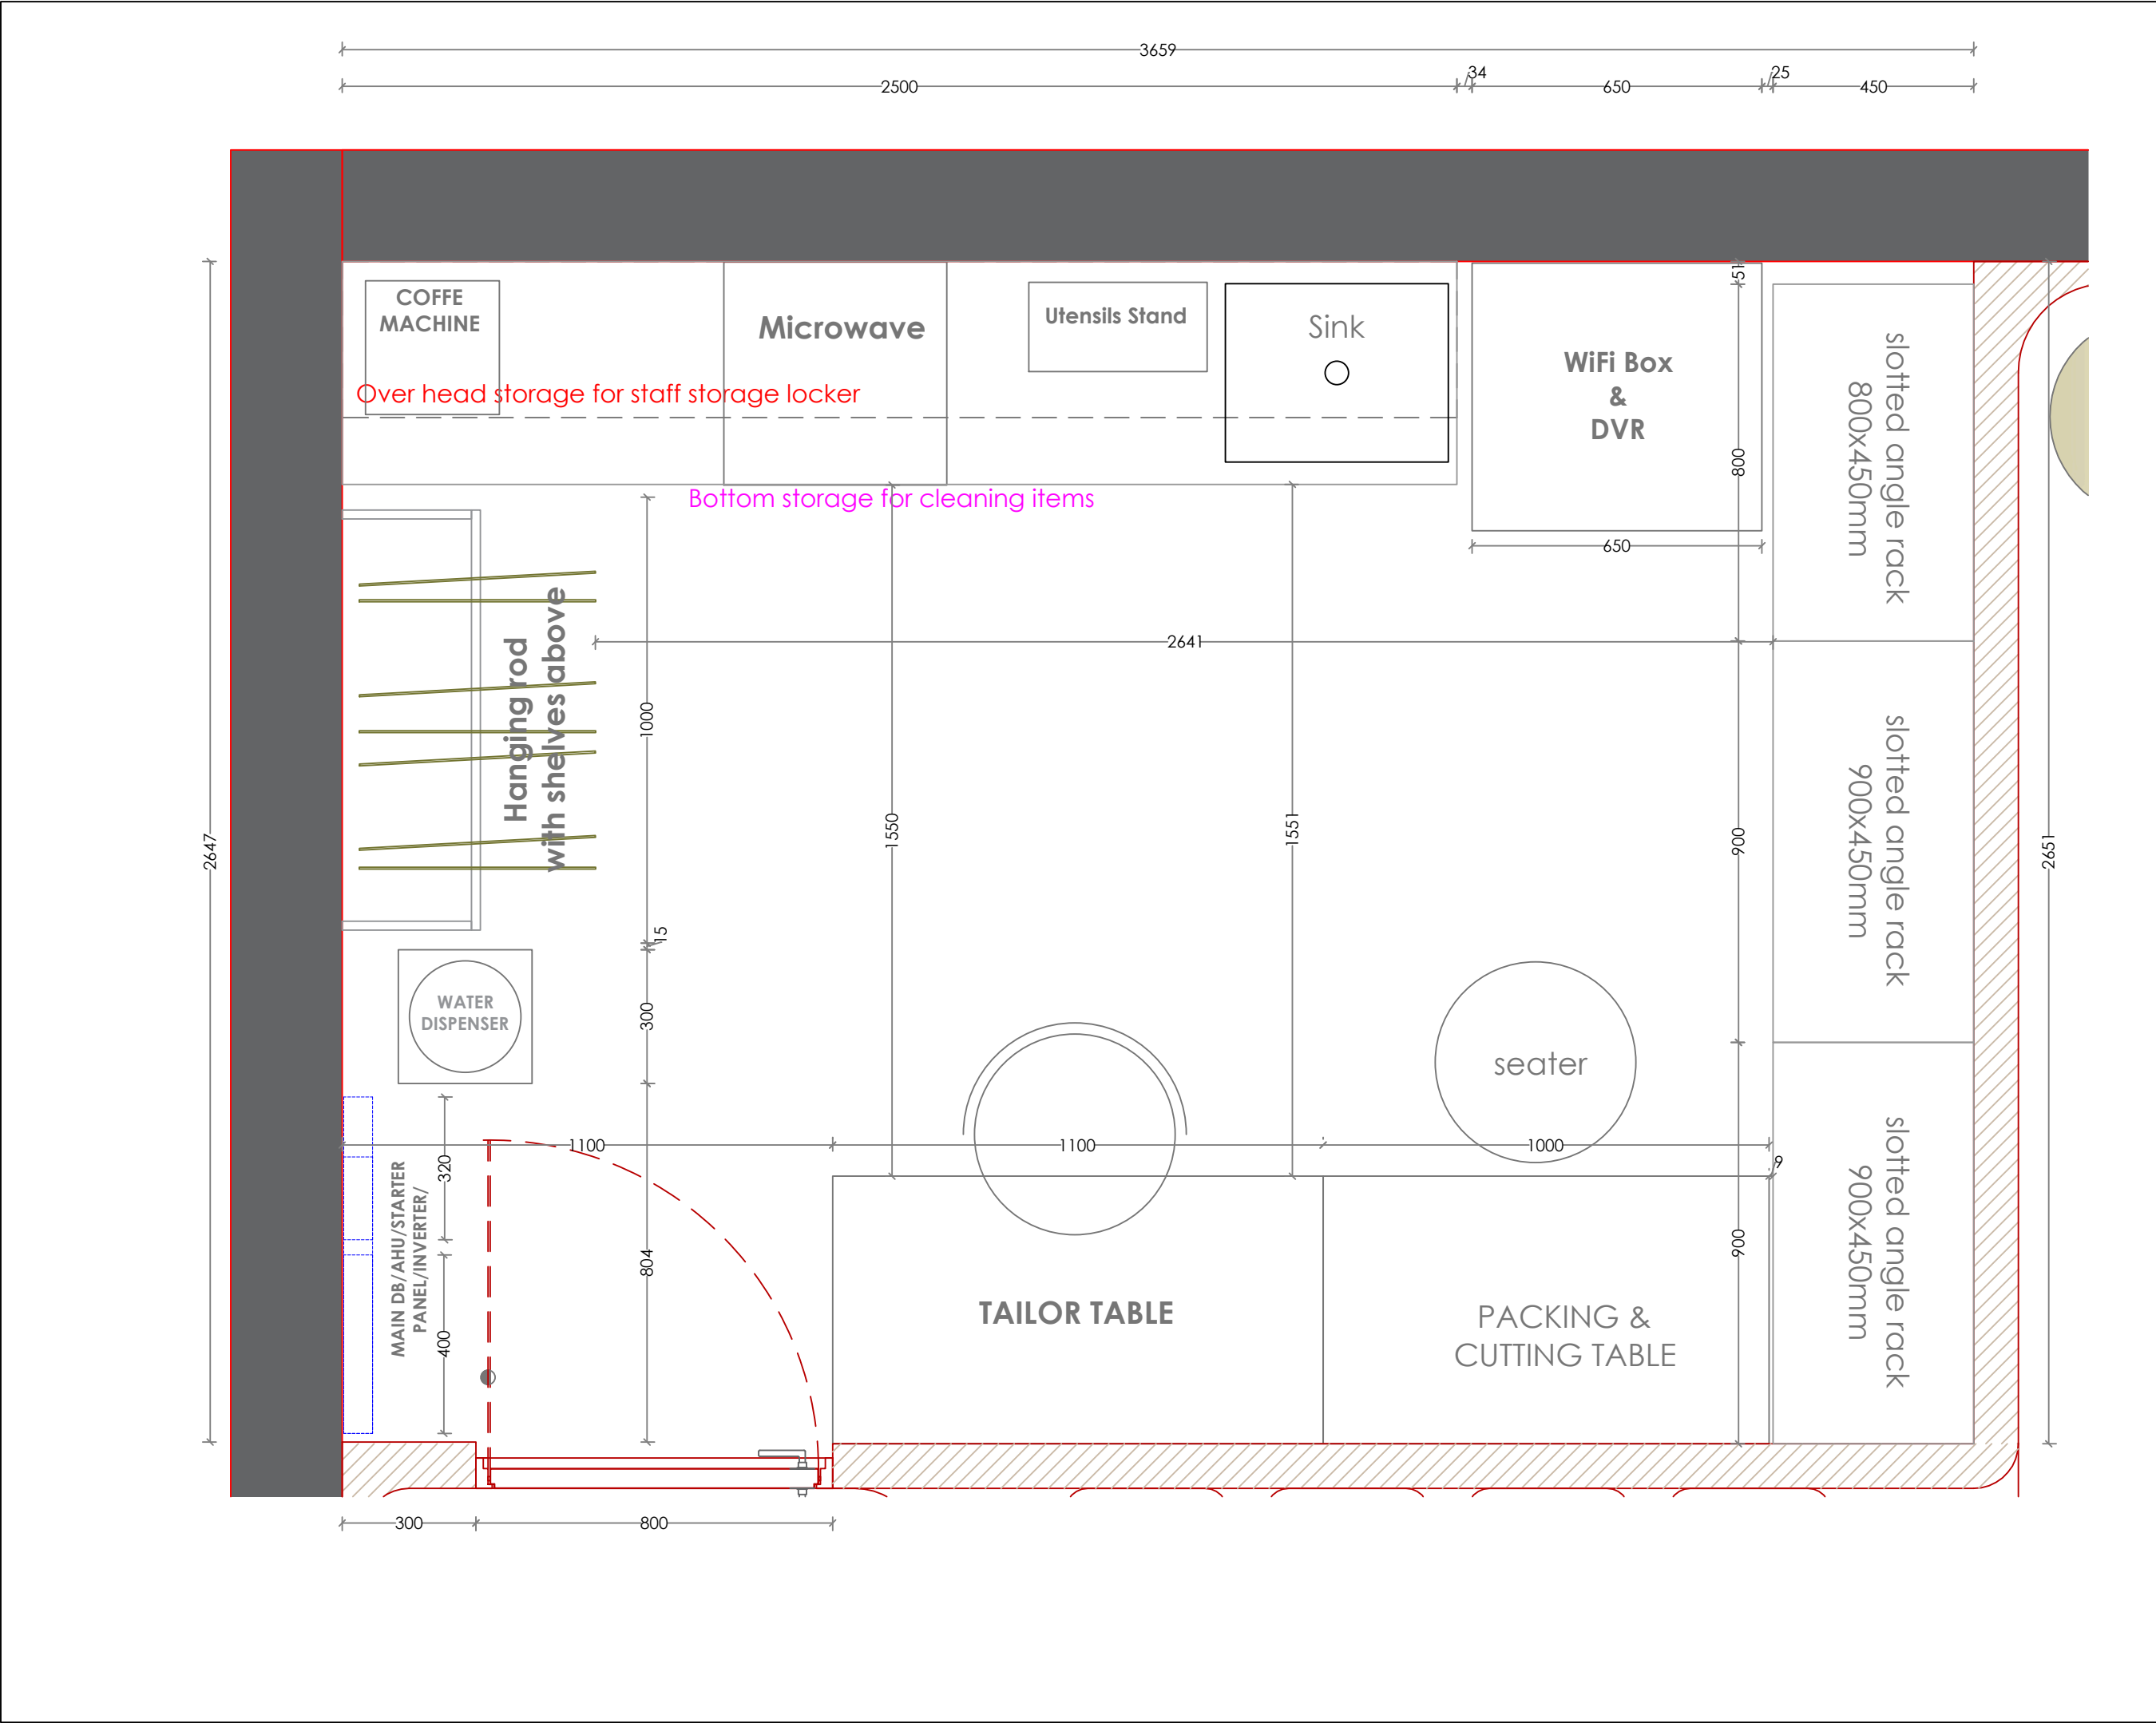

Sureena Chowdhri
-
Jaipur

Brand Info

Shop info


Market	INDIA
Province	RAJASTHAN
City	JAIPUR
City tier (tier 1/2/3)	TIER 1
Mall Name	HIGH STREET
New /Reno /Relo	NEW
FSS / SIS	FSS
Shop concept	SUREENA CHOWDHRI
Net size	957 SFT
Slab height	4395MM
B.O.B height	4267MM


Drawing info

Title	BOH LAYOUT
Designed by	RISHAD
Checked by	SOUMYA
Date	
Revision	R1
Dwg no.	

Notes:


Direction:

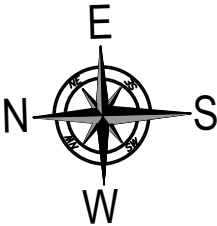

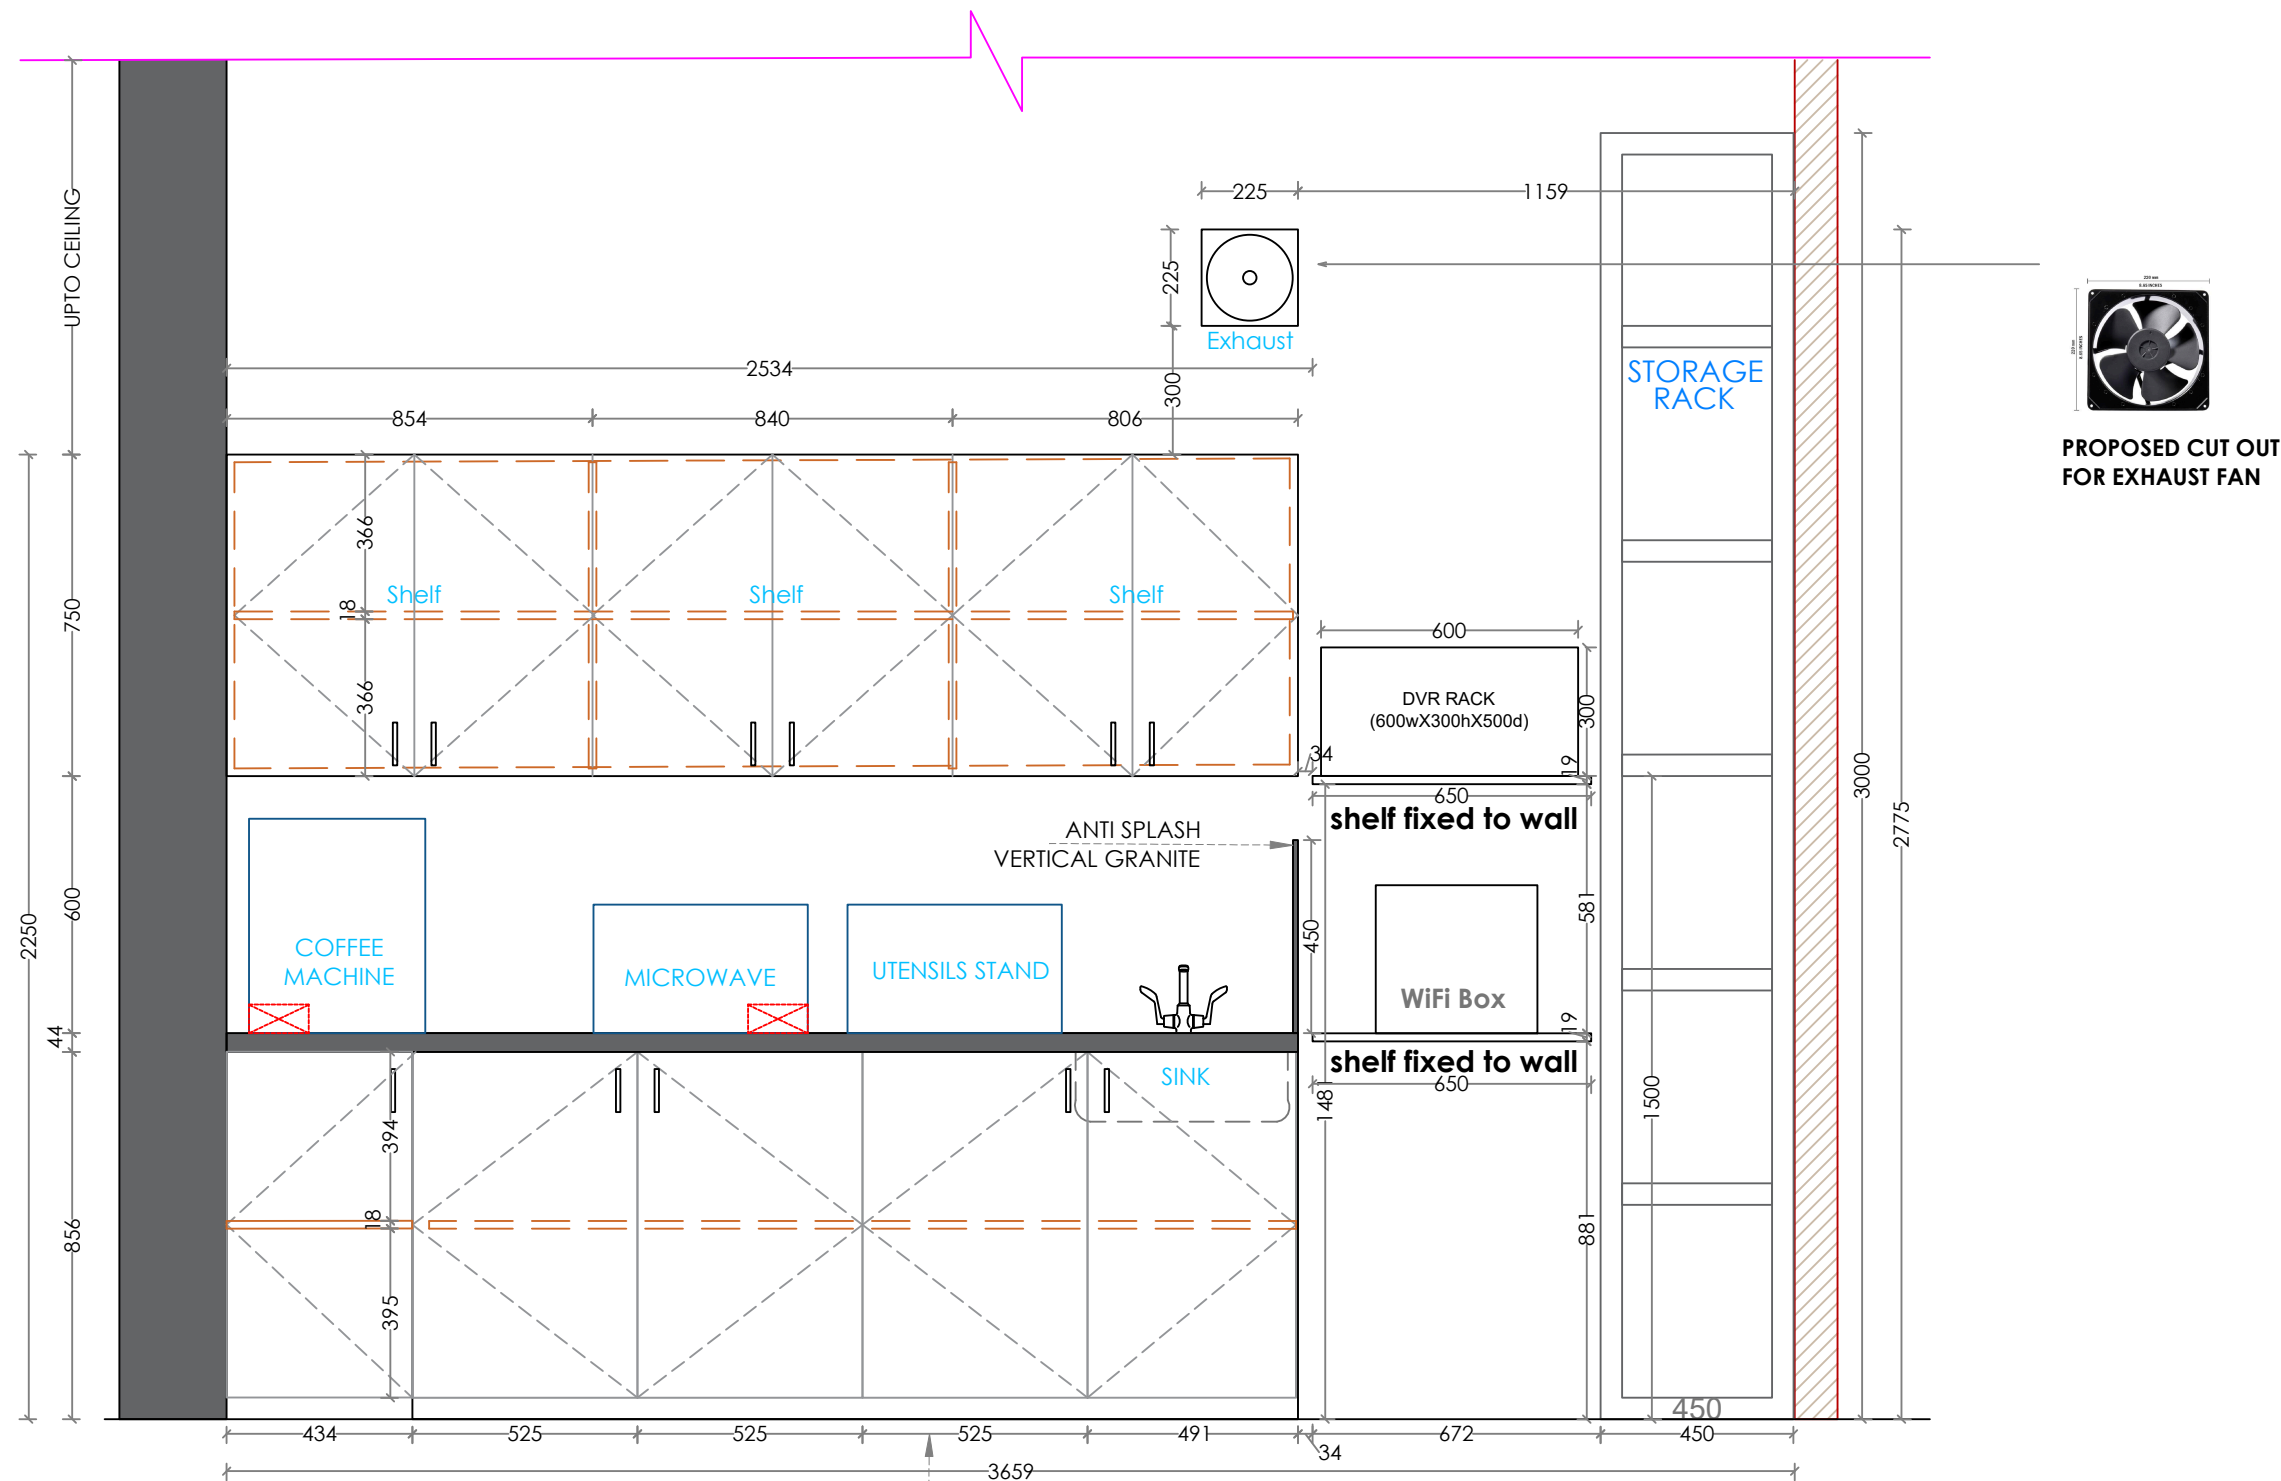

1 ELEVATION E1
Scale: NTS

CABINETS/DOORS
AND SHELVES IN MDF
FINISHED WITH
LAMINATE
GREENLAM - FROSTY
WHITE 107

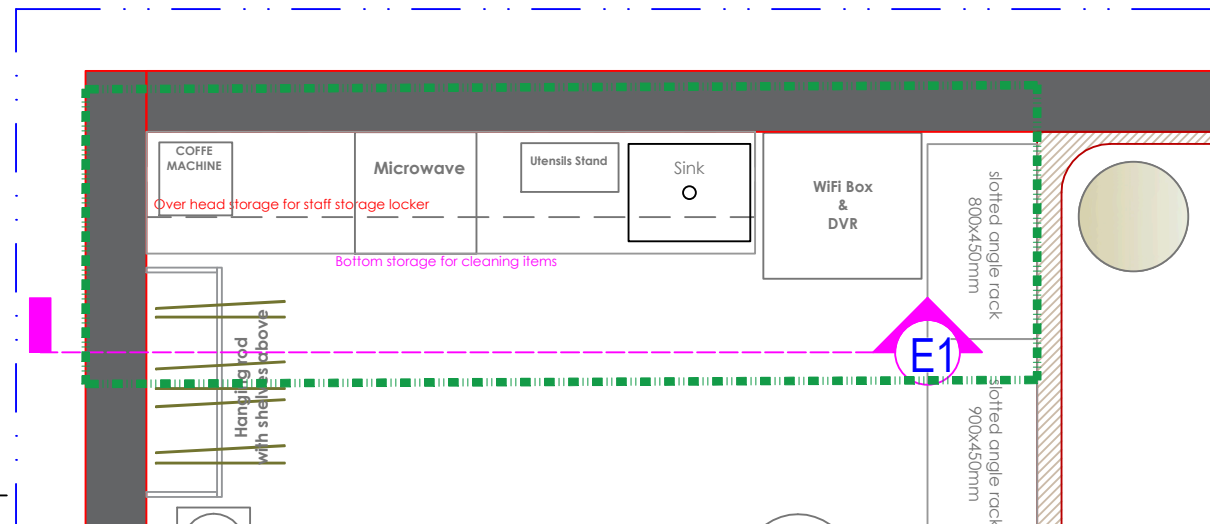

1 KEY PLAN
Scale: NTS



Sureena Chowdhri
-
Jaipur

Brand Info

Shop info


Market	INDIA
Province	RAJASTHAN
City	JAIPUR
City tier (tier 1/2/3)	TIER 1
Mall Name	HIGH STREET
New /Reno /Relo	NEW
FSS / SIS	FSS
Shop concept	SUREENA CHOWDHRI
Net size	957 SFT
Slab height	4395MM
B.O.B height	4267MM

Drawing info

Title	BOH ELEVATION 1
Designed by	RISHAD
Checked by	SOUMYA
Date	
Revision	R1
Dwg no.	

Notes:

Direction:

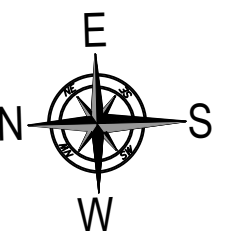



Sureena Chowdhri
-
Jaipur

Brand Info

Shop info




Market	INDIA
Province	RAJASTHAN
City	JAIPUR
City tier (tier 1/2/3)	TIER 1
Mall Name	HIGH STREET
New /Reno /Relo	NEW
FSS / SIS	FSS
Shop concept	SUREENA CHOWDHRI
Net size	957 SFT
Slab height	4395MM
B.O.B height	4267MM

Drawing info


Title	BOH ELEVATION 2
Designed by	RISHAD
Checked by	SOUMYA
Date	
Revision	R1
Dwg no.	

Notes:



Direction:

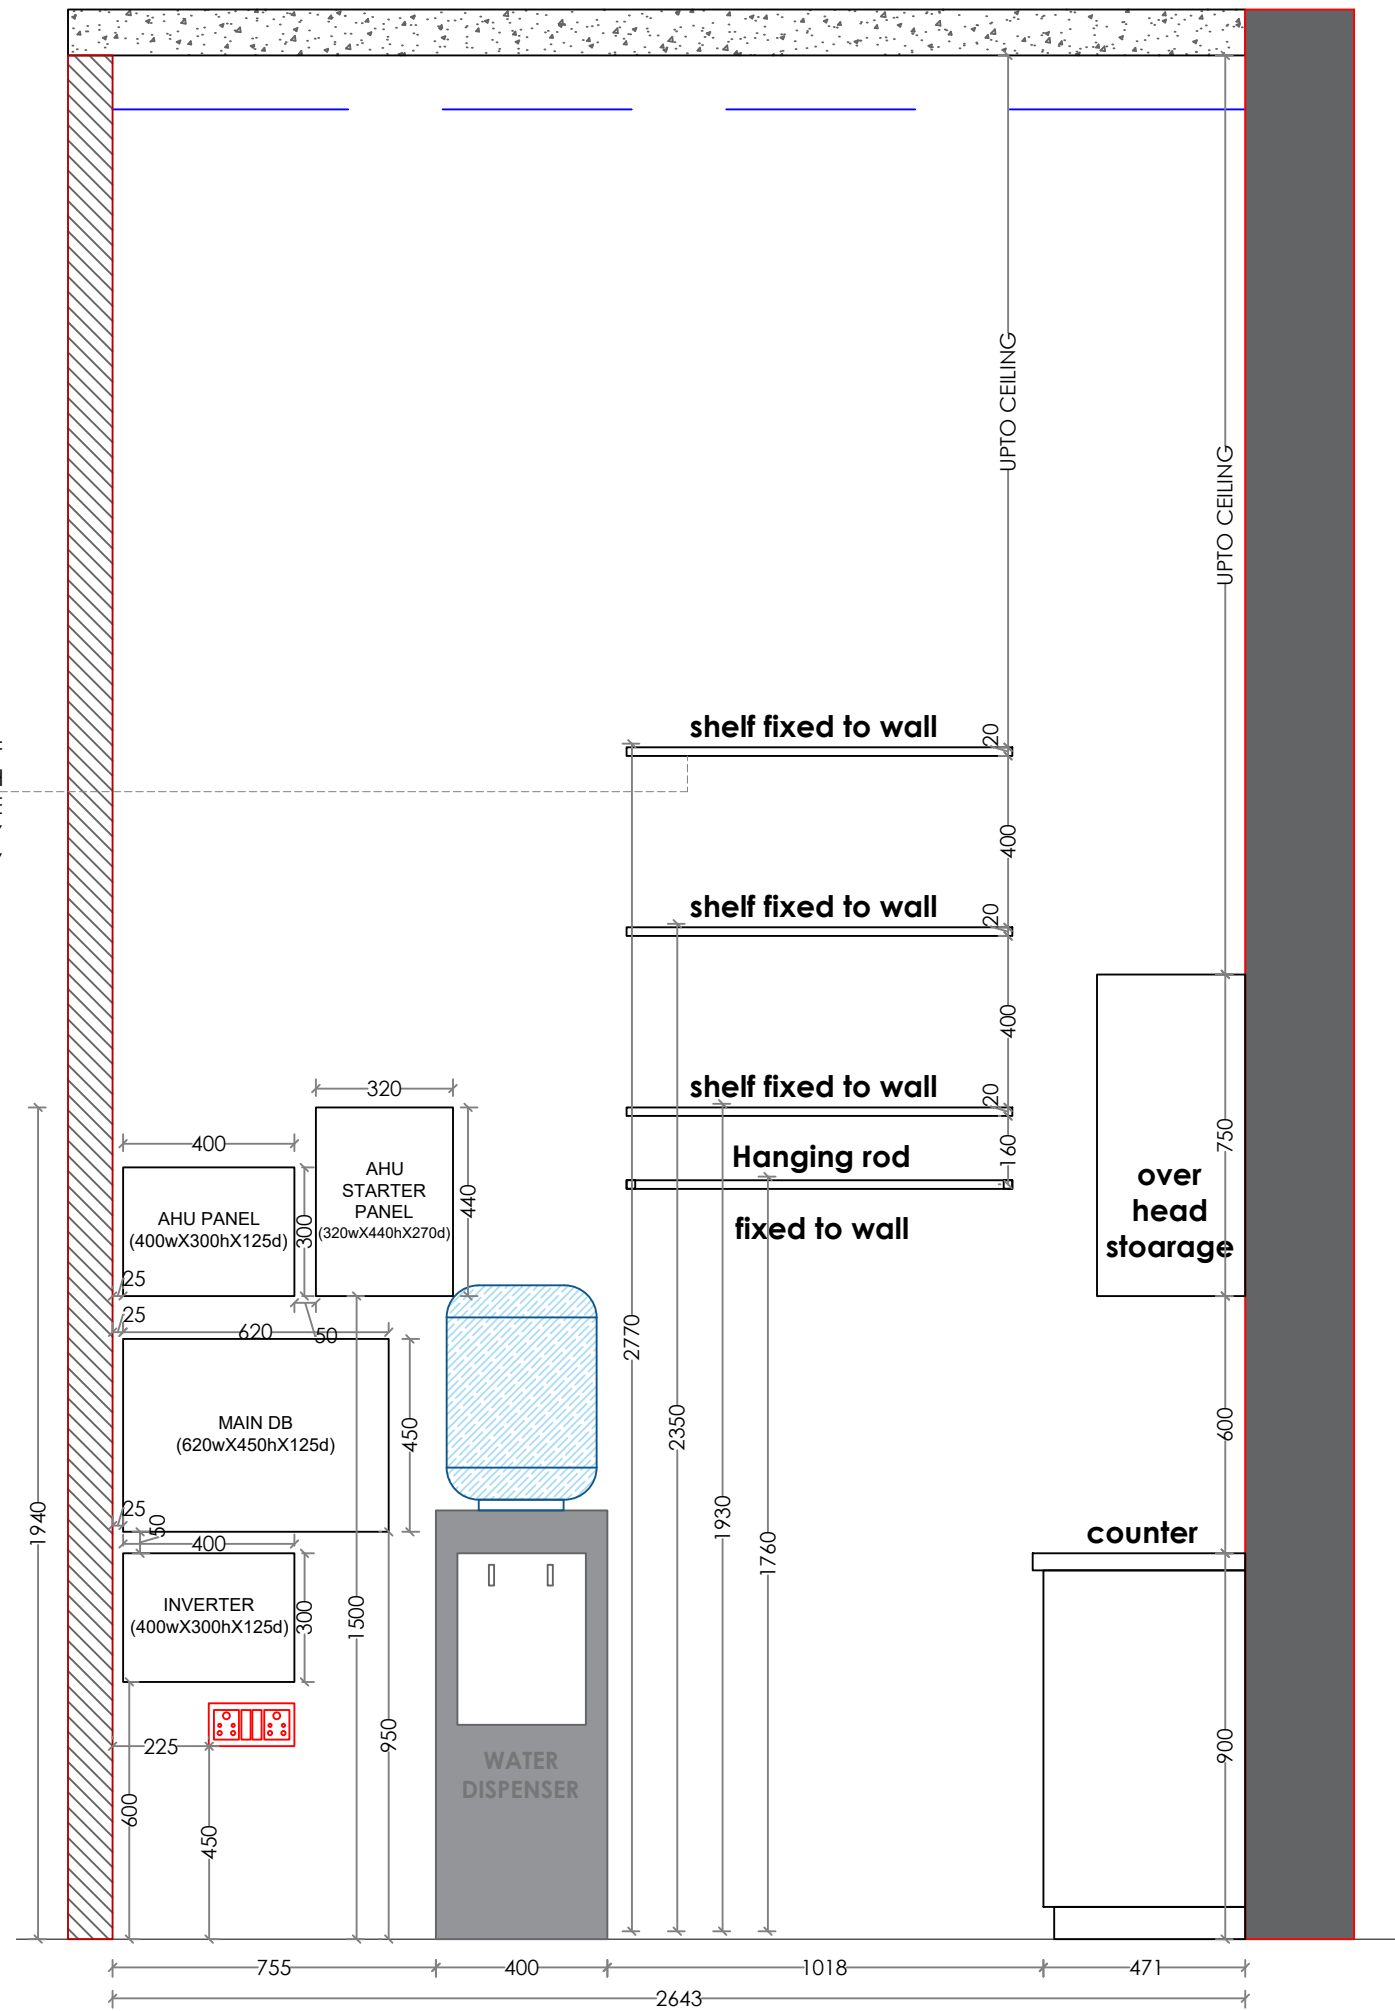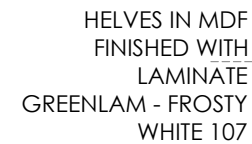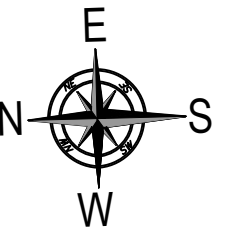

2 ELEVATION E2
Scale: NTS

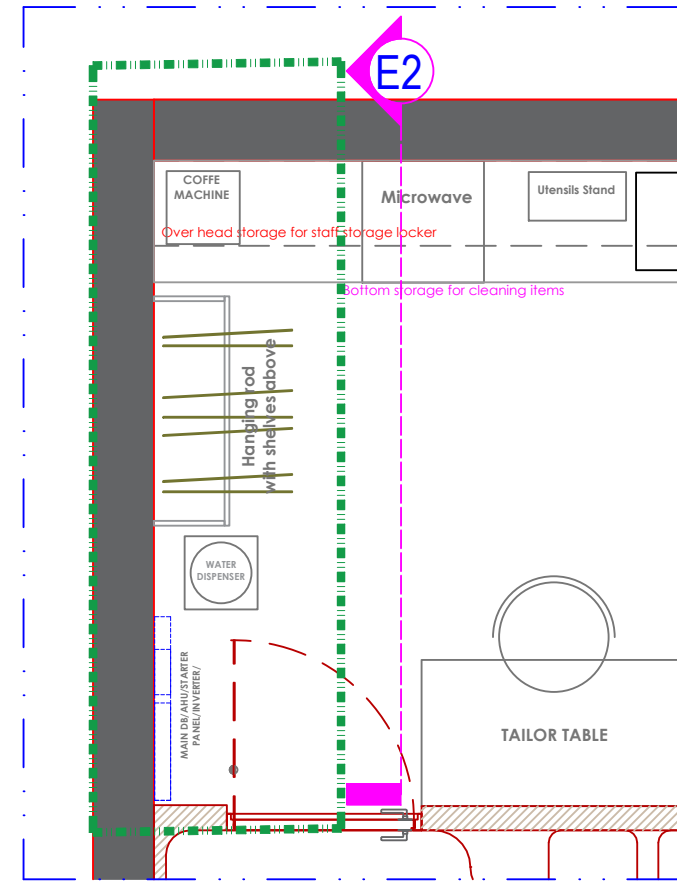

1 KEY PLAN

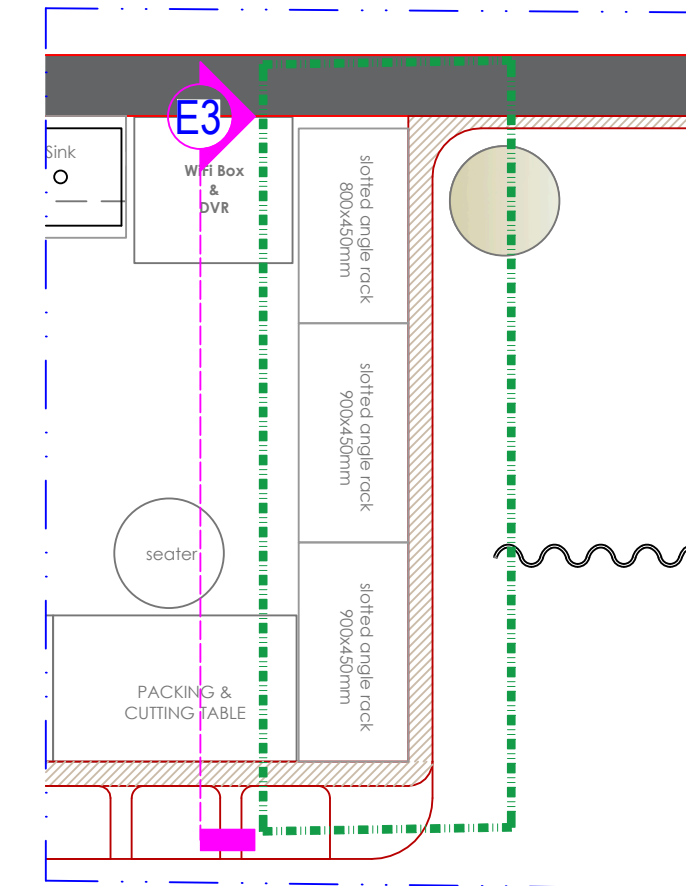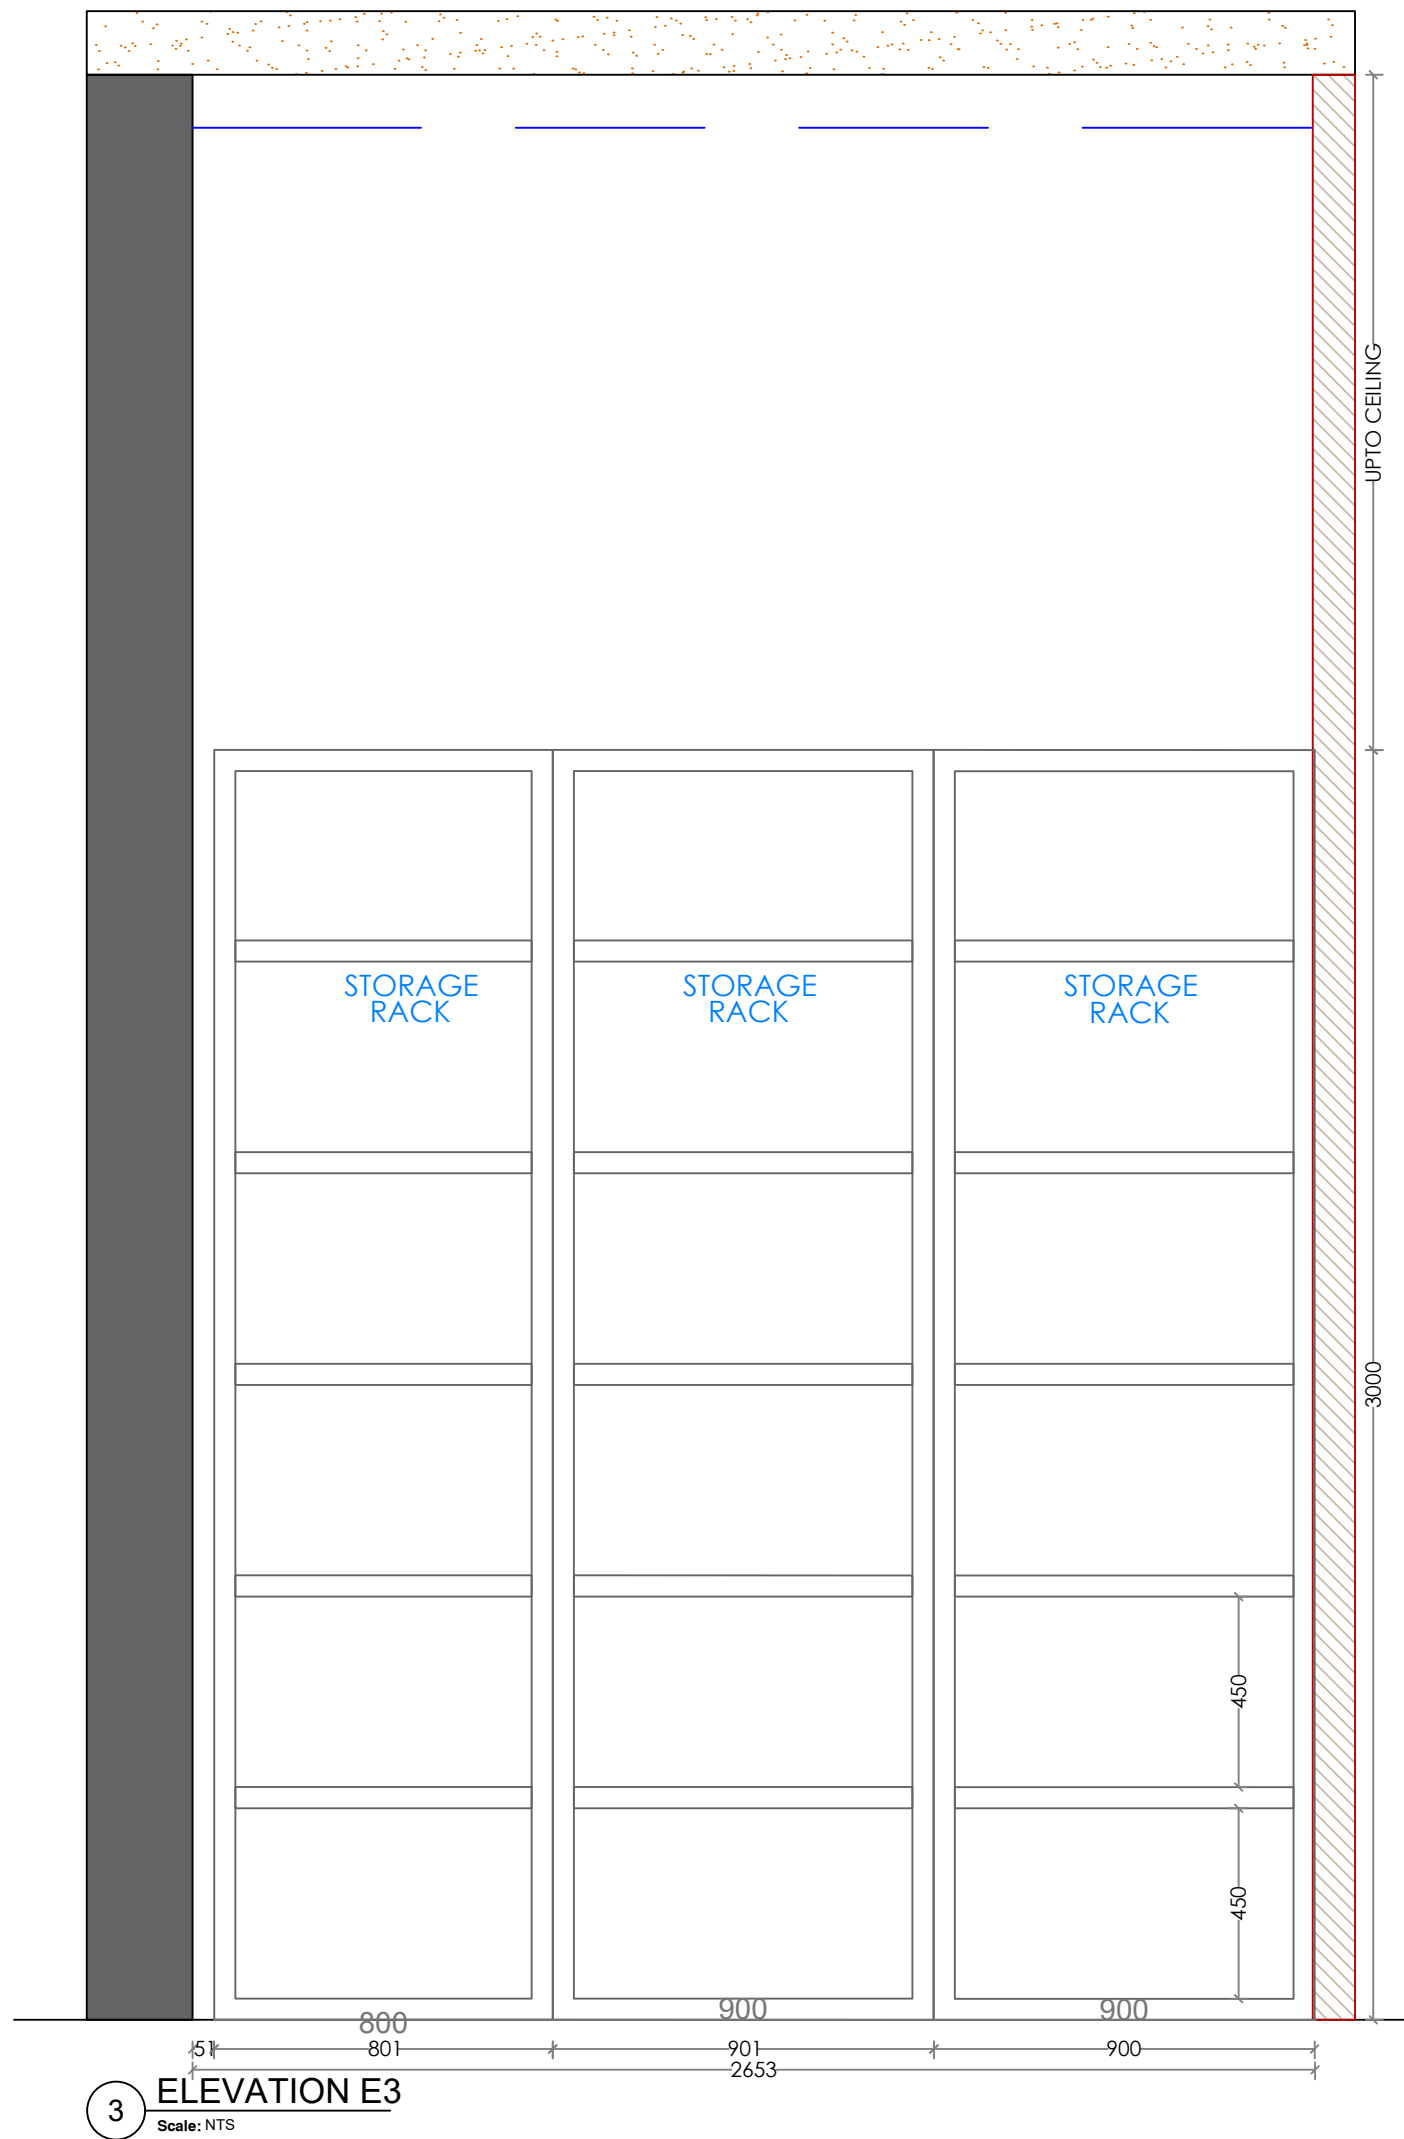

Sureena Chowdhri
-
Jaipur

Brand Info

Shop info


Market	INDIA
Province	RAJASTHAN
City	JAIPUR
City tier (tier 1/2/3)	TIER 1
Mall Name	HIGH STREET
New /Reno /Relo	NEW
FSS / SIS	FSS
Shop concept	SUREENA CHOWDHRI
Net size	957 SFT
Slab height	4395MM
B.O.B height	4267MM

Drawing info

Title	BOH ELEVATION 3
Designed by	RISHAD
Checked by	SOUMYA
Date	
Revision	R1
Dwg no.	

Notes:

Direction:

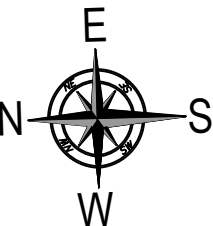



Sureena Chowdhri
-
Jaipur

Brand Info

Shop info


Market	INDIA
Province	RAJASTHAN
City	JAIPUR
City tier (tier 1/2/3)	TIER 1
Mall Name	HIGH STREET
New /Reno /Relo	NEW
FSS / SIS	FSS
Shop concept	SUREENA CHOWDHRI
Net size	957 SFT
Slab height	4395MM
B.O.B height	4267MM

Drawing info


Title	BOH ELEVATION 4
Designed by	RISHAD
Checked by	SOUMYA
Date	
Revision	R1
Dwg no.	

Notes:


Direction:

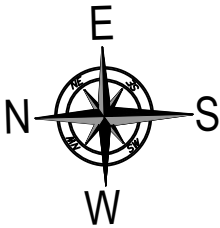


REFERENCE IMAGE -PACKAGING AND CUTTING TABLE

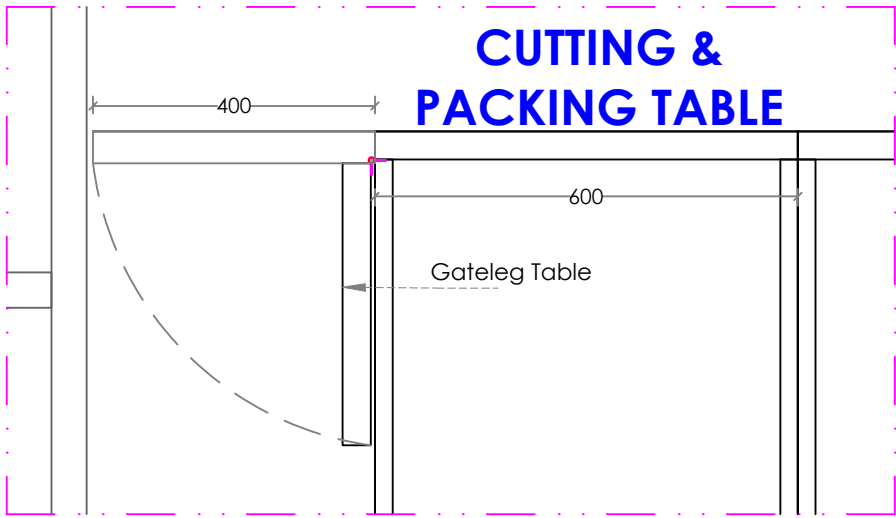


DETAIL A

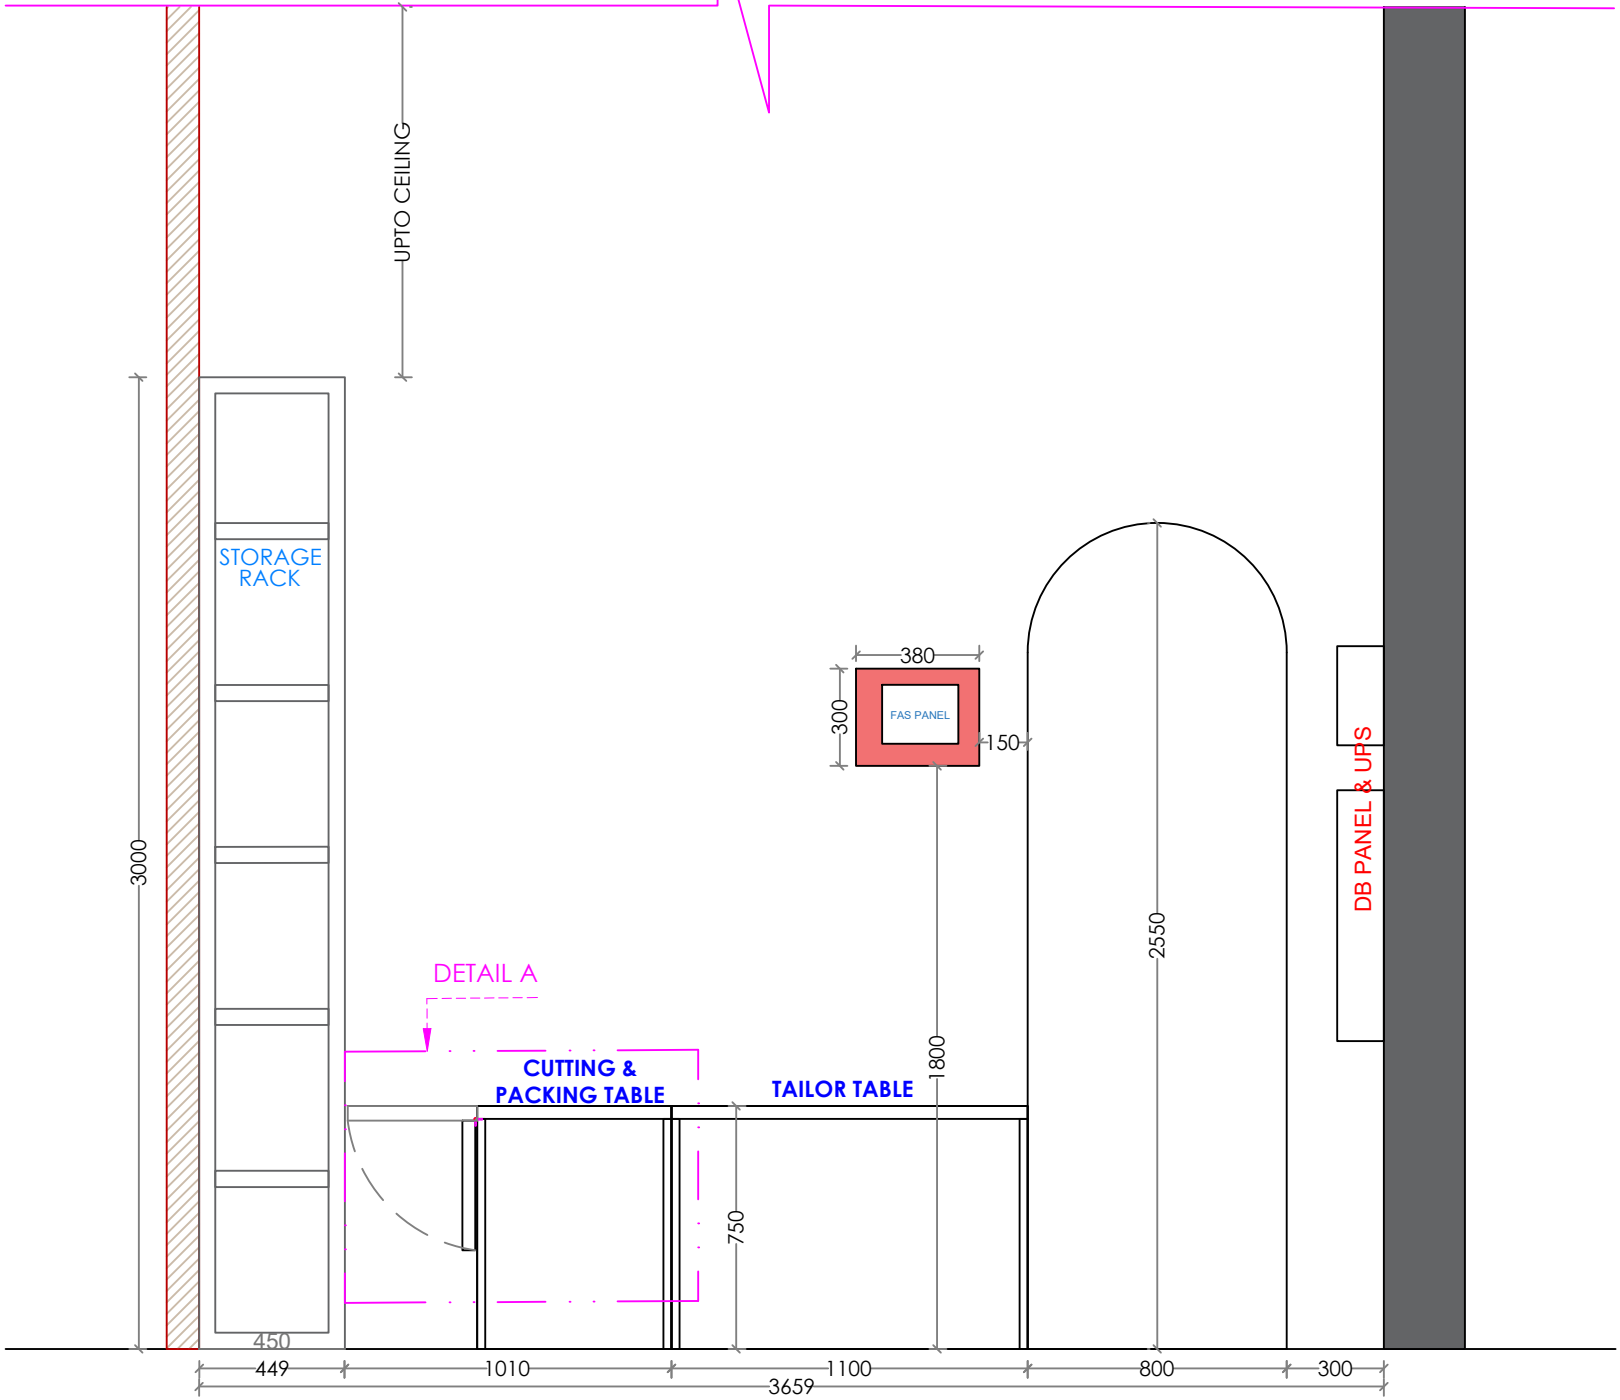


4 ELEVATION E4
Scale: NTS

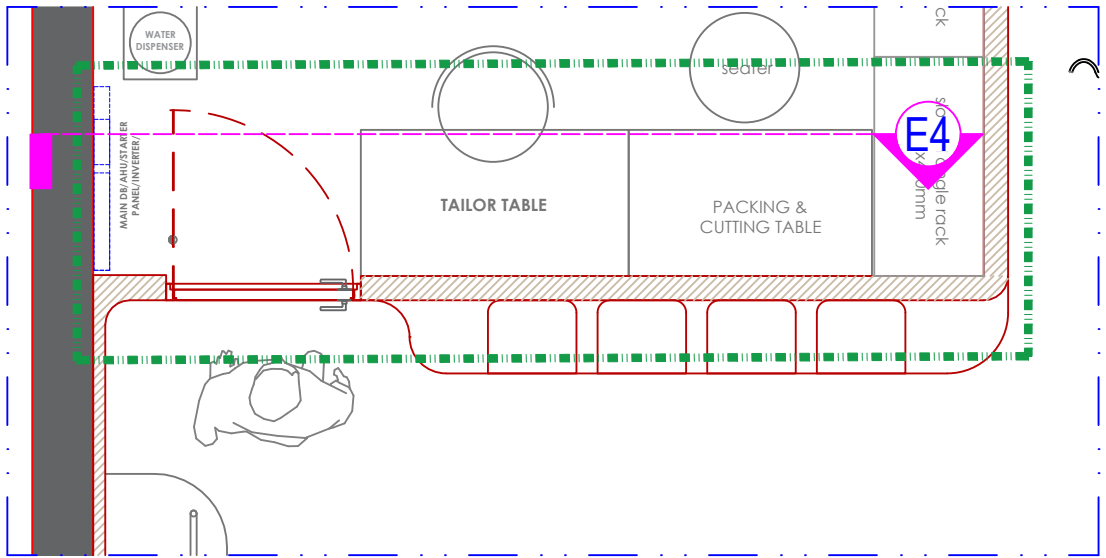


1 KEY PLAN
Scale: NTS

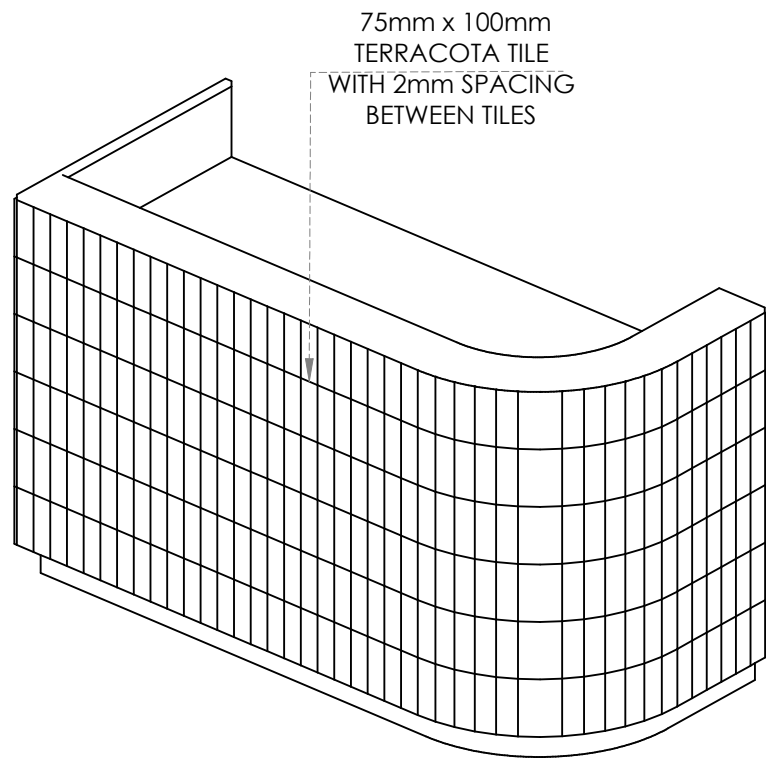


ISO - FRONT VEIW

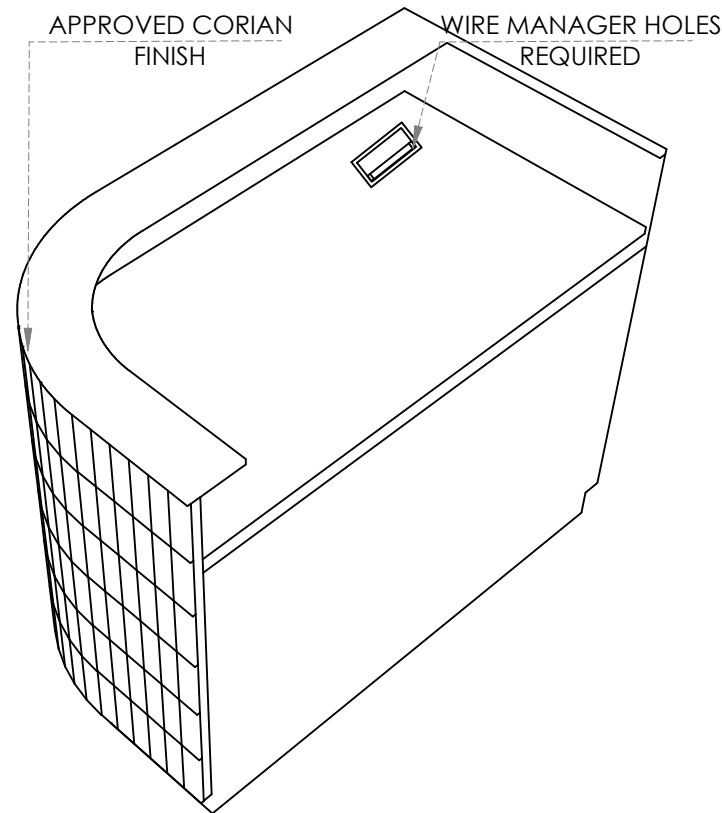


ISO - REAR VEIW

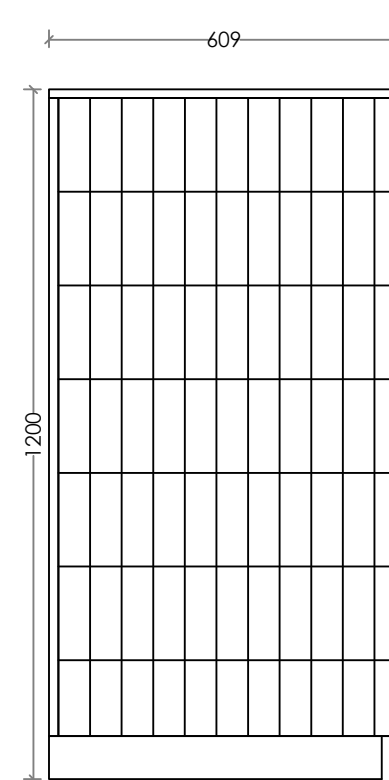


SIDE VEIW

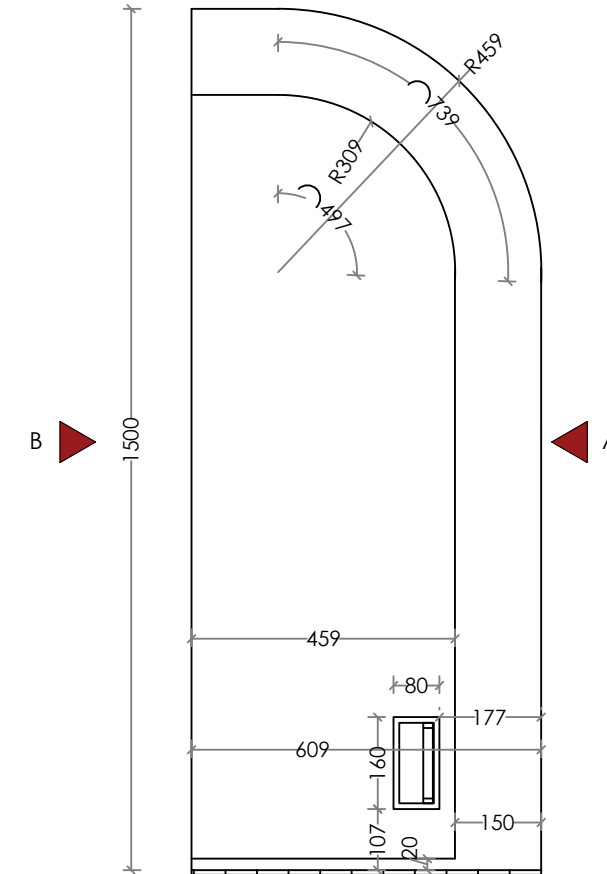

TOP VEIW

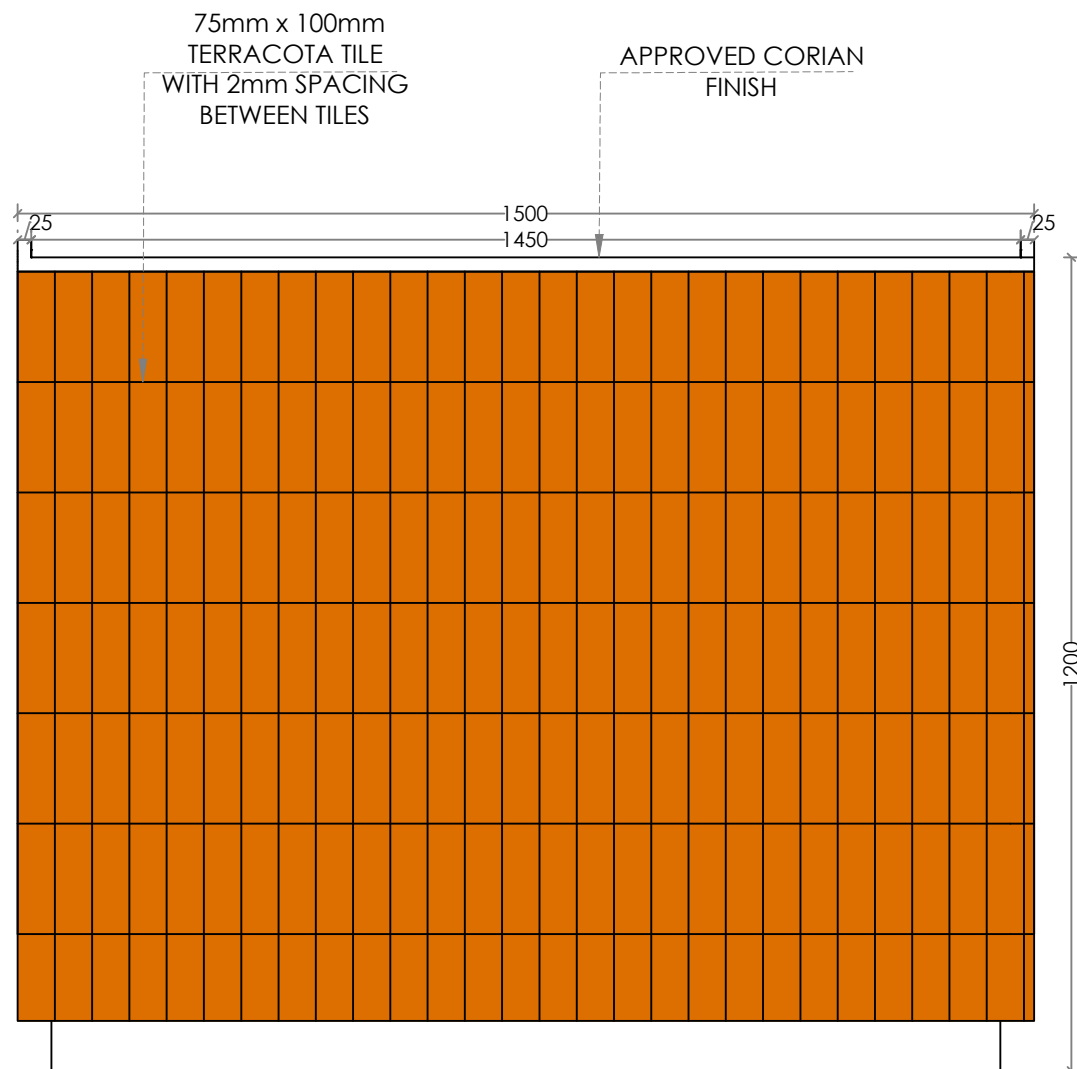

FRONT VEIW(A)

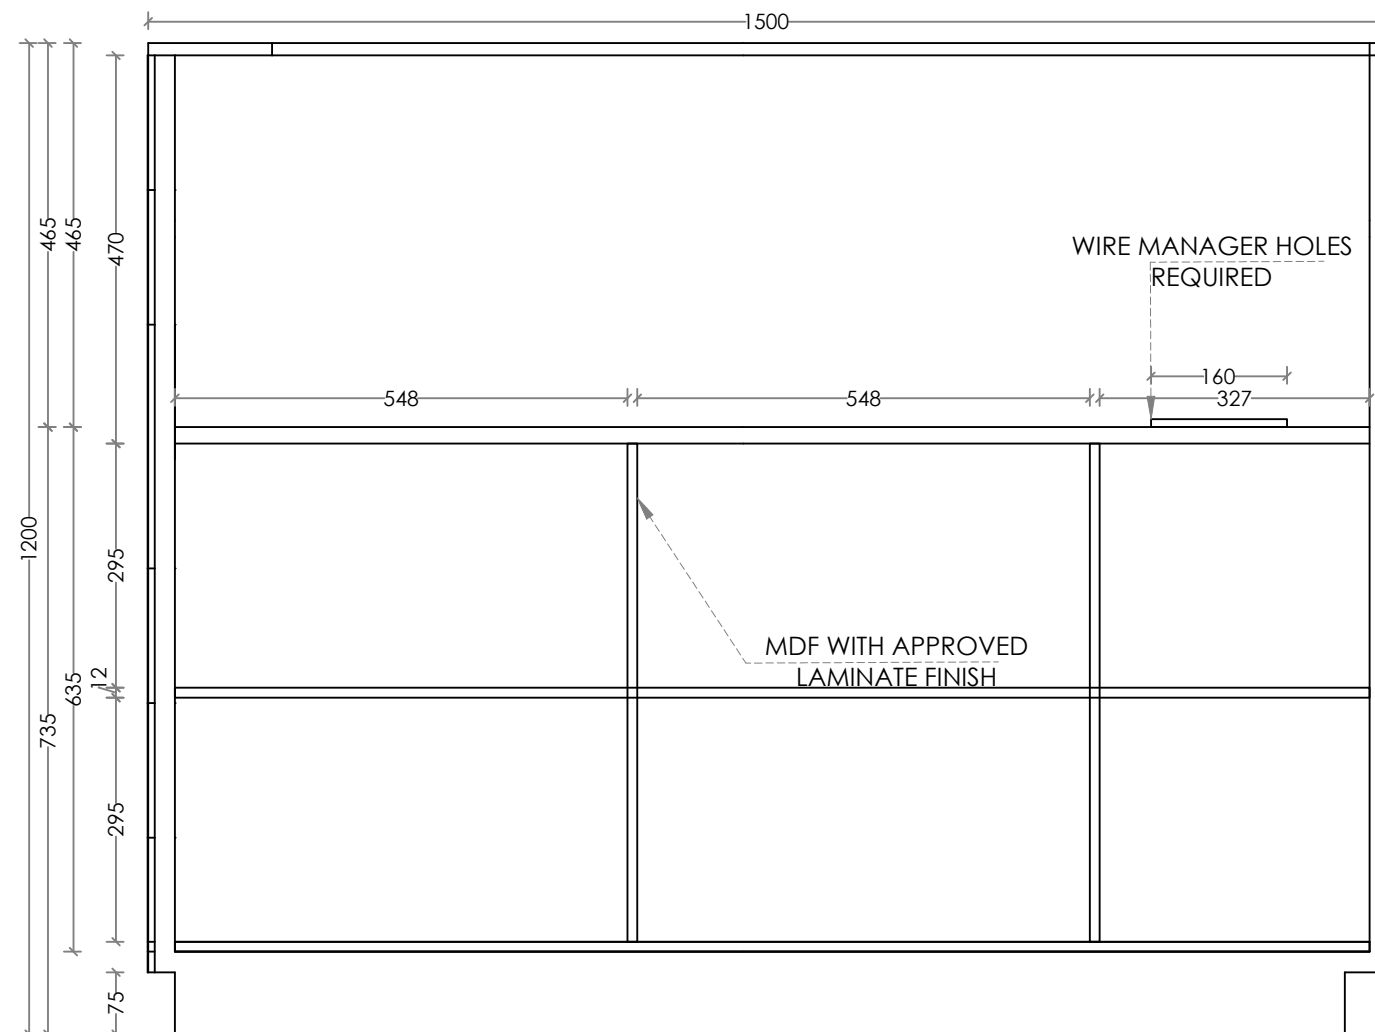

BACK VEIW(B)



Sureena Chowdhri
-
Jaipur

Brand Info


Market	INDIA
Province	RAJASTHAN
City	JAIPUR
City tier (tier 1/2/3)	TIER 1
Mall Name	HIGH STREET
New /Reno /Relo	NEW
FSS / SIS	FSS
Shop concept	SUREENA CHOWDHRI
Net size	957 SFT
Slab height	4395MM
B.O.B height	4267MM


Drawing info

Title	CASH COUNTER DWG
Designed by	RISHAD
Checked by	SOUMYA
Date	
Revision	R1
Dwg no.	


Notes:

Direction:

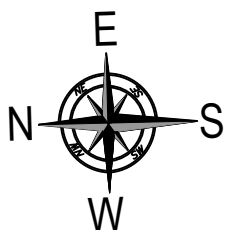


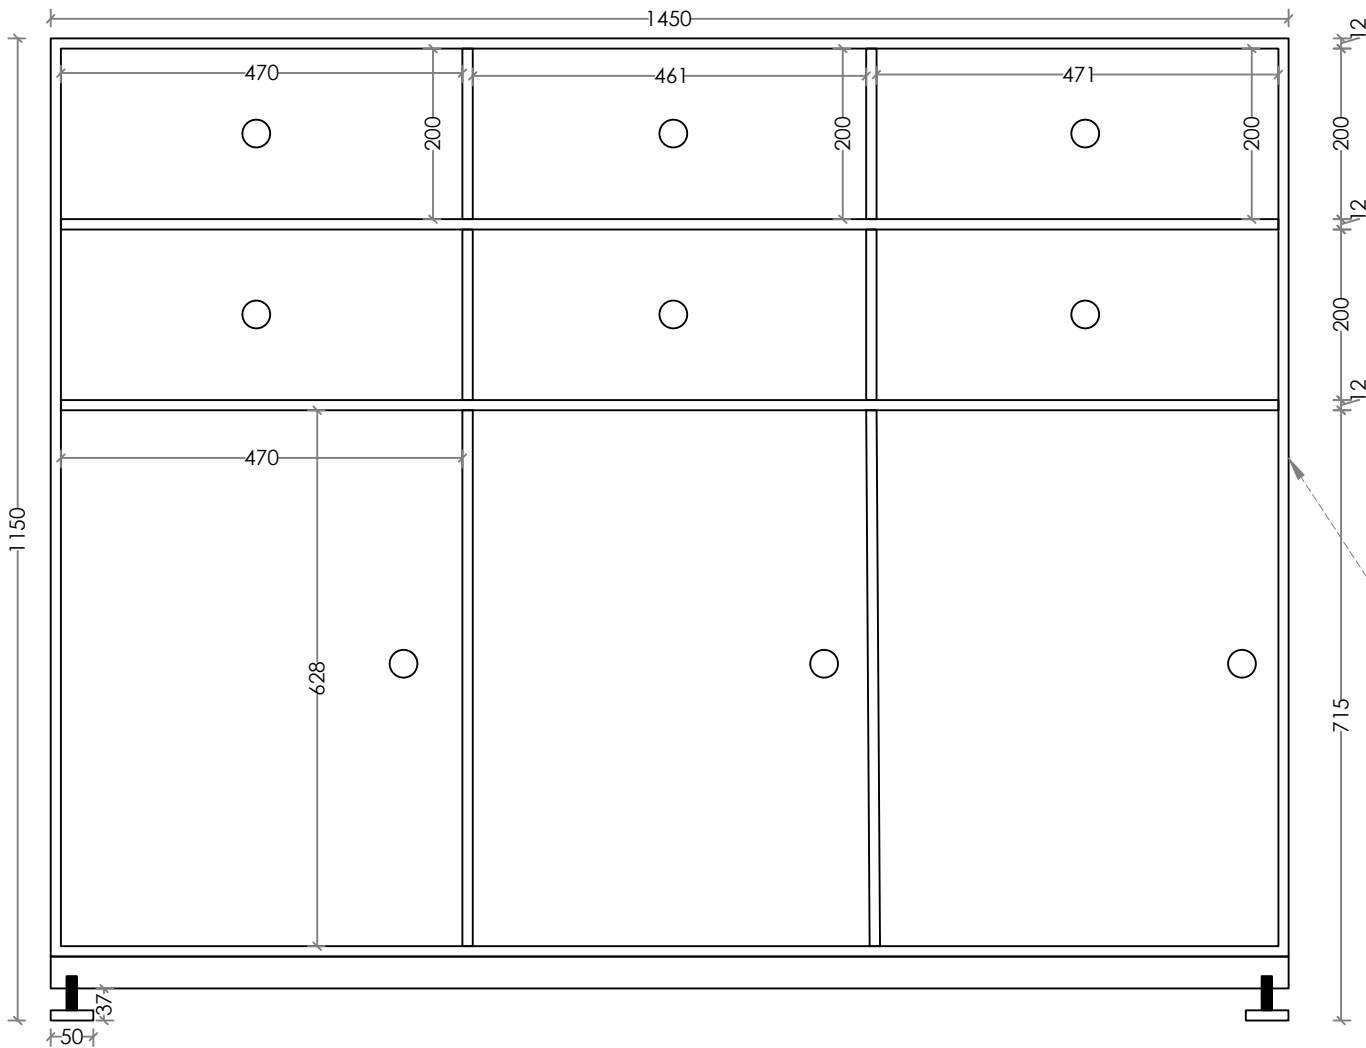


FRONT VEIW(A)

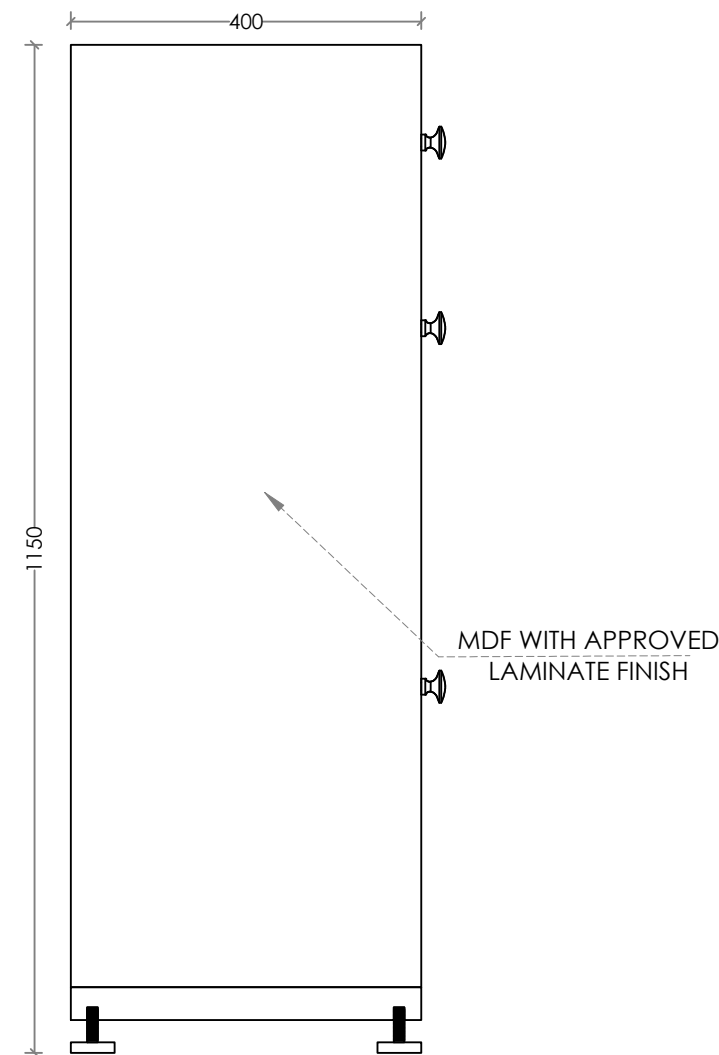

SIDE VEIW(B)

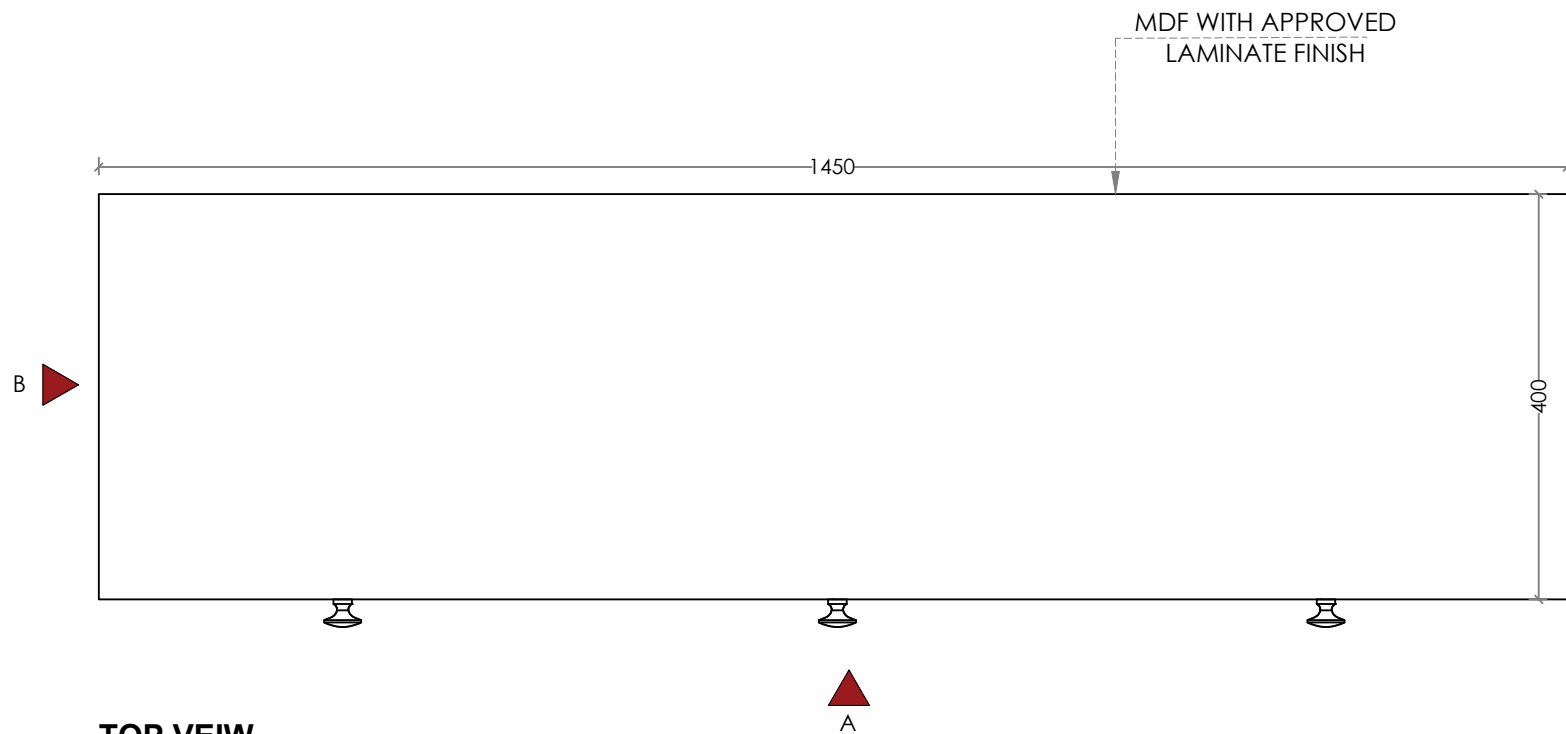

TOP VEIW

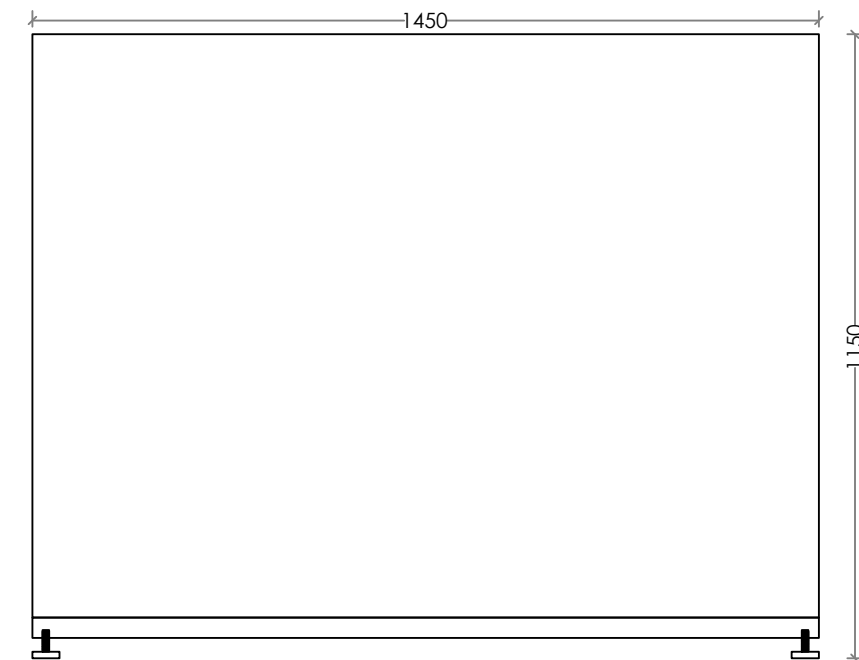

BACK VEIW



Sureena Chowdhri
-
Jaipur

Brand Info

Shop info


Market	INDIA
Province	RAJASTHAN
City	JAIPUR
City tier (tier 1/2/3)	TIER 1
Mall Name	HIGH STREET
New /Reno /Relo	NEW
FSS / SIS	FSS
Shop concept	SUREENA CHOWDHRI
Net size	957 SFT
Slab height	4395MM
B.O.B height	4267MM

Drawing info

Title	
Designed by	RISHAD
Checked by	SOUMYA
Date	CASH BACK DWG
Revision	R1
Dwg no.	

Notes:

Direction:

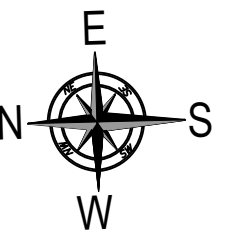



Sureena Chowdhri
-
Jaipur

Brand Info

Shop info


Market	INDIA
Province	RAJASTHAN
City	JAIPUR
City tier (tier 1/2/3)	TIER 1
Mall Name	HIGH STREET
New /Reno /Relo	NEW
FSS / SIS	FSS
Shop concept	SUREENA CHOWDHRI
Net size	957 SFT
Slab height	4395MM
B.O.B height	4267MM

Drawing info

Title	PODIUM DETAIL
Designed by	RISHAD
Checked by	SOUMYA
Date	
Revision	R1
Dwg no.	

Notes:

Direction:

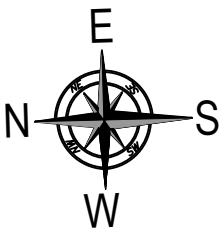

PODIUM TOP SURFACE TO BE DIP BY 10MM TO
ACCOMODATE MOSAIC TILES, SO FINISHED TILE SURFACE
AND PERIPHERAL VENEER SURFACE TO BE SAME LVL.


TOP SURFACE
FINISHED IN MOSAIC FLOORING (TO BE
SPECIFICALLY DESIGNED IN A PATTERN BY ARTIST)

FACIA FINISHED IN
VENEER

Beading finished
in veneer



cove lighting

1 SECTION S1
Scale: NTS

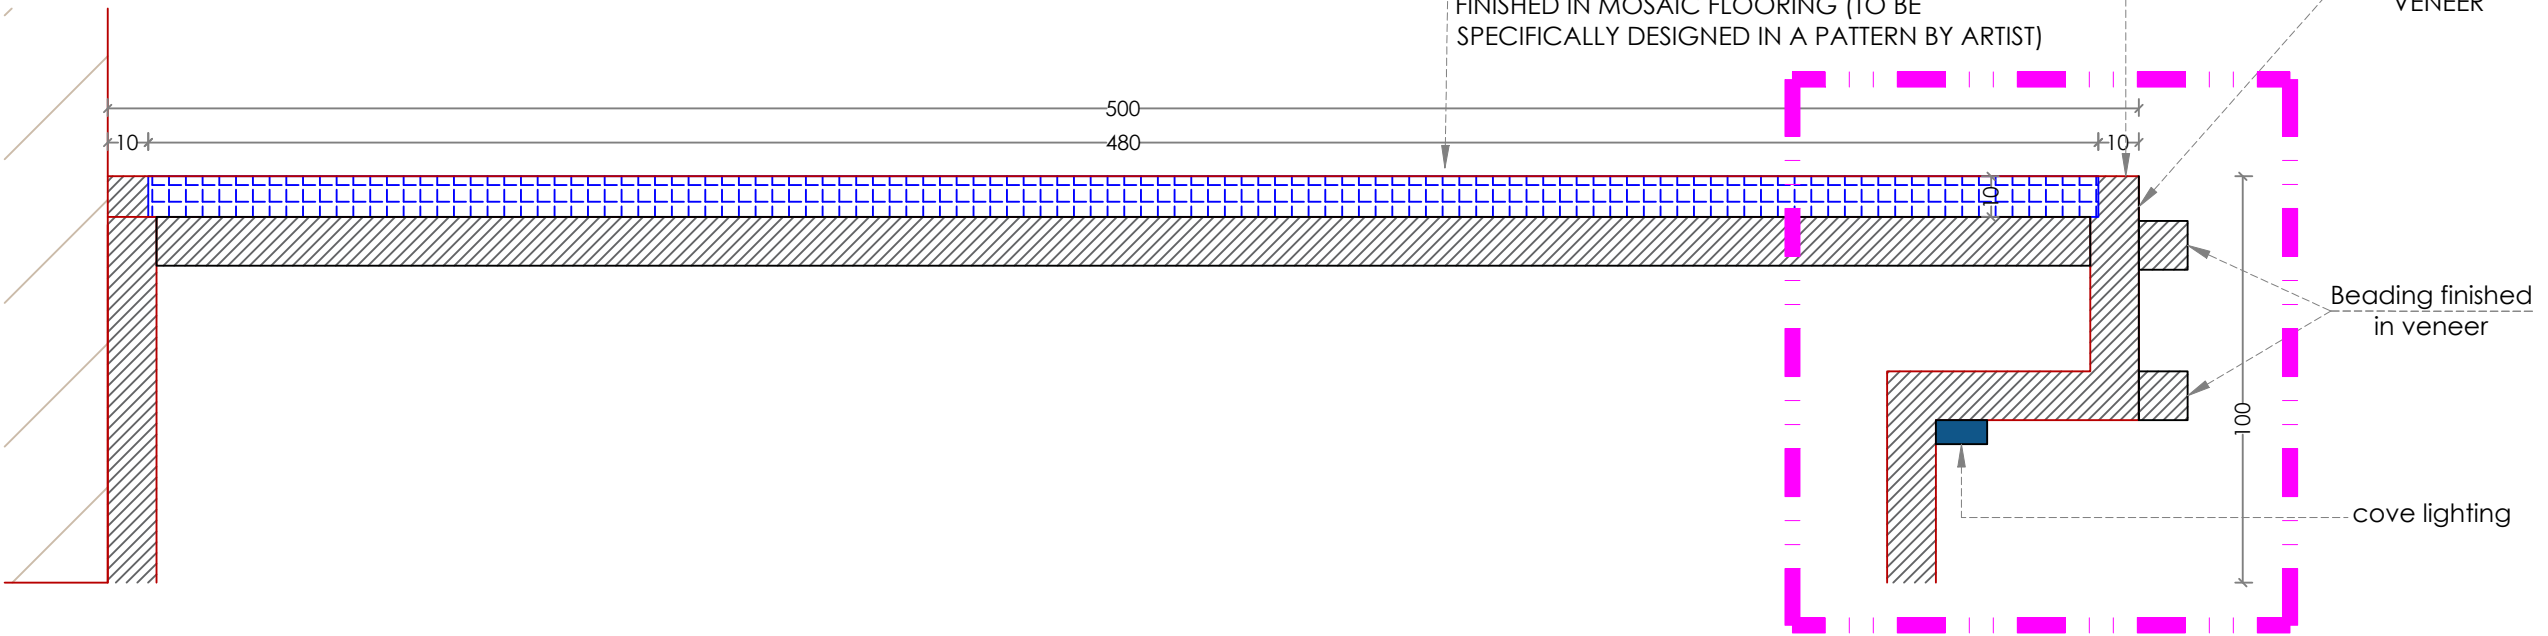

DETAIL
S1

mosaic tile
same level
veneer finish

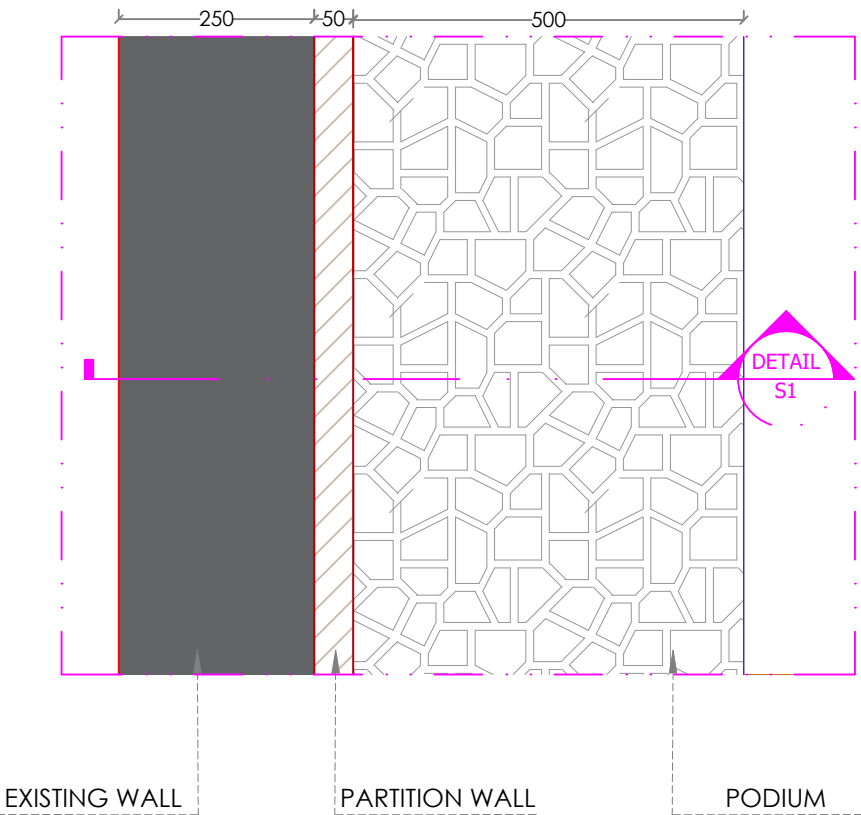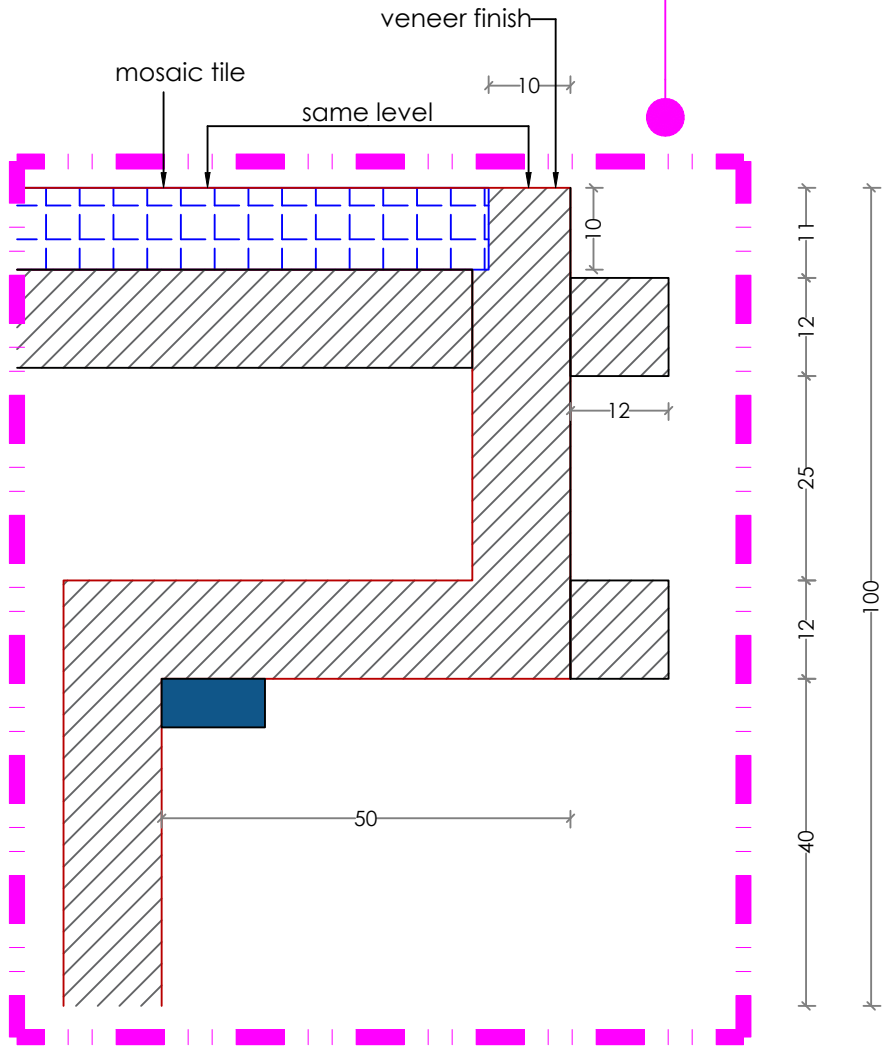

1 KEY PLAN
Scale: NTS

EXISTING WALL
PARTITION WALL
PODIUM