



THE BEAR HOUSE

**M3M PARAGON 57
GURUGRAM, HARYANA**

CARPET AREA :

1778 SFT

TITLE

GFC DRAWINGS - R1

DATE: 17-09-2026



DOMORE DESIGN PVT. LTD.
NO.681, SUKHADA, 2ND FLOOR, 2ND PHASE, 2ND BLOCK,
RAILWAY PARALLEL ROAD,
NEAR MALL OF ASIA, BANGALORE, KARNATAKA, 560097
domoredesign.co.in

PROJECT DRAWING LIST				
PROJECT NAME			THE BEAR HOUSE	
LOCATION			GURUGRAM	
CARPET AREA (in SFT)			1778	
Sl. No.	Drawing List	WG.N	STATUS	REMARKS
A	ARCHITECTURAL DRAWINGS(1st SET)			
1	AREA STATEMENT	1	Attached	
2	FIXTURE LAYOUT	2	Attached	
3	POWER POINT LAYOUT	3	Attached	
4	FLOORING	4	Attached	
5	FLOOR POWER POINT LAYOUT	5	Attached	
6	SKIRTING	6	Attached	
7	PARTITION	7	Attached	
8	FC W FURNITURE	8	Attached	
9	FC W/O FURNITURE	9	Attached	
10	FC SECTION	10	Attached	
11	LIGHTING W FURNITURE	12	Attached	
12	LIGHTING W/O FURNITURE	13	Attached	
13	HVAC	14	Attached	
14	HVAC DETAIL	15	Attached	
15	CCTV	16	Attached	
16	CCTV W/O FURNITURE	17	Attached	
17	AUDIO	18	Attached	
18	FAS	19	Attached	
19	RCP W FURNITURE	20	Attached	
20	RC W/O FURNITURE	21	Attached	
C	ARCHITECTURAL DRAWINGS(2nd SET)			
17	ELEVATION 1	23	Attached	
18	ELEVATION 2	24	Attached	
19	ELEVATION 3	25	Attached	
20	ELEVATION 4	26	Attached	
21	TRAIL ROOM DETAIL GF	27	Attached	
22	TRAIL ROOM DETAIL MEZ	28	Attached	
23	CASHBACK DETAIL	29	Attached	
24	FAÇADE	30	Attached	

LEGEND :

KEY PLAN :



NO.681, SUKHADA, 2ND FLOOR, 2ND PHASE,
2ND BLOCK, RAILWAY PARALLEL ROAD,
NEAR MALL OF ASIA, BANGALORE,
KARNATAKA, 560097

domoredesign.co.in

GENERAL NOTES:


- THIS DRAWING IS COPYRIGHT & PROPERTY OF DOMORE DESIGN PVT.LTD. AND IS NOT TO BE REPRODUCED, COPIED OR USED FOR ANY OTHER PURPOSE.
- WRITTEN DIMENSIONS TO BE FOLLOWED.
- DIMENSIONS TO BE CHECKED PRIOR TO THE COMMENCEMENT OF WORK.
- ALL DRAWINGS TO BE READ IN CONJUNCTION TO THE CONSULTANTS AND VENDORS DRAWINGS/DETAILS.
- FOR ALL LEGENDS, SYMBOLS, ABBREVIATIONS AND ANNOTATIONS RELATED QUERIES, REFER TO REFERENCE SHEET.
- ANY DISCREPANCY OR DOUBT IN DRAWING TO BE BROUGHT TO THE NOTICE OF DOMORE DESIGN PVT.LTD.

SCALE : AS MENTIONED

PROJECT NAME :

THE BEAR HOUSE
M3M PARAGON 57 -
GURUGRAM

COMPASS

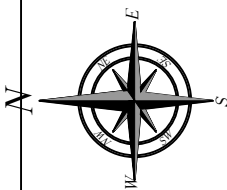



STORE INFO:

STATE	HARAYANA
CITY	GURUGRAM
HIGHSTREET/MALL	M3M PARAGON 57 MALL
AREA	1178 SFT
SLAB BOTTOM:	6809 MM
BEAM BOTTOM:	6329 MM

DRAWING NAME:


DRAWING LIST

DESIGNED BY:	CHECKED BY:	
RISHAD	-	
DATE:	REVISION NO:	DWG NO:
24/7/26	00	00

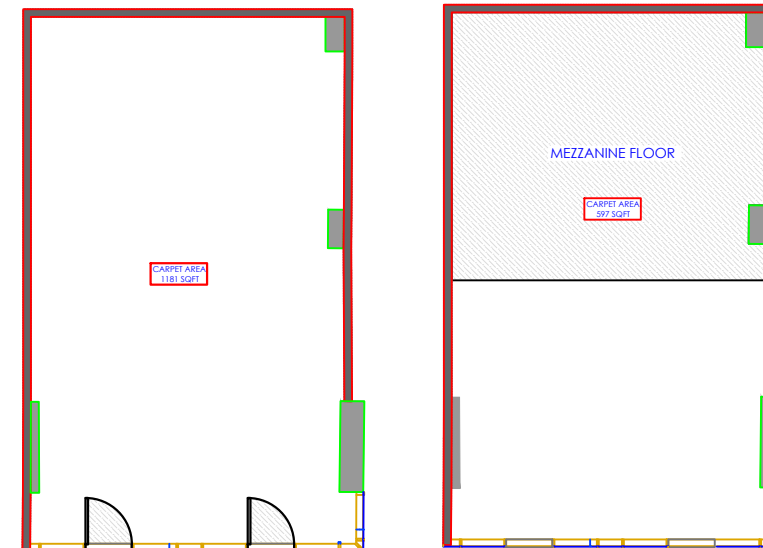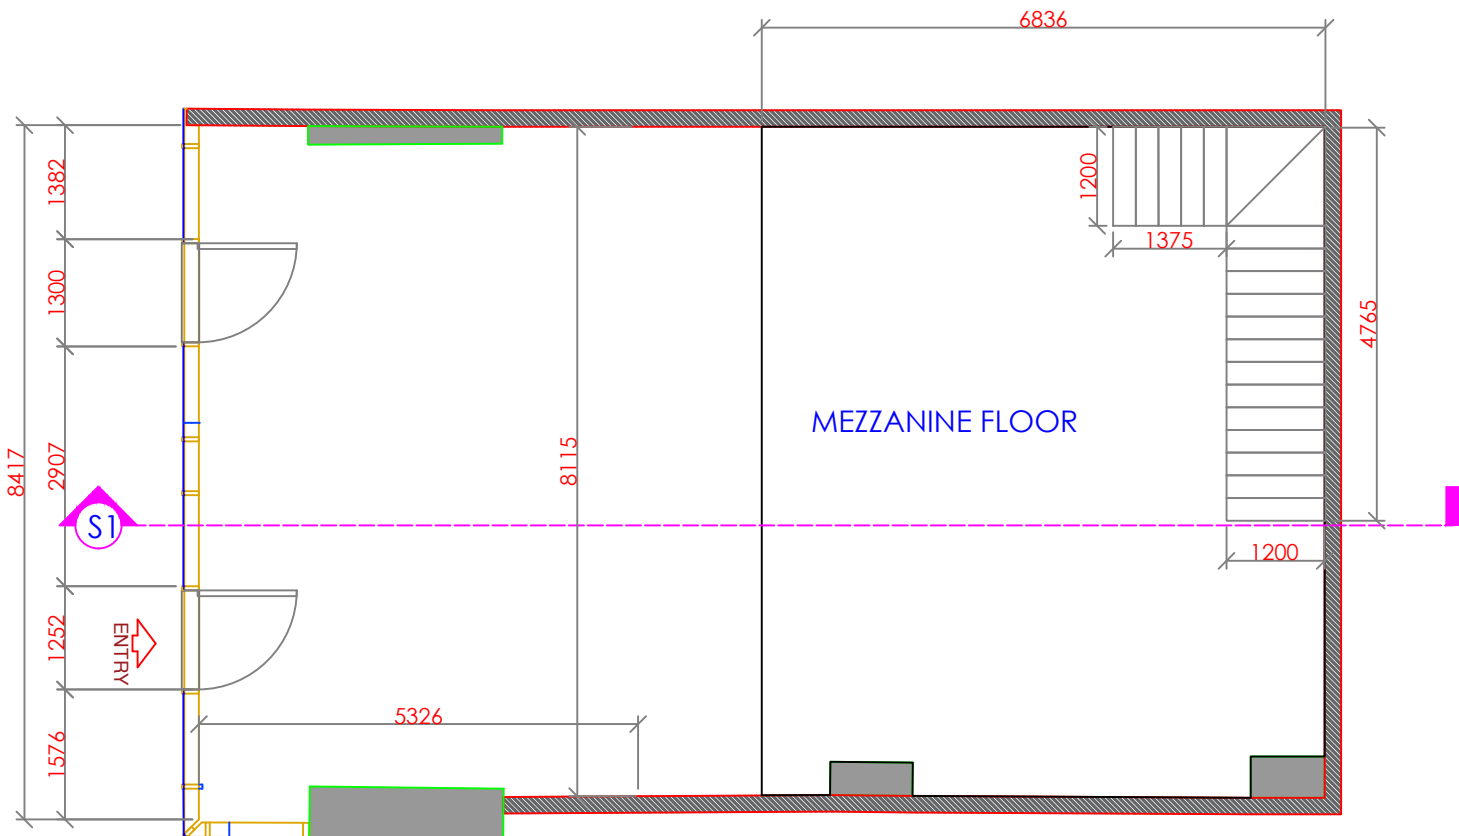

LEGEND :

KEY PLAN :

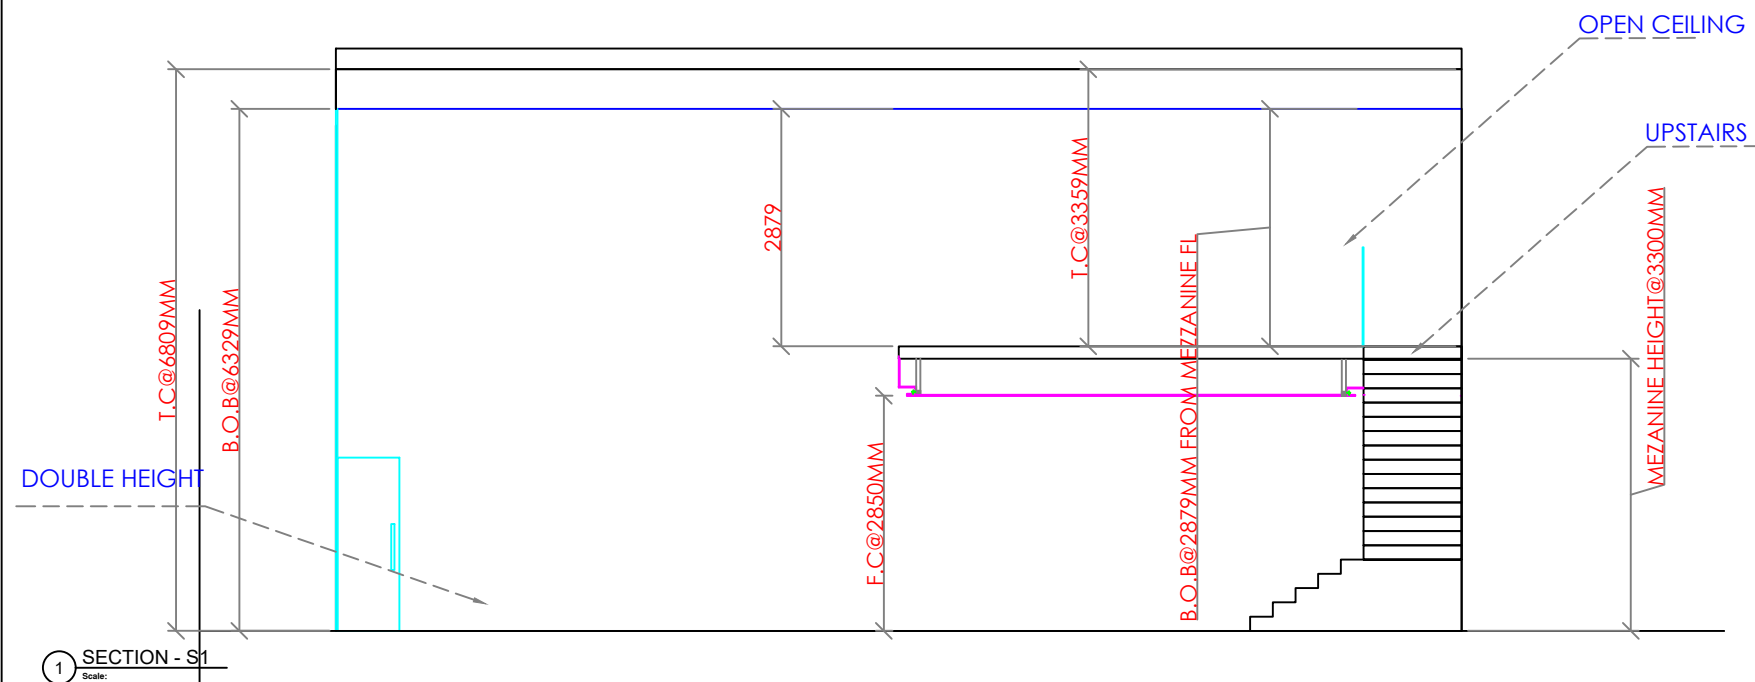

1 SECTION - S1
Scale



DOMORE DESIGN PVT. LTD.
NO.681, SUKHADA, 2ND FLOOR, 2ND PHASE, 2ND BLOCK,
RAILWAY PARALLEL ROAD,
NEAR MALL OF ASIA, BANGALORE, KARNATAKA, 560097
domoredesign.co.in

GENERAL NOTES

- THIS DRAWING IS COPYRIGHT & PROPERTY OF DOMORE DESIGN PVT.LTD, AND IS NOT TO BE REPRODUCED, COPIED OR USED FOR ANY OTHER PURPOSE.
- WRITTEN DIMENSIONS TO BE FOLLOWED.
- DIMENSIONS TO BE CROSS CHECKED PRIOR TO THE COMMENCEMENT OF WORK.
- ALL DRAWINGS TO BE READ IN CONJUNCTION TO THE CONSULTANTS AND VENDORS DRAWINGS/DETAILS.
- FOR ALL LEGENDS, SYMBOLS, ABBREVIATIONS AND ANNOTATIONS RELATED QUERIES, REFER TO REFERENCE SHEET.
- ANY DISCREPANCY OR DOUBT IN DRAWING TO BE BROUGHT TO THE NOTICE OF DOMORE DESIGN PVT.LTD

SCALE : AS MENTIONED


REVISIONS

R01
R02
R03

PROJECT NAME :

M3M PARAGON 57
GURGOAN

COMPASS:

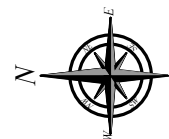

STORE INFO:

STATE	XXX
CITY	GURUGRAM
HIGHSTREET/MALL	M3M PARAGON 57
AREA	1900
SLAB BOTTOM: 6809MM	BEAM BOTTOM: 6329 MM

DRAWING NAME:

AREA STATEMENT


DESIGNED BY:	CHECKED BY:	
RISHAD	AAA	
DATE:	REVISION NO:	DWG NO:
17-09-2026	R0	00

CARPET AREA - 1778 SFT
RETAIL AREA - 1575SFT
STOCK ROOM -93 SFT
TRIAL ROOM &
PASSAGE AREA -110 SFT
CASH AREA - 35SFT
STORE EFFICEINY - 88.5%


FLOOR HEIGHT - 3450MM
RISER - 173 MM
TREAD - 275MM

LEGEND :

KEY PLAN :

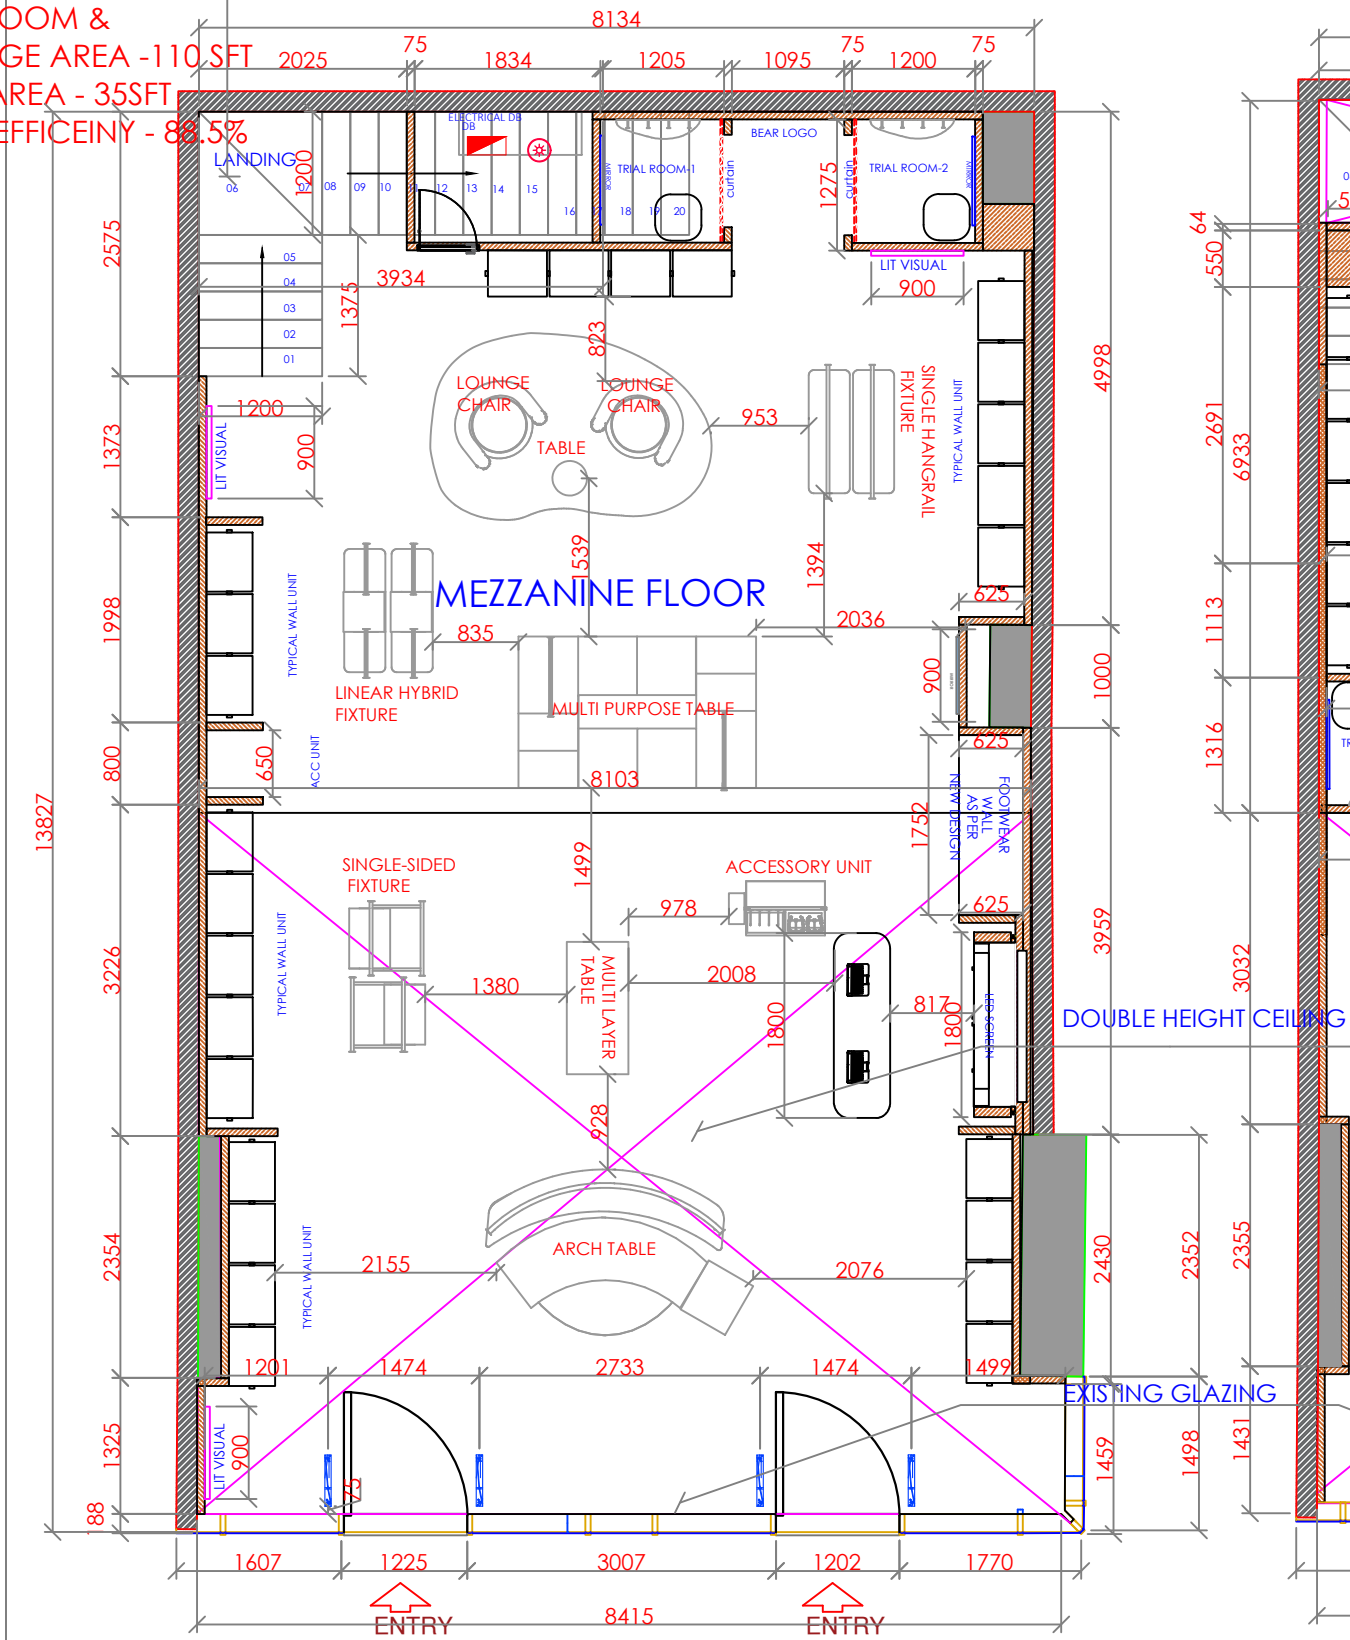

GROUND FLOOR

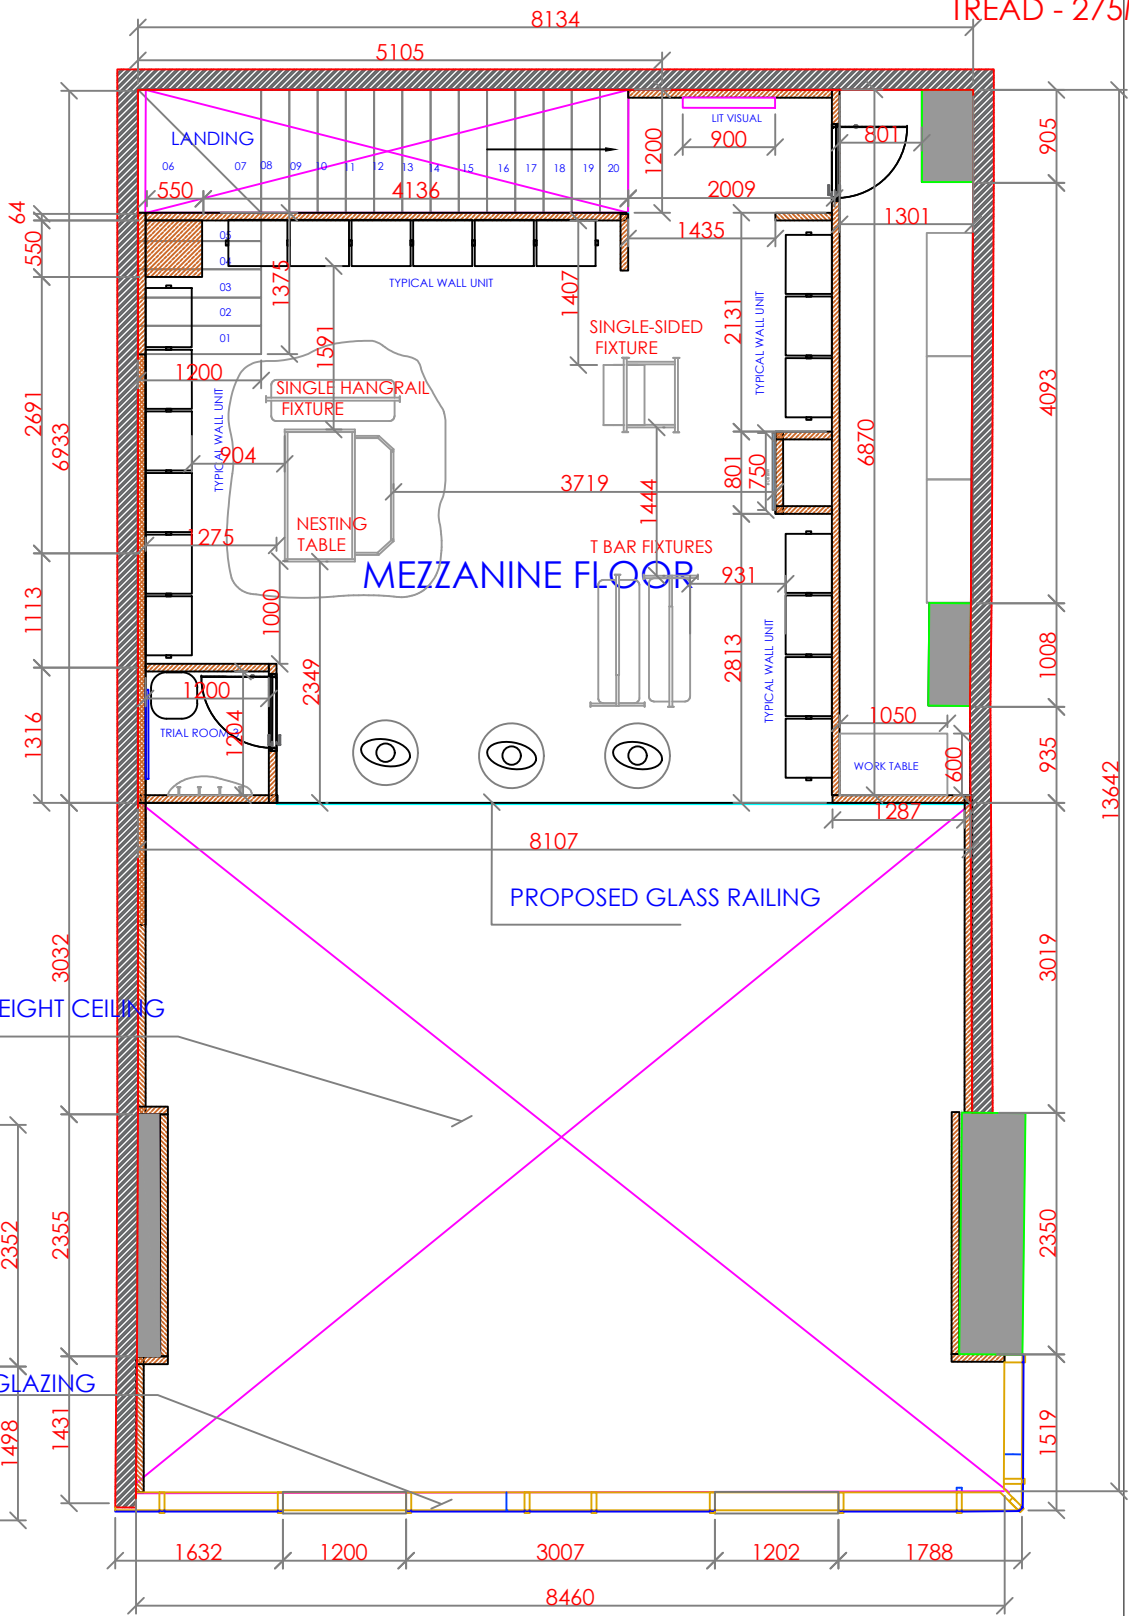

FIRST FLOOR



DOMORE DESIGN PVT. LTD.
NO.681, SUKHADA, 2ND FLOOR, 2ND PHASE, 2ND BLOCK,
RAILWAY PARALLEL ROAD,
NEAR MALL OF ASIA, BANGALORE, KARNATAKA, 560097
domoredesign.co.in

GENERAL NOTES

- THIS DRAWING IS COPYRIGHT & PROPERTY OF DOMORE DESIGN PVT.LTD. AND IS NOT TO BE REPRODUCED, COPIED OR USED FOR ANY OTHER PURPOSE.
- WRITTEN DIMENSIONS TO BE FOLLOWED.
- DIMENSIONS TO BE CROSS CHECKED PRIOR TO THE COMMENCEMENT OF WORK.
- ALL DRAWINGS TO BE READ IN CONJUNCTION TO THE CONSULTANTS AND VENDORS DRAWINGS/DETAILS.
- FOR ALL LEGENDS, SYMBOLS, ABBREVIATIONS AND ANNOTATIONS RELATED QUERIES, REFER TO REFERENCE SHEET.
- ANY DISCREPANCY OR DOUBT IN DRAWING TO BE BROUGHT TO THE NOTICE OF DOMORE DESIGN PVT.LTD

SCALE : AS MENTIONED


REVISIONS

R01
R02
R03

PROJECT NAME :

M3M PARAGON 57
GURGOAN

COMPASS:

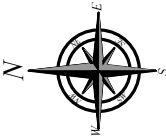





STORE INFO:

STATE	XXX
CITY	GURUGRAM
HIGHSTREET/MALL	M3M PARAGON 57
AREA	1769 SFT
SLAB BOTTOM: 6809MM	BEAM BOTTOM: 6329 MM

DRAWING NAME:



FIXTURE LAYOUT

DESIGNED BY:	CHECKED BY:	
RISHAD	AAA	
DATE:	REVISION NO:	DWG NO:
17-09-2026	R0	00

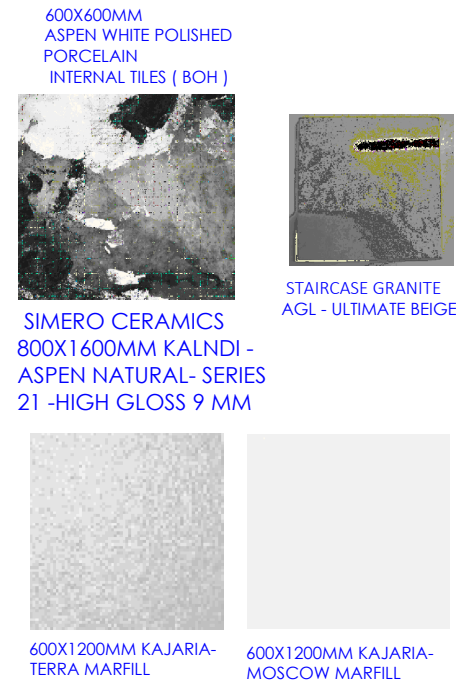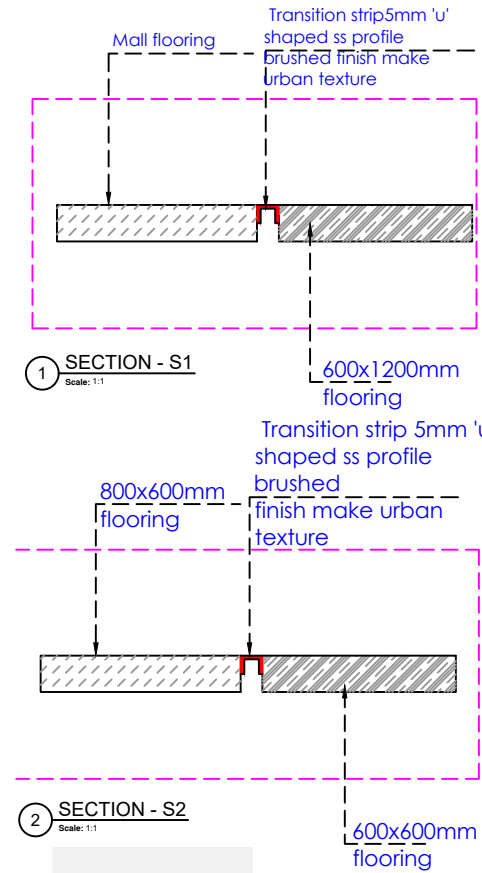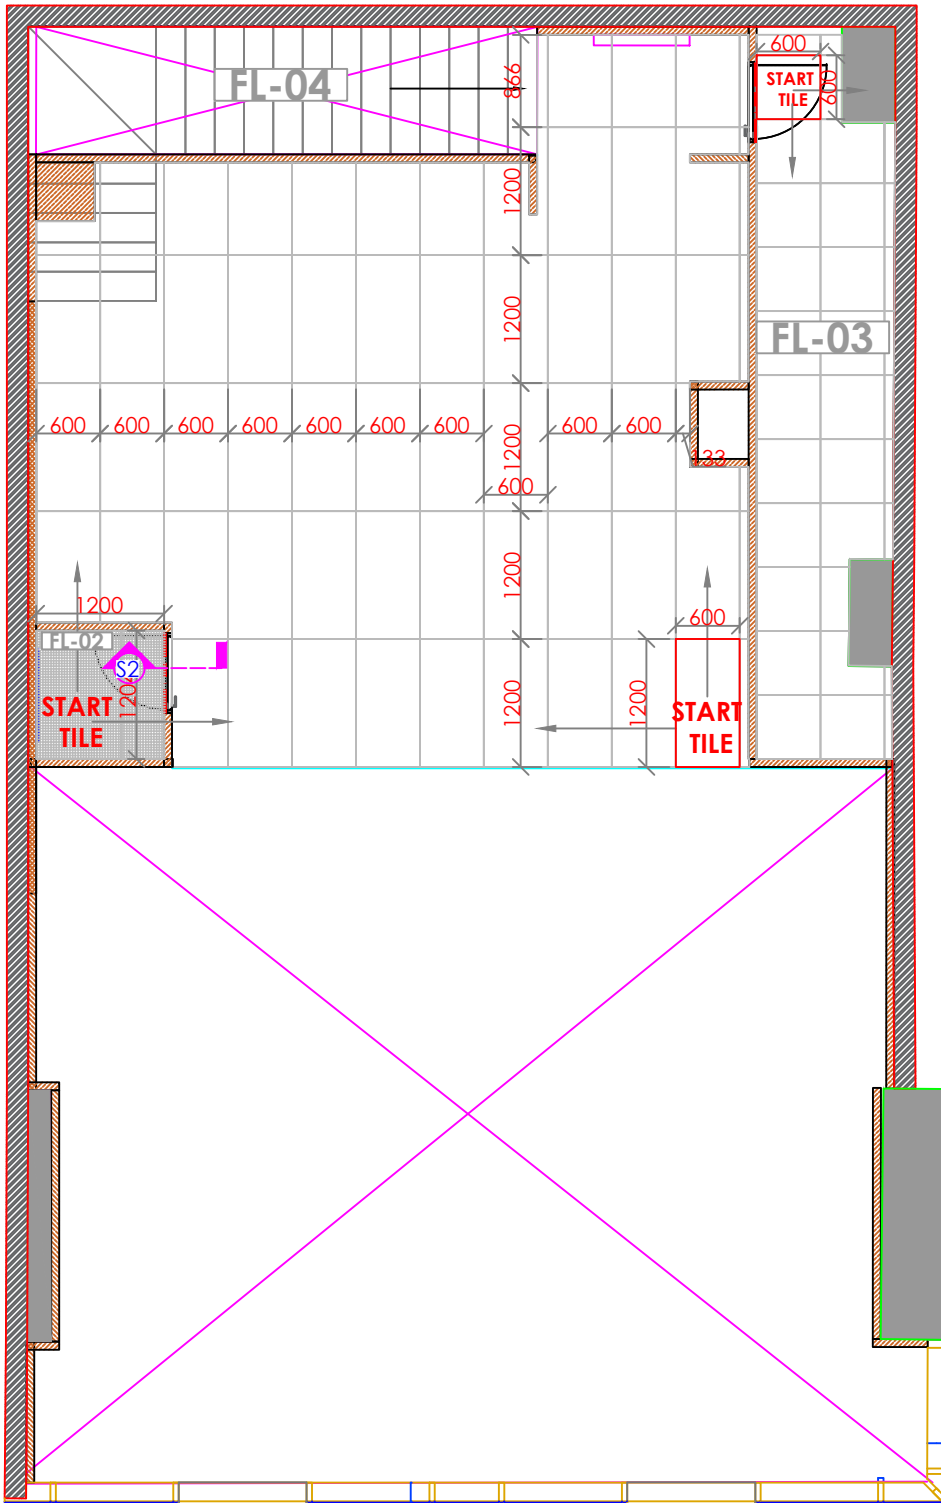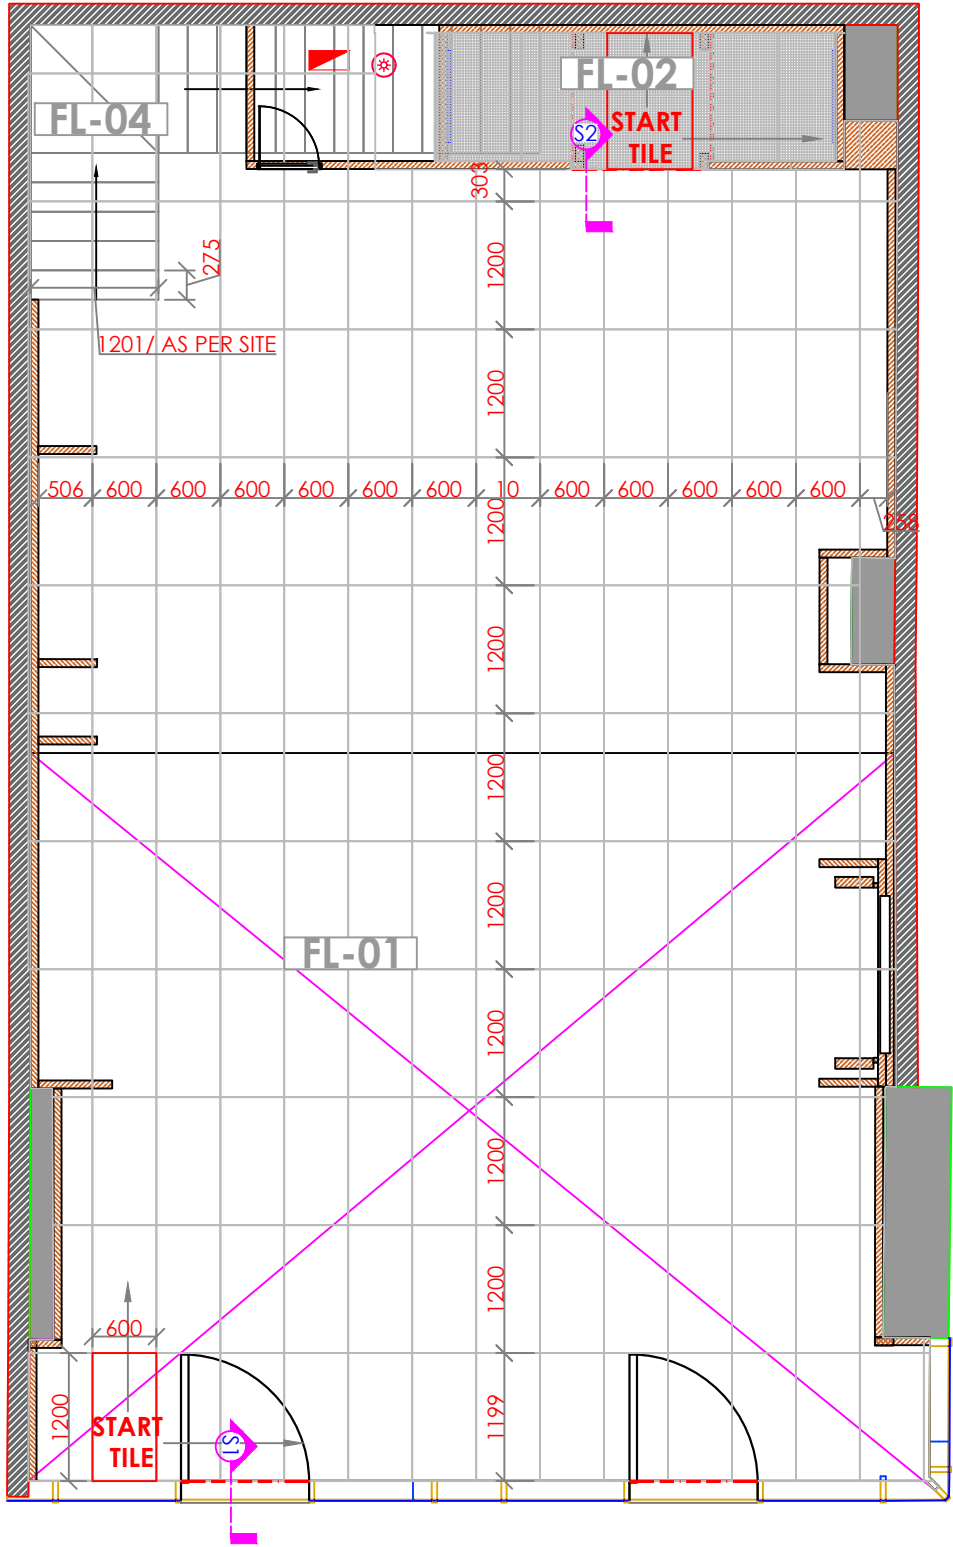

LEGEND :				
LEGEND : FLOORING				
SINO	SYMBOL	DESCRIPTION	SQ.FT + 10%	
FL-01		KAJARIA 600X1200MM TERRA MARFILL/ MOSCOW MARFILL	1770 SFT	
FL-02		800X1600MM KALNDI - ASPEN NATURAL- SERIES 21 -HIGH GLOSS 9 MM	100 SFT	
FL-03		600X600MM ASPEN WHITE POLISHED PORCELAIN INTERNAL TILES (BOH)	120 SFT	
FL-04		STAIRCASE GRANITE AGL ULTIMATE BEIGE	AS PER SITE	
FL-05		5MM THK. SS TRANSITION PROFILE.	20 RFT	

KEY PLAN :	

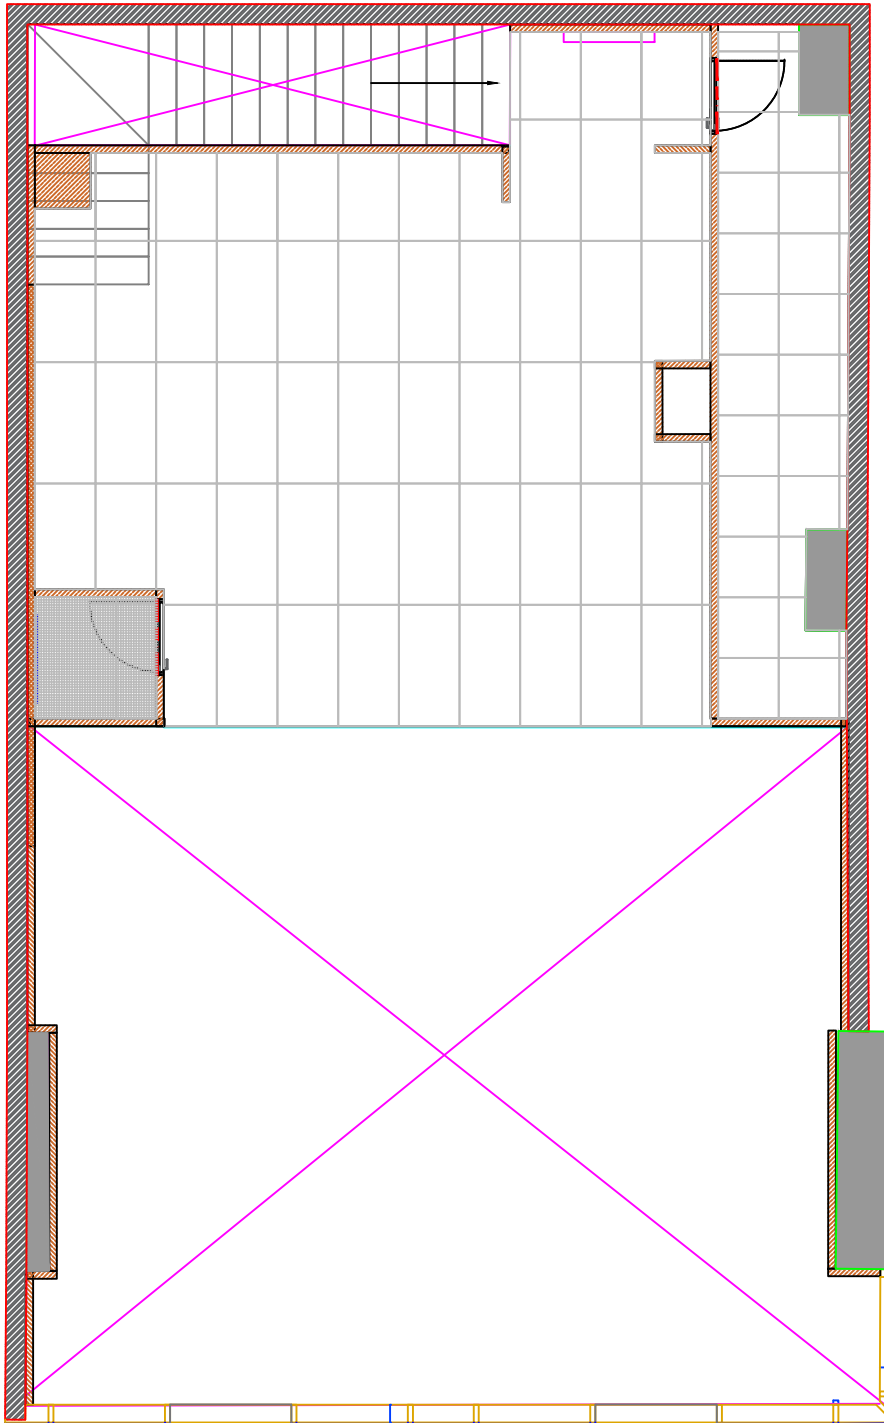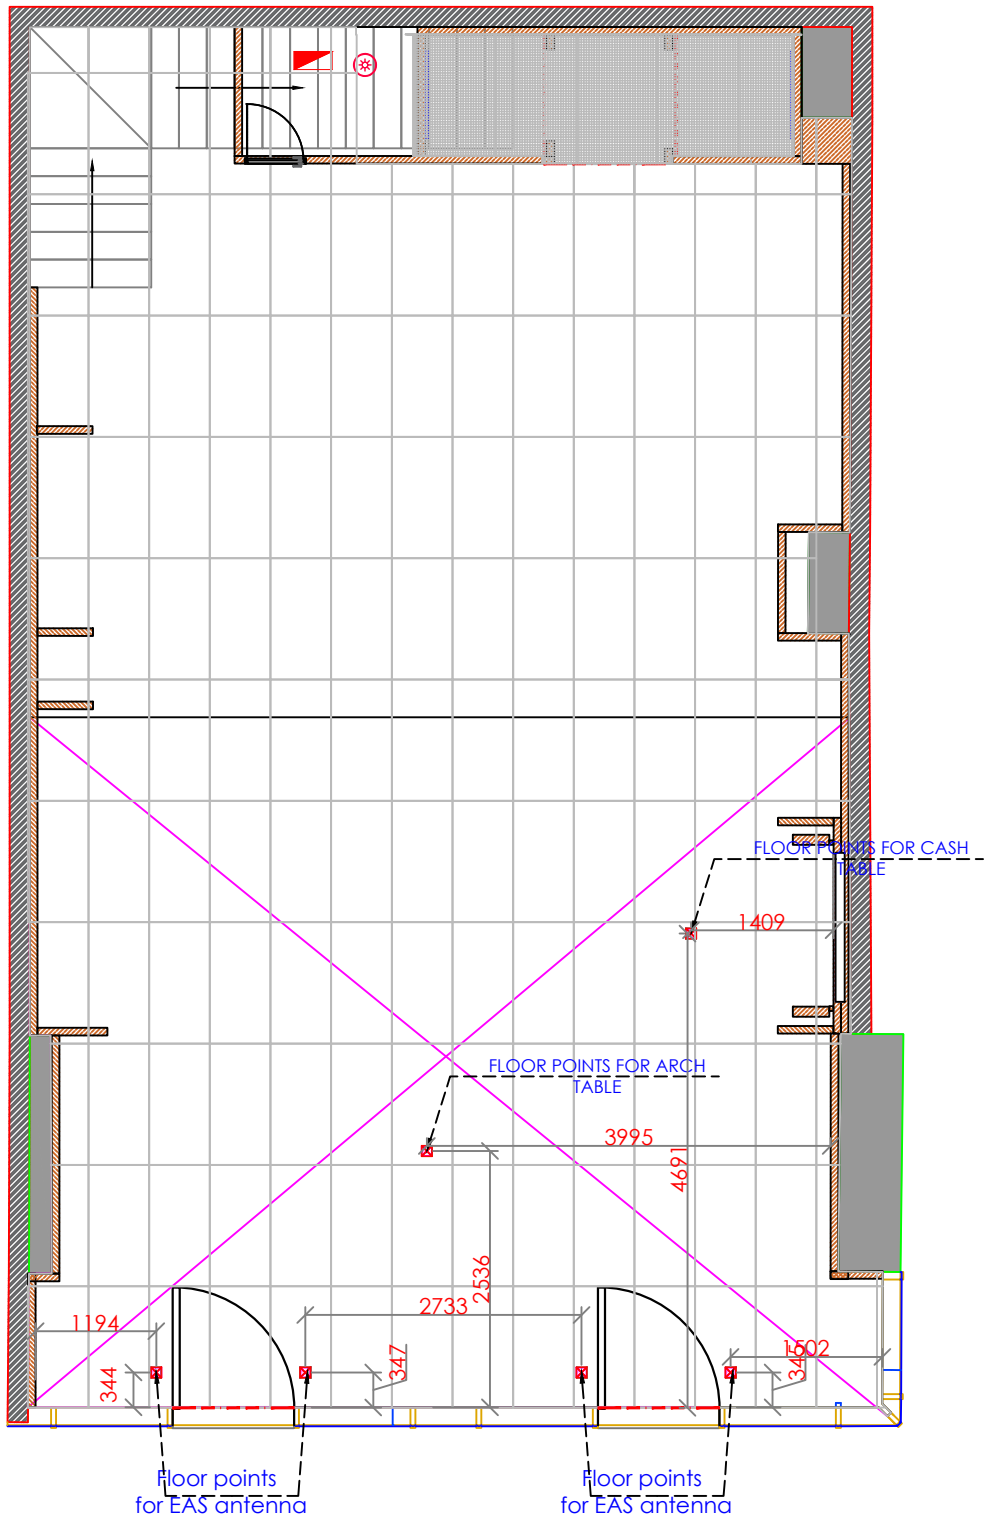

LEGEND :

KEY PLAN :



DOMORE DESIGN PVT. LTD.
NO.681, SUKHADA, 2ND FLOOR, 2ND PHASE, 2ND BLOCK,
RAILWAY PARALLEL ROAD,
NEAR MALL OF ASIA, BANGALORE, KARNATAKA, 560097
domoredesign.co.in

GENERAL NOTES


- THIS DRAWING IS COPYRIGHT & PROPERTY OF DOMORE DESIGN PVT.LTD. AND IS NOT TO BE REPRODUCED, COPIED OR USED FOR ANY OTHER PURPOSE.
- WRITTEN DIMENSIONS TO BE FOLLOWED.
- DIMENSIONS TO BE CROSS CHECKED PRIOR TO THE COMMENCEMENT OF WORK.
- ALL DRAWINGS TO BE READ IN CONJUNCTION TO THE CONSULTANTS AND VENDORS DRAWINGS/DETAILS.
- FOR ALL LEGENDS, SYMBOLS, ABBREVIATIONS AND ANNOTATIONS RELATED QUERIES, REFER TO REFERENCE SHEET.
- ANY DISCREPANCY OR DOUBT IN DRAWING TO BE BROUGHT TO THE NOTICE OF DOMORE DESIGN PVT.LTD

SCALE : AS MENTIONED

REVISIONS
R01
R02
R03




PROJECT NAME :

M3M PARAGON 57
GURGOAN

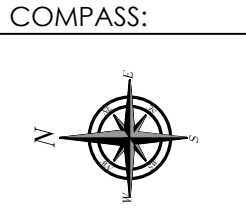

STORE INFO:	
STATE	XXX
CITY	GURUGRAM
HIGHSTREET/MALL	M3M PARAGON 57
AREA	1769 SFT
SLAB BOTTOM: 6809MM	BEAM BOTTOM: 6329 MM

DRAWING NAME:		
FLOOR CONDUIT LAYOUT		
DESIGNED BY:	CHECKED BY:	
RISHAD	AAA	
DATE:	REVISION NO:	DWG NO:
17-09-2026	R0	00

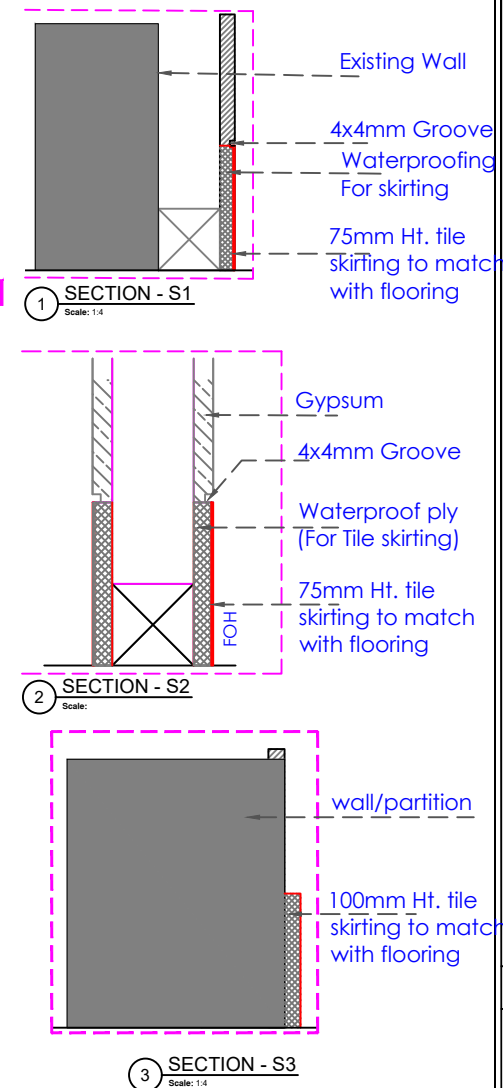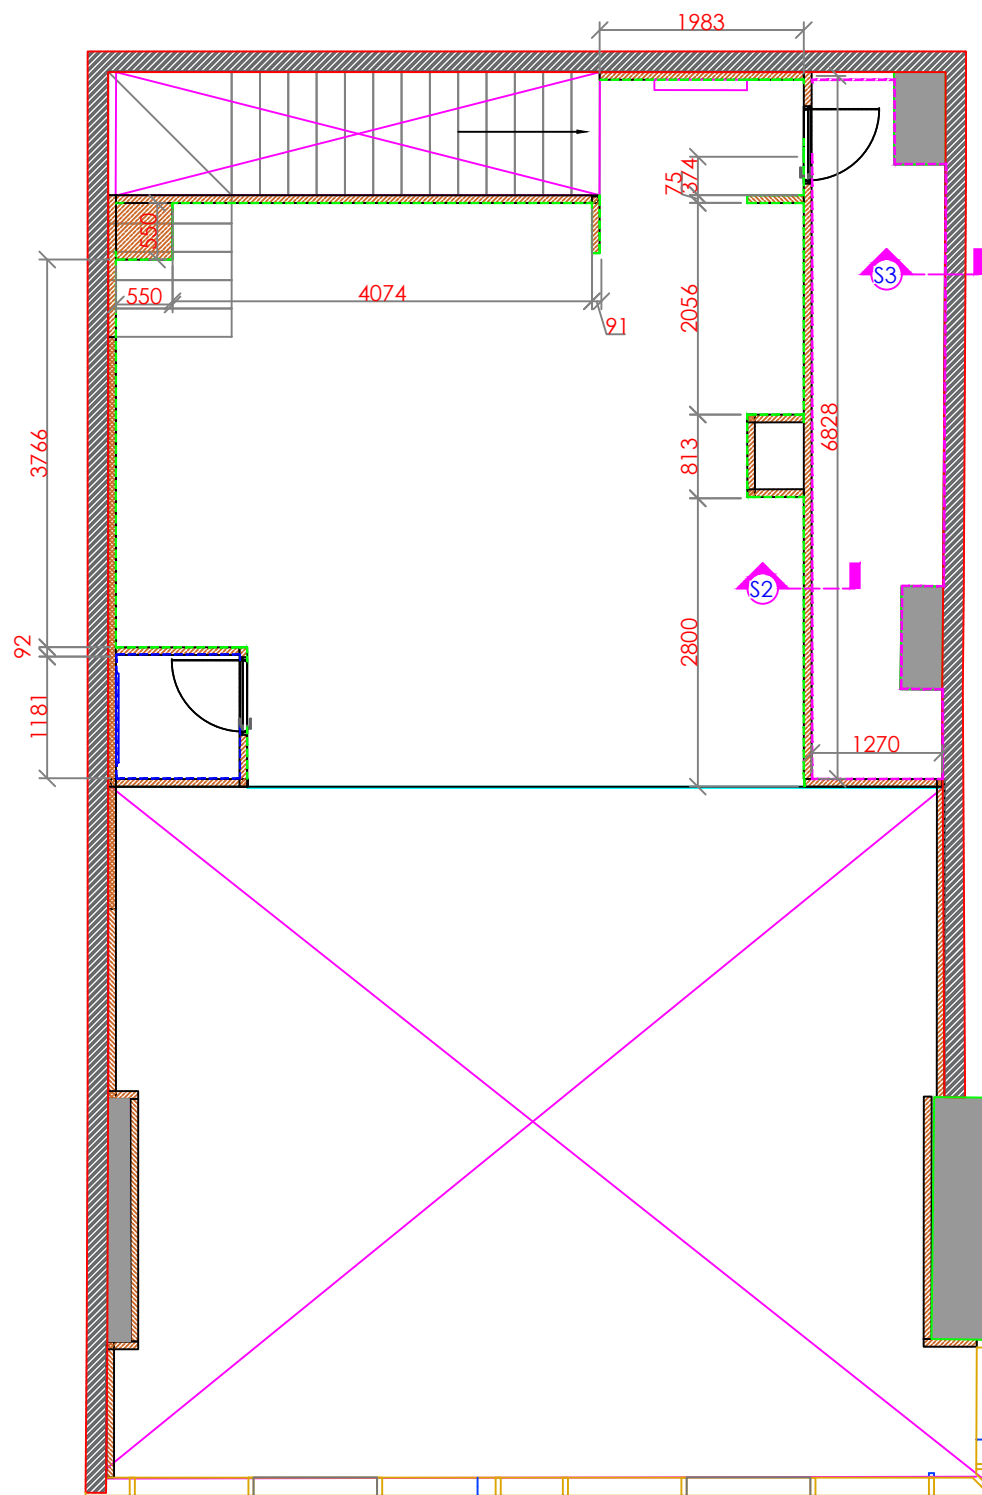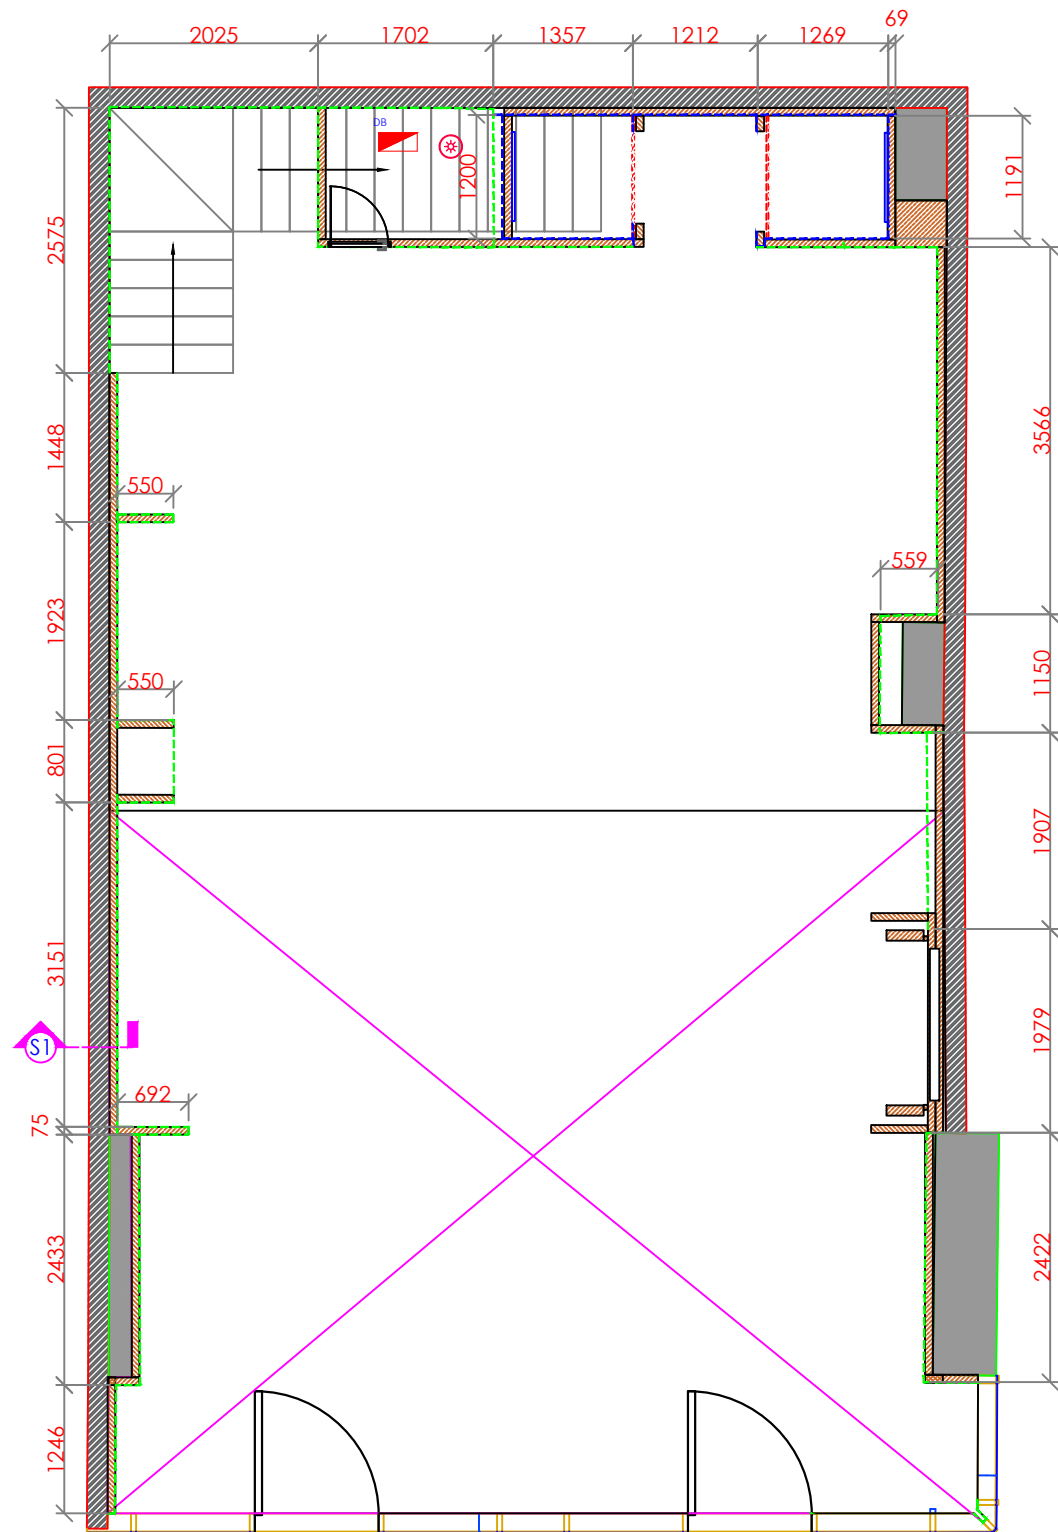

LEGEND : SKIRTING		
SINO	SYMBOL	DESCRIPTION
S1		75 MM HT SKIRTING TO MATCH WITH FL-01 600X1200MM KAJARIA-LUXOR BEIGE
S2		75 MM HT SKIRTING TO MATCH WITH FL-02- 800X1600MM KALNDI - ASPEN NATURAL - SERIES 21 -HIGH GLOSS 9 MM
S3		100MM HT. SKIRTING MATCHING TO FLOOR TILE

KEY PLAN :

DRAWING NAME:

SKIRTING LAYOUT		
DESIGNED BY:	CHECKED BY:	
RISHAD	AAA	
DATE:	REVISION NO:	DWG NO:
17-09-2026	R0	00

DOMORE DESIGN PVT. LTD.
NO.681, SUKHADA, 2ND FLOOR, 2ND PHASE, 2ND BLOCK,
RAILWAY PARALLEL ROAD,
NEAR MALL OF ASIA, BANGALORE, KARNATAKA, 560097
domoredesign.co.in

GENERAL NOTES

- THIS DRAWING IS COPYRIGHT & PROPERTY OF DOMORE DESIGN PVT.LTD. AND IS NOT TO BE REPRODUCED, COPIED OR USED FOR ANY OTHER PURPOSE.
- WRITTEN DIMENSIONS TO BE FOLLOWED.
- DIMENSIONS TO BE CROSS CHECKED PRIOR TO THE COMMENCEMENT OF WORK.
- ALL DRAWINGS TO BE READ IN CONJUNCTION TO THE CONSULTANTS AND VENDORS DRAWINGS/DETAILS.
- FOR ALL LEGENDS, SYMBOLS, ABBREVIATIONS AND ANNOTATIONS RELATED QUERIES, REFER TO REFERENCE SHEET.
- ANY DISCREPANCY OR DOUBT IN DRAWING TO BE BROUGHT TO THE NOTICE OF DOMORE DESIGN PVT.LTD

SCALE : AS MENTIONED

REVISIONS	
R01	
R02	
R03	


PROJECT NAME :

M3M PARAGON 57



GURGOAN

COMPASS:

STORE INFO:		
STATE	XXX	
CITY	GURUGRAM	
HIGHSTREET/MALL	M3M PARAGON 57	
AREA	1769 SFT	
SLAB BOTTOM: 6809MM	BEAM BOTTOM: 6329 MM	

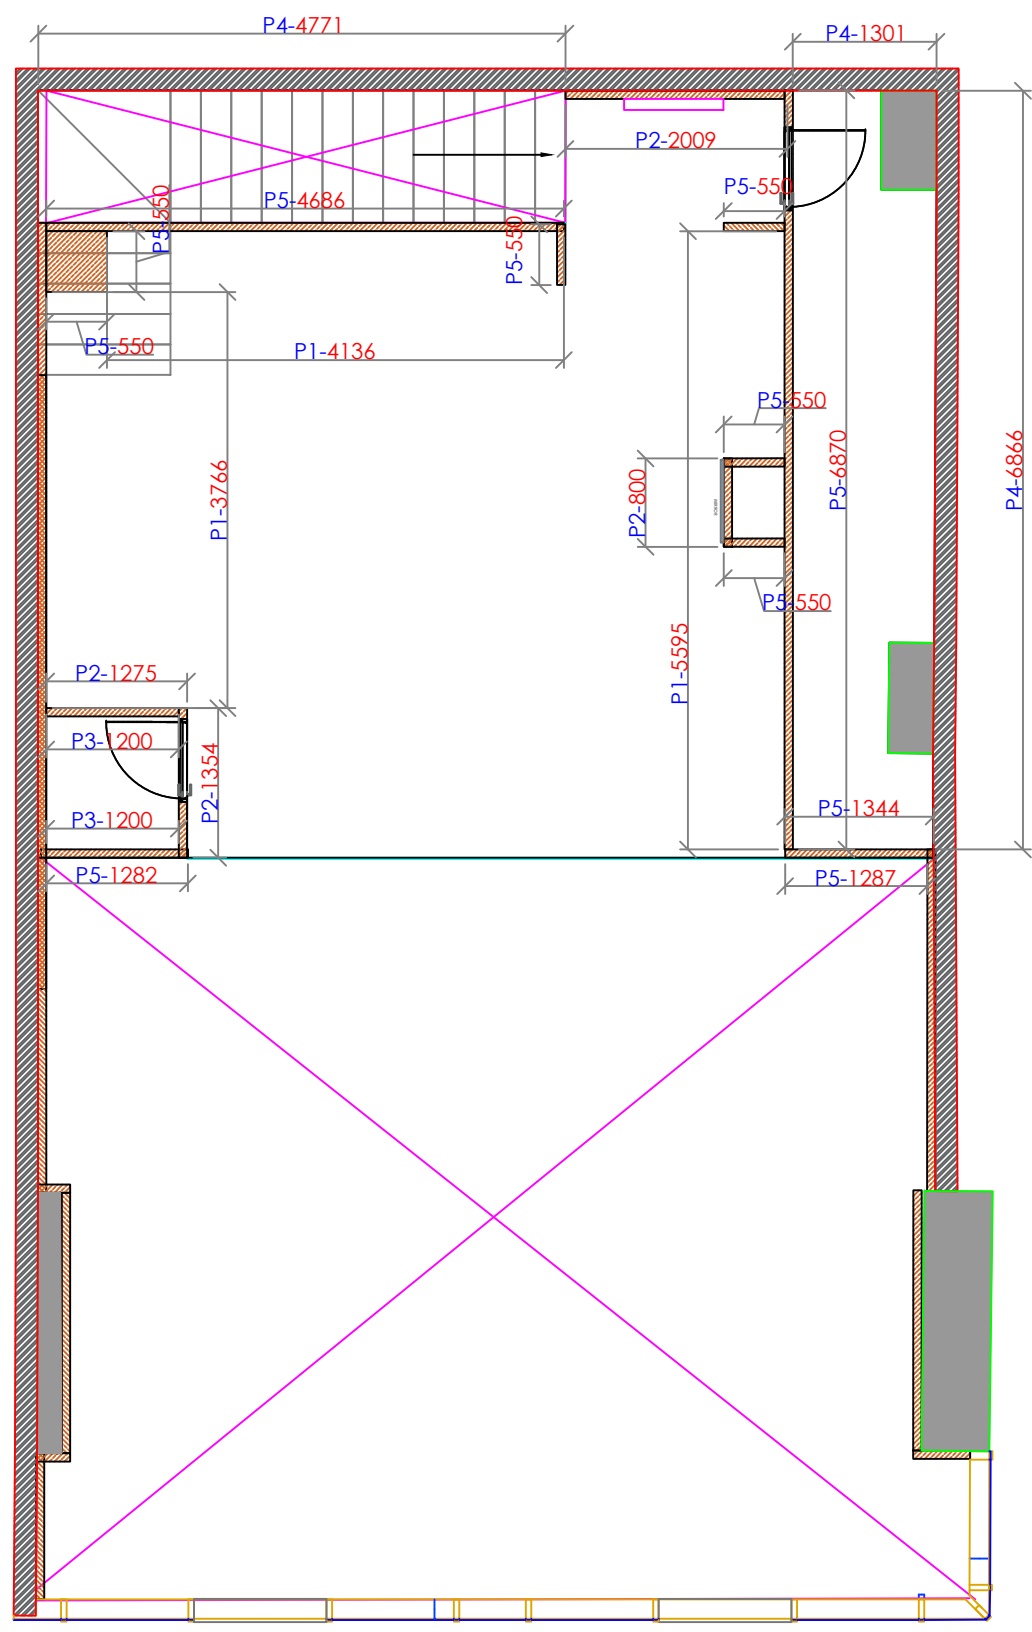

PARTITION LAYOUT		
DESIGNED BY:	CHECKED BY:	
RISHAD	AAA	
DATE:	REVISION NO:	DWG NO:
17-09-2026	R0	00

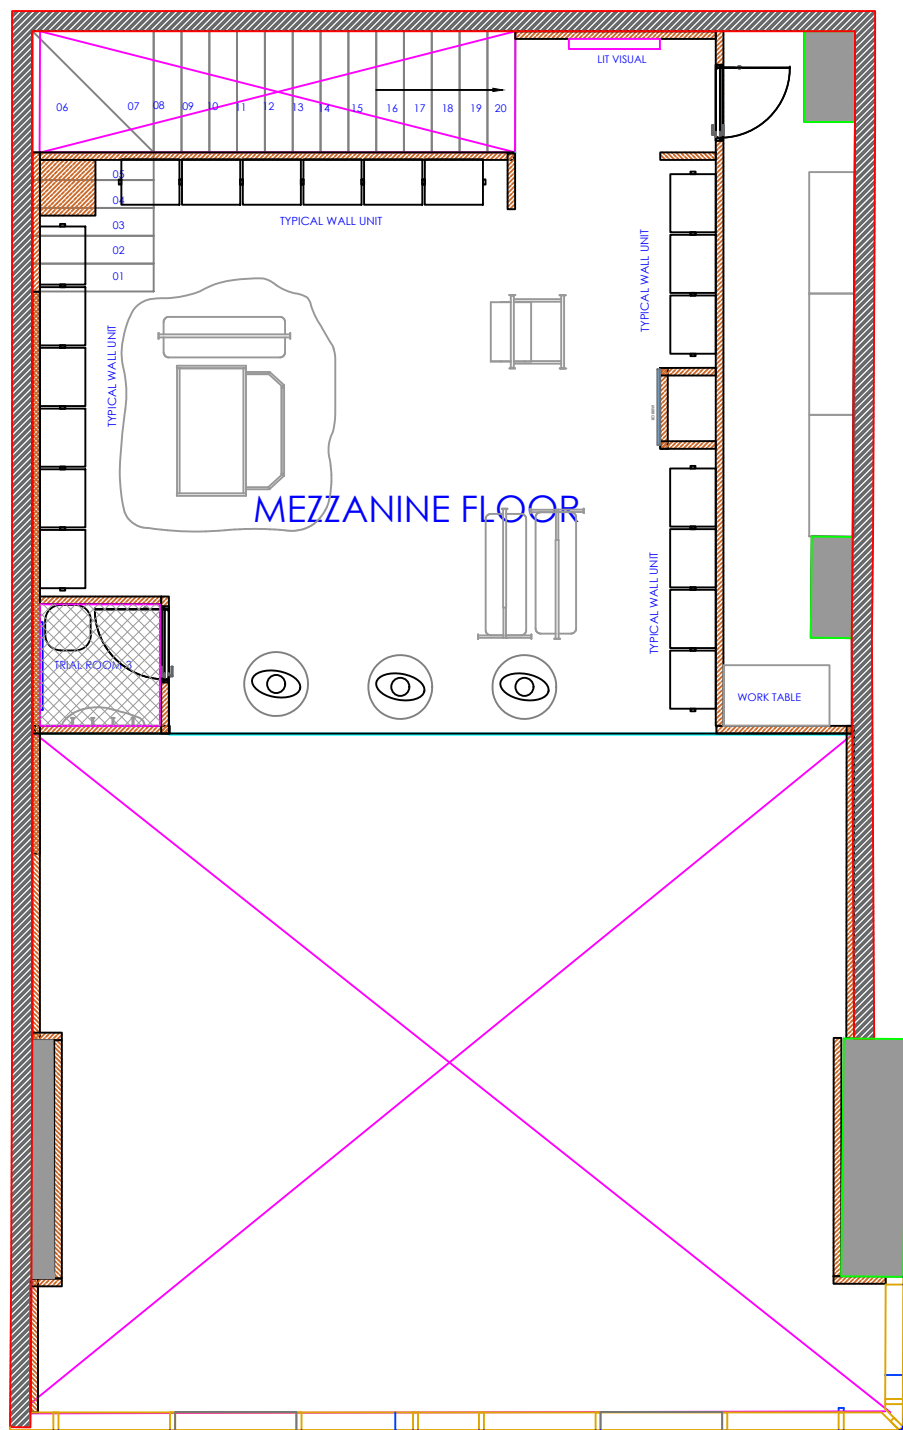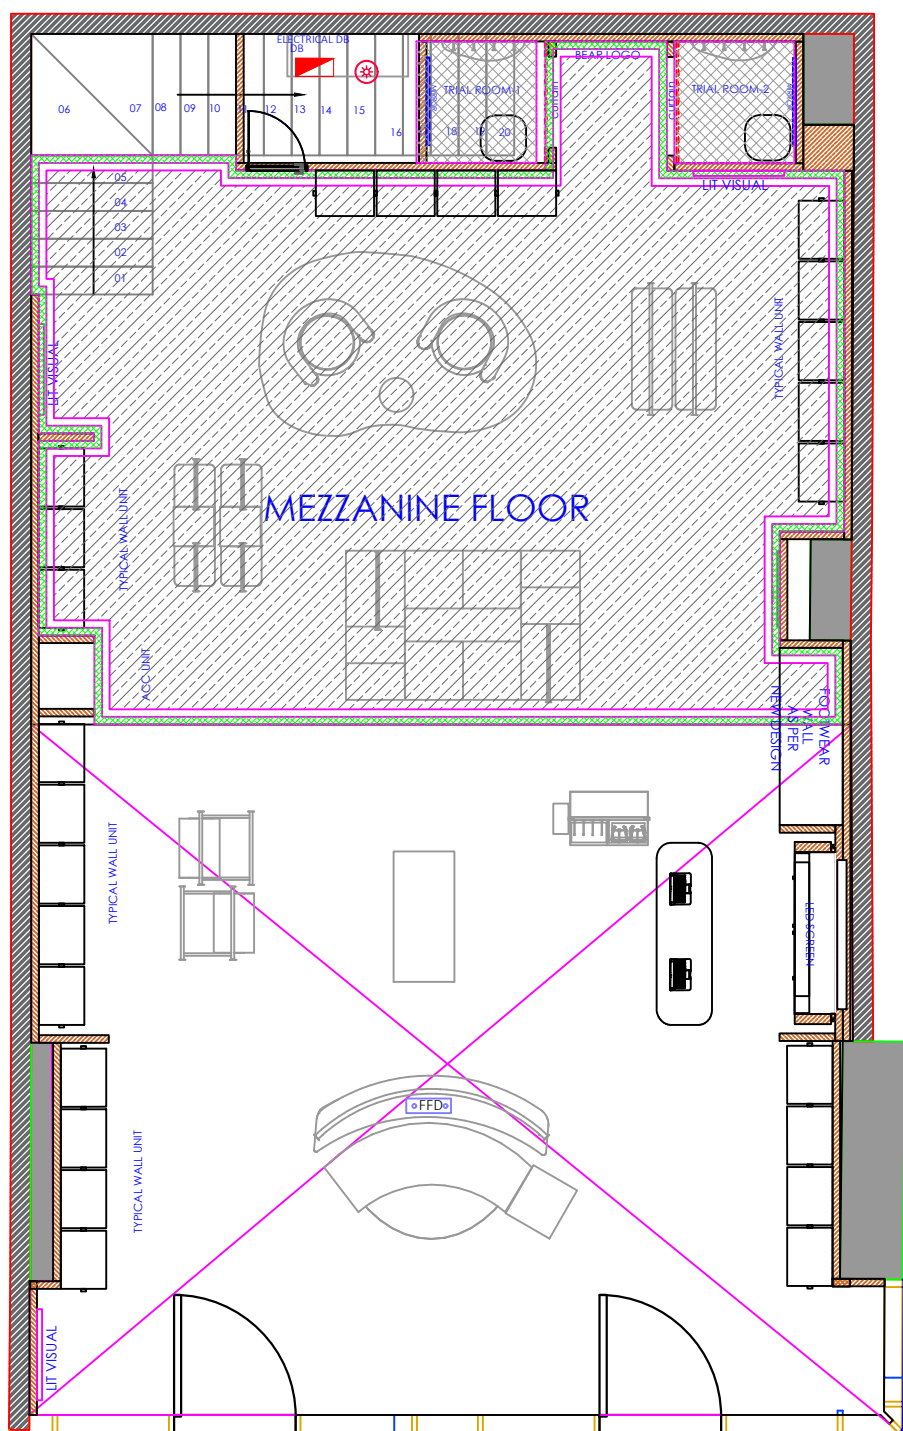

LEGEND :

LEGEND: FALSE CEILING

LEGEND NO	SYMBOL	DESCRIPTION
FC-01		GYPSUM FALSE CEILING @ 2850 MM FROM FFL FINISHED WITH CEILING-PAINT WITH ASIAN PAINTS 8780 SOUTHERN SAND CASSIN
FC-02		GYPSUM FALSE CEILING COVE @ 2950 MM FROM FFL FINISHED WITH -PAINT WITH ASIAN PAINTS 8780 SOUTHERN SAND CASSIN
FC-03		BULKHEAD IN MDF & PAINT FINISH @ MM FROM FFL (REFER FACADE)
FC-04		GYPSUM FALSE CEILING @ 2400 MM FROM FFL FINISHED WITH ASIAN PAINTS 8780 SOUTHERN SAND CASSIN SNOWFLAKE
TC		TRUE CEILING FINISHED WITH ASIAN PAINTS 8780 SOUTHERN SAND CASSIN

KEY PLAN :



DOMORE DESIGN PVT. LTD.
NO.681, SUKHADA, 2ND FLOOR, 2ND PHASE, 2ND BLOCK,
RAILWAY PARALLEL ROAD,
NEAR MALL OF ASIA, BANGALORE, KARNATAKA, 560097
domoredesign.co.in

GENERAL NOTES

- THIS DRAWING IS COPYRIGHT & PROPERTY OF DOMORE DESIGN PVT.LTD, AND IS NOT TO BE REPRODUCED, COPIED OR USED FOR ANY OTHER PURPOSE.
- WRITTEN DIMENSIONS TO BE FOLLOWED.
- DIMENSIONS TO BE CROSS CHECKED PRIOR TO THE COMMENCEMENT OF WORK.
- ALL DRAWINGS TO BE READ IN CONJUNCTION TO THE CONSULTANTS AND VENDORS DRAWINGS/DETAILS.
- FOR ALL LEGENDS, SYMBOLS, ABBREVIATIONS AND ANNOTATIONS RELATED QUERIES, REFER TO REFERENCE SHEET.
- ANY DISCREPANCY OR DOUBT IN DRAWING TO BE BROUGHT TO THE NOTICE OF DOMORE DESIGN PVT.LTD

SCALE : AS MENTIONED


REVISIONS

R01
R02
R03

PROJECT NAME :

M3M PARAGON 57
GURGOAN

COMPASS:

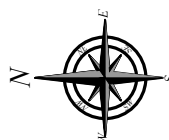



STORE INFO:

STATE	XXX
CITY	GURUGRAM
HIGHSTREET/MALL	M3M PARAGON 57
AREA	1769 SFT
SLAB BOTTOM: 6809MM	BEAM BOTTOM: 6329 MM

DRAWING NAME:

FC LAYOUT

DESIGNED BY:	CHECKED BY:	
RISHAD	AAA	
DATE:	REVISION NO:	DWG NO:
17-09-2026	R0	00

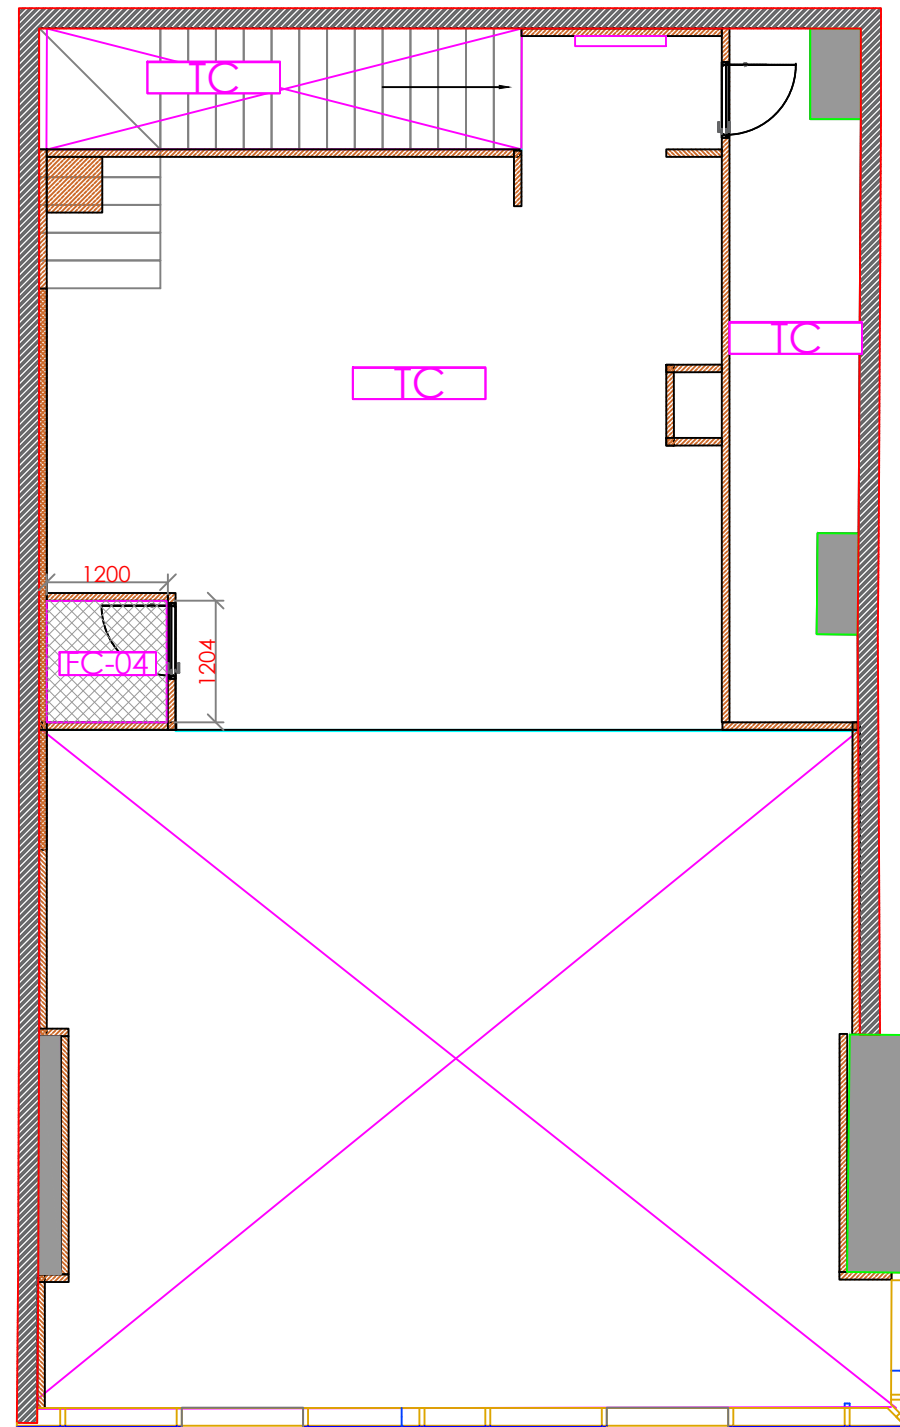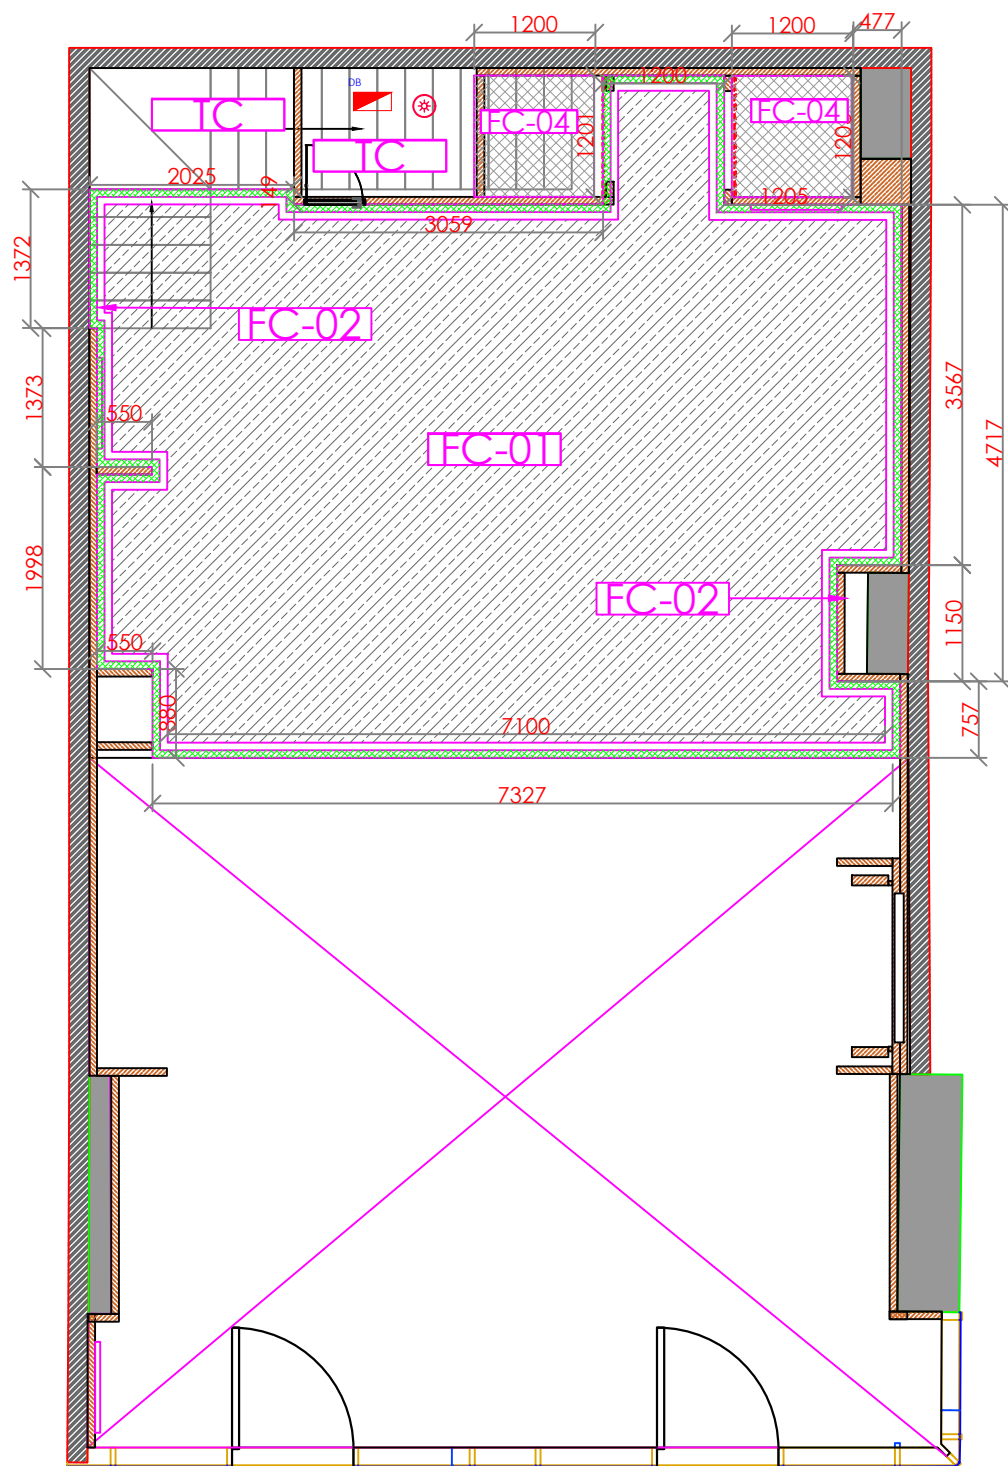

LEGEND :

LEGEND: FALSE CEILING

LEGEND NO	SYMBOL	DESCRIPTION
FC-01		GYPSUM FALSE CEILING @ 2850 MM FROM FFL FINISHED WITH CEILING-PAINT WITH ASIAN PAINTS 8780 SOUTHERN SAND CASSIN
FC-02		GYPSUM FALSE CEILING COVE @ 2950 MM FROM FFL FINISHED WITH -PAINT WITH ASIAN PAINTS 8780 SOUTHERN SAND CASSIN
FC-03		BULKHEAD IN MDF & PAINT FINISH @ MM FROM FFL (REFER FACADE)
FC-04		GYPSUM FALSE CEILING @ 2400 MM FROM FFL FINISHED WITH ASIAN PAINTS 8780 SOUTHERN SAND CASSIN:SNOWFLAKE
TC		TRUE CEILING FINISHED WITH ASIAN PAINTS 8780 SOUTHERN SAND CASSIN

KEY PLAN :




DOMORE
DESIGN PVT LTD

DOMORE DESIGN PVT. LTD.
NO.681, SUKHADA, 2ND FLOOR, 2ND PHASE, 2ND BLOCK,
RAILWAY PARALLEL ROAD,
NEAR MALL OF ASIA, BANGALORE, KARNATAKA, 560097
domoredesign.co.in

- ### GENERAL NOTES
- THIS DRAWING IS COPYRIGHT & PROPERTY OF DOMORE DESIGN PVT.LTD. AND IS NOT TO BE REPRODUCED, COPIED OR USED FOR ANY OTHER PURPOSE.
 - WRITTEN DIMENSIONS TO BE FOLLOWED.
 - DIMENSIONS TO BE CROSS CHECKED PRIOR TO THE COMMENCEMENT OF WORK.
 - ALL DRAWINGS TO BE READ IN CONJUNCTION TO THE CONSULTANTS AND VENDORS DRAWINGS/DETAILS.
 - FOR ALL LEGENDS, SYMBOLS, ABBREVIATIONS AND ANNOTATIONS RELATED QUERIES, REFER TO REFERENCE SHEET.
 - ANY DISCREPANCY OR DOUBT IN DRAWING TO BE BROUGHT TO THE NOTICE OF DOMORE DESIGN PVT.LTD
- SCALE: AS MENTIONED.


REVISIONS
R01
R02
R03

PROJECT NAME :
**M3M PARAGON 57
GURGOAN**

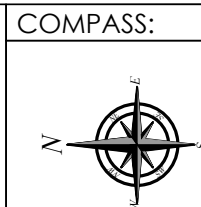


STORE INFO:	
STATE	XXX
CITY	GURUGRAM
HIGHSTREET/MALL	M3M PARAGON 57
AREA	1769 SFT
SLAB BOTTOM: 6809MM	BEAM BOTTOM: 6329 MM


DRAWING NAME:		
FC LAYOUT W/O FURNITURE		
DESIGNED BY:	CHECKED BY:	
RISHAD	AAA	
DATE:	REVISION NO:	DWG NO:
17-09-2026	R0	00

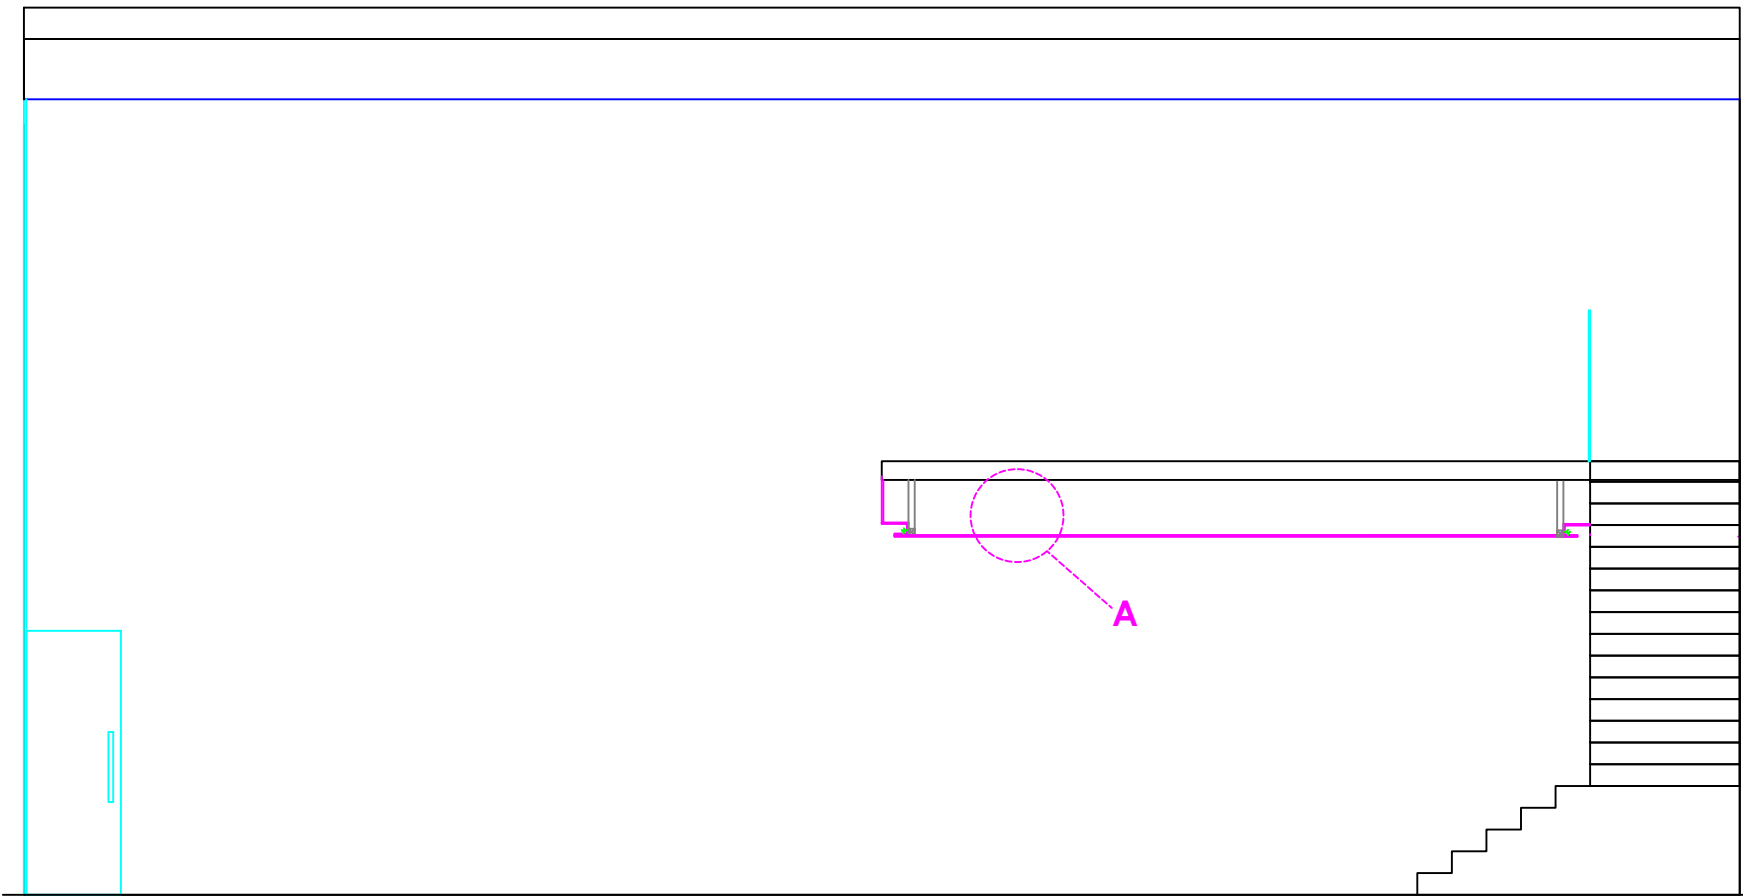

1 SECTION S1
Scale: NTS

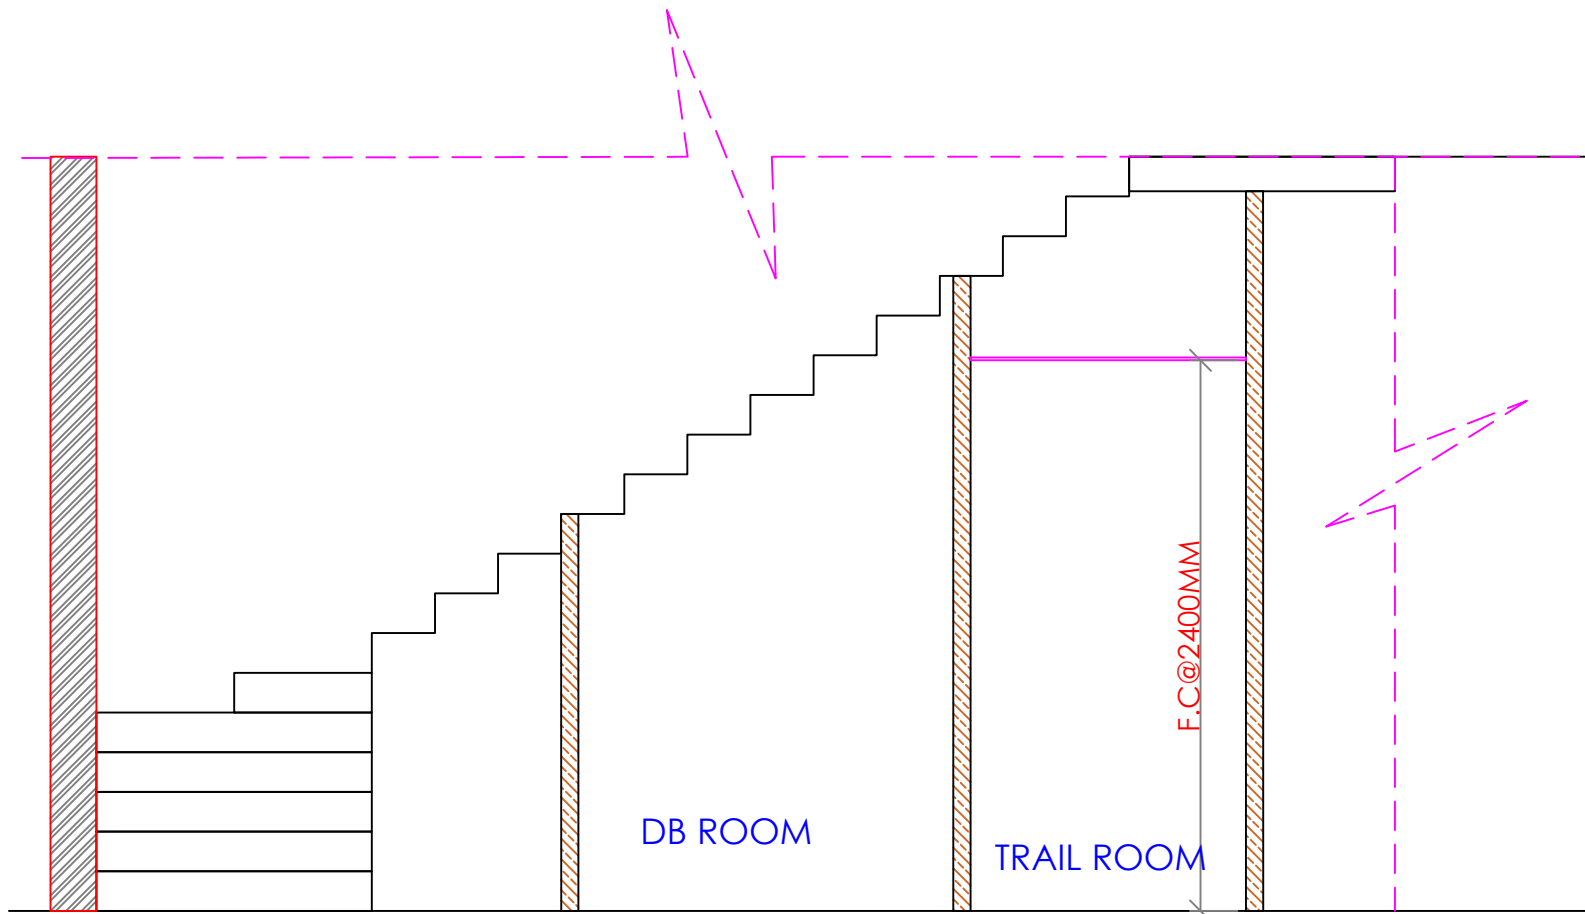

2 SECTION S2
Scale: NTS

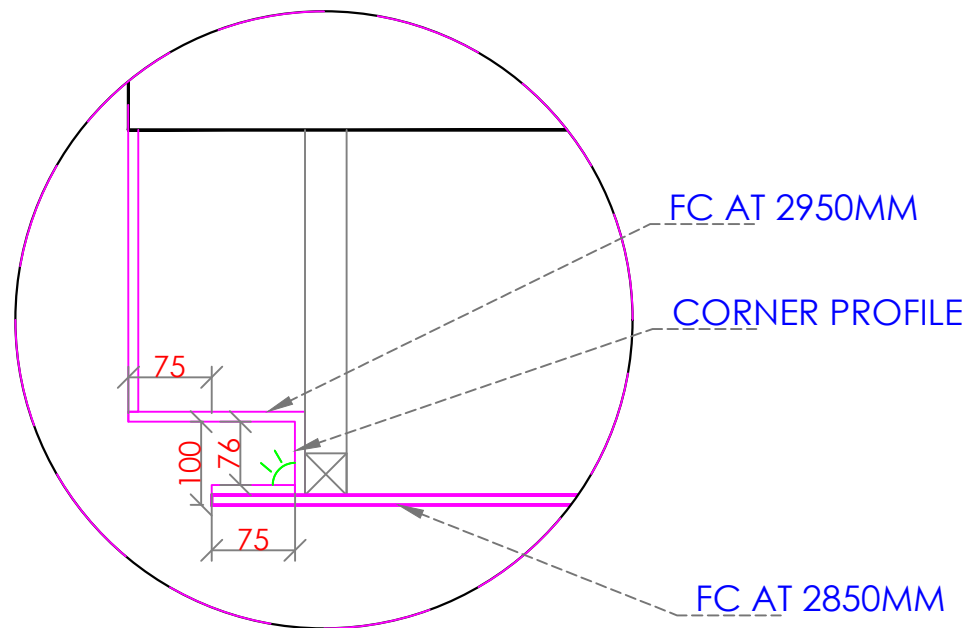


DETAIL - A

LEGEND :

LEGEND: FALSE CEILING

LEGEND NO	SYMBOL	DESCRIPTION
FC-01		GYPSUM FALSE CEILING @ 2850 MM FROM FFL FINISHED WITH CEILING-PAINT WITH ASIAN PAINTS 8780 SOUTHERN SAND CASSIN
FC-02		GYPSUM FALSE CEILING COVE @ 2950 MM FROM FFL FINISHED WITH -PAINT WITH ASIAN PAINTS 8780 SOUTHERN SAND CASSIN
FC-03		BULKHEAD IN MDF & PAINT FINISH @ MM FROM FFL (REFER FACADE)
FC-04		GYPSUM FALSE CEILING @ 2400 MM FROM FFL FINISHED WITH ASIAN PAINTS 8780 SOUTHERN SAND CASSINSNOWFLAKE
TC		TRUE CEILING FINISHED WITH ASIAN PAINTS 8780 SOUTHERN SAND CASSIN

KEY PLAN :

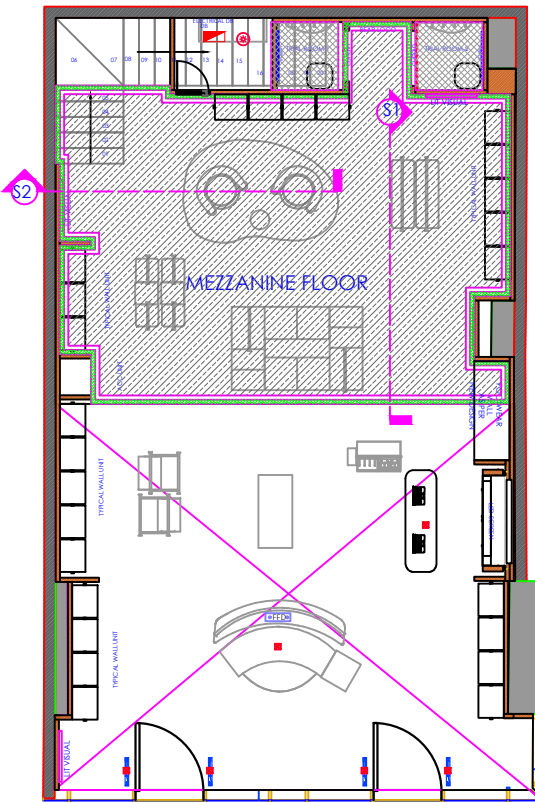

DOMORE DESIGN PVT. LTD.
NO.681, SUKHADA, 2ND FLOOR, 2ND PHASE, 2ND BLOCK,
RAILWAY PARALLEL ROAD,
NEAR MALL OF ASIA, BANGALORE, KARNATAKA, 560097
domoredesign.co.in

GENERAL NOTES

- THIS DRAWING IS COPYRIGHT & PROPERTY OF DOMORE DESIGN PVT.LTD. AND IS NOT TO BE REPRODUCED, COPIED OR USED FOR ANY OTHER PURPOSE.
- WRITTEN DIMENSIONS TO BE FOLLOWED.
- DIMENSIONS TO BE CROSS CHECKED PRIOR TO THE COMMENCEMENT OF WORK.
- ALL DRAWINGS TO BE READ IN CONJUNCTION TO THE CONSULTANTS AND VENDORS DRAWINGS/DETAILS.
- FOR ALL LEGENDS, SYMBOLS, ABBREVIATIONS AND ANNOTATIONS RELATED QUERIES, REFER TO REFERENCE SHEET.
- ANY DISCREPANCY OR DOUBT IN DRAWING TO BE BROUGHT TO THE NOTICE OF DOMORE DESIGN PVT.LTD

SCALE : AS MENTIONED


REVISIONS

R01
R02
R03

PROJECT NAME :

M3M PARAGON 57
GURGOAN

COMPASS:


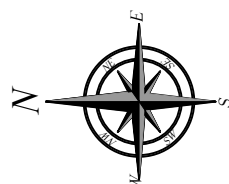


STORE INFO:

STATE	XXX
CITY	GURUGRAM
HIGHSTREET/MALL	M3M PARAGON 57
AREA	1769 SFT
SLAB BOTTOM: 6809MM	BEAM BOTTOM: 6329 MM

DRAWING NAME:

FC SECTION		
DESIGNED BY:	CHECKED BY:	
RISHAD	AAA	
DATE:	REVISION NO:	DWG NO:
17-09-2026	R0	00

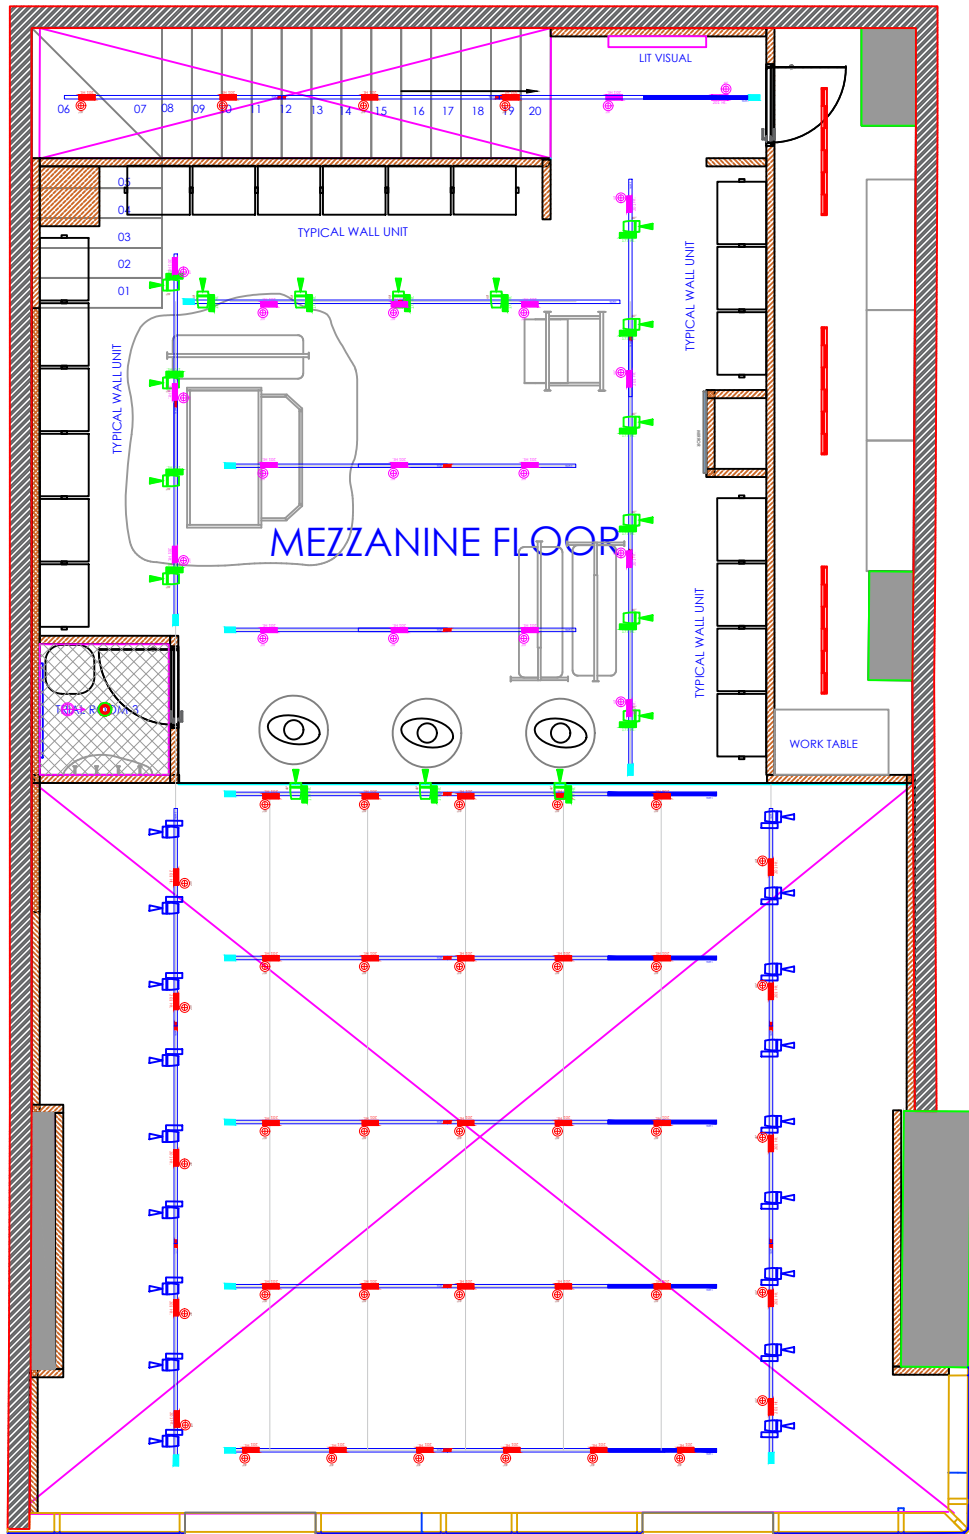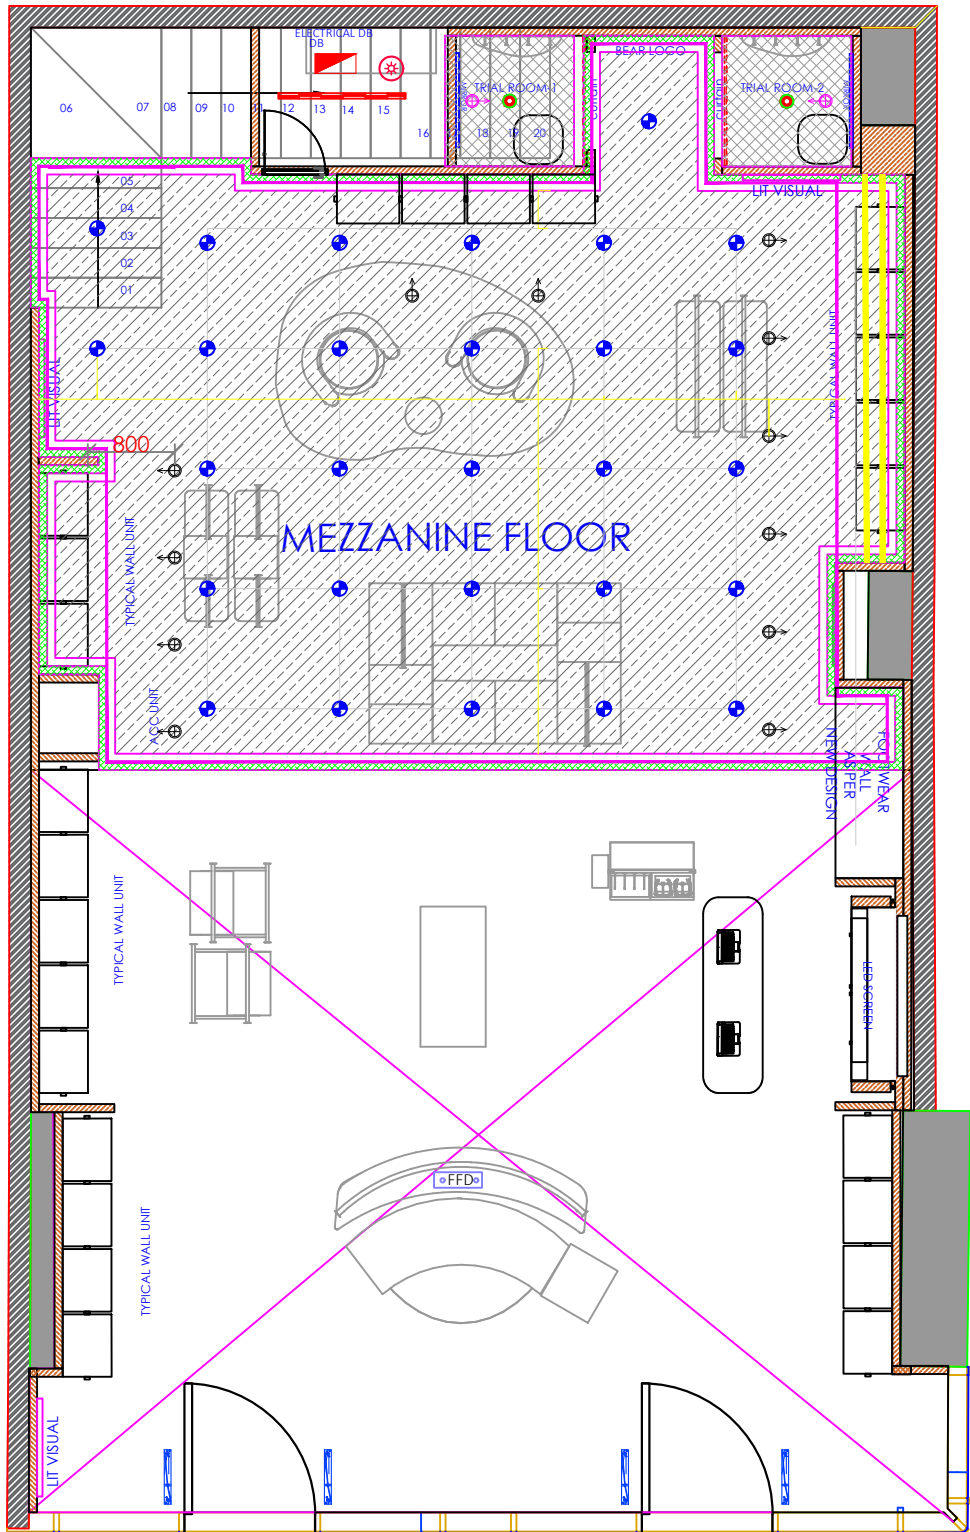

LEGEND :

LIGHTING LEGEND						
Bear house @ M3m Paragon - R00-20.07.2026						
S. NO.	SYMBOL	WATT	DESCRIPTION	GP	MP	TOTAL
1		30	METRA-30W-400 RECESSED DOWN LIGHT-ARROW	28	0	28
2		30	100-30W-400 RECESSED WALL WASHER-ARROW	12	0	12
3		30	30W-30W-400 TRACK LIGHT-ARROW	0	17	17
4		30	30W-30W-400 TRACK LIGHT-ARROW	0	18	18
5		40	30W-40W-400 TRACK LIGHT-ARROW	0	18	18
6		40	30W-40W-400 TRACK LIGHT-ARROW	0	40	40
7		30	METRA-30W-400 RECESSED DOWN LIGHT-ARROW	2	1	3
8		30	100-30W-400 RECESSED WALL WASHER-ARROW	2	1	3
9		15	LED TUBE LIGHT-18W	2	3	5
10			MTR. POWER TRACK	0	30	30
11			MTR. POWER TRACK	0	6	6
12			CONNECTOR	0	23	23
13			LED CAP	0	13	13
14			LED CAP	0	13	13
15			SUSPENSION WIRE-1.5MTR.	0	102	102
16		14.40W	LED STRIP LIGHT-14.40W FOR CEILING COVER-1.5MTR.	30	0	30
17			30W-30W SURFACE MOUNT LED TUBE LIGHT-18W-18W-18W	2	0	2

KEY PLAN :



DOMORE DESIGN PVT. LTD.
NO.681, SUKHADA, 2ND FLOOR, 2ND PHASE, 2ND BLOCK,
RAILWAY PARALLEL ROAD,
NEAR MALL OF ASIA, BANGALORE, KARNATAKA, 560097
domoredesign.co.in

GENERAL NOTES

- THIS DRAWING IS COPYRIGHT & PROPERTY OF DOMORE DESIGN PVT.LTD. AND IS NOT TO BE REPRODUCED, COPIED OR USED FOR ANY OTHER PURPOSE.
- WRITTEN DIMENSIONS TO BE FOLLOWED.
- DIMENSIONS TO BE CROSS CHECKED PRIOR TO THE COMMENCEMENT OF WORK.
- ALL DRAWINGS TO BE READ IN CONJUNCTION TO THE CONSULTANTS AND VENDORS DRAWINGS/DETAILS.
- FOR ALL LEGENDS, SYMBOLS, ABBREVIATIONS AND ANNOTATIONS RELATED QUERIES, REFER TO REFERENCE SHEET.
- ANY DISCREPANCY OR DOUBT IN DRAWING TO BE BROUGHT TO THE NOTICE OF DOMORE DESIGN PVT.LTD

SCALE : AS MENTIONED


REVISIONS

R01
R02
R03

PROJECT NAME :

M3M PARAGON 57
GURGOAN

COMPASS:

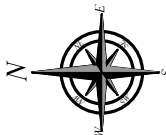


STORE INFO:

STATE	XXX
CITY	GURUGRAM
HIGHSTREET/MALL	M3M PARAGON 57
AREA	1769 SFT
SLAB BOTTOM: 6809MM	BEAM BOTTOM: 6329 MM

DRAWING NAME:

LIGHTING LAYOUT

DESIGNED BY:	CHECKED BY:	
RISHAD	AAA	
DATE:	REVISION NO:	DWG NO:
17-09-2026	R0	00

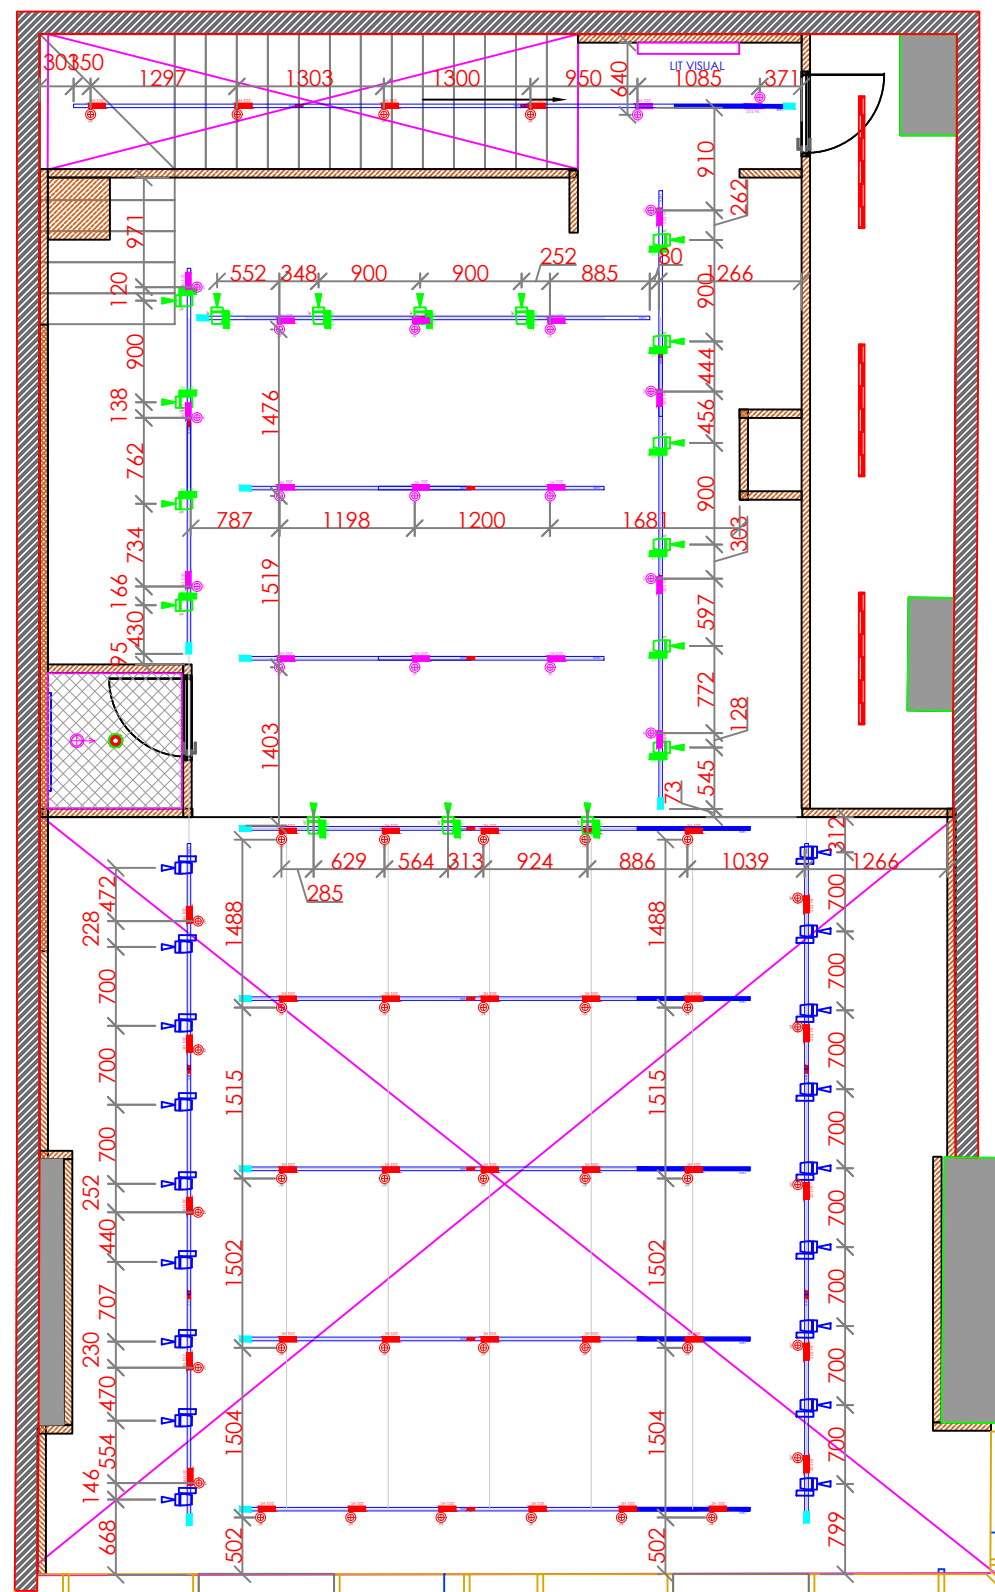

DRAWING NAME:		
LIGHTING W/O LAYOUT		
DESIGNED BY:	CHECKED BY:	
RISHAD	AAA	
DATE:	REVISION NO:	DWG NO:
17-09-2026	R0	00

BEAM BOTTOM: 6329 MM

00


LEGEND :

KEY PLAN :

DRAWING NAME:

HVAC LAYOUT

DESIGNED BY:	CHECKED BY:	
RISHAD	AAA	
DATE:	REVISION NO:	DWG NO:
17-09-2026	R0	00

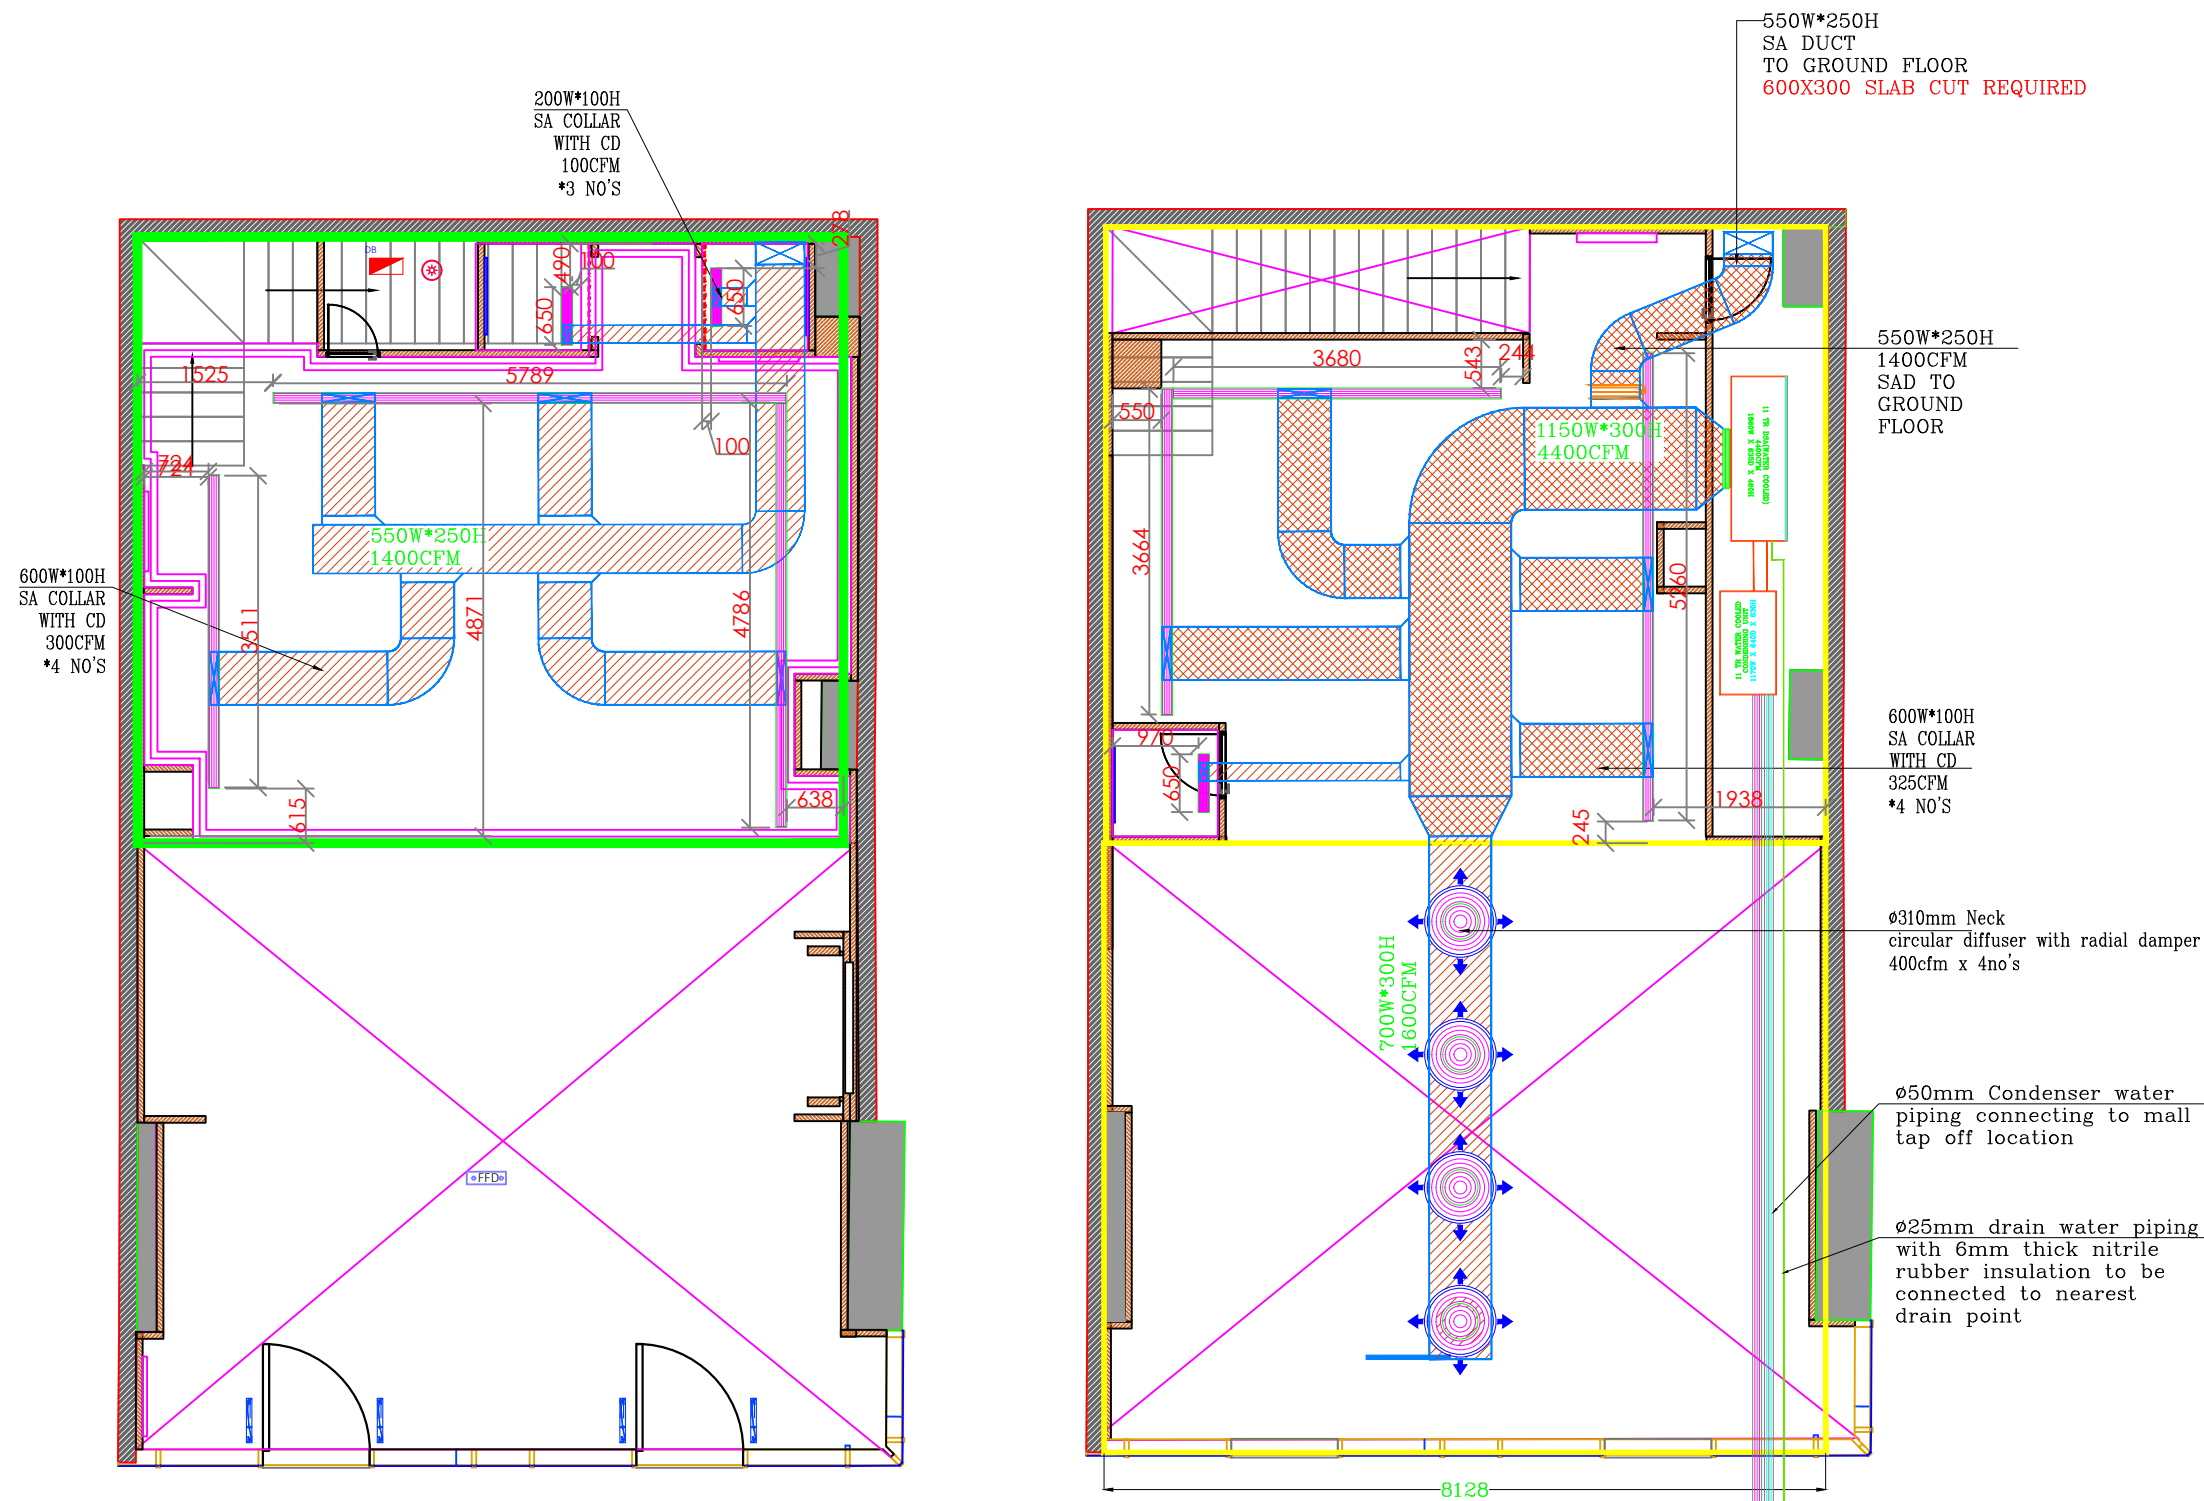

GENERAL NOTES

- THIS DRAWING IS COPYRIGHT & PROPERTY OF DOMORE DESIGN PVT.LTD. AND IS NOT TO BE REPRODUCED, COPIED OR USED FOR ANY OTHER PURPOSE.
- WRITTEN DIMENSIONS TO BE FOLLOWED.
- DIMENSIONS TO BE CROSS CHECKED PRIOR TO THE COMMENCEMENT OF WORK.
- ALL DRAWINGS TO BE READ IN CONJUNCTION TO THE CONSULTANTS AND VENDORS DRAWINGS/DETAILS.
- FOR ALL LEGENDS, SYMBOLS, ABBREVIATIONS AND ANNOTATIONS RELATED QUERIES, REFER TO REFERENCE SHEET.
- ANY DISCREPANCY OR DOUBT IN DRAWING TO BE BROUGHT TO THE NOTICE OF DOMORE DESIGN PVT.LTD

SCALE : AS MENTIONED


REVISIONS

R01
R02
R03

PROJECT NAME :

M3M PARAGON 57
GURGOAN

COMPASS:

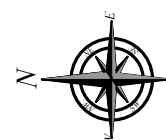

STORE INFO:

STATE	XXX
CITY	GURUGRAM
HIGHSTREET/MALL	M3M PARAGON 57
AREA	1769 SFT
SLAB BOTTOM: 6809MM	BEAM BOTTOM: 6329 MM

LEGEND :

KEY PLAN :

DRAWING NAME:

HVAC LAYOUT

DESIGNED BY:	CHECKED BY:	
RISHAD	AAA	
DATE:	REVISION NO:	DWG NO:
17-09-2026	R0	00

SCHEDULE OF TRAPEZE HANGER

NOMINAL PIPE SIZE		MAXIMUM HANGER SPACING (mm)	MINIMUM ROD SIZE (mm)	M.S.ANGLE SIZE (mm)
inc	mm			
1/2"	15	2500	8	40 X 40 X 4
3/4"	20	2500	8	40 X 40 X 4
1"	25	2500	8	40 X 40 X 4
1¼"	32	2800	8	40 X 40 X 4
1½"	40	2800	8	40 X 40 X 4
2"	50	2800	10	40 X 40 X 4
2½"	65	3200	10	50 X 50 X 4
3"	80	3200	10	50 X 50 X 4
4"	100	4200	12	50 X 50 X 4
5"	125	4200	16	50 X 50 X 4
6"	150	5200	16	50 X 50 X 4

1. ALL DIMENSIONS ARE IN MM.
2. RECTANGULAR DUCTS ARE FACTORY MADE WITH TDC/TDF.
3. DRAIN PIPE TO BE CONNECTED TO NEAREST DRAIN POINT.

SCHEDULE OF DUCT


DUCT SIZE IN mm	SHEET GAUGE	FULLY THREADED ROD IN (mm)	TYPE OF JOINT	SPACING SUPPORT	TYPE OF SUPPORT
25 TO 750	24 G	6mm	TDF/TDC FLANGES	2000mm	GI SLOTTED ANGLE
751 TO 1500	22 G	8mm	TDF/TDC FLANGES	2000mm	GI SLOTTED ANGLE
1501 & 2250	20 G	10mm	TDF/TDC FLANGES	2000mm	MS L ANGLE 25X25X5 MM THICK
2251 & Above	18 G	12mm	TDF/TDC FLANGES	2000mm	MS L ANGLE 25X25X5 MM THICK

SL No.	LOCATION	MODEL	Cooling capacity TR	AIR FLOW CFM	ESP (ft) of WCL	"AIR ON COIL DB/WB-C"	"AIR OFF COIL DB/WB-C"	WATER FLOW GPM	"UNIT TYPE"	Power I/P Watts	Dimensions (mm) H D W	Electrical Power Supply	Weight Kg	QTY Nos
1	NORBERO@M3M PARAGON 57		3.0	1200	10	24.0 / 17.1	13.39/12.04	12	Water cooled Ducted Split AC	—	—	—	—	2

SCHEDULE OF CHILLED WATER PIPE SUPPORT

NOMINAL PIPE SIZE		MAXIMUM SUPPORT SPACING (mm)	ANCHOR BOLT SIZE (mm)	M.S.ANGLE SIZE (mm)	CLAMP SIZE (mm)
inc	mm				
1/2"	15	2500	8	40 X 40 X 4	2 x 25
3/4"	20	2500	8	40 X 40 X 4	2 x 25
1"	25	2500	8	40 X 40 X 4	2 x 25
1¼"	32	2800	8	40 X 40 X 4	2 x 25
1½"	40	2800	8	40 X 40 X 4	2 x 25
2"	50	2800	10	40 X 40 X 4	2 x 25
2½"	65	3200	10	50 X 50 X 4	3 x 40
3"	80	3200	10	50 X 50 X 4	3 x 40
4"	100	4200	12	50 X 50 X 4	3 x 50
5"	125	4200	16	50 X 50 X 4	3 x 50
6"	150	5200	16	50 X 50 X 4	3 x 50
8" TO 10"	200 TO 250	5200	16	50 X 50 X 4	4 x 50

Valves Connections

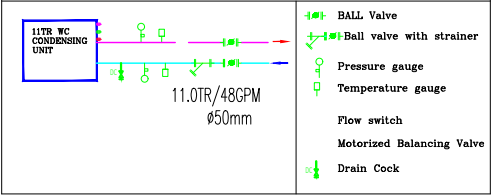


- Notes:
1. DX IDU and Condensing Unit to be connected with Fire alarm system using control module. Condensing unit needs to be off incase of fire
 2. The DX IDU and Condensing unit should be getting turned off incase of smoke detectors are detecting fire above and below false ceiling.


HVAC Legend

1		Evaporator Unit
2		Water Cooled Condensing Unit
3		Supply Rectangular Air Duct
4		Acoustic Insulation
5		Thermal Insulation
6		Supply Air Grill
7		Volume Control Damper
8		Refrigerant Pipe
9		S/R Condenser Water Pipe
10		Drain pipe connected to nearest drain point.
11		Circular Diffuser


THERMAL INSULATION DETAILS

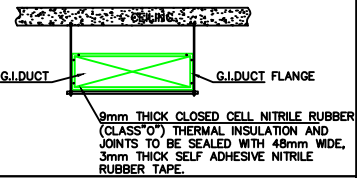

ACOUSTIC INSULATION DETAILS

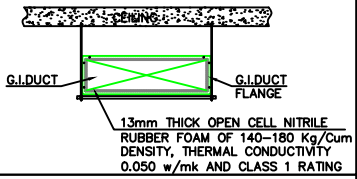

DUCT SUPPORT DETAILS

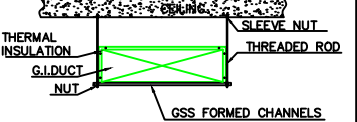

DOMORE DESIGN PVT. LTD.
NO.681, SUKHADA, 2ND FLOOR, 2ND PHASE, 2ND BLOCK,
RAILWAY PARALLEL ROAD,
NEAR MALL OF ASIA, BANGALORE, KARNATAKA, 560097
domoredesign.co.in

GENERAL NOTES

- THIS DRAWING IS COPYRIGHT & PROPERTY OF DOMORE DESIGN PVT.LTD. AND IS NOT TO BE REPRODUCED, COPIED OR USED FOR ANY OTHER PURPOSE.
- WRITTEN DIMENSIONS TO BE FOLLOWED.
- DIMENSIONS TO BE CROSS CHECKED PRIOR TO THE COMMENCEMENT OF WORK.
- ALL DRAWINGS TO BE READ IN CONJUNCTION TO THE CONSULTANTS AND VENDORS DRAWINGS/DETAILS.
- FOR ALL LEGENDS, SYMBOLS, ABBREVIATIONS AND ANNOTATIONS RELATED QUERIES, REFER TO REFERENCE SHEET.
- ANY DISCREPANCY OR DOUBT IN DRAWING TO BE BROUGHT TO THE NOTICE OF DOMORE DESIGN PVT.LTD

SCALE : AS MENTIONED


REVISIONS

R01
R02
R03

PROJECT NAME :



M3M PARAGON 57
GURGOAN

COMPASS:

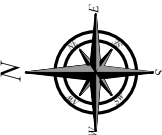

STORE INFO:

STATE	XXX
CITY	GURUGRAM
HIGHSTREET/MALL	M3M PARAGON 57
AREA	1769 SFT
SLAB BOTTOM: 6809MM	BEAM BOTTOM: 6329 MM

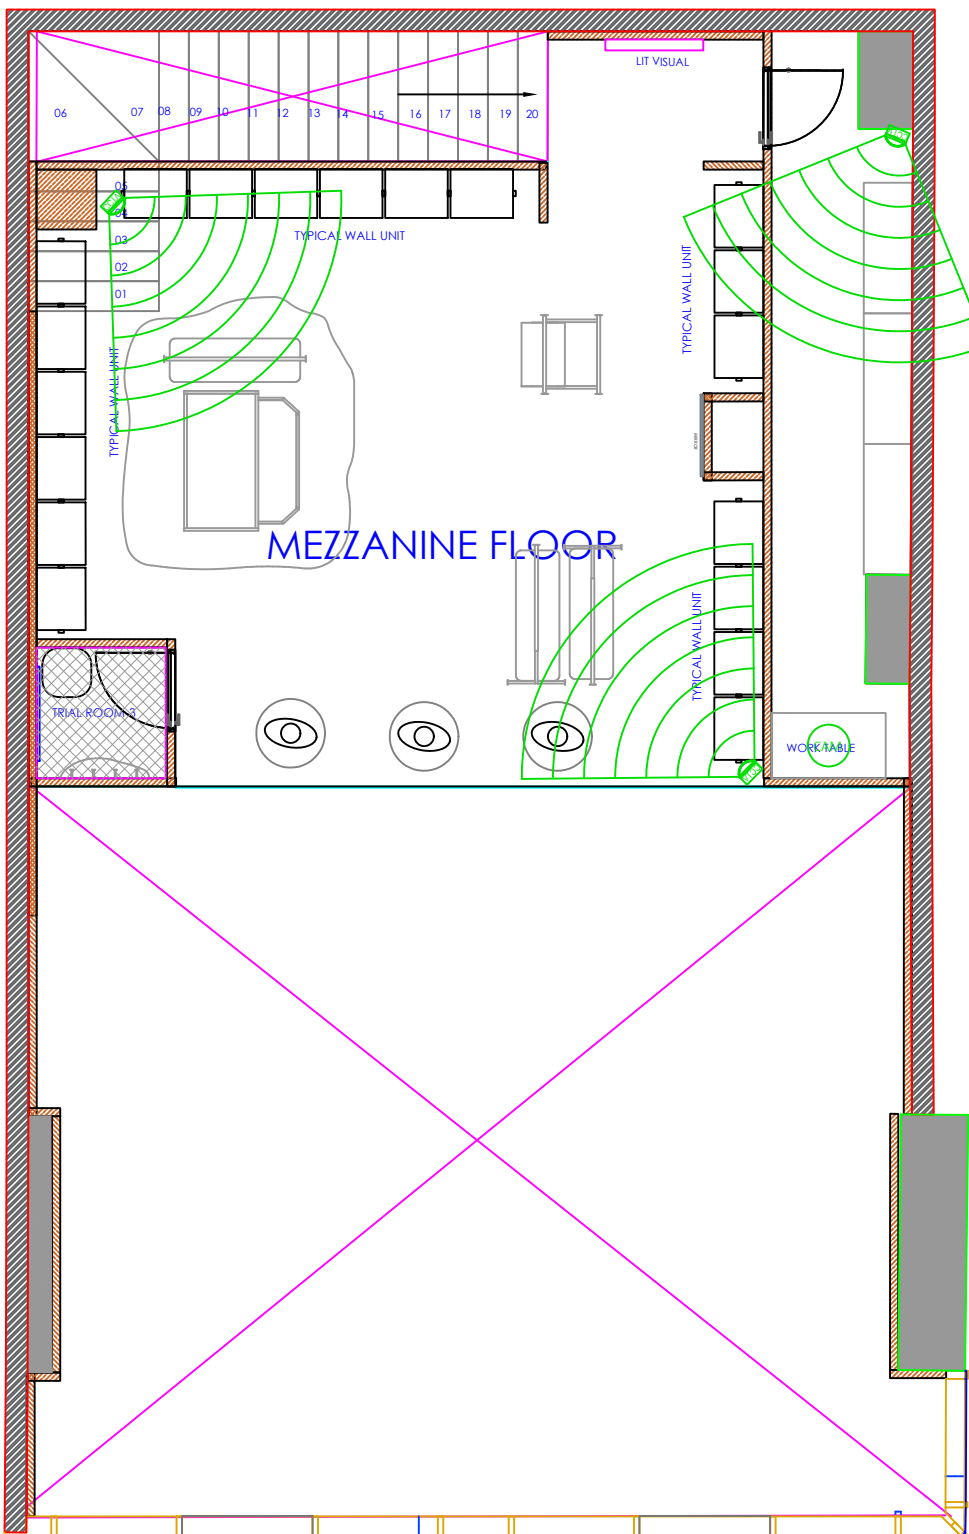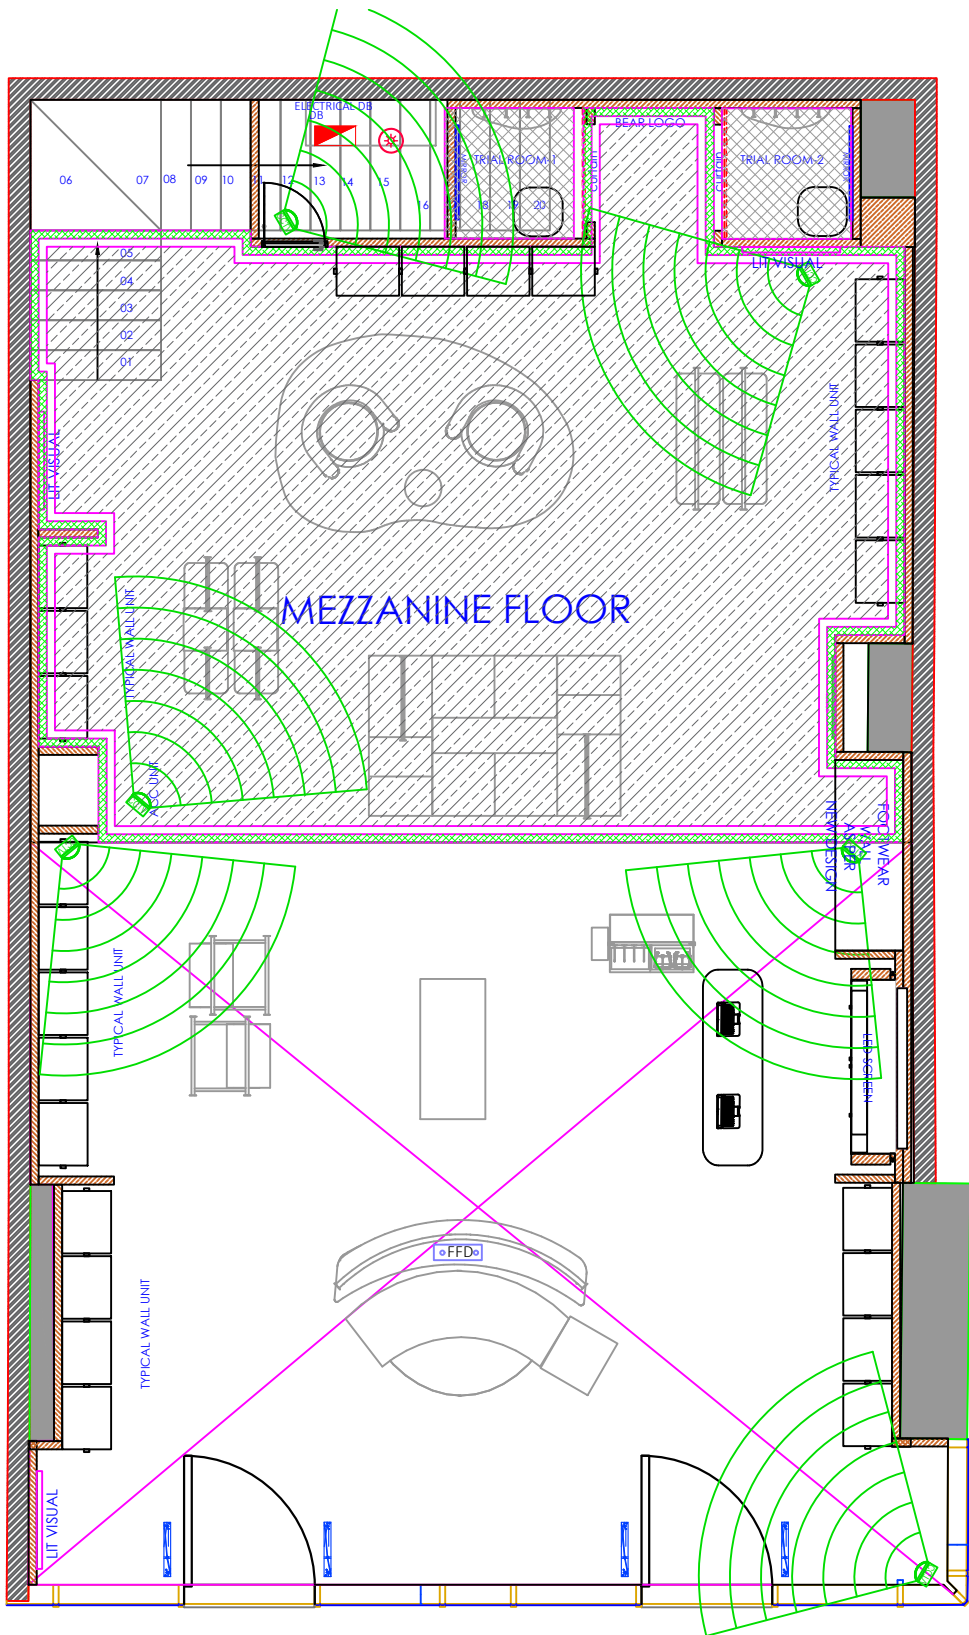

LEGEND :

LEGEND : CCTV

SINO	SYMBOL	DESCRIPTION	QTY.
1		HIK VISION MAKE ,INFRARED ENABLED ONE HIGH RESOLUTION , FIXED 6.0MM LENS DOME CAMERA	09
2		FISH EYE CAMERA	00
3		BULLET-PROOF CAMERA FOR OUTSIDE	00
4		DVR UNIT	01

KEY PLAN :

DRAWING NAME:

CCTV LAYOUT

DESIGNED BY:	CHECKED BY:	
RISHAD	AAA	
DATE:	REVISION NO:	DWG NO:
17-09-2026	R0	00



DOMORE DESIGN PVT. LTD.
NO.681, SUKHADA, 2ND FLOOR, 2ND PHASE, 2ND BLOCK,
RAILWAY PARALLEL ROAD,
NEAR MALL OF ASIA, BANGALORE, KARNATAKA, 560097
domoredesign.co.in

GENERAL NOTES

- THIS DRAWING IS COPYRIGHT & PROPERTY OF DOMORE DESIGN PVT.LTD, AND IS NOT TO BE REPRODUCED, COPIED OR USED FOR ANY OTHER PURPOSE.
- WRITTEN DIMENSIONS TO BE FOLLOWED.
- DIMENSIONS TO BE CROSS CHECKED PRIOR TO THE COMMENCEMENT OF WORK.
- ALL DRAWINGS TO BE READ IN CONJUNCTION TO THE CONSULTANTS AND VENDORS DRAWINGS/DETAILS.
- FOR ALL LEGENDS, SYMBOLS, ABBREVIATIONS AND ANNOTATIONS RELATED QUERIES, REFER TO REFERENCE SHEET.
- ANY DISCREPANCY OR DOUBT IN DRAWING TO BE BROUGHT TO THE NOTICE OF DOMORE DESIGN PVT.LTD

SCALE : AS MENTIONED


REVISIONS

R01
R02
R03

PROJECT NAME :



M3M PARAGON 57
GURGOAN

COMPASS:

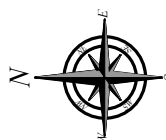

STORE INFO:

STATE	XXX
CITY	GURUGRAM
HIGHSTREET/MALL	M3M PARAGON 57
AREA	1769 SFT
SLAB BOTTOM: 6809MM	BEAM BOTTOM: 6329 MM

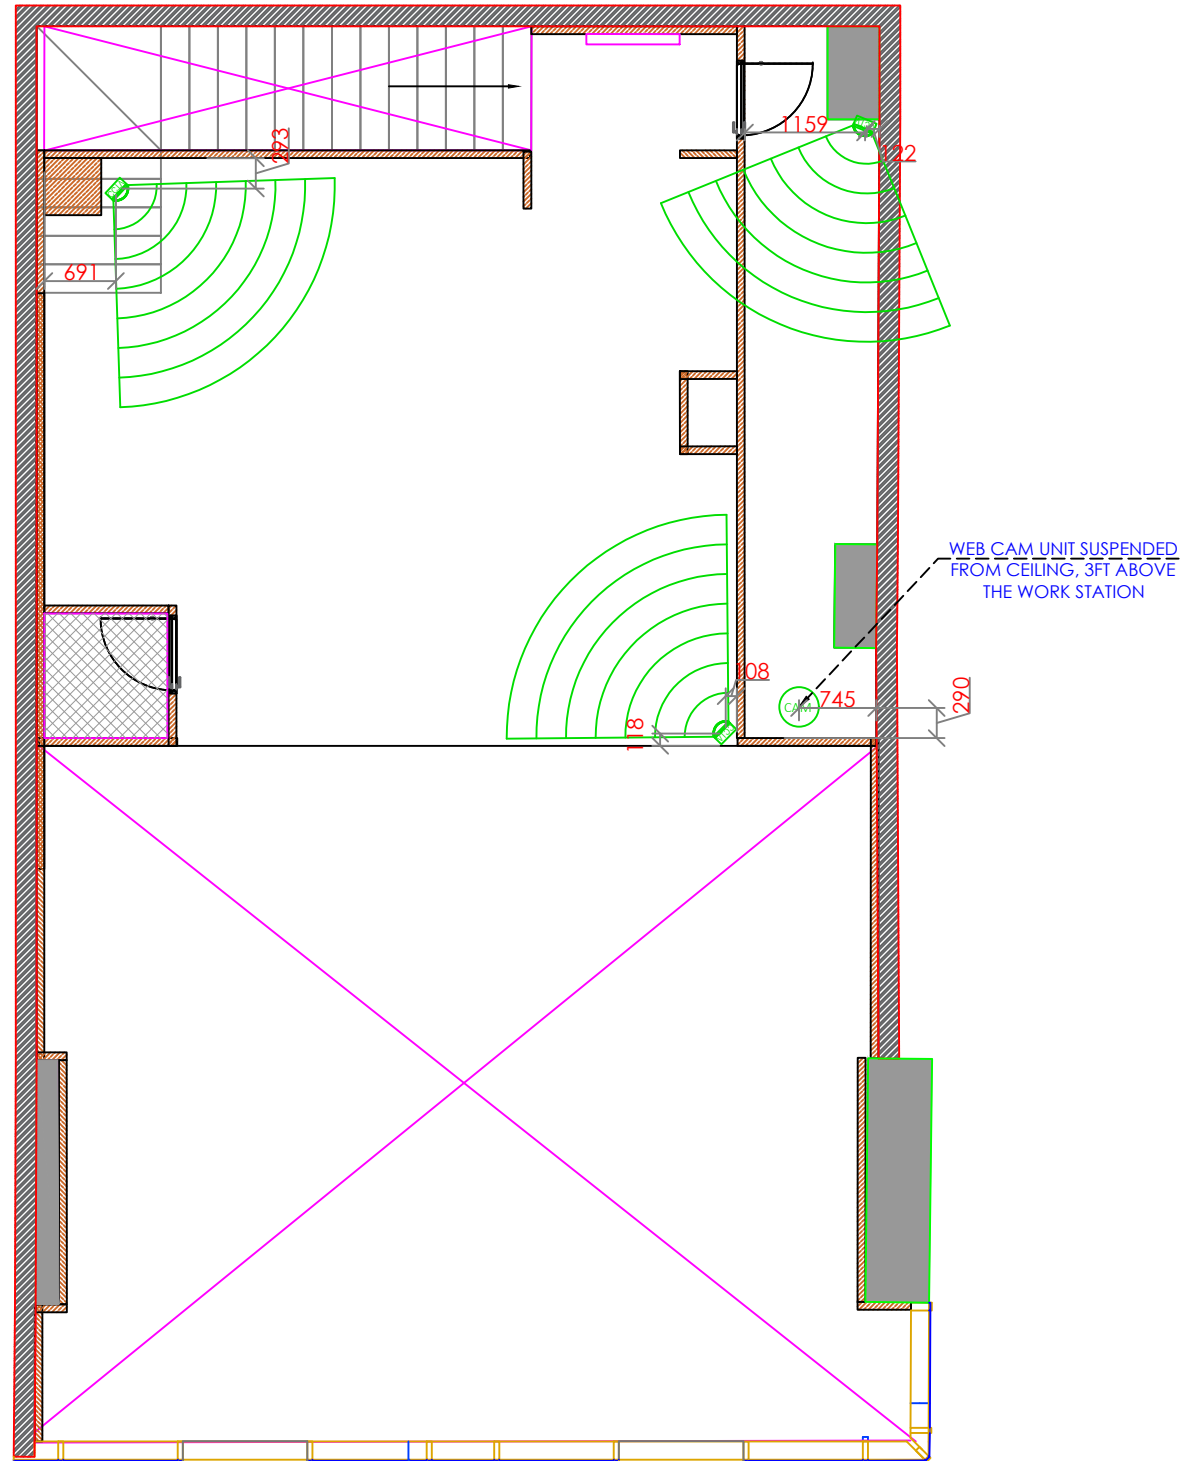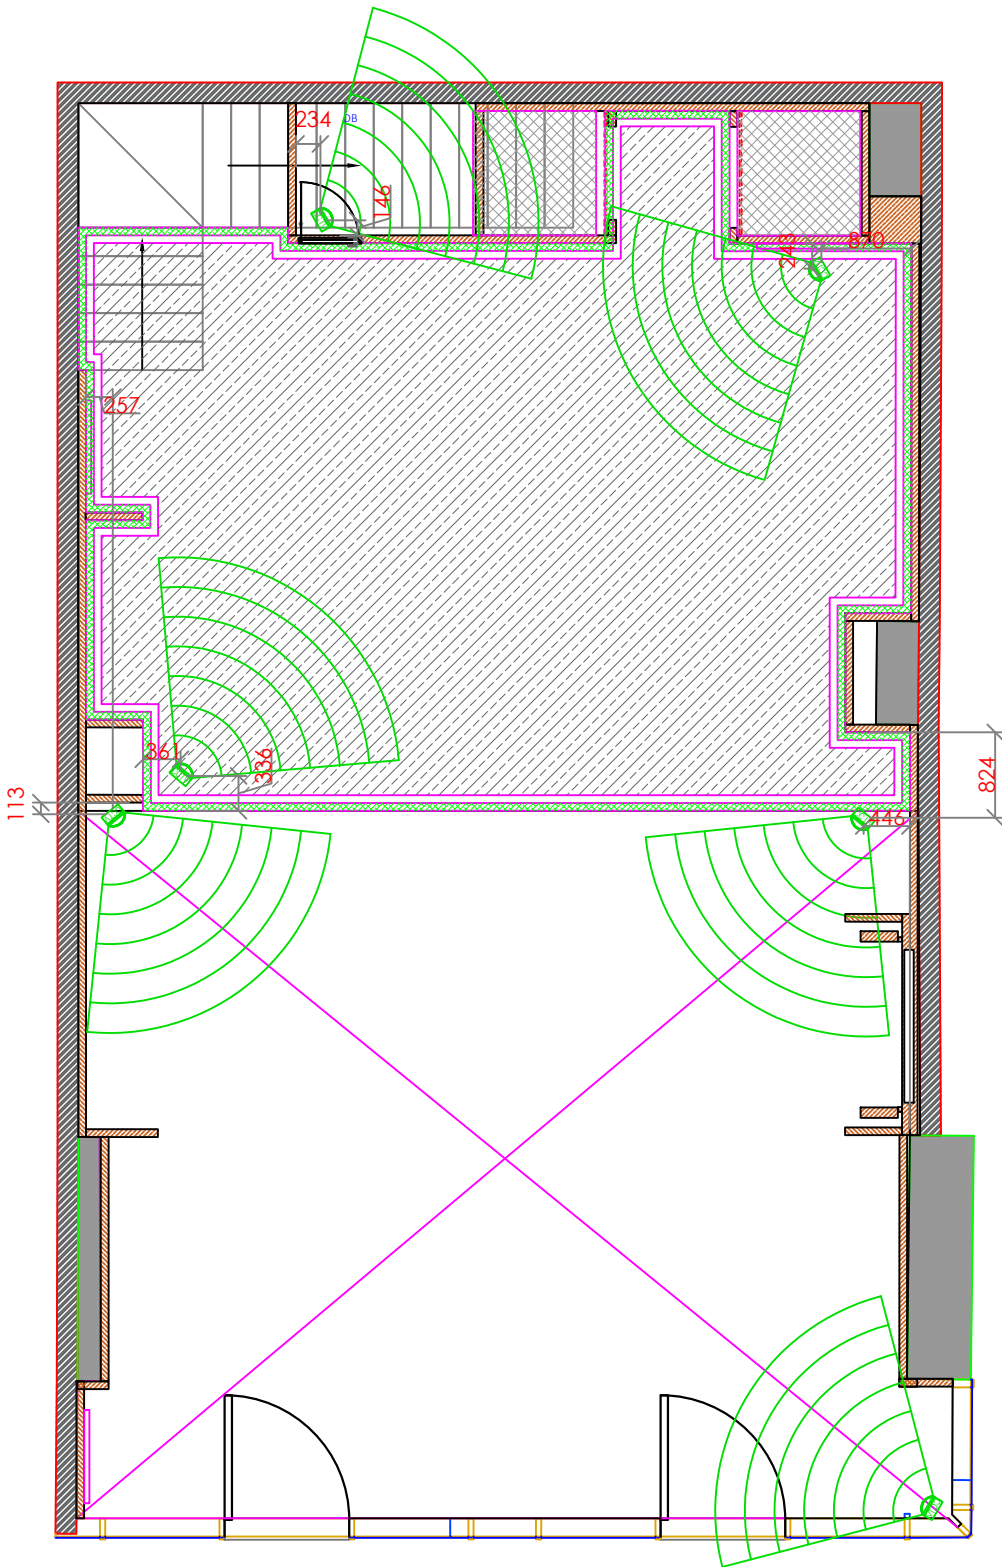

LEGEND :

KEY PLAN :



DOMORE DESIGN PVT. LTD.
NO.681, SUKHADA, 2ND FLOOR, 2ND PHASE, 2ND BLOCK,
RAILWAY PARALLEL ROAD,
NEAR MALL OF ASIA, BANGALORE, KARNATAKA, 560097
domoredesign.co.in

GENERAL NOTES

- THIS DRAWING IS COPYRIGHT & PROPERTY OF DOMORE DESIGN PVT.LTD. AND IS NOT TO BE REPRODUCED, COPIED OR USED FOR ANY OTHER PURPOSE.
- WRITTEN DIMENSIONS TO BE FOLLOWED.
- DIMENSIONS TO BE CROSS CHECKED PRIOR TO THE COMMENCEMENT OF WORK.
- ALL DRAWINGS TO BE READ IN CONJUNCTION TO THE CONSULTANTS AND VENDORS DRAWINGS/DETAILS.
- FOR ALL LEGENDS, SYMBOLS, ABBREVIATIONS AND ANNOTATIONS RELATED QUERIES, REFER TO REFERENCE SHEET.
- ANY DISCREPANCY OR DOUBT IN DRAWING TO BE BROUGHT TO THE NOTICE OF DOMORE DESIGN PVT.LTD

SCALE : AS MENTIONED


REVISIONS

R01
R02
R03

PROJECT NAME :

M3M PARAGON 57
GURGOAN

COMPASS:

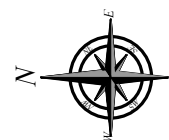



STORE INFO:

STATE	XXX
CITY	GURUGRAM
HIGHSTREET/MALL	M3M PARAGON 57
AREA	1769 SFT
SLAB BOTTOM: 6809MM	BEAM BOTTOM: 6329 MM

DRAWING NAME:

CCTV W/O LAYOUT

DESIGNED BY:	CHECKED BY:	
RISHAD	AAA	
DATE:	REVISION NO:	DWG NO:
17-09-2026	R0	00

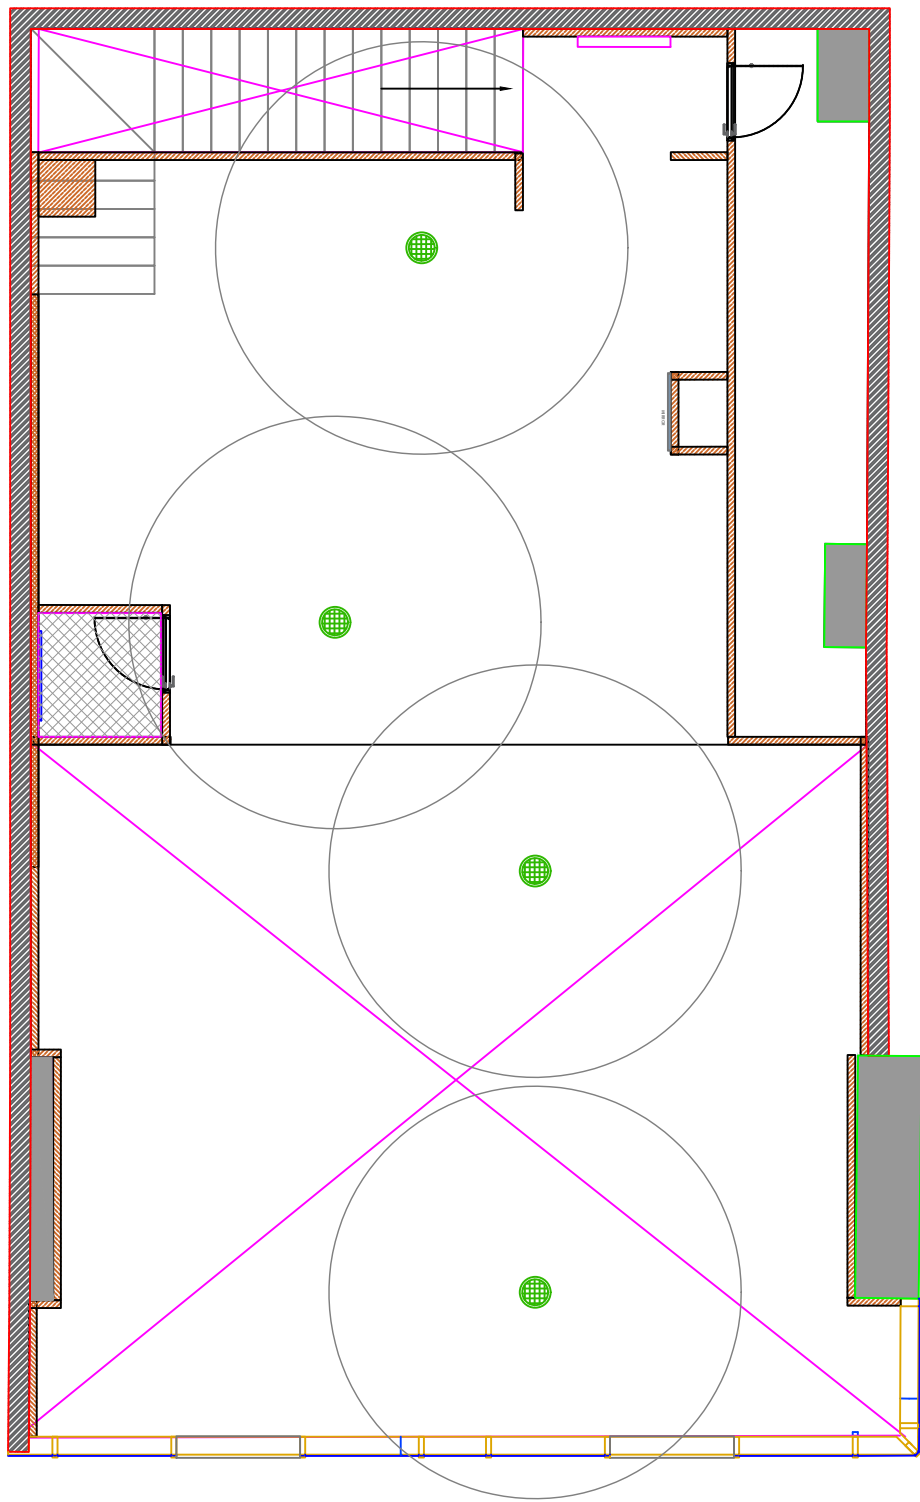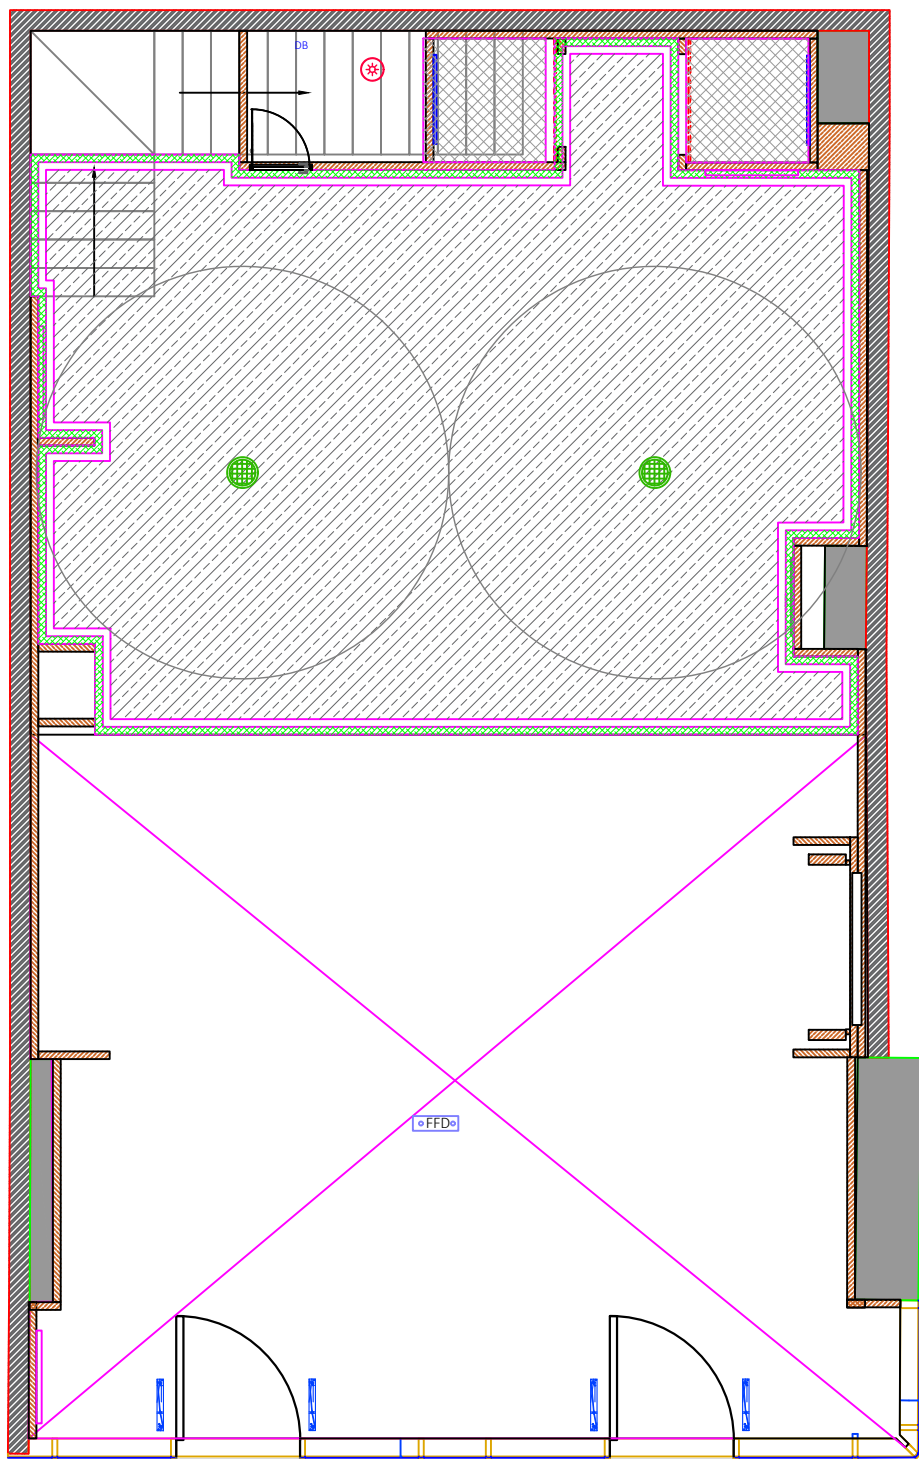

LEGEND :

LEGEND : AUDIO

SINO	SYMBOL	DESCRIPTION	QTY.
1		CEILING MOUNTED SPEAKERS	06
2		SURFACE MOUNTED SPEAKERS	00
3		AMPLIFIER	01

KEY PLAN :

DRAWING NAME:

AUDIO LAYOUT		
DESIGNED BY:	CHECKED BY:	
RISHAD	AAA	
DATE:	REVISION NO:	DWG NO:
17-09-2026	R0	00



DOMORE DESIGN PVT. LTD.
NO.681, SUKHADA, 2ND FLOOR, 2ND PHASE, 2ND BLOCK,
RAILWAY PARALLEL ROAD,
NEAR MALL OF ASIA, BANGALORE, KARNATAKA, 560097
domoredesign.co.in

GENERAL NOTES

- THIS DRAWING IS COPYRIGHT & PROPERTY OF DOMORE DESIGN PVT.LTD, AND IS NOT TO BE REPRODUCED, COPIED OR USED FOR ANY OTHER PURPOSE.
- WRITTEN DIMENSIONS TO BE FOLLOWED.
- DIMENSIONS TO BE CROSS CHECKED PRIOR TO THE COMMENCEMENT OF WORK.
- ALL DRAWINGS TO BE READ IN CONJUNCTION TO THE CONSULTANTS AND VENDORS DRAWINGS/DETAILS.
- FOR ALL LEGENDS, SYMBOLS, ABBREVIATIONS AND ANNOTATIONS RELATED QUERIES, REFER TO REFERENCE SHEET.
- ANY DISCREPANCY OR DOUBT IN DRAWING TO BE BROUGHT TO THE NOTICE OF DOMORE DESIGN PVT.LTD

SCALE : AS MENTIONED


REVISIONS

R01
R02
R03

PROJECT NAME :


M3M PARAGON 57
GURGOAN

COMPASS:

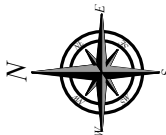

STORE INFO:

STATE	XXX
CITY	GURUGRAM
HIGHSTREET/MALL	M3M PARAGON 57
AREA	1769 SFT
SLAB BOTTOM: 6809MM	BEAM BOTTOM: 6329 MM

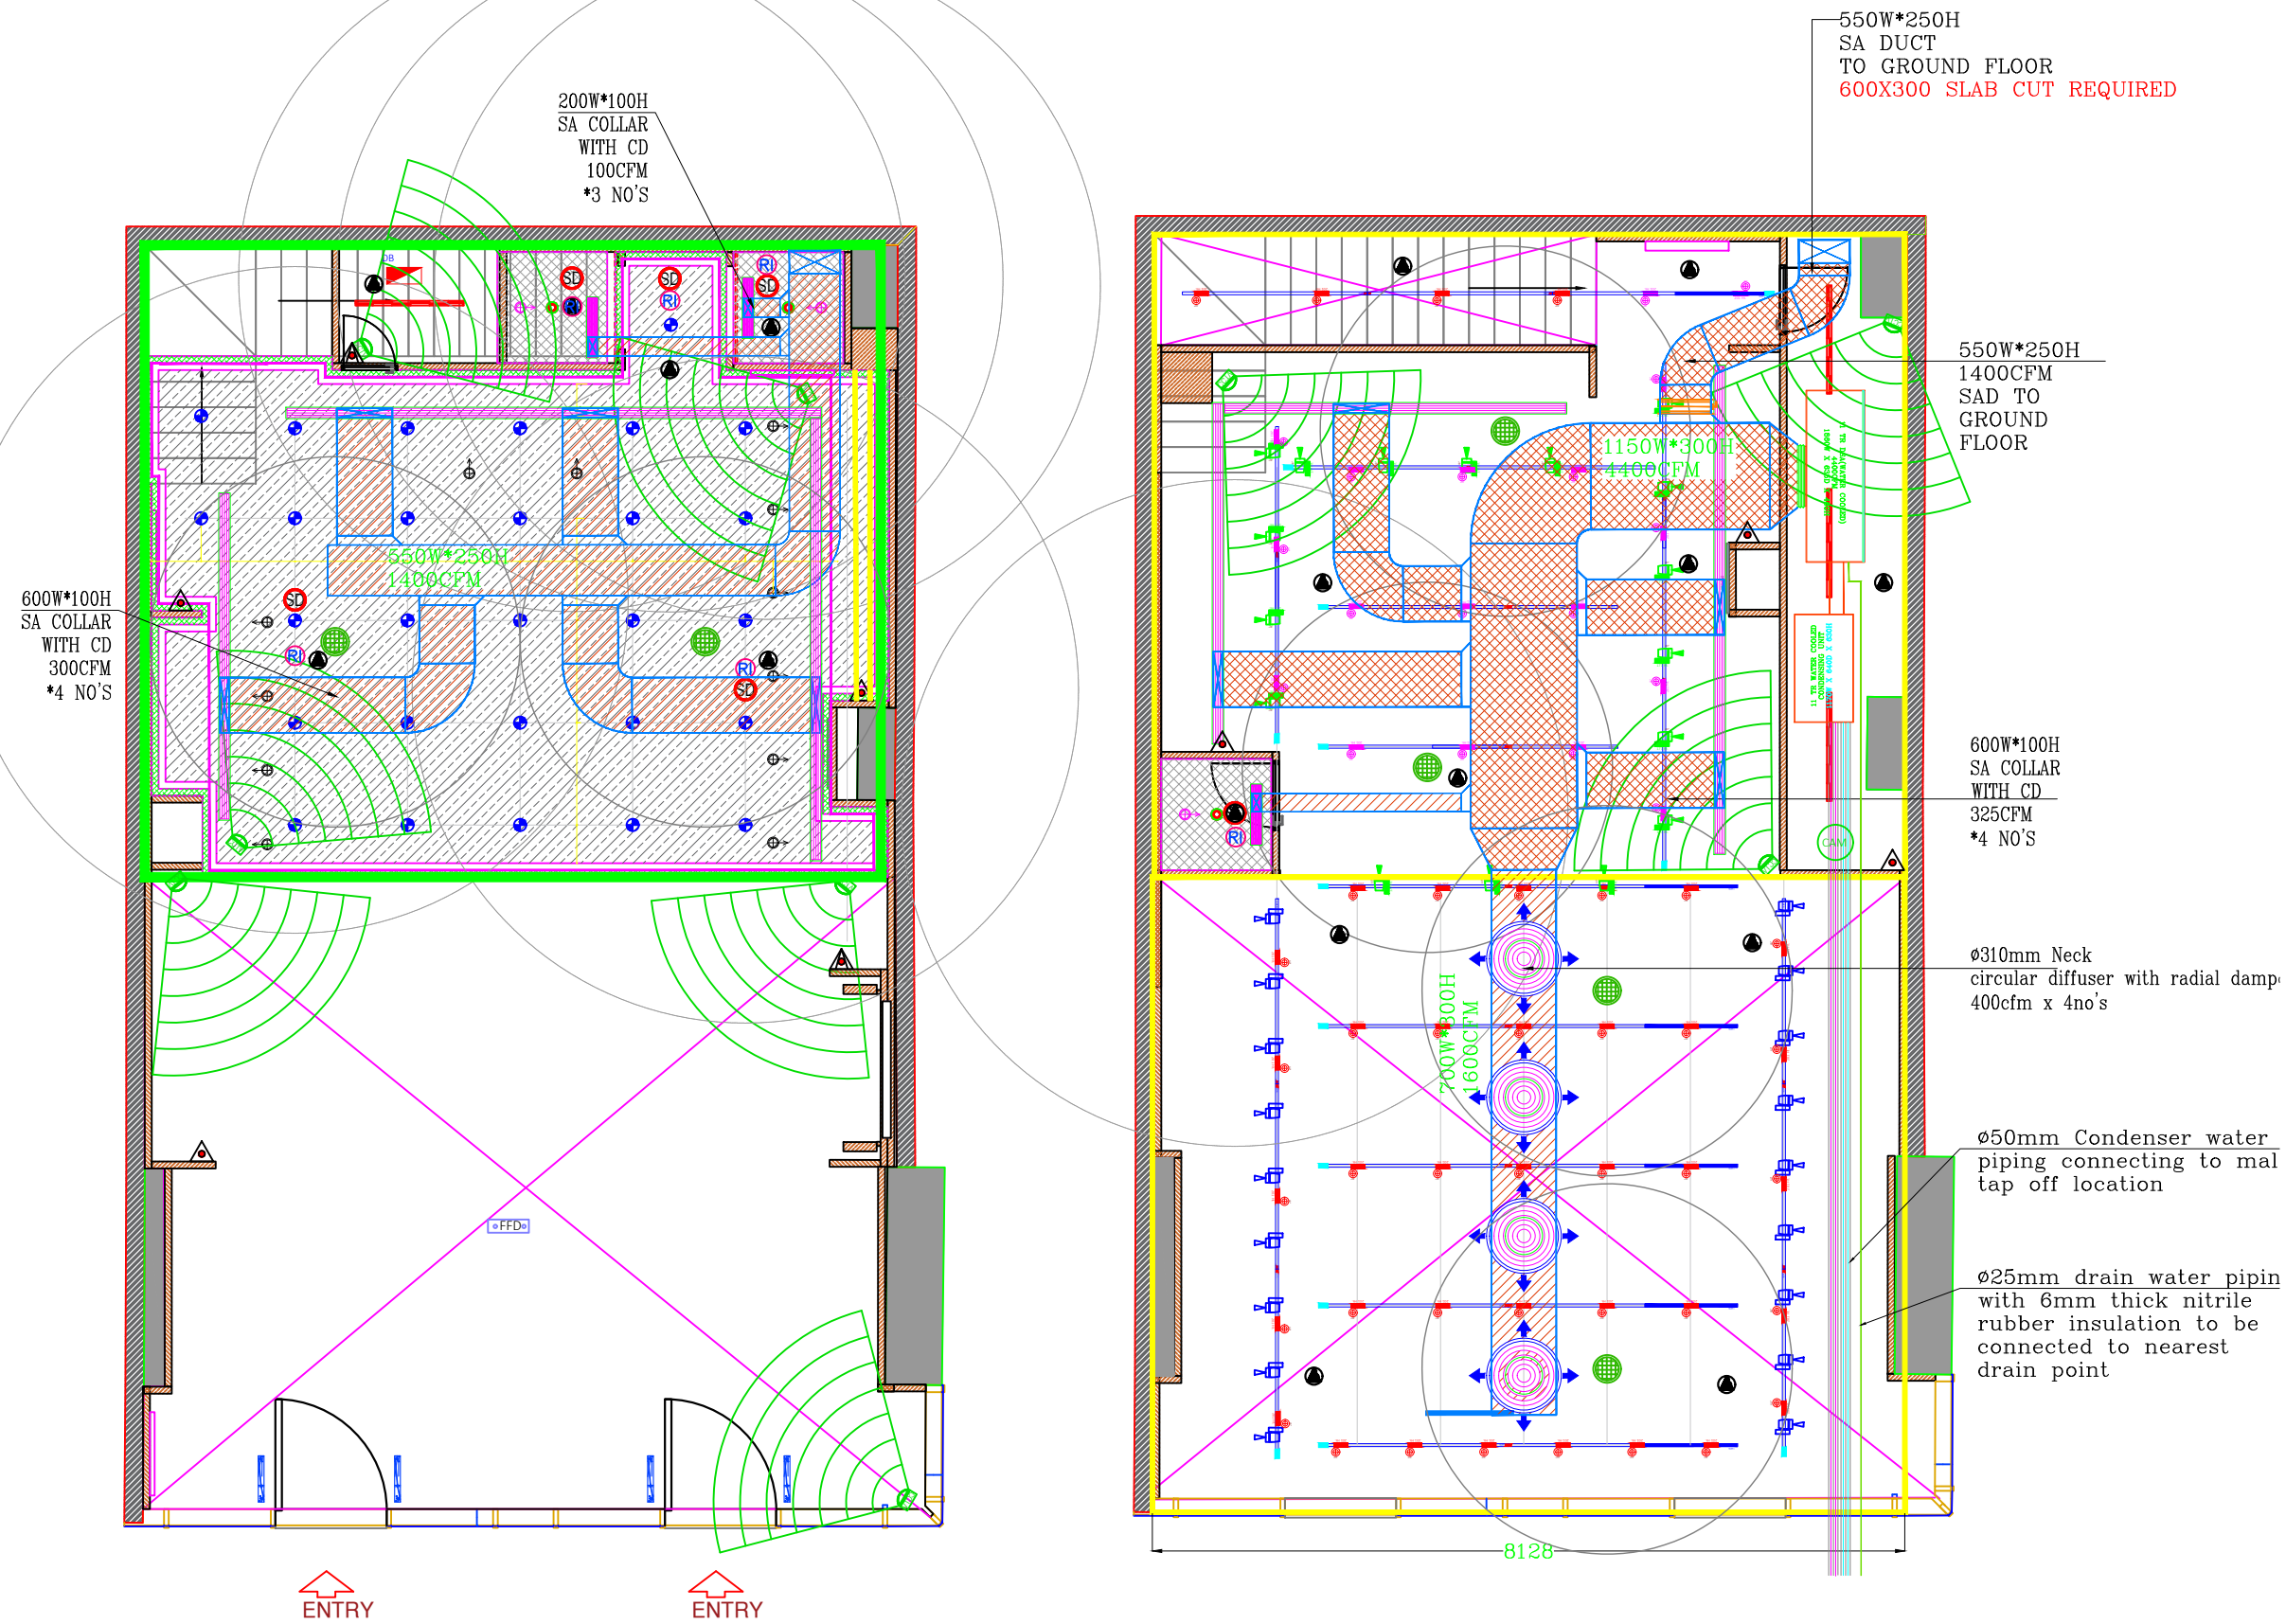

LEGEND :

KEY PLAN :

DRAWING NAME:

RCP LAYOUT

DESIGNED BY:RISHAD

CHECKED BY:AAA

DATE:17-09-2026

REVISION NO:R0

DWG NO:00

DOMORE

DESIGN PVT LTD

DOMORE DESIGN PVT. LTD.

NO.681, SUKHADA, 2ND FLOOR, 2ND PHASE, 2ND BLOCK,

RAILWAY PARALLEL ROAD,

NEAR MALL OF ASIA, BANGALORE, KARNATAKA, 560097

domoredesign.co.in

GENERAL NOTES

- THIS DRAWING IS COPYRIGHT & PROPERTY OF DOMORE DESIGN PVT.LTD. AND IS NOT TO BE REPRODUCED, COPIED OR USED FOR ANY OTHER PURPOSE.
- WRITTEN DIMENSIONS TO BE FOLLOWED.
- DIMENSIONS TO BE CROSS CHECKED PRIOR TO THE COMMENCEMENT OF WORK.
- ALL DRAWINGS TO BE READ IN CONJUNCTION TO THE CONSULTANTS AND VENDORS DRAWINGS/DETAILS.
- FOR ALL LEGENDS, SYMBOLS, ABBREVIATIONS AND ANNOTATIONS RELATED QUERIES, REFER TO REFERENCE SHEET.
- ANY DISCREPANCY OR DOUBT IN DRAWING TO BE BROUGHT TO THE NOTICE OF DOMORE DESIGN PVT.LTD

SCALE : AS MENTIONED

REVISIONS

R01

R02

R03

PROJECT NAME :

M3M PARAGON 57

GURGOAN

COMPASS:

STORE INFO:

STATE

XXX

CITY

GURUGRAM

HIGHSTREET/MALL



M3M PARAGON 57

AREA

1769 SFT

SLAB BOTTOM: 6809MM

BEAM BOTTOM: 6329 MM

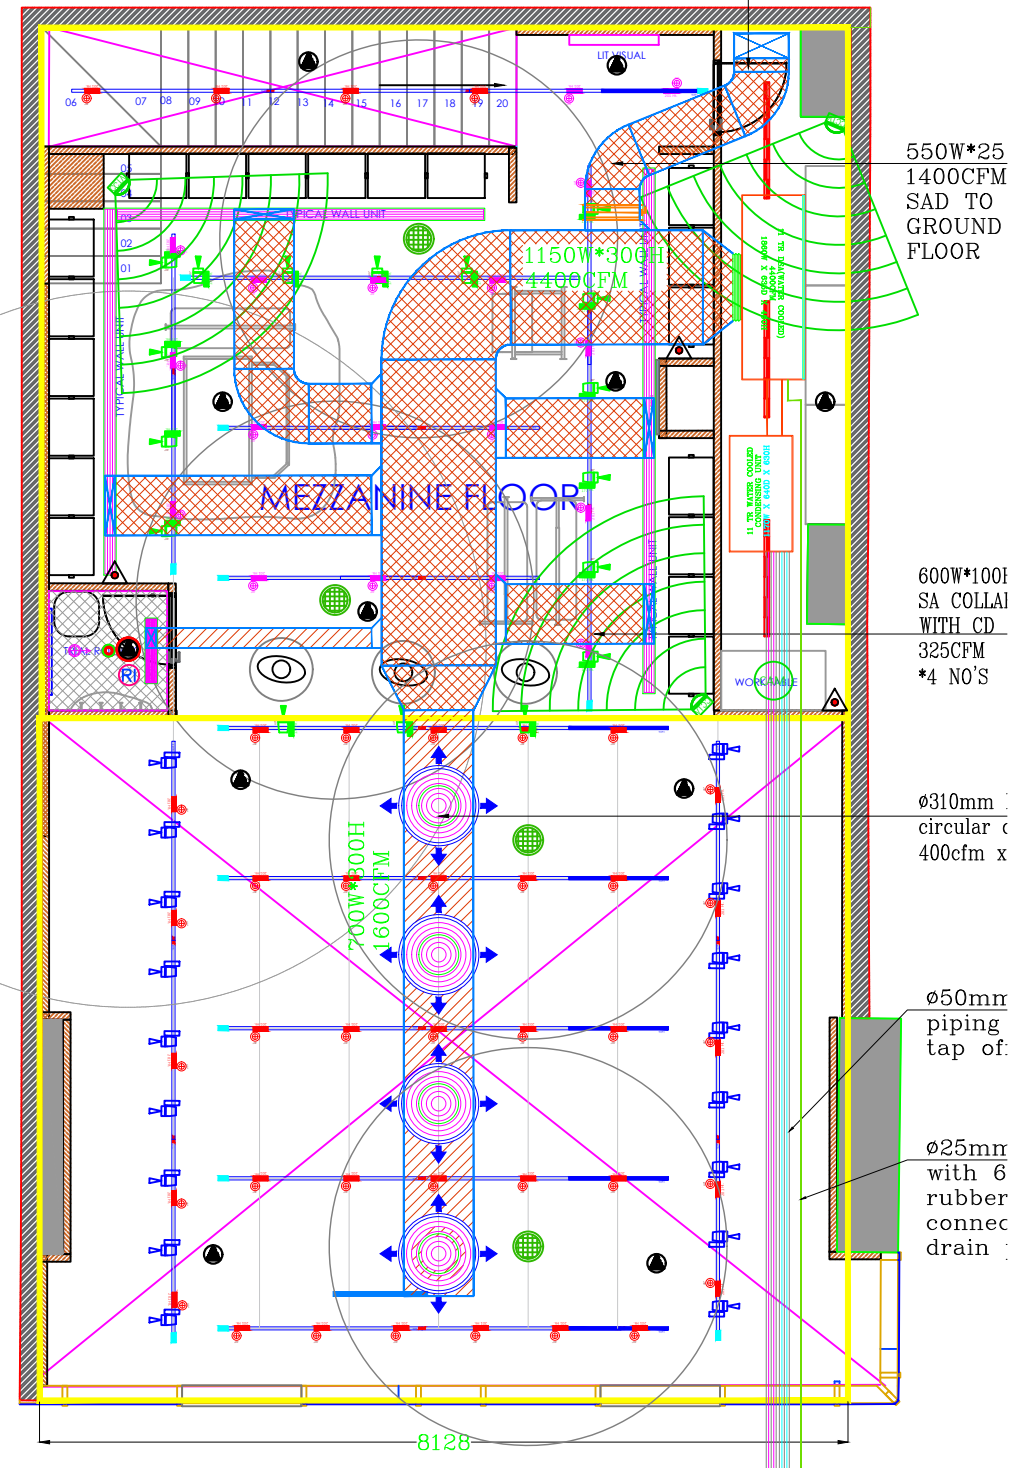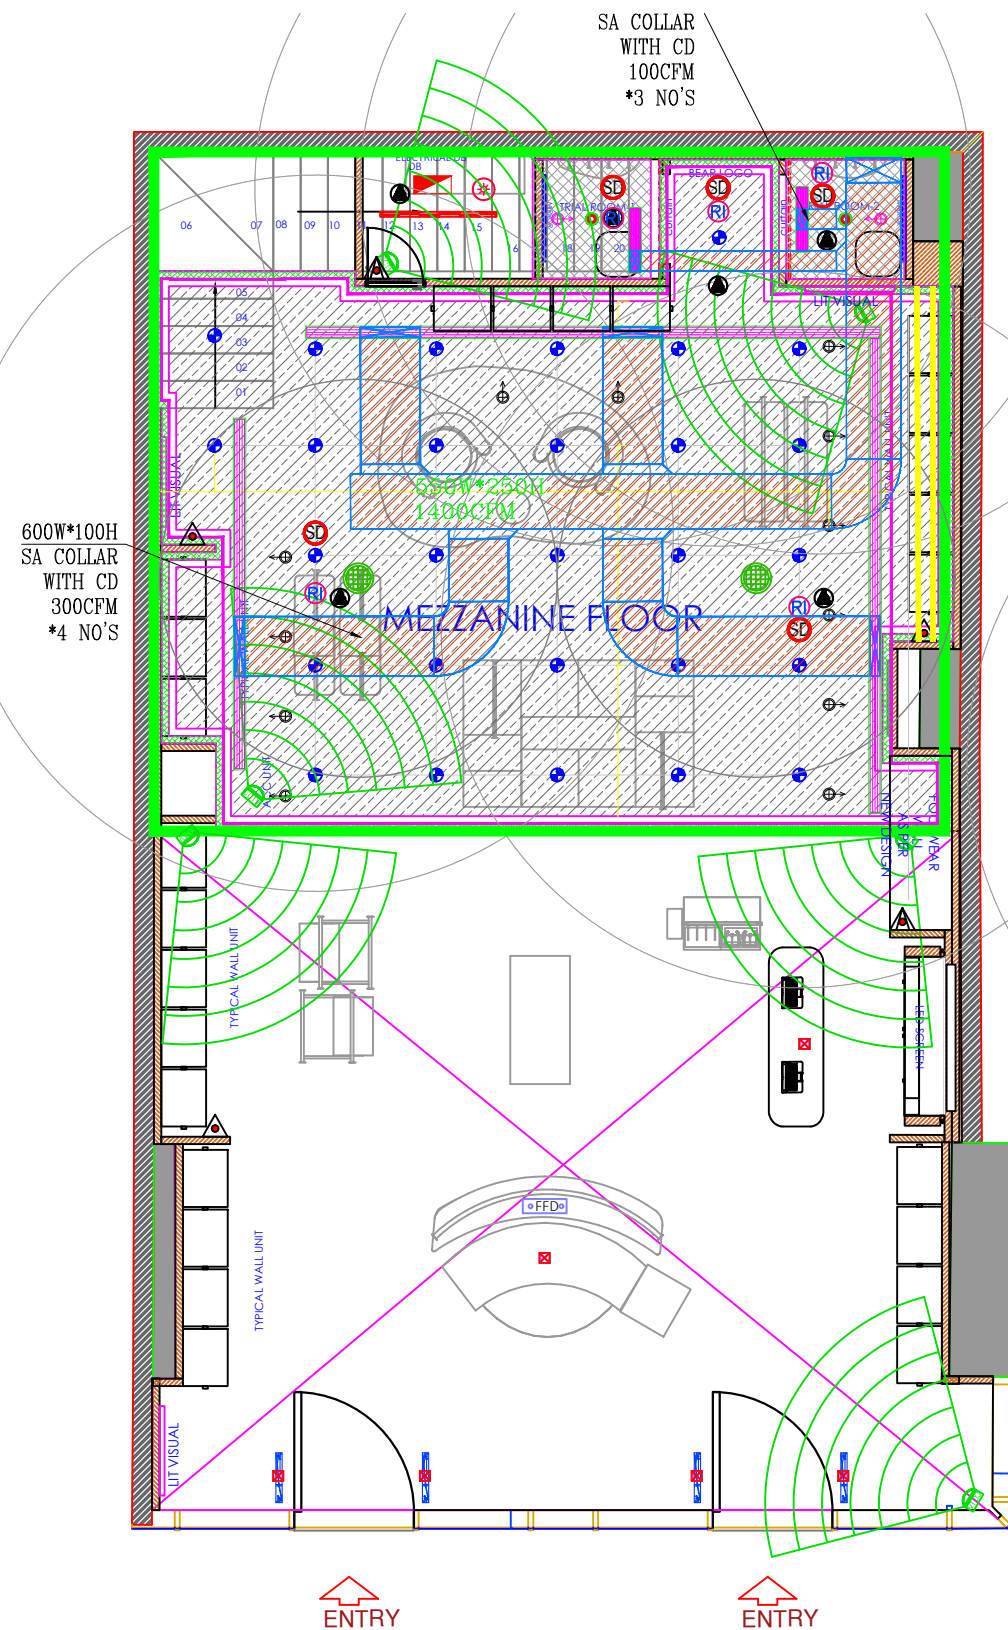

LEGEND :

KEY PLAN :



DOMORE DESIGN PVT. LTD.
NO.681, SUKHADA, 2ND FLOOR, 2ND PHASE, 2ND BLOCK,
RAILWAY PARALLEL ROAD,
NEAR MALL OF ASIA, BANGALORE, KARNATAKA, 560097
domoredesign.co.in

GENERAL NOTES

- THIS DRAWING IS COPYRIGHT & PROPERTY OF DOMORE DESIGN PVT.LTD. AND IS NOT TO BE REPRODUCED, COPIED OR USED FOR ANY OTHER PURPOSE.
- WRITTEN DIMENSIONS TO BE FOLLOWED.
- DIMENSIONS TO BE CROSS CHECKED PRIOR TO THE COMMENCEMENT OF WORK.
- ALL DRAWINGS TO BE READ IN CONJUNCTION TO THE CONSULTANTS AND VENDORS DRAWINGS/DETAILS.
- FOR ALL LEGENDS, SYMBOLS, ABBREVIATIONS AND ANNOTATIONS RELATED QUERIES, REFER TO REFERENCE SHEET.
- ANY DISCREPANCY OR DOUBT IN DRAWING TO BE BROUGHT TO THE NOTICE OF DOMORE DESIGN PVT.LTD.

SCALE : AS MENTIONED


REVISIONS

R01
R02
R03

PROJECT NAME :

M3M PARAGON 57
GURGOAN

COMPASS:

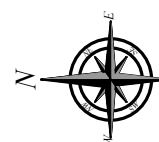

STORE INFO:


STATE	XXX
CITY	GURUGRAM
HIGHSTREET/MALL	M3M PARAGON 57
AREA	1769 SFT
SLAB BOTTOM: 6809MM	BEAM BOTTOM: 6329 MM

DRAWING NAME:


RCP W/O LAYOUT

DESIGNED BY:	CHECKED BY:	
RISHAD	AAA	
DATE:	REVISION NO:	DWG NO:
17-09-2026	R0	00

GROUND FLOOR

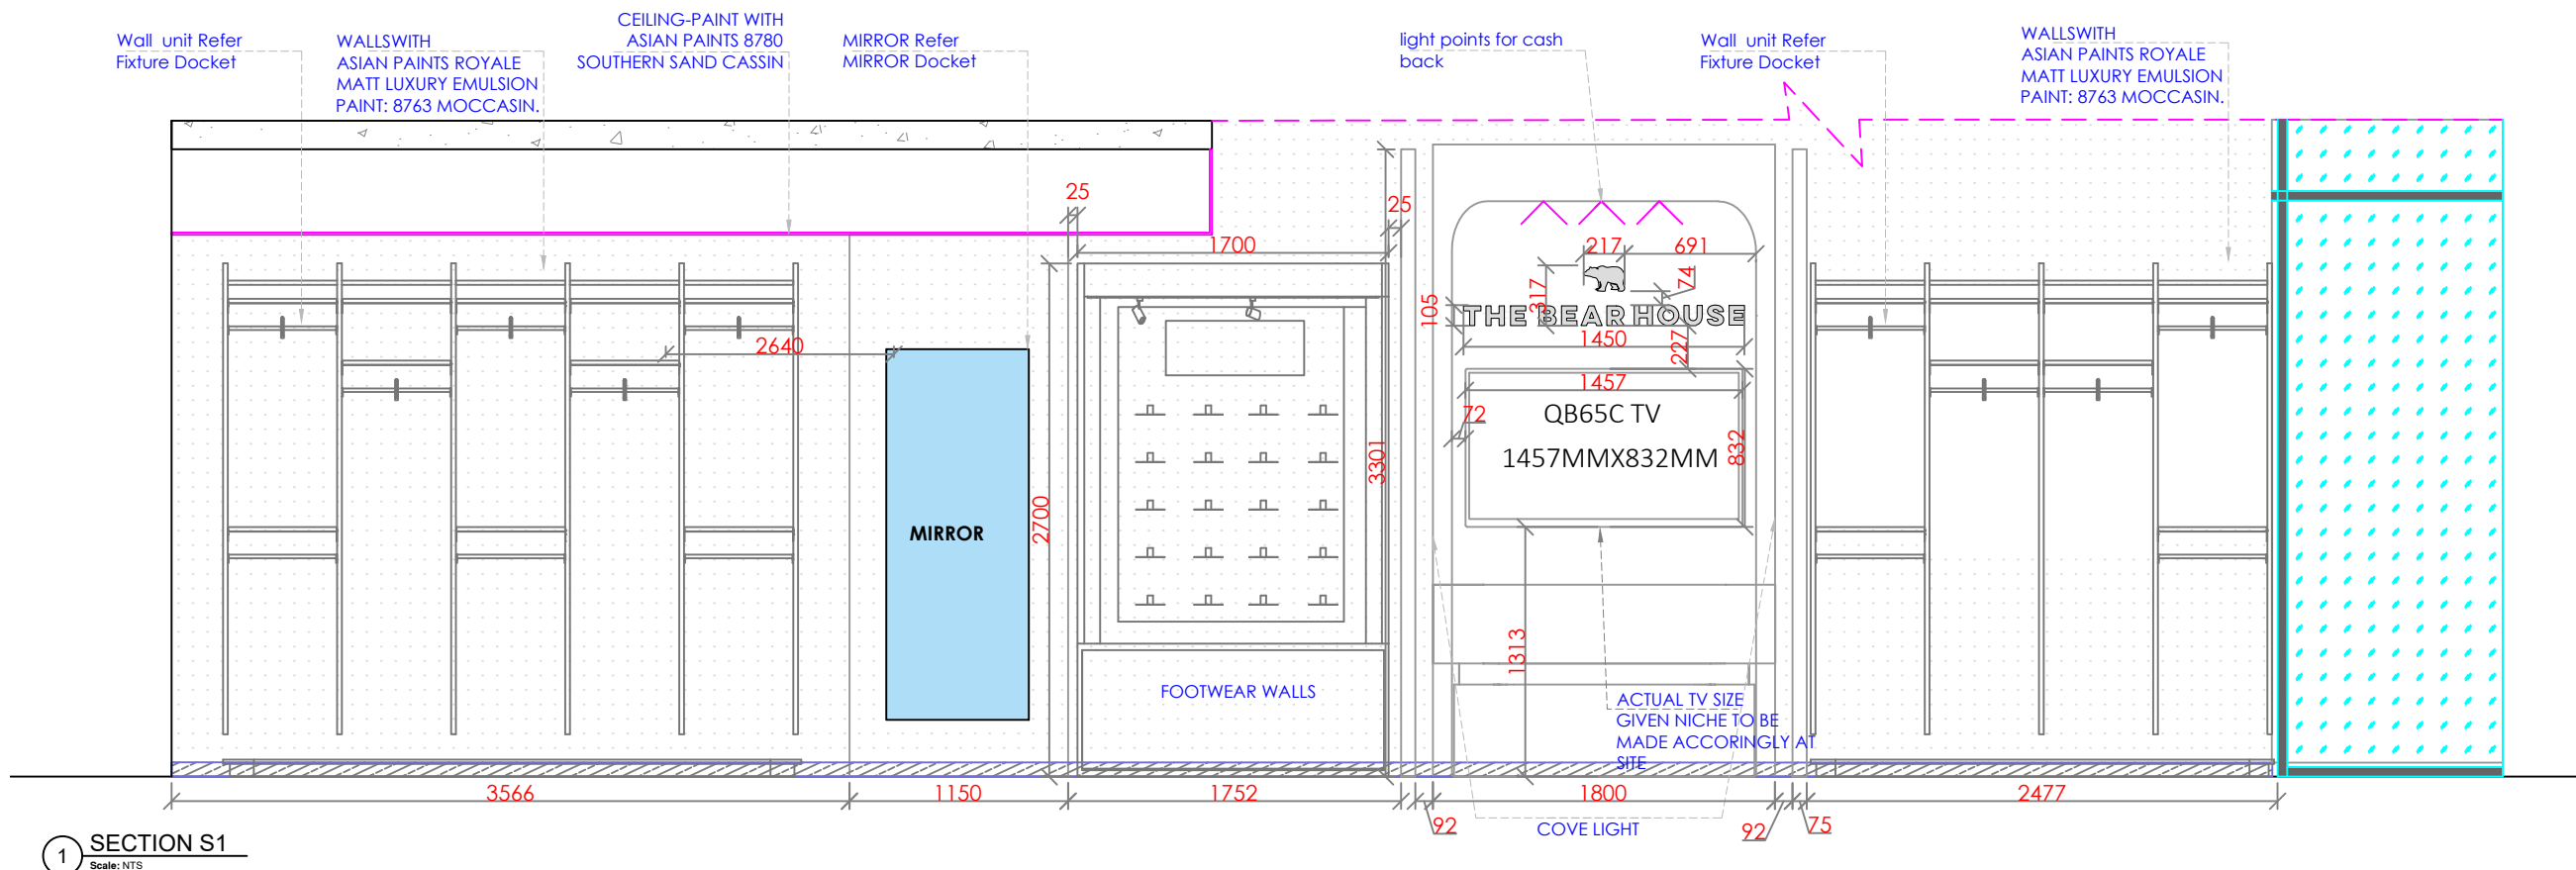

1 **SECTION S1**
Scale: NTS

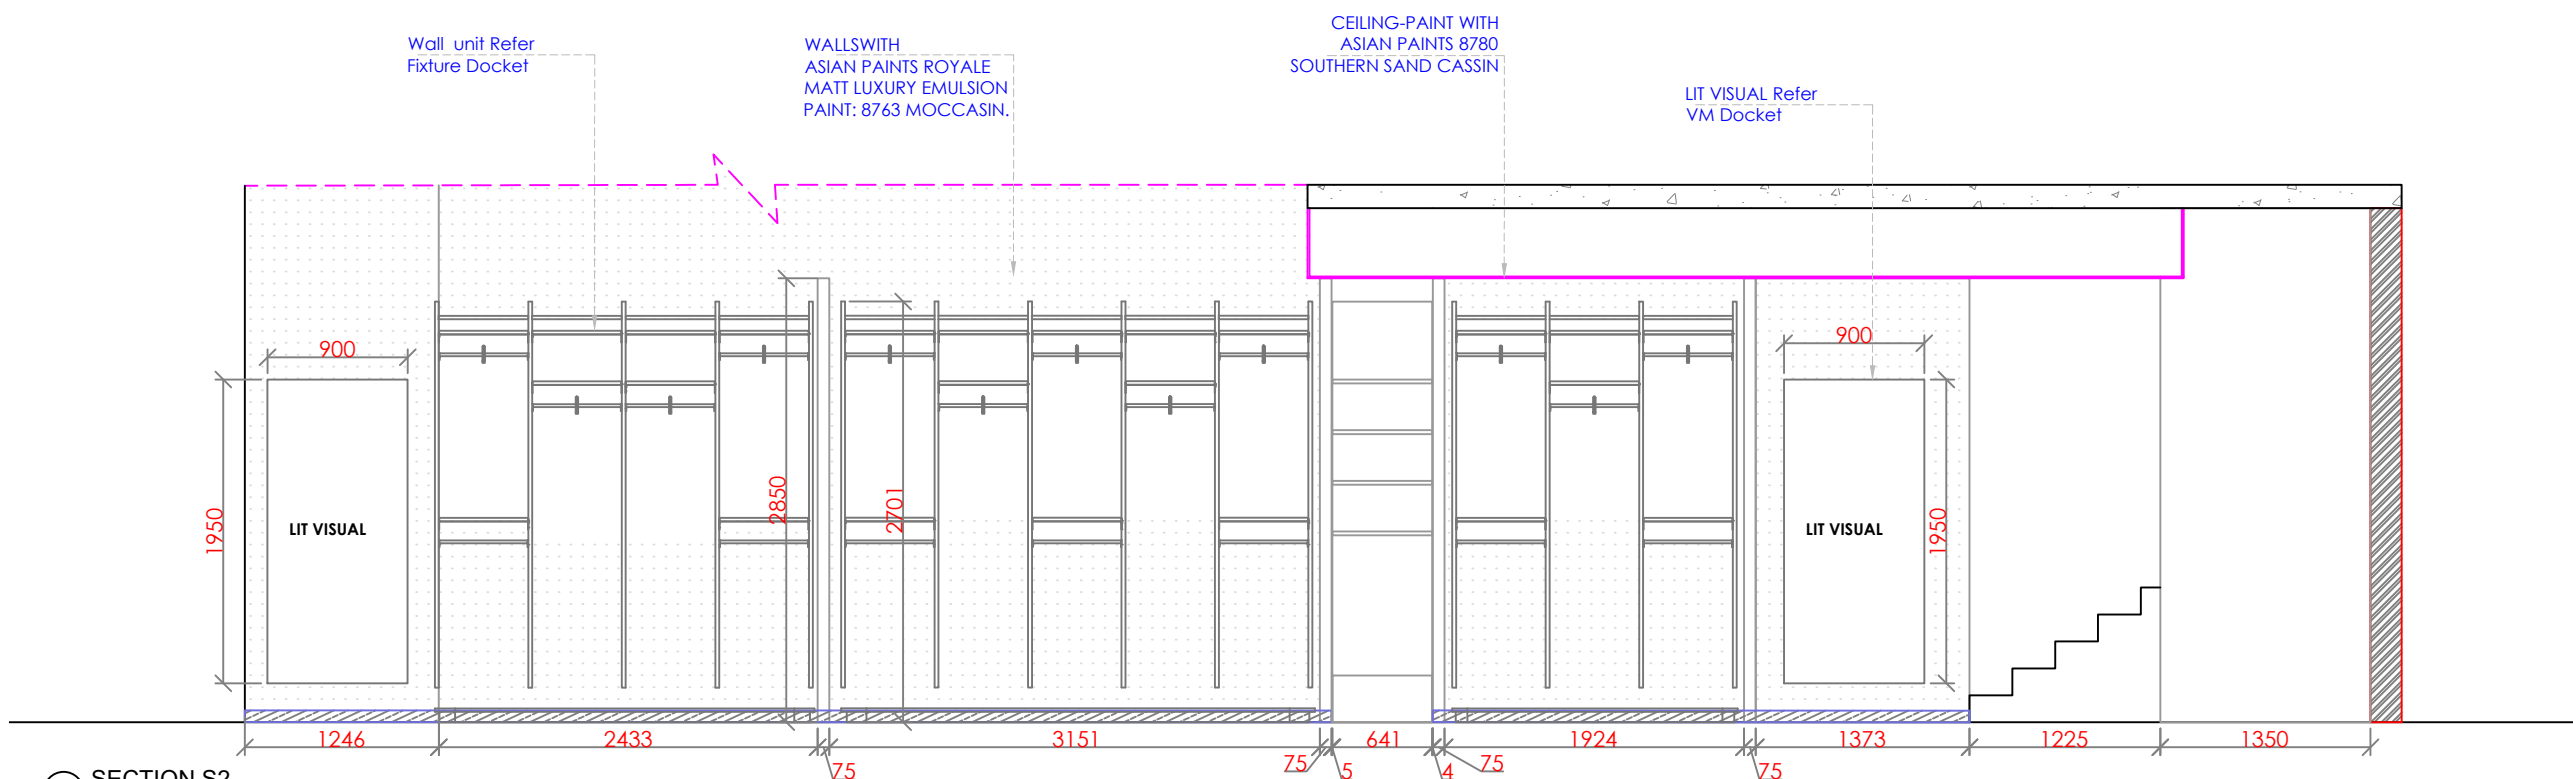


2 SECTION S2

NOTE : ALL WALL SHELVES TO BE LIT

LEGEND :

KEY PLAN :

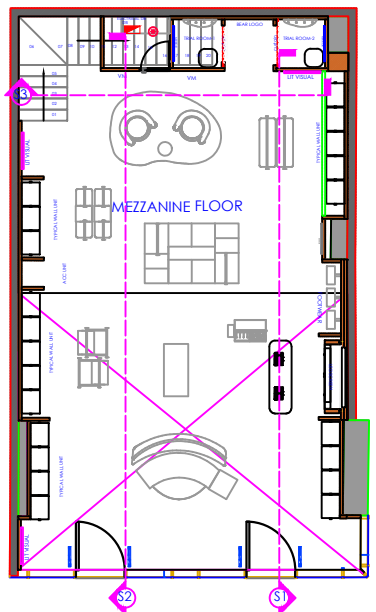

DRAWING NAME:

ELEVATION

DESIGNED BY:	CHECKED BY:	
RISHAD	AAA	
DATE:	REVISION NO:	DWG NO:
17-09-2026	R0	00



DOMORE DESIGN PVT. LTD.
NO.681, SUKHADA, 2ND FLOOR, 2ND PHASE, 2ND BLOCK,
RAILWAY PARALLEL ROAD,
NEAR MALL OF ASIA, BANGALORE, KARNATAKA, 560097
domoredesign.co.in

GENERAL NOTES

- THIS DRAWING IS COPYRIGHT & PROPERTY OF DOMORE DESIGN PVT.LTD. AND IS NOT TO BE REPRODUCED, COPIED OR USED FOR ANY OTHER PURPOSE.
- WRITTEN DIMENSIONS TO BE FOLLOWED.
- DIMENSIONS TO BE CROSS CHECKED PRIOR TO THE COMMENCEMENT OF WORK.
- ALL DRAWINGS TO BE READ IN CONJUNCTION TO THE CONSULTANTS AND VENDORS DRAWINGS/DETAILS.
- FOR ALL LEGENDS, SYMBOLS, ABBREVIATIONS AND ANNOTATIONS RELATED QUERIES, REFER TO REFERENCE SHEET.
- ANY DISCREPANCY OR DOUBT IN DRAWING TO BE BROUGHT TO THE NOTICE OF DOMORE DESIGN PVT.LTD

SCALE : AS MENTIONED


REVISIONS

R01
R02
R03

PROJECT NAME :

M3M PARAGON 57
GURGOAN

COMPASS:

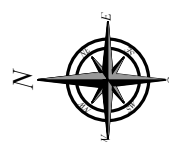


STORE INFO:

STATE	XXX	
CITY	GURUGRAM	
HIGHSTREET/MALL	M3M PARAGON 57	
AREA	1769 SFT	
SLAB BOTTOM: 6809MM		BEAM BOTTOM: 6329 MM

DRAWING NAME:

GROUND FLOOR

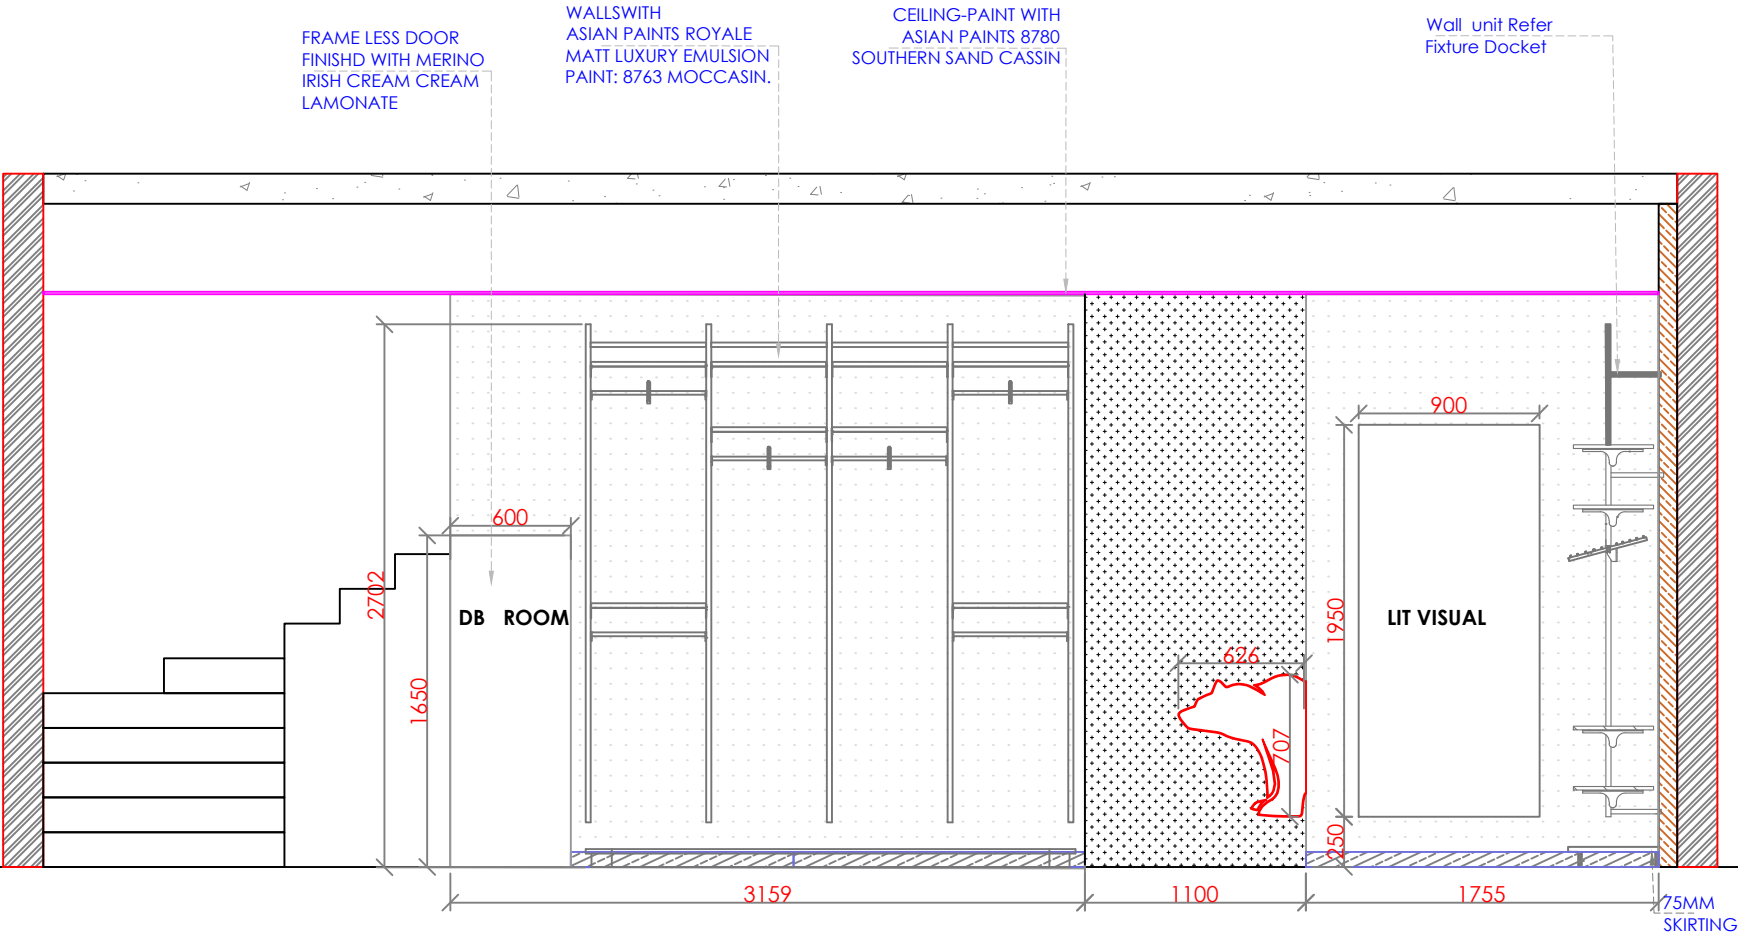


3 SECTION S3
Scale: NTS

NOTE : ALL WALL SHELVES TO BE LIT

LEGEND :

KEY PLAN :

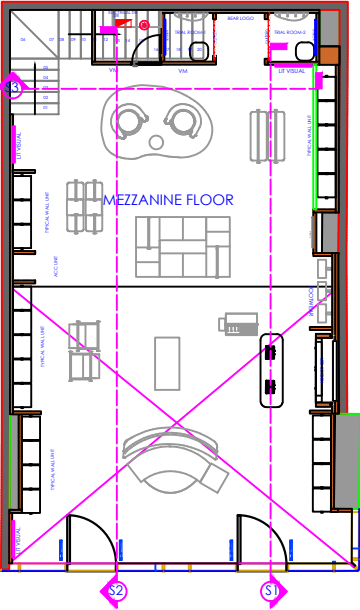

DOMORE DESIGN PVT. LTD.
NO.681, SUKHADA, 2ND FLOOR, 2ND PHASE, 2ND BLOCK,
RAILWAY PARALLEL ROAD,
NEAR MALL OF ASIA, BANGALORE, KARNATAKA, 560097
domoredesign.co.in

GENERAL NOTES

- THIS DRAWING IS COPYRIGHT & PROPERTY OF DOMORE DESIGN PVT.LTD. AND IS NOT TO BE REPRODUCED, COPIED OR USED FOR ANY OTHER PURPOSE.
- WRITTEN DIMENSIONS TO BE FOLLOWED.
- DIMENSIONS TO BE CROSS CHECKED PRIOR TO THE COMMENCEMENT OF WORK.
- ALL DRAWINGS TO BE READ IN CONJUNCTION TO THE CONSULTANTS AND VENDORS DRAWINGS/DETAILS.
- FOR ALL LEGENDS, SYMBOLS, ABBREVIATIONS AND ANNOTATIONS RELATED QUERIES, REFER TO REFERENCE SHEET.
- ANY DISCREPANCY OR DOUBT IN DRAWING TO BE BROUGHT TO THE NOTICE OF DOMORE DESIGN PVT.LTD

SCALE : AS MENTIONED


REVISIONS

R01
R02
R03

PROJECT NAME :

M3M PARAGON 57
GURGOAN

COMPASS:

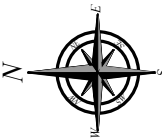



STORE INFO:

STATE	XXX
CITY	GURUGRAM
HIGHSTREET/MALL	M3M PARAGON 57
AREA	1769 SFT
SLAB BOTTOM: 6809MM	BEAM BOTTOM: 6329 MM

DRAWING NAME:


ELEVATION

DESIGNED BY:	CHECKED BY:	
RISHAD	AAA	
DATE:	REVISION NO:	DWG NO:
17-09-2026	R0	00

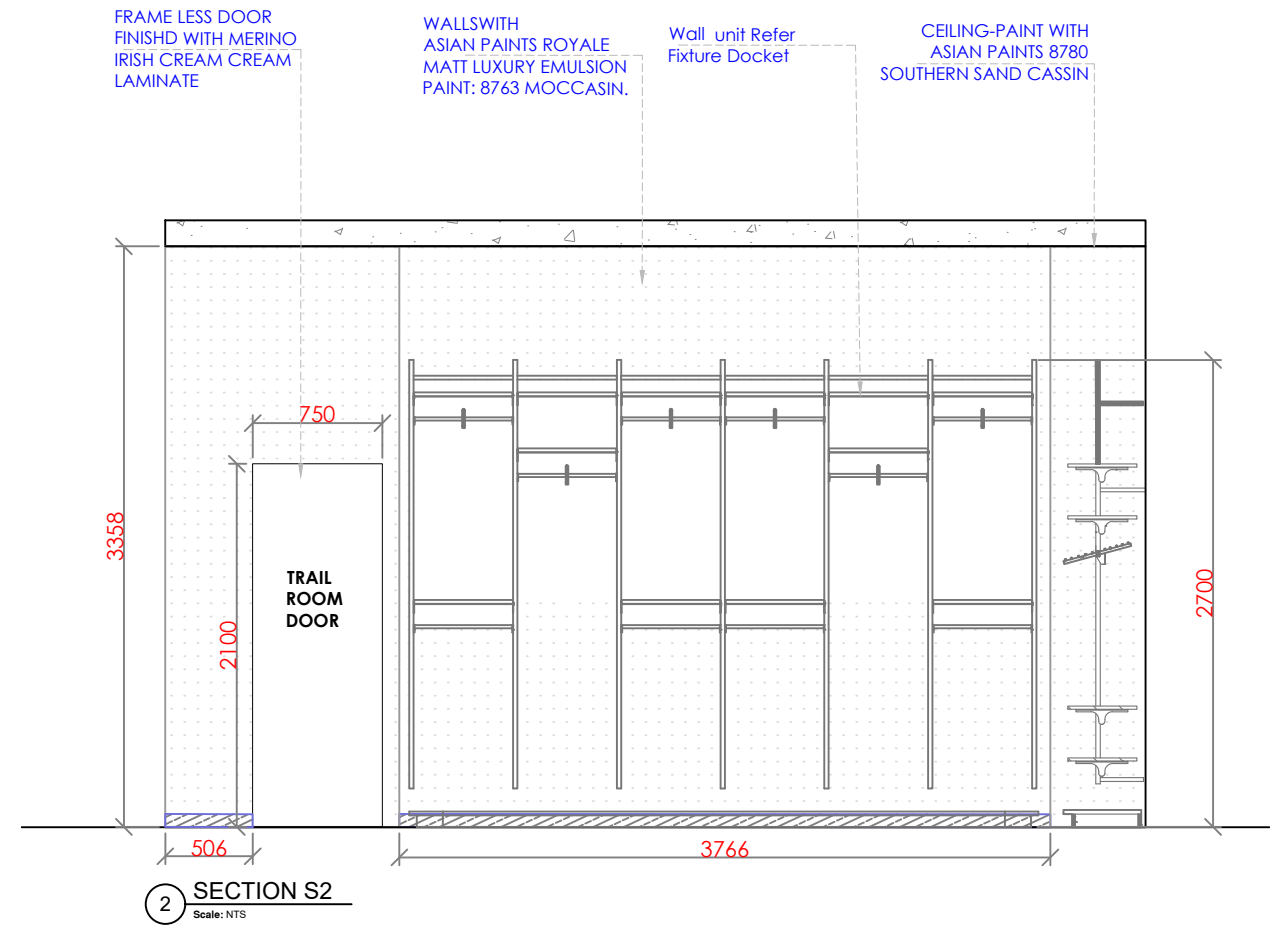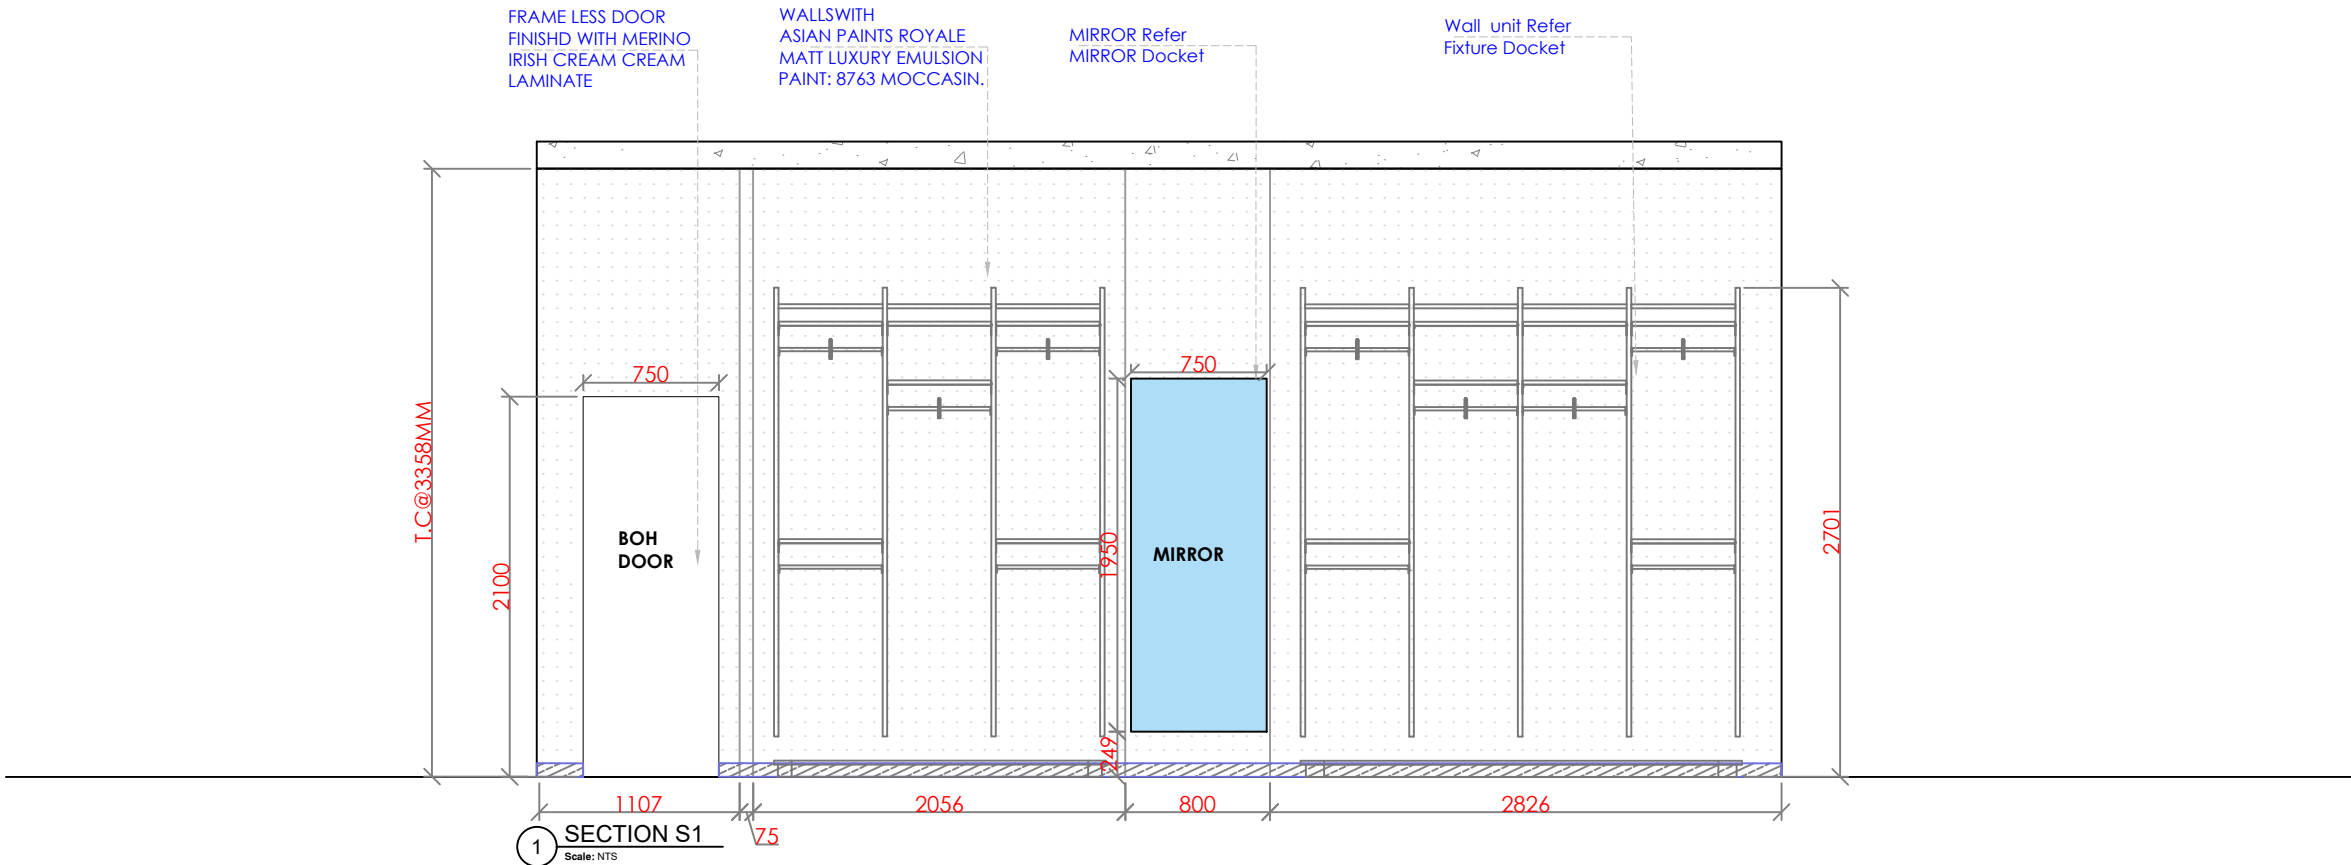

NOTE : ALL WALL SHELVES TO BE LIT

LEGEND :

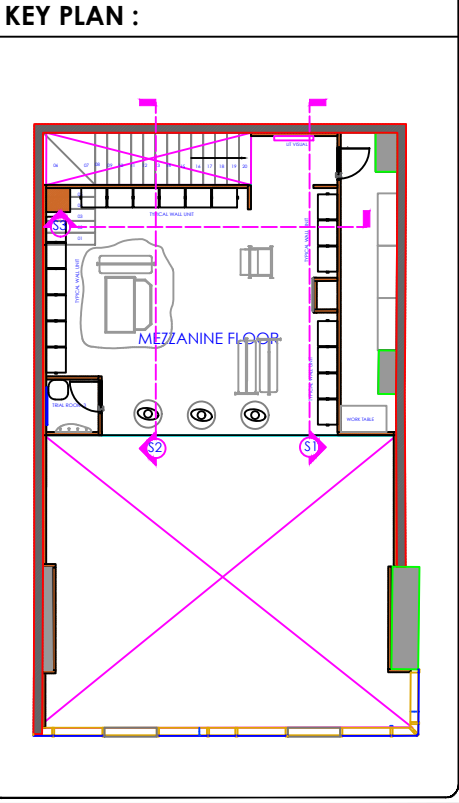

DOMORE
DESIGN PVT LTD

DOMORE DESIGN PVT. LTD.
NO.681, SUKHADA, 2ND FLOOR, 2ND PHASE, 2ND BLOCK,
RAILWAY PARALLEL ROAD,
NEAR MALL OF ASIA, BANGALORE, KARNATAKA, 560097
domoredesign.co.in

GENERAL NOTES

- THIS DRAWING IS COPYRIGHT & PROPERTY OF DOMORE DESIGN PVT.LTD, AND IS NOT TO BE REPRODUCED, COPIED OR USED FOR ANY OTHER PURPOSE.
- WRITTEN DIMENSIONS TO BE FOLLOWED.
- DIMENSIONS TO BE CROSS CHECKED PRIOR TO THE COMMENCEMENT OF WORK.
- ALL DRAWINGS TO BE READ IN CONJUNCTION TO THE CONSULTANTS AND VENDORS DRAWINGS/DETAILS.
- FOR ALL LEGENDS, SYMBOLS, ABBREVIATIONS AND ANNOTATIONS RELATED QUERIES, REFER TO REFERENCE SHEET.
- ANY DISCREPANCY OR DOUBT IN DRAWING TO BE BROUGHT TO THE NOTICE OF DOMORE DESIGN PVT.LTD

SCALE : AS MENTIONED

REVISIONS
R01
R02
R03


PROJECT NAME :

M3M PARAGON 57
GURGOAN

COMPASS:

STORE INFO:	
STATE	XXX
CITY	GURUGRAM
HIGHSTREET/MALL	M3M PARAGON 57
AREA	1769 SFT
SLAB BOTTOM: 6809MM	BEAM BOTTOM: 6329 MM


DRAWING NAME:		
ELEVATION		
DESIGNED BY:	CHECKED BY:	
RISHAD	AAA	
DATE:	REVISION NO:	DWG NO:
17-09-2026	R0	00

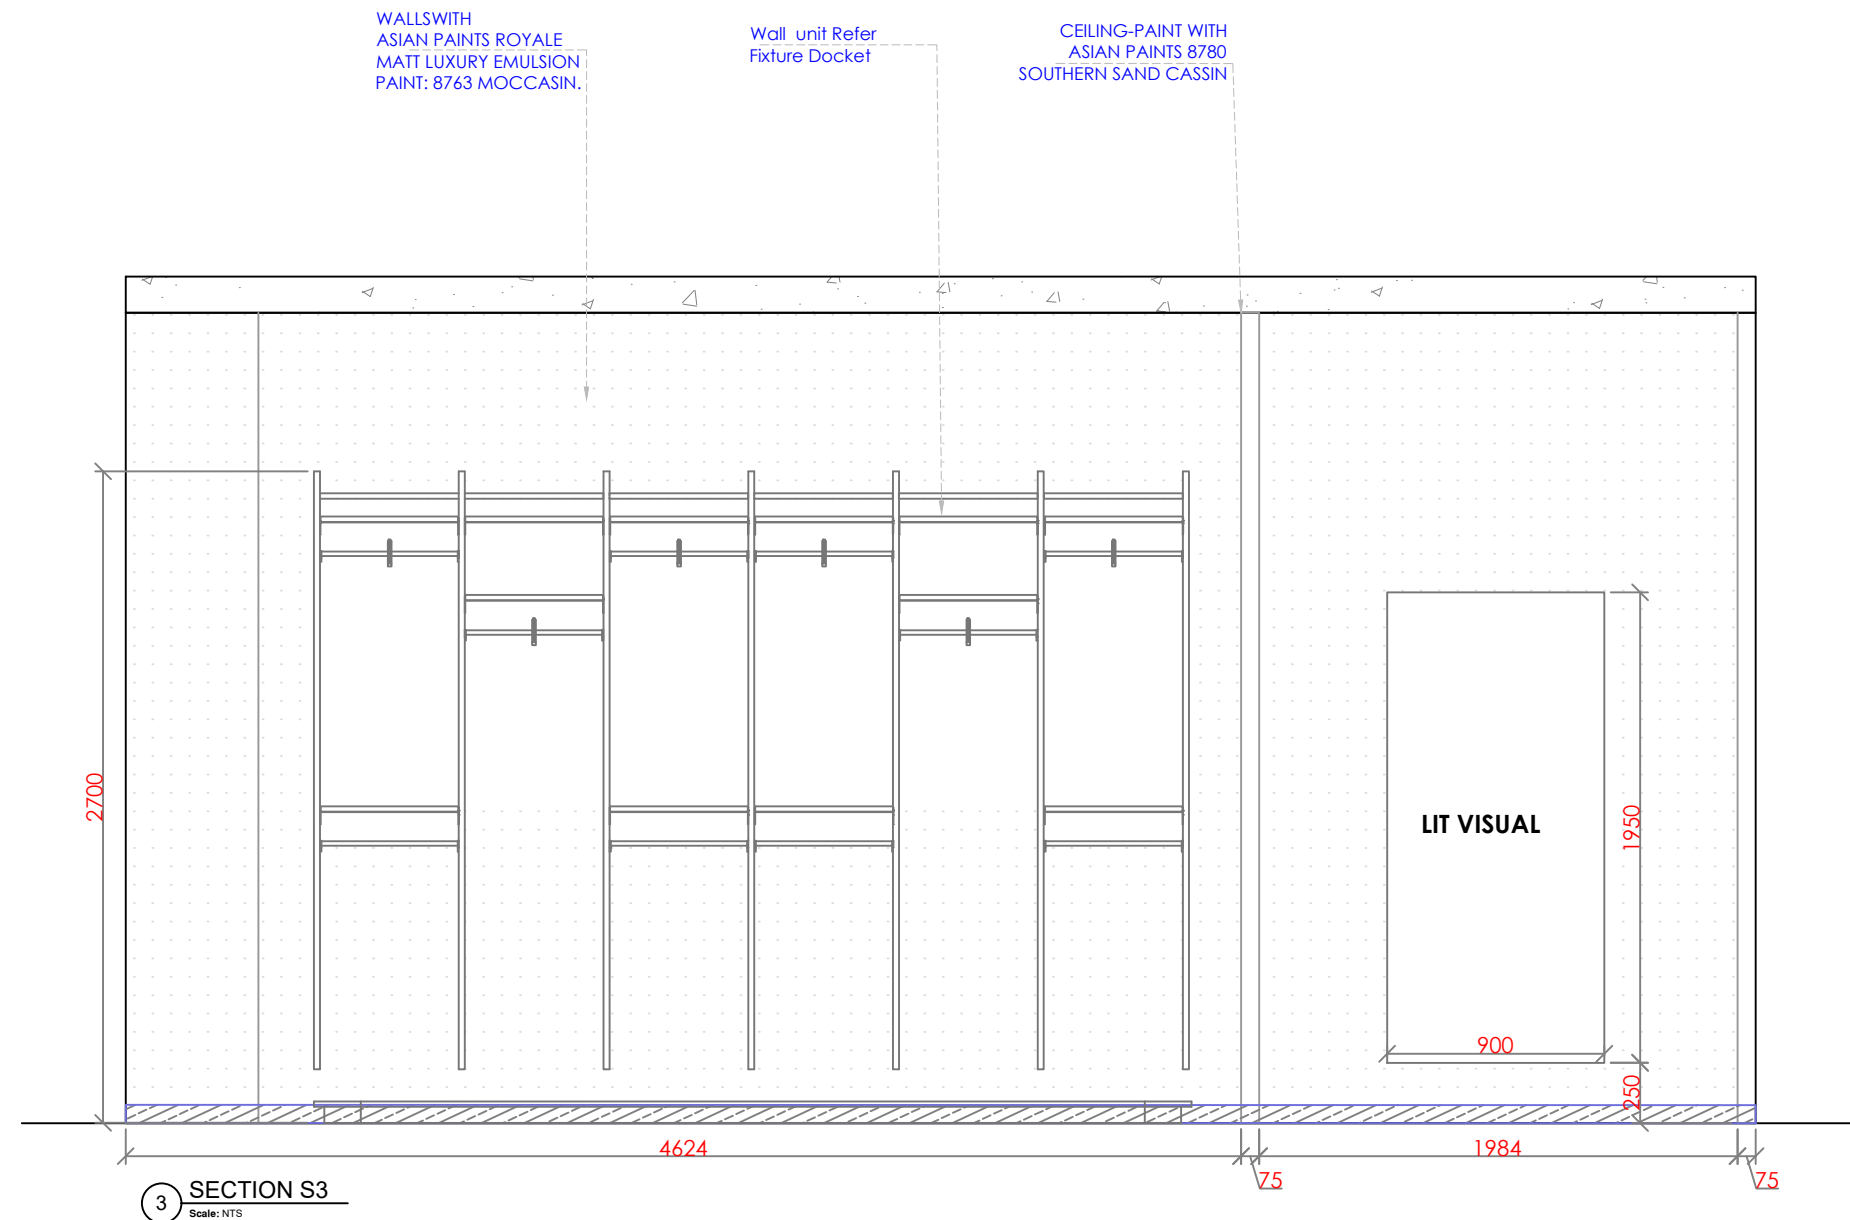

NOTE : ALL WALL SHELVES TO BE LIT

LEGEND :

KEY PLAN :

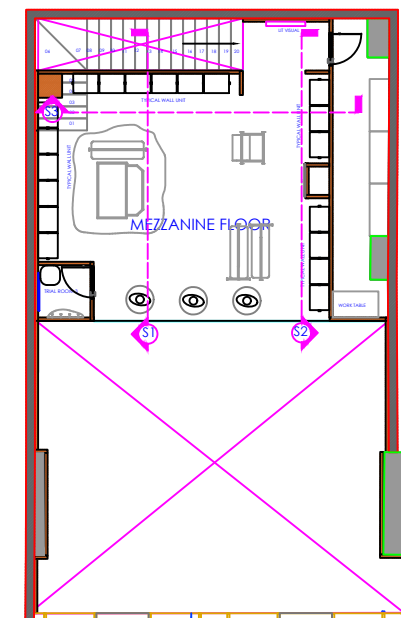

DOMORE
DESIGN PVT LTD

DOMORE DESIGN PVT. LTD.
NO.681, SUKHADA, 2ND FLOOR, 2ND PHASE, 2ND BLOCK,
RAILWAY PARALLEL ROAD,
NEAR MALL OF ASIA, BANGALORE, KARNATAKA, 560097
domoredesign.co.in

GENERAL NOTES

- THIS DRAWING IS COPYRIGHT & PROPERTY OF DOMORE DESIGN PVT.LTD. AND IS NOT TO BE REPRODUCED, COPIED OR USED FOR ANY OTHER PURPOSE.
- WRITTEN DIMENSIONS TO BE FOLLOWED.
- DIMENSIONS TO BE CROSS CHECKED PRIOR TO THE COMMENCEMENT OF WORK.
- ALL DRAWINGS TO BE READ IN CONJUNCTION TO THE CONSULTANTS AND VENDORS DRAWINGS/DETAILS.
- FOR ALL LEGENDS, SYMBOLS, ABBREVIATIONS AND ANNOTATIONS RELATED QUERIES, REFER TO REFERENCE SHEET.
- ANY DISCREPANCY OR DOUBT IN DRAWING TO BE BROUGHT TO THE NOTICE OF DOMORE DESIGN PVT.LTD

SCALE : AS MENTIONED

REVISIONS
R01
R02
R03



PROJECT NAME :

M3M PARAGON 57
GURGOAN

COMPASS:


STORE INFO:	
STATE	XXX
CITY	GURUGRAM
HIGHSTREET/MALL	M3M PARAGON 57
AREA	1769 SFT
SLAB BOTTOM: 6809MM	BEAM BOTTOM: 6329 MM

DRAWING NAME:		
ELEVATION		
DESIGNED BY:	CHECKED BY:	
RISHAD	AAA	
DATE:	REVISION NO:	DWG NO:
17-09-2026	R0	00

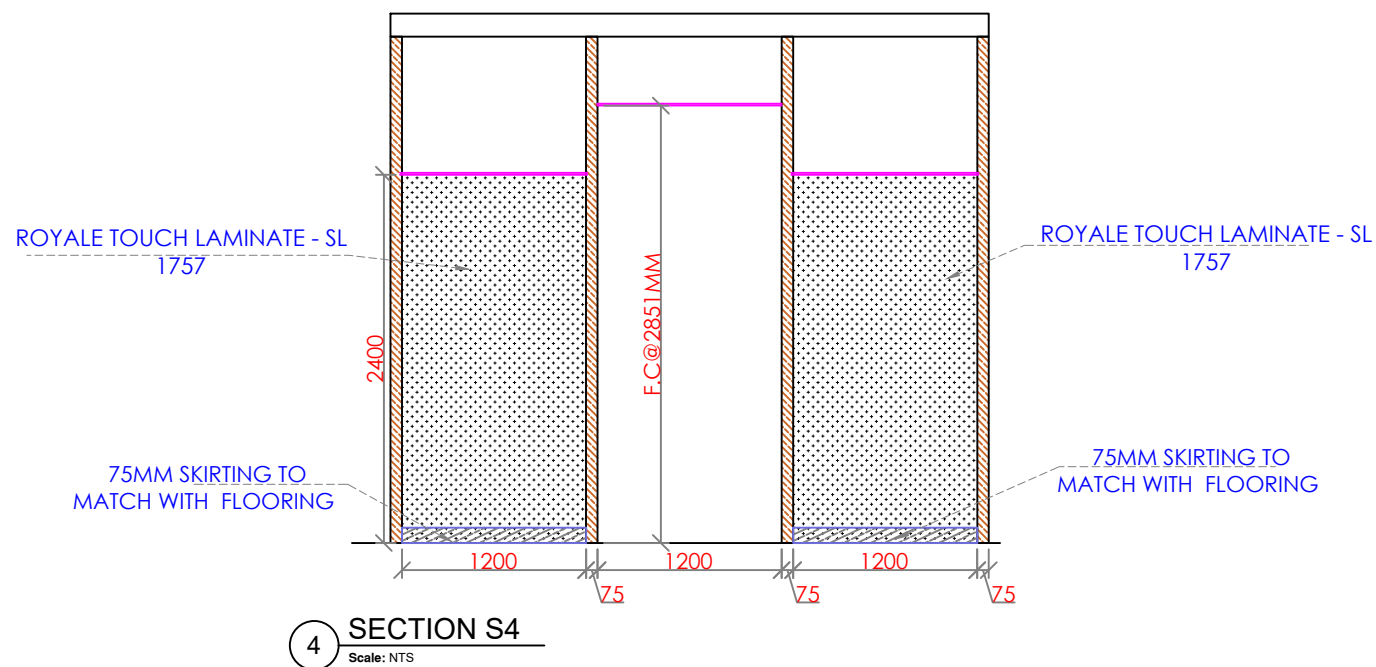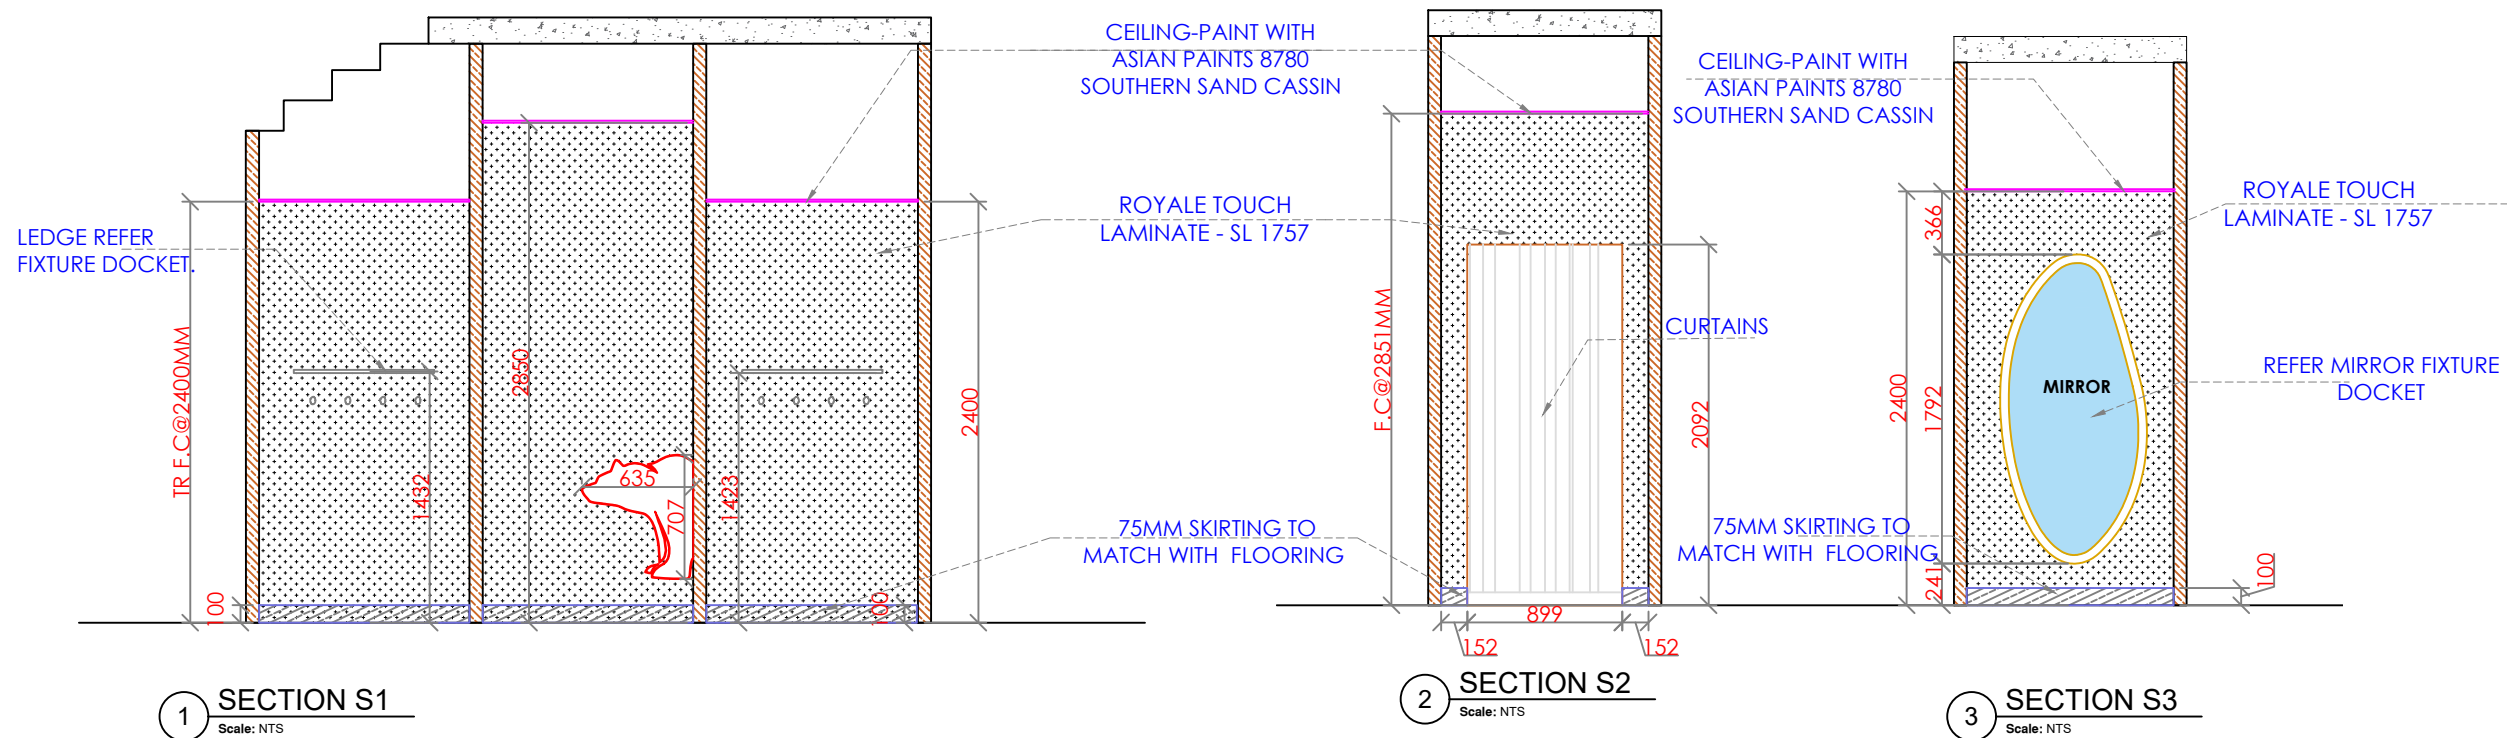

LEGEND :

KEY PLAN :

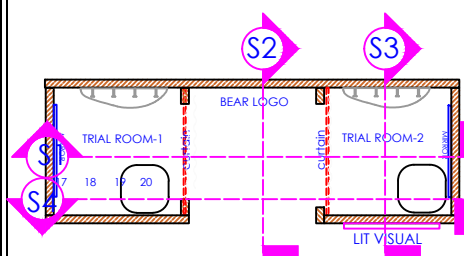

DOMORE DESIGN PVT. LTD.
NO.681, SUKHADA, 2ND FLOOR, 2ND PHASE, 2ND BLOCK,
RAILWAY PARALLEL ROAD,
NEAR MALL OF ASIA, BANGALORE, KARNATAKA, 560097
domoredesign.co.in

GENERAL NOTES

- THIS DRAWING IS COPYRIGHT & PROPERTY OF DOMORE DESIGN PVT.LTD. AND IS NOT TO BE REPRODUCED, COPIED OR USED FOR ANY OTHER PURPOSE.
- WRITTEN DIMENSIONS TO BE FOLLOWED.
- DIMENSIONS TO BE CROSS CHECKED PRIOR TO THE COMMENCEMENT OF WORK.
- ALL DRAWINGS TO BE READ IN CONJUNCTION TO THE CONSULTANTS AND VENDORS DRAWINGS/DETAILS.
- FOR ALL LEGENDS, SYMBOLS, ABBREVIATIONS AND ANNOTATIONS RELATED QUERIES, REFER TO REFERENCE SHEET.
- ANY DISCREPANCY OR DOUBT IN DRAWING TO BE BROUGHT TO THE NOTICE OF DOMORE DESIGN PVT.LTD

SCALE : AS MENTIONED


REVISIONS

R01
R02
R03

PROJECT NAME :

M3M PARAGON 57
GURGOAN

COMPASS:

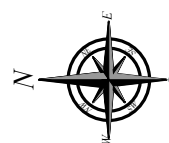


STORE INFO:

STATE	XXX
CITY	XXX
HIGHSTREET/MALL	XXX
AREA	SFT
SLAB BOTTOM: MM	BEAM BOTTOM: MM

DRAWING NAME:


TRAIL ROOM DETAIL

DESIGNED BY:	CHECKED BY:	
AA	AAA	
DATE:	REVISION NO:	DWG NO:
17-09-2026	R0	00

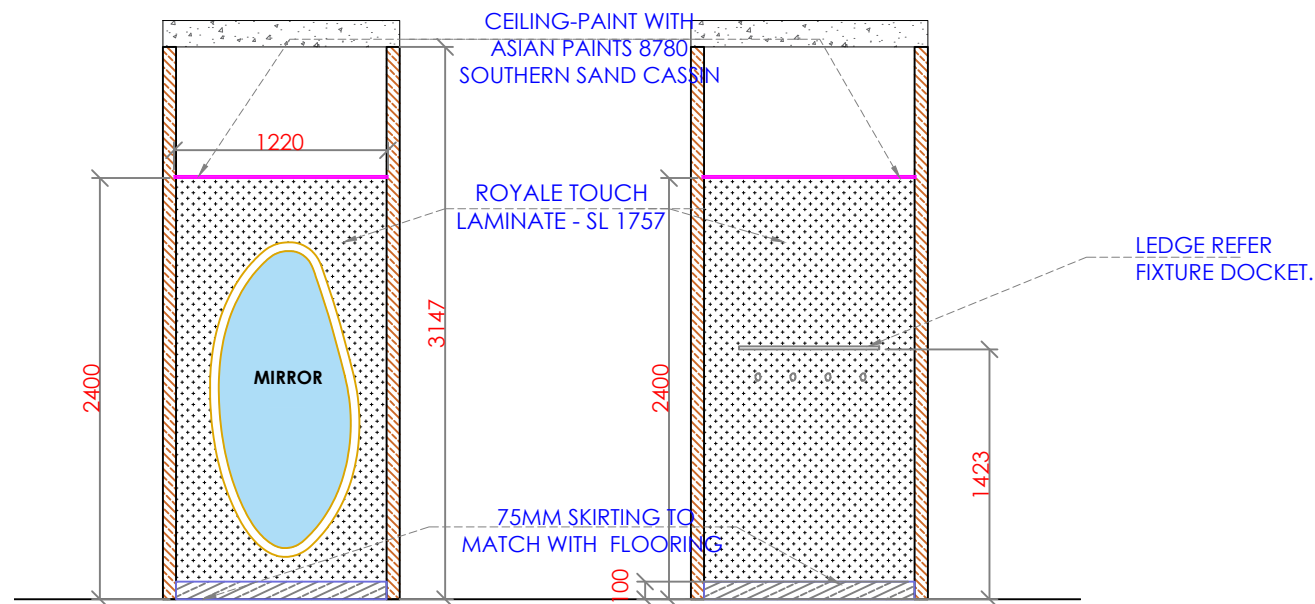


1 SECTION S1
Scale: NTS

2 SECTION S2
Scale: NTS

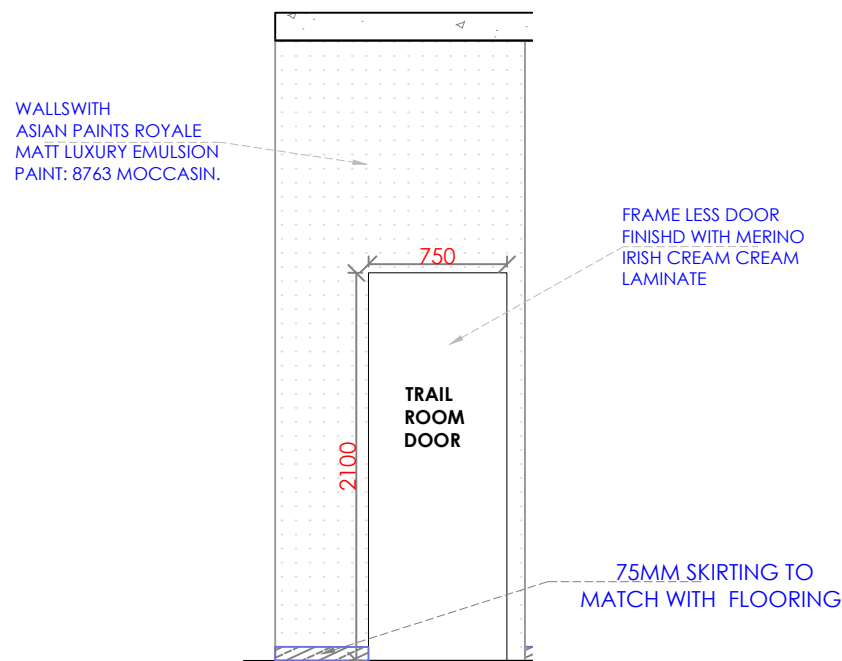


3 SECTION S3
Scale: NTS

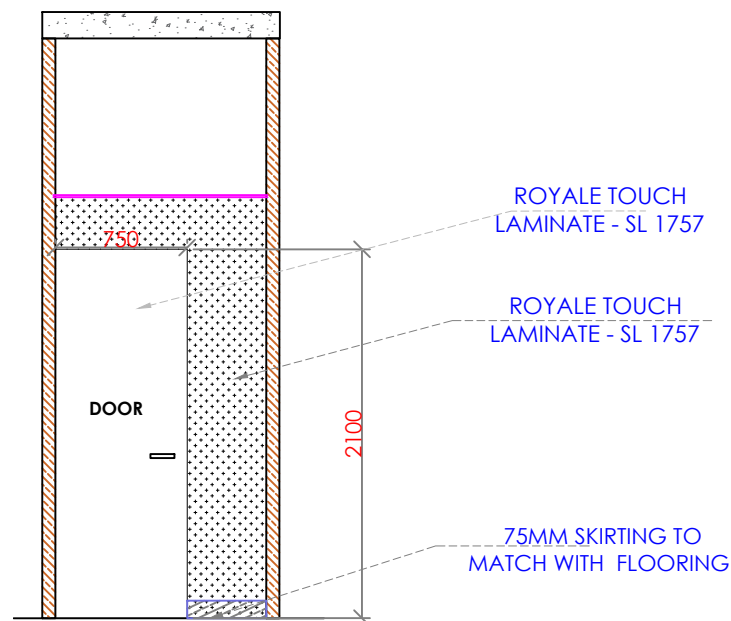

4 SECTION S4
Scale: NTS

LEGEND :

KEY PLAN :

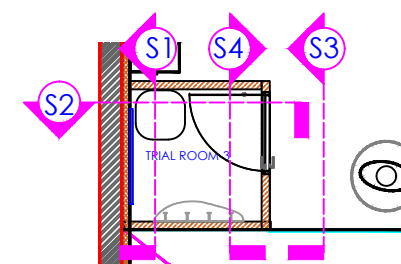

DOMORE DESIGN PVT. LTD.
NO. 681, SUKHADA, 2ND FLOOR, 2ND PHASE, 2ND BLOCK,
RAILWAY PARALLEL ROAD,
NEAR MALL OF ASIA, BANGALORE, KARNATAKA, 560097
domoredesign.co.in

GENERAL NOTES

- THIS DRAWING IS COPYRIGHT & PROPERTY OF DOMORE DESIGN PVT.LTD. AND IS NOT TO BE REPRODUCED, COPIED OR USED FOR ANY OTHER PURPOSE.
- WRITTEN DIMENSIONS TO BE FOLLOWED.
- DIMENSIONS TO BE CROSS CHECKED PRIOR TO THE COMMENCEMENT OF WORK.
- ALL DRAWINGS TO BE READ IN CONJUNCTION TO THE CONSULTANTS AND VENDORS DRAWINGS/DETAILS.
- FOR ALL LEGENDS, SYMBOLS, ABBREVIATIONS AND ANNOTATIONS RELATED QUERIES, REFER TO REFERENCE SHEET.
- ANY DISCREPANCY OR DOUBT IN DRAWING TO BE BROUGHT TO THE NOTICE OF DOMORE DESIGN PVT.LTD.

SCALE : AS MENTIONED


REVISIONS

R01
R02
R03

PROJECT NAME :

M3M PARAGON 57
GURGOAN

COMPASS:

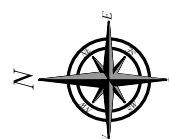



STORE INFO:

STATE	XXX
CITY	XXX
HIGHSTREET/MALL	XXX
AREA	SFT
SLAB BOTTOM: MM	BEAM BOTTOM: MM


DRAWING NAME:

TRAIL ROOM DETAIL


DESIGNED BY:	CHECKED BY:	
AA	AAA	
DATE:	REVISION NO:	DWG NO:
17-09-2026	R0	00

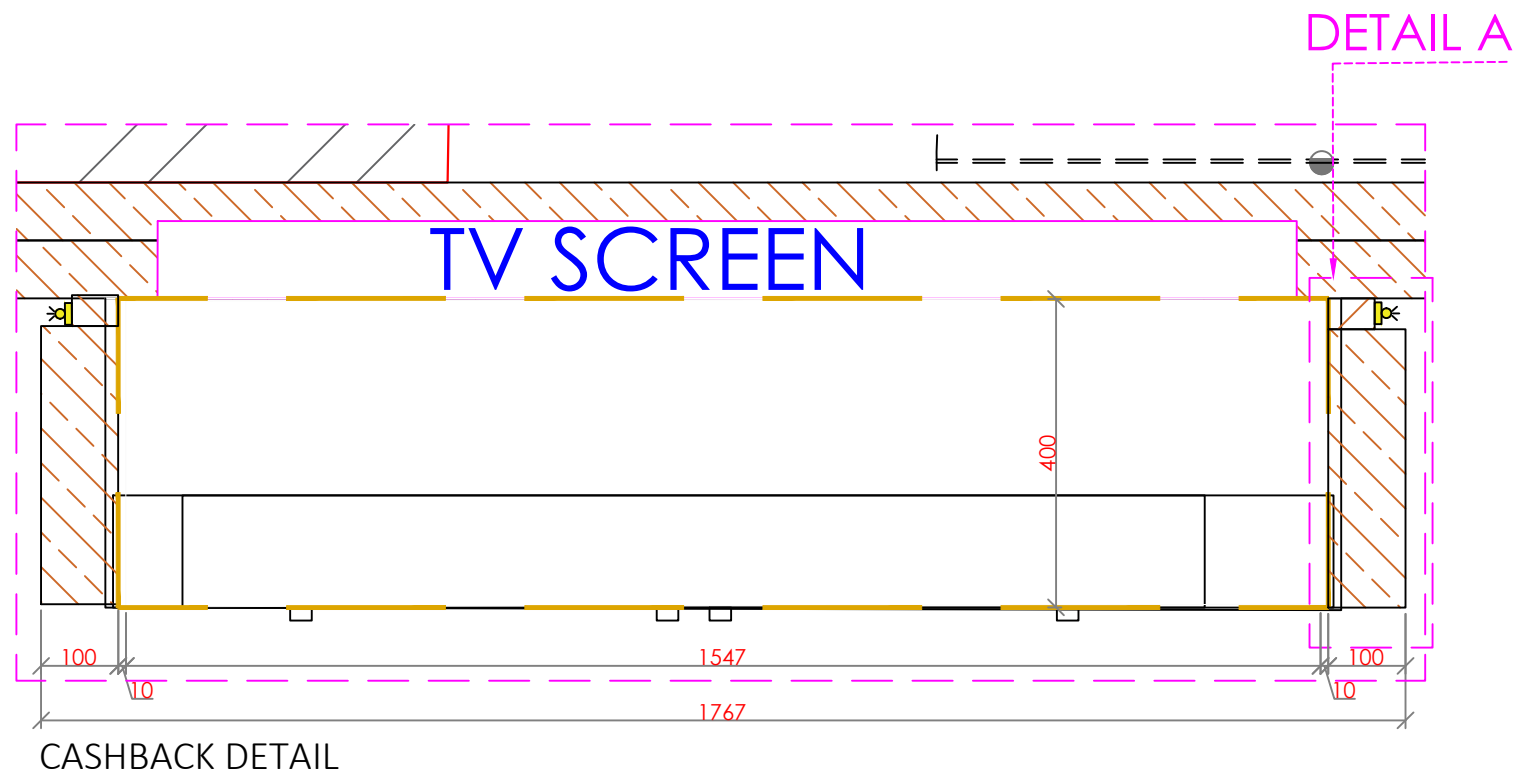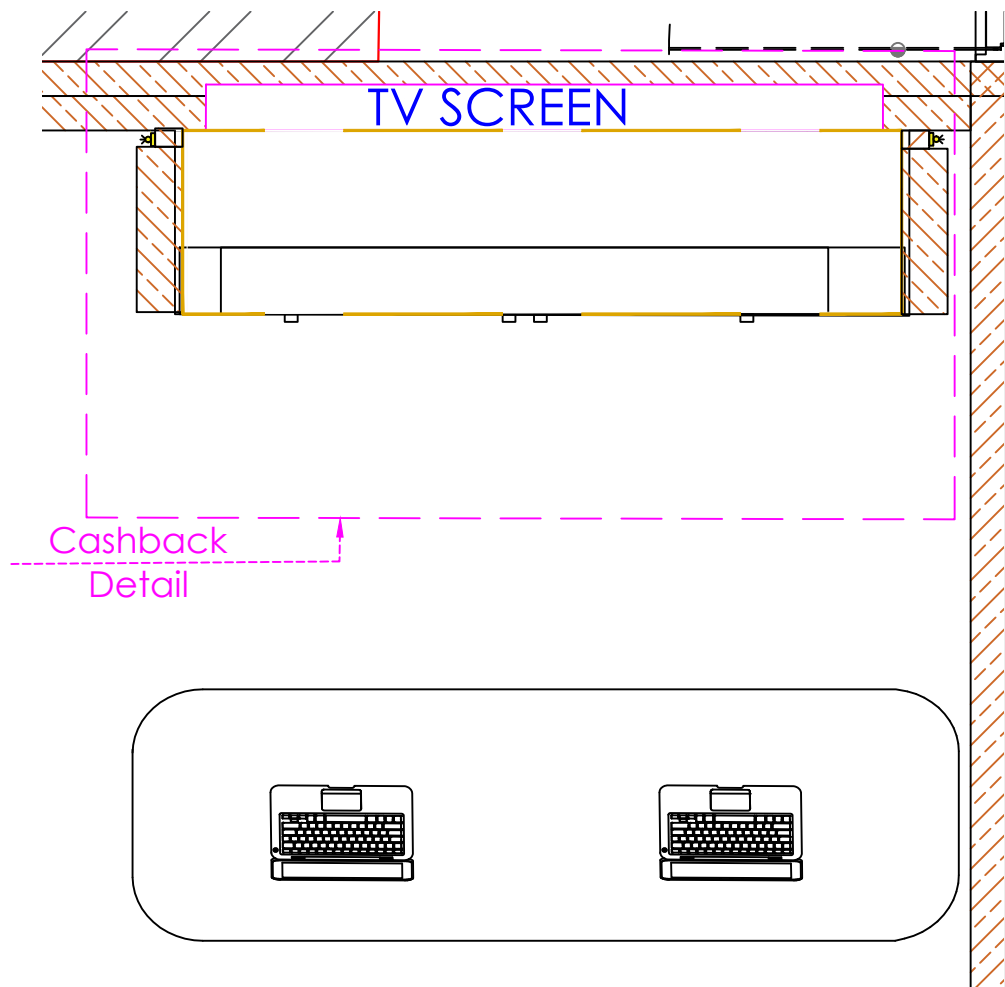

DETAIL A

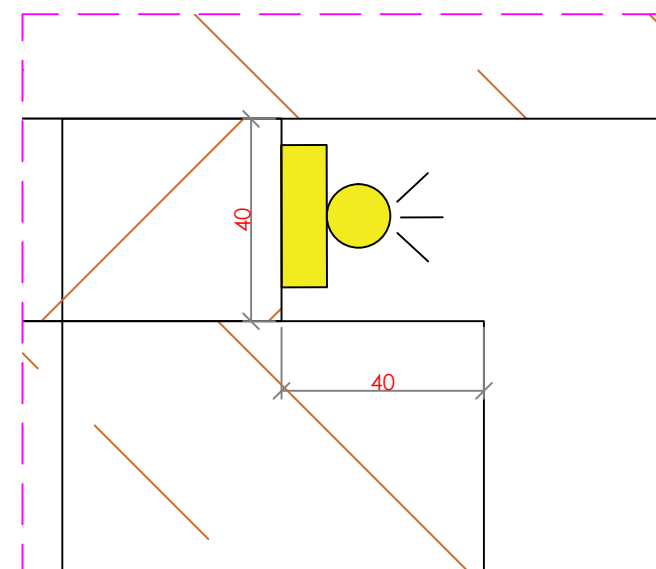

DETAIL B

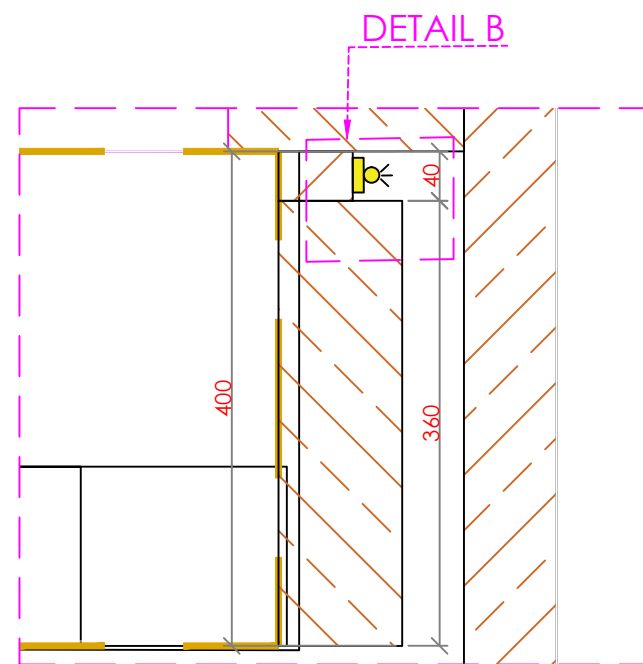

LEGEND :

KEY PLAN :

DRAWING NAME:

CASHBACK DETAIL

DESIGNED BY:	CHECKED BY:	
AA	AAA	
DATE:	REVISION NO:	DWG NO:
17-09-2026	R0	00

DOMORE
DESIGN PVT LTD

DOMORE DESIGN PVT. LTD.
NO.681, SUKHADA, 2ND FLOOR, 2ND PHASE, 2ND BLOCK,
RAILWAY PARALLEL ROAD,
NEAR MALL OF ASIA, BANGALORE, KARNATAKA, 560097
domoredesign.co.in

GENERAL NOTES

- THIS DRAWING IS COPYRIGHT & PROPERTY OF DOMORE DESIGN PVT.LTD. AND IS NOT TO BE REPRODUCED, COPIED OR USED FOR ANY OTHER PURPOSE.
- WRITTEN DIMENSIONS TO BE FOLLOWED.
- DIMENSIONS TO BE CROSS CHECKED PRIOR TO THE COMMENCEMENT OF WORK.
- ALL DRAWINGS TO BE READ IN CONJUNCTION TO THE CONSULTANTS AND VENDORS DRAWINGS/DETAILS.
- FOR ALL LEGENDS, SYMBOLS, ABBREVIATIONS AND ANNOTATIONS RELATED QUERIES, REFER TO REFERENCE SHEET.
- ANY DISCREPANCY OR DOUBT IN DRAWING TO BE BROUGHT TO THE NOTICE OF DOMORE DESIGN PVT.LTD

SCALE : AS MENTIONED


REVISIONS

R01
R02
R03

PROJECT NAME :


M3M PARAGON 57
GURGOAN

COMPASS:

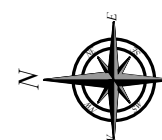

STORE INFO:

STATE	XXX
CITY	XXX
HIGHSTREET/MALL	XXX
AREA	SFT
SLAB BOTTOM: MM	BEAM BOTTOM: MM

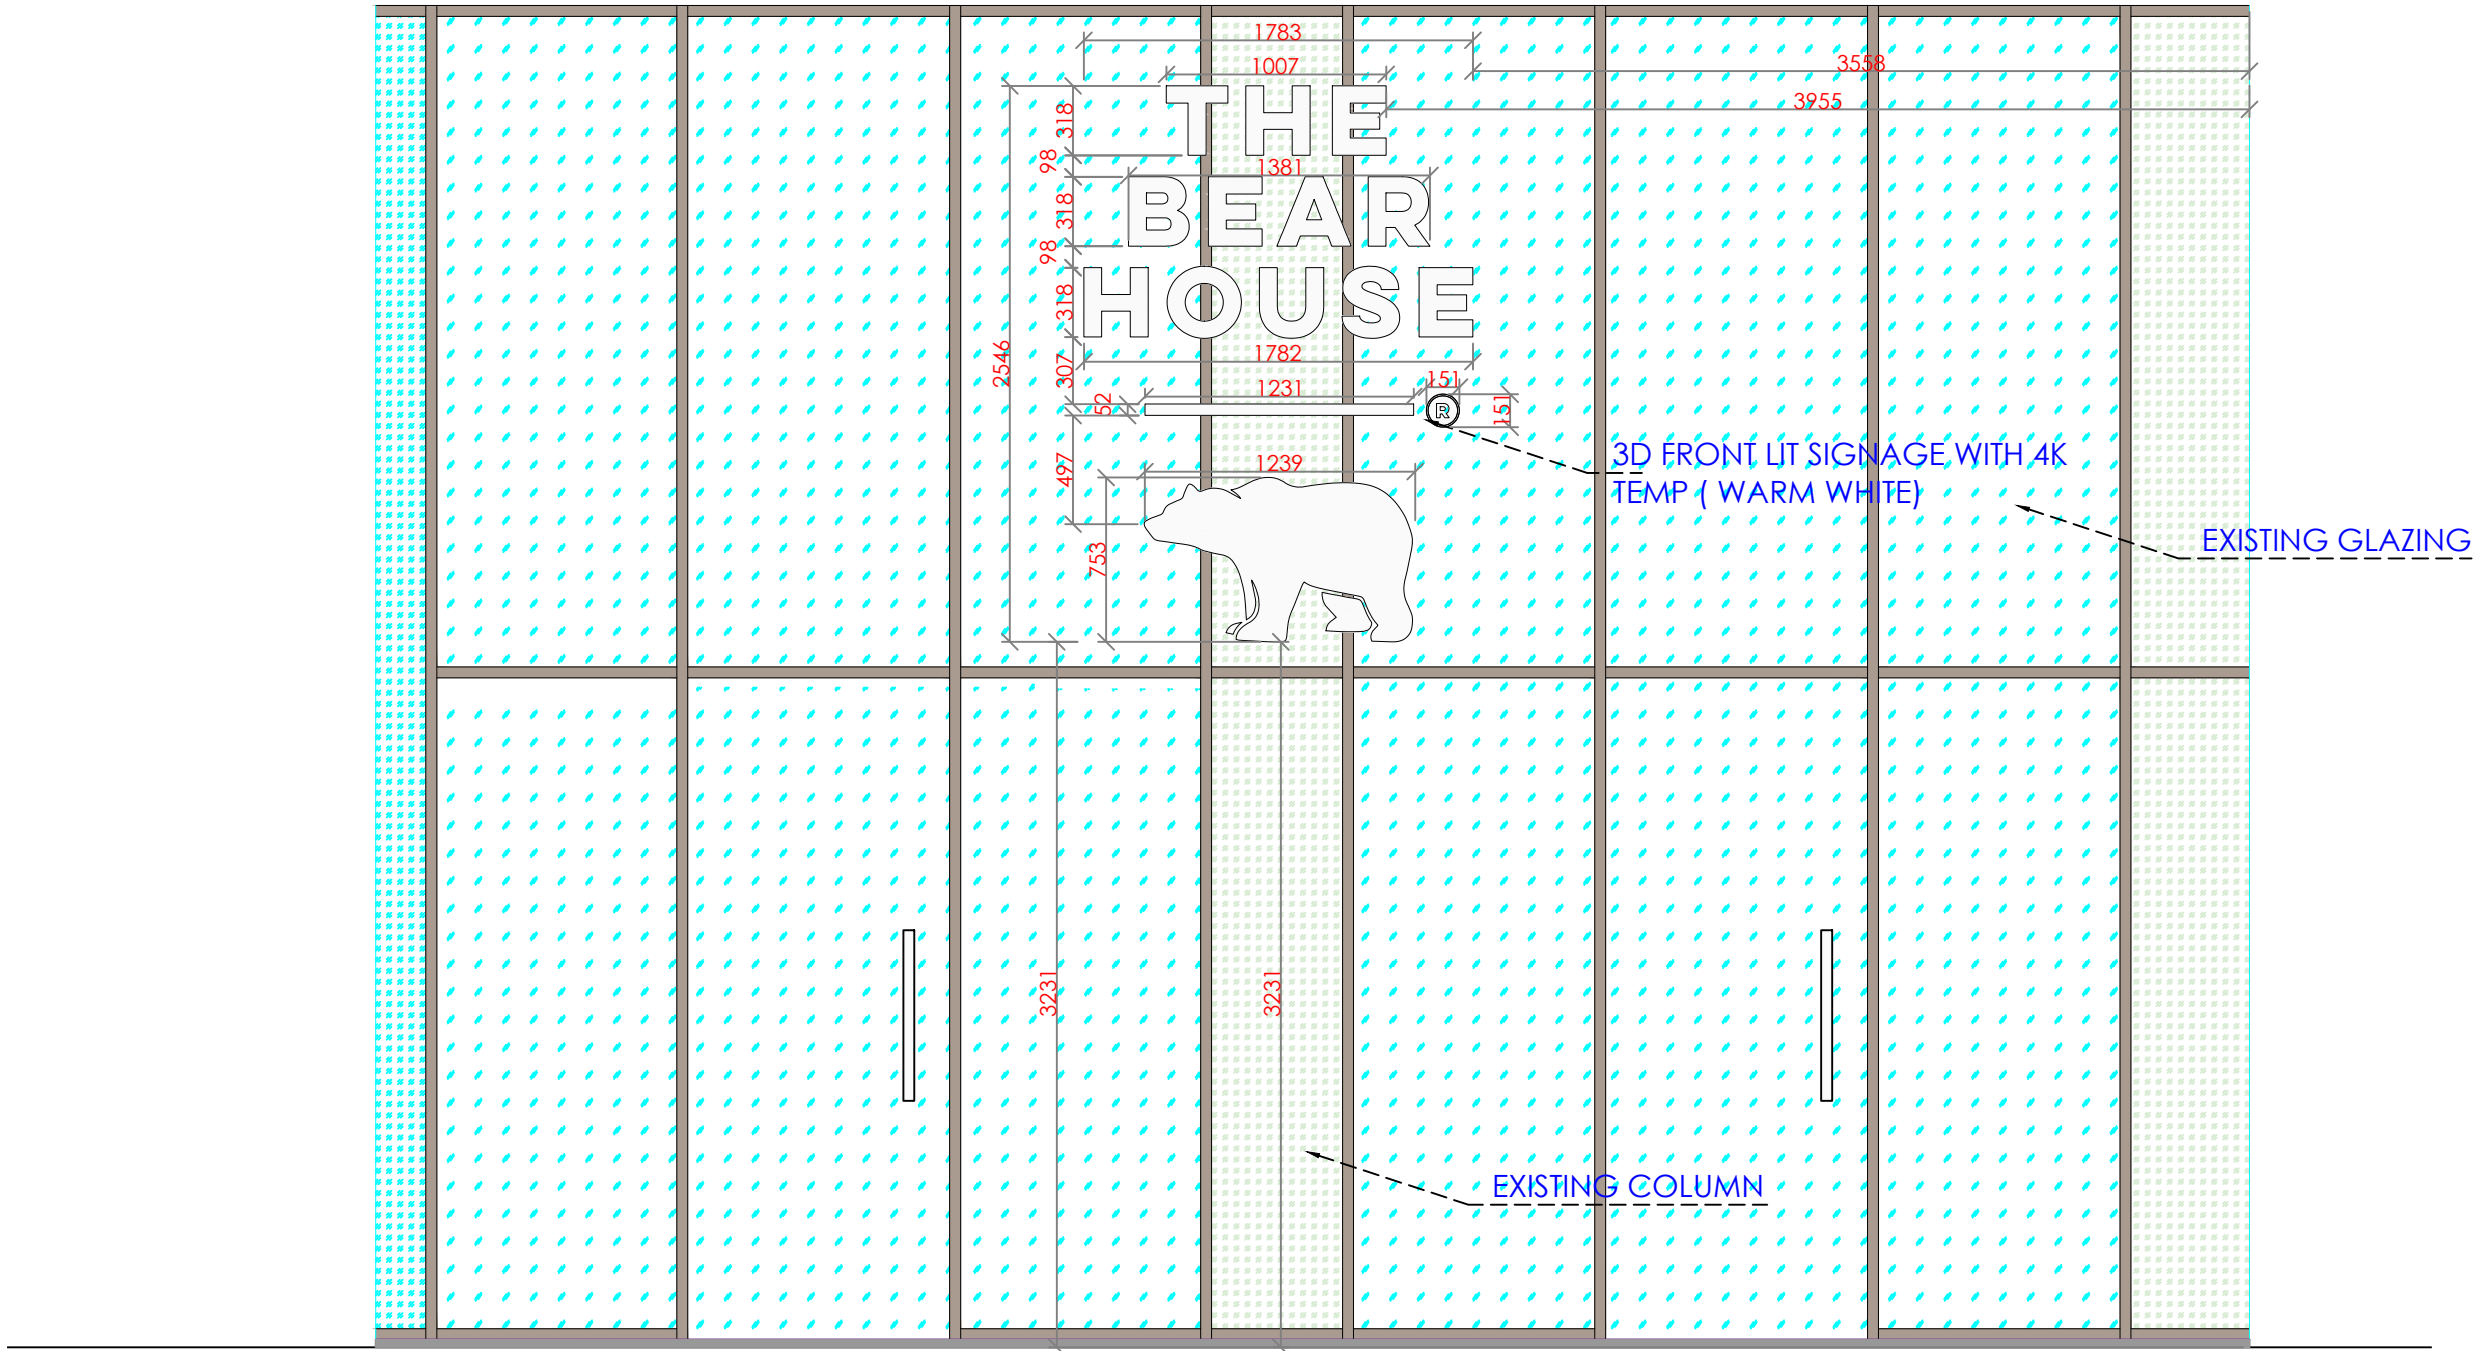

LEGEND :

KEY PLAN :



DOMORE DESIGN PVT. LTD.
NO.681, SUKHADA, 2ND FLOOR, 2ND PHASE, 2ND BLOCK,
RAILWAY PARALLEL ROAD,
NEAR MALL OF ASIA, BANGALORE, KARNATAKA, 560097
domoredesign.co.in

GENERAL NOTES

- THIS DRAWING IS COPYRIGHT & PROPERTY OF DOMORE DESIGN PVT.LTD, AND IS NOT TO BE REPRODUCED, COPIED OR USED FOR ANY OTHER PURPOSE.
- WRITTEN DIMENSIONS TO BE FOLLOWED.
- DIMENSIONS TO BE CROSS CHECKED PRIOR TO THE COMMENCEMENT OF WORK.
- ALL DRAWINGS TO BE READ IN CONJUNCTION TO THE CONSULTANTS AND VENDORS DRAWINGS/DETAILS.
- FOR ALL LEGENDS, SYMBOLS, ABBREVIATIONS AND ANNOTATIONS RELATED QUERIES, REFER TO REFERENCE SHEET.
- ANY DISCREPANCY OR DOUBT IN DRAWING TO BE BROUGHT TO THE NOTICE OF DOMORE DESIGN PVT.LTD

SCALE : AS MENTIONED


REVISIONS

R01
R02
R03

PROJECT NAME :

M3M PARAGON 57
GURGOAN

COMPASS:

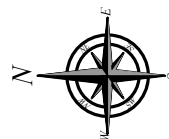

STORE INFO:

STATE	XXX
CITY	XXX
HIGHSTREET/MALL	XXX
AREA	SFT
SLAB BOTTOM: MM	BEAM BOTTOM: MM

DRAWING NAME:

FACADE

DESIGNED BY:	CHECKED BY:	
AA	AAA	
DATE:	REVISION NO:	DWG NO:
17-09-2026	R0	00